主桥上构工程数量表（一）（上层）

材料	项目	单位	主桥上构			附属工程			合计
			主桁	主桁拼接	上层桥面系	检修轨道及检查车	伸缩缝	集中排水	
Q420D	δ=100	kg	8737.1						8737.1
	δ=80	kg	6989.7						6989.7
	δ=60	kg	2458.8						2458.8
	δ=48	kg	191337.7	1633.4					192971.1
	δ=48（Z35）	kg	56689.0						56689.0
	δ=44	kg	149564.2	10164.6					159728.8
	δ=44（Z35）	kg	96292.7						96292.7
	δ=40	kg	307680.3	33604.5					341284.8
	δ=36	kg	3283.8	8986.5					12270.3
	δ=32	kg	275007.2	10990.2					285997.4
	δ=28	kg		12062.2					12062.2
	δ=24	kg		11198.7					11198.7
	δ=16	kg	27946.9						27946.9
	δ=14	kg	2518.5						2518.5
	焊缝重	kg	16927.6						16927.6
	合计	kg	1145433.4	88640.0					1234073.4
Q355D	δ=100	kg	3815.1						3815.1
	δ=80	kg	3052.1						3052.1
	δ=48	kg	33973.3						33973.3
	δ=44	kg		10730.2					10730.2
	δ=44（Z35）	kg	140063.0						140063.0
	δ=40	kg	314452.2						314452.2
	δ=40（Z35）	kg	182732.3						182732.3
	δ=36	kg	521193.4	10581.6					531775.0
	δ=32	kg	398720.8	9954.8					408675.6
	δ=28	kg	60106.8	45262.6					105369.4
	δ=24	kg	301501.0	43378.8	545983.2				890862.9
	δ=20	kg	423735.0	22910.7	431122.0		1753.2		879520.9
	δ=16	kg	115785.1	9958.7	1867.2		1623.4		129234.4
	δ=14	kg	56947.4	554.4	789637.2				847139.0
	δ=12	kg		2006.1	191453.0				193459.1
	δ=10	kg			40128.0				40128.0
	δ=8	kg		1352.2					1352.2
	焊缝重	kg	38341.2		30002.9				68344.0
	合计	kg	2594418.4	156690.0	2030193.5		3376.6		4784678.5
Q235B钢板		kg			484.4				484.4
Q355B		kg	311.1	513.6		65513.5			66338.2
Q355C		kg			28.4				28.4
10.9S高强螺栓	M30x200	kg		85774.2					85774.2
	M24	kg			26229.5				26229.5
M20x80螺栓(A5-80 GB31.1)		kg				780.6			780.6
现场连接焊缝		m		94.9					94.9
剪力钉	Φ22x150	kg			28337.6				28337.6
钢结构防腐外涂装		m²	17709.9	1164.3	30037.7				48911.9
检查车		套				1.5			1.5
定位筐		套						354.0	354.0

中交第二公路勘察设计研究院有限公司	狮子洋通道工程勘察设计 施 工 图 设 计	K6+418.3 新沙高架桥 主桥上构工程数量表	设计	余汪千	复核	袁勤	一审	沈维	二审	韦忠	图号	SZYS/04/02/02/01/01

主桥上构工程数量表（二）（上层）

材料	项目	单位	主桥上构	附属工程						合计
			上层桥面系	伸缩缝	支座及垫石	集中排水	上层防撞护栏	路灯底座预埋	健康监测	
混凝土	UC140-预制	m³	1915.3							1915.3
	UC140-现浇	m³	635.1							635.1
	C50钢纤维混凝土	m³	13.1	8.8						21.9
	C50砼	m³					137.6			137.6
	C30砼	m³						3.2		3.2
	C50小石子砼	m³			11.2					11.2
Q355C		kg					250569.2	314.0		250883.2
10.9S高强螺栓	M30x780	kg					19562.1			19562.1
	M22不锈钢螺栓	套						64.0		64.0
8.8级螺栓	M16x50	kg					632.0			632.0
	M16x170	kg					782.3			782.3
	M16x55	kg					607.9			607.9
HRB400钢筋	Φ18	kg	487145.1							487145.1
	Φ16	kg	369482.5	95.1			33563.5			403141.1
	Φ12	kg			3951.7			320.0		4271.7
	Φ10	kg	21321.2		824.9					22146.1
	合计	kg	877948.8	95.1	4776.5		33563.5	320.0		916704.0
HRB300钢筋	Φ10	kg						36.8		36.8
	Φ8	kg		15.9						15.9
	合计	kg		15.9				36.8		52.7
支座	XI-GSQZ60000GD-e300	套			0.5					0.5
	XI-GSQZ60000DX-e300	套			0.5					0.5
	XI-GSQZ50000DX-e300	套			1.0					1.0
	XI-GSQZ50000SX-e300	套			1.0					1.0
	XI-GSQZ25000DX-e200	套			1.0					1.0
	GSQZ(FS)-15000-SX-e150	套			2.0					2.0
2cm厚可压缩橡塑垫条		m²	659.8							659.8
Φ150mm镀锌钢管		m				44.8				44.8
防撞护栏密封构件		套					916.0			916.0
Φ350mm镀锌钢管		m				845.2				845.2
Φ100mm镀锌钢管		m				487.2				487.2
三通管		个				224.0				224.0
泄水槽		套				224.0				224.0
盖板		套				224.0				224.0
健康监测系统		套							0.5	0.5
伸缩缝	D240型	m/道		39.3/1						39.3/1
	D320型	m/道		39.3/1						39.3/1

注：

1、受上、下层工程数量拆分的影响，本表中支座、检查车、健康监测系统等数量统计会出现半套的情况。

中交第二公路勘察设计研究院有限公司	狮子洋通道工程勘察设计 施 工 图 设 计	K6+418.3 新沙高架桥 主桥上构工程数量表	设计	余汪千	复核	袁勤	一审	沈 华	二审	李忠	图号	SZYS/04/02/02/01/01

节段01材料数量表

名称	编号	材质	规格	数量	单件重	共重（kg）	备注
上弦顶板	N11	Q355D	t=20mm,A=27m2	1	4239	4239	
上弦底板	N12	Q355D	□13350x1200x20	1	2515.1	2515.1	
上弦节点板	N14	Q355D	t=28mm,A=13.05m2	2	2868.4	5736.8	
	N14a	Q355D	t=40mm,A=25m2	2	7850	15700	
上弦横隔板	N15	Q355D	□1980x1200x16	6	298.9	1793.4	
	N15‘	Q355D	□2057×200×16	4	51.5	206	
	N15b	Q355B	□2057×40×4	4	2.5	10	
	N15c	Q355D	□800×400×16	4	40.2	160.8	
上弦加劲肋	N16a	Q355D	□5651x240x20	4	213.5	854	
	N16b	Q355D	□7700x240x20	4	290.5	1162	
	N16c	Q355D	□7700x240x20	0	290.5	0	
	N16d	Q355D	□13300x240x20	1	500.8	500.8	
	N16e	Q355D	□13300x240x20	1	500.8	500.8	
下弦顶板	N21	Q355D	□4790x2500x20	1	1880.9	1880.9	
	N21a	Q355D	□10105x2500x20	1	3965.8	3965.8	
下弦底板	N22	Q355D	t=36mm,A=9.36m2	1	2645.1	2645.1	
	N22a	Q355D	t=20mm,A=15.68m2	1	2461.8	2461.8	
下弦腹板	N23	Q355D	□10105x1880x24	2	3579.6	7159.2	
下弦节点板	N24	Q355D	t=40mm,A=17.33m2	2	5441.6	10883.2	Z35钢
下弦横隔板	N25	Q355D	□1800x1200x16	1	271.3	271.3	
	N25’	Q355D	□2057x200x16	3	51.5	154.5	
	N25a	Q355D	□1800x1200x16	3	271.3	813.9	
下弦加劲肋	N26a	Q355D	□2792x240x20	2	105.2	210.4	
	N26b	Q355D	□10105x240x20	2	381.5	763	
	N26c	Q355D	□12897x240x20	1	486.7	486.7	
	N26d	Q355D	□10105x240x20	1	381.5	381.5	
	N26d’	Q355D	□2792x320x32	1	223.6	223.6	
	N26e	Q355D	□12897x170x14	2	240.7	481.4	
斜腹杆	N31	Q355D	□14038×1200×36	1	4761.8	4761.8	
	N31a	Q355D	□14038×1200×36	1	4761.8	4761.8	
	N32	Q355D	□9838×1360×36	2	3781.2	7562.4	
	N33	Q355D	□9838×320×32	2	791.3	1582.6	
	N33a	Q355D	□12638×320×32	1	1014.8	1014.8	
	N33b	Q355D	□12638×320×32	1	1014.8	1014.8	
	N34	Q355D	□1200×1200×16	4	180.9	723.6	
	N41	Q355D	□6725×1200×36	1	2280.6	2280.6	
	N41a	Q355D	□6925×1200×36	1	2348.4	2348.4	
	N42	Q355D	□4925×1360×36	2	1893.4	3786.8	
	N43	Q355D	□4925×320×32	2	396.9	793.8	
	N43a	Q355D	□6025×320×32	1	484.8	484.8	
	N43b	Q355D	□6225×320×32	1	499.9	499.9	
	N44	Q355D	□1200×1200×16	2	180.9	361.8	
竖腹杆顶底板	N51	Q355D	□13418x1200x20	1	2527.7	2527.7	
	N51a	Q355D	□11818x1200x20	1	2226.3	2226.3	
竖腹杆腹板	N52	Q355D	□9133x1500x20	2	2150.9	4301.8	
竖腹杆横隔板	N54	Q355D	□1400x1200x16	3	211	633	
竖腹杆加劲肋	N53	Q355D	□9133x190x16	2	218.5	437	
	N53a	Q355D	□12018x190x16	1	286.4	286.4	
	N53b	Q355D	□10418x190x16	1	248.7	248.7	
节点板加劲	N61	Q355D	□2800x320x32	2	226.1	452.2	
	N62	Q355D	□2600x320x32	2	208.5	417	
	N63	Q355D	□750x320x28	2	52.8	105.6	
	N64	Q355D	□2100x320x32	2	168.3	336.6	
	N65	Q355D	□2100x320x32	2	168.3	336.6	

名称	编号	材质	规格	数量	单件重	共重（kg）	备注
横梁接头	N71	Q355D	□1980x610x16	6	152	912	
	N71’	Q355D	□1980x650x16	2	162	324	
	N71a	Q355D	□1980x622x16	4	154.5	618	
	N72	Q355D	t=24mm,A=0.47m2	6	88.4	530.4	
	N72’	Q355D	t=24mm,A=0.48m2	6	90.4	542.4	
	N72a	Q355D	t=24mm,A=0.97m2	2	182	364	
	N72b	Q355D	t=24mm,A=0.48m2	2	90	180	
	N73	Q355D	□1800x626x16	8	141.9	1135.2	
	N73a	Q355D	□1800x610x28	4	241.8	967.2	
支承加劲肋	N81	Q355D	□1800x1200x32	4	542.6	2170.4	
	N82	Q355D	□502x240x20	2	18.8	37.6	
	N83	Q355D	□1800x1800x100	1	2543.4	2543.4	
	N84	Q355D	□1000x568x32	3	143.2	429.6	
	N85	Q355D	□1350x570x32	4	193.4	773.6	
小计						121975.6	
焊缝重1.5%						1829.6	
合计						123805.2	

节段01材料数量汇总表

规格（mm）	材质	单个合计	全桥共1个
t=100	Q355D	2543.4	2543.4
t=40		26583.2	26583.2
t=36		28146.9	28146.9
t=32		10530.3	10530.3
t=28		6809.6	6809.6
t=24		8776	8776
t=20		29015.2	29015.2
t=16		9079.6	9079.6
t=14		481.4	481.4
t=4		10	10
焊缝重（1.5%）		1829.6	1829.6
合计	Q355D	123805.2	123805.2
内表面涂装（m²）		677.5	677.5
外表面涂装（m²）		460.1	460.1

中交第二公路勘察设计研究院有限公司	狮子洋通道工程勘察设计 施 工 图 设 计	K6+418.3 新沙高架桥 中桥节段01设计图	设计	余汪千	复核	袁勤	一审	张华	二审	李忠	图号	SZYS/04/02/02/01/09

大样A（节段1~节段2）

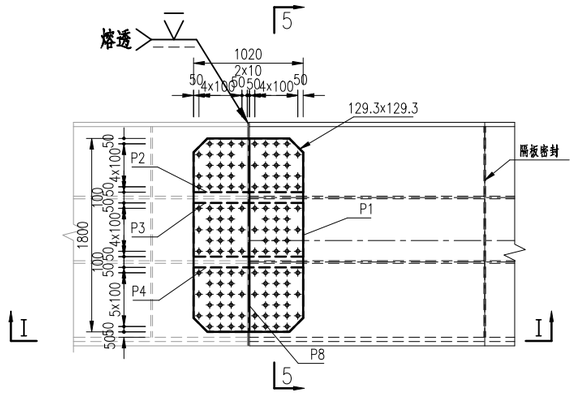

5-5

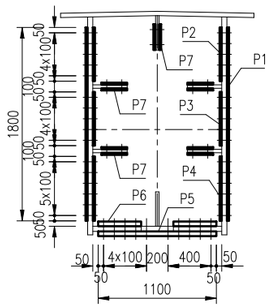

大样C（节段1~节段2）

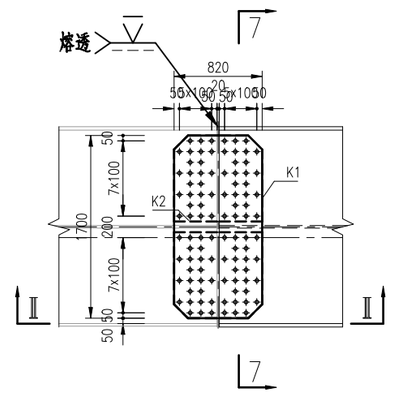

7-7

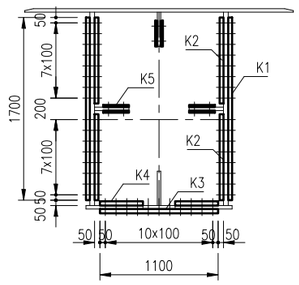

Ⅰ－Ⅰ

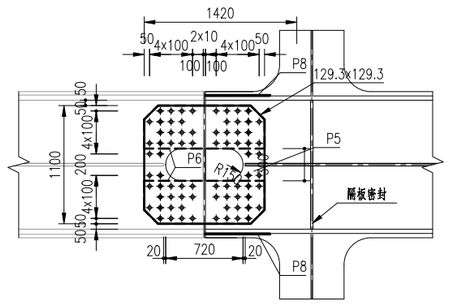

上弦杆顶板、腹板加劲肋拼接

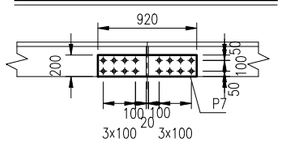

Ⅳ－Ⅳ

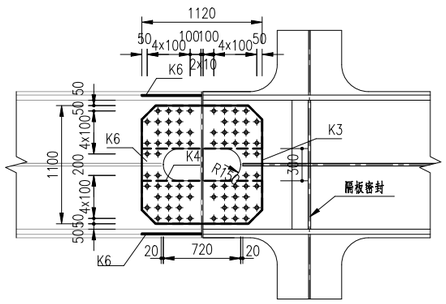

下弦杆顶板、腹板加劲肋拼接

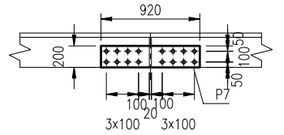

注：

1、本图尺寸均以mm计。

2、未注明的板件裁切边距M30螺栓不小50mm，M24螺栓不小40mm。

3、图中未注明的过焊孔圆弧切角半径为35mm。

4、图中未注明焊缝详见《钢梁焊缝及细节设计图》。

符号：

⊕ —— M30螺栓，开孔直径33mm

⊗ —— M24螺栓，开孔直径26mm

大样B（节段1~节段2）

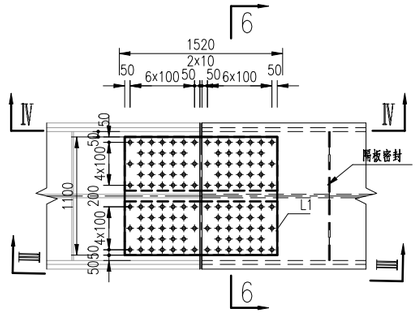

6-6

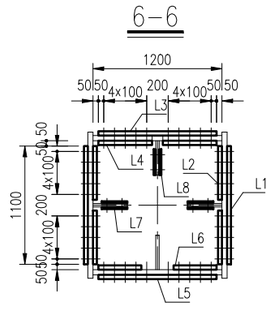

腹杆腹板加劲肋拼接

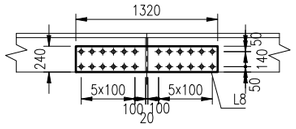

腹杆顶加劲肋拼接

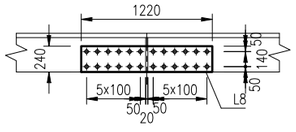

Ⅲ－Ⅲ

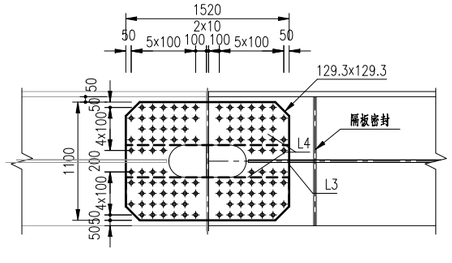

Ⅳ－Ⅳ

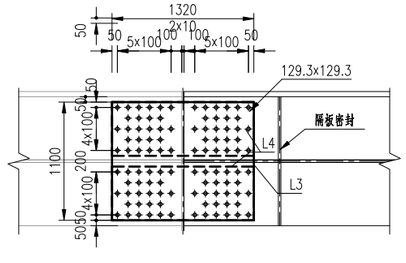

节段1~节段2拼接数量表

名称	编号	材质	规格	数量	单件重	共重（kg）	备注
上弦杆拼接	P1	Q355D	□1020×1800×16	2	231.1	462.2	
	P2		□1020×500×16	2	64.1	128.2	
	P3		□1020×500×16	2	64.1	128.2	
	P4		□1020×600×16	2	76.6	153.2	
	P5		□1420×1100×28	1	342.9	342.9	
	P6		□1420×400×28	2	125.3	250.6	
	P7		□920×200×20	10	28.3	283	
	P8		□600×1800×20	2	169.6	339.2	
	M30高强螺栓	10.9S	M30x200	508	1.94	985.5	
下弦杆拼接	K1	Q355D	□820×1700×20	2	218.2	436.4	
	K2		□820×800×20	4	103.6	414.4	
	K3		□1120×1100×32	1	309	309	
	K4		□1120×400×32	2	113	226	
	K5		□920×200×20	6	28.3	169.8	
	K6		□400×1700×20	2	106.8	213.6	
	M30高强螺栓	10.9S	M30x200	324	1.94	628.6	
腹杆拼接	L1	Q355D	□1520×1100×24	2	314.6	629.2	
	L2		□1520×500×24	4	143.2	572.8	
	L3		□1320×1100×28	1	318.7	318.7	
	L4		□1320×500×28	2	145.1	290.2	
	L5		□1520×1100×44	1	576.8	576.8	
	L6		□1520×240×44	2	124.3	248.6	
	L7		□1220×240×24	4	54.6	218.4	
	L8		□1320×240×24	2	60.3	120.6	
	M30高强螺栓	10.9S	M30x200	540	1.94	1047.6	

中交第二公路勘察设计研究院有限公司	狮子洋通道工程勘察设计 施 工 图 设 计	K6+418.3 新沙高架桥 中桥节段02设计图	设计	余汪千	复核	袁勤	一审	沈雁	二审	李忠	图号	SZYS/04/02/02/01/ 10

2251001719411202

节段02材料数量表

名称	编号	材质	规格	数量	单件重	共重（kg）	备注
上弦顶板	N11a	Q355D	t=20mm,A=15.65m2	1	2456.6	2456.6	
	N11b	Q355D	t=20mm,A=20.05m2	1	3147.9	3147.9	
上弦底板	N12a	Q355D	□7902×1200×20	1	1488.4	1488.4	
	N12b	Q355D	□10151×1200×20	1	1912.3	1912.3	
上弦节点板	N13	Q355D	t=40mm,A=22.29m2	2	6999.1	13998.2	
上弦腹板	N14	Q355D	□10351×2048×20	2	3328.4	6656.8	
上弦横隔板	N15	Q355D	□1980×1200×16	3	298.9	896.7	
	N15a	Q355D	□1980×1200×16	3	298.9	896.7	
	N15‘	Q355D	□2057×200×16	4	51.5	206	
	N15b	Q355B	□2057×40×4	4	2.5	10	
	N15c	Q355D	□800×400×16	4	40.2	160.8	
上弦加劲肋	N16a	Q355D	□7902×240×20	6	298.3	1789.8	
	N16b	Q355D	□10151×240×20	6	383.1	2298.6	
下弦顶板	N21a	Q355D	□7902×2500×24	1	3722.8	3722.8	
	N21b	Q355D	□10105×2500×24	1	4759	4759	
下弦底板	N22a	Q355D	t=24mm,A=12.96m2	1	2441.6	2441.6	
	N22b	Q355D	t=24mm,A=15.96m2	1	3006	3006	
下弦节点板	N23	Q355D	t=40mm,A=21.84m2	2	6858.5	13717	Z35钢
下弦腹板	N24	Q355D	□10305×1880×24	2	3649.3	7298.6	
下弦横隔板	N25	Q355D	□1800×1200×16	3	271.3	813.9	
	N25a	Q355D	□1800×1200×16	3	271.3	813.9	
	N25’	Q355D	□2057×200×16	6	51.5	309	
下弦加劲肋	N26a	Q355D	□7902×240×20	2	298.3	596.6	
	N26a’	Q355D	□7902×240×20	2	298.3	596.6	
	N26b	Q355D	□10105×240×20	4	381.5	1526	
	N26c	Q355D	□18007×170×14	2	336.3	672.6	
斜腹杆	N31	Q355D	□10047×900×36	2	2554.7	5109.4	
	N32	Q355D	□14547×1200×32	1	4386	4386	
	N33	Q355D	□13147×240×24	2	595.3	1190.6	
	N41	Q355D	□4796×900×36	2	1220.8	2441.6	
	N42	Q355D	□7096×1200×32	1	2140.2	2140.2	
	N43	Q355D	□6396×240×24	2	290.1	580.2	
	N51	Q355D	□7125×1200×36	1	2416.2	2416.2	
	N51a	Q355D	□6725×1200×36	1	2280.6	2280.6	
	N52	Q355D	□4925×1360×36	2	1893.4	3786.8	
	N53	Q355D	□4925×320×32	2	396.9	793.8	
节点板加劲	N53a	Q355D	□6425×320×32	1	517.5	517.5	
	N53b	Q355D	□6025×320×32	1	484.8	484.8	
	N54	Q355D	□1200×1200×16	2	180.9	361.8	
	N55	Q355D	□2150×320×32	2	173.3	346.6	
横梁接头	N61	Q355D	□1980×610×14	6	133	798	
	N61a	Q355D	□1980×630×14	6	137.4	824.4	
	N62	Q355D	t=24mm,A=0.47m2	6	89.3	535.8	
	N62a	Q355D	t=24mm,A=0.48m2	6	90.4	542.4	
	N63	Q355D	□1800×610×14	6	120.9	725.4	
	N63a	Q355D	□1800×626×14	6	124.2	745.2	
小计						107199.7	
焊缝重1.5%						1608.0	
合计						108807.7	

节段02材料数量汇总表

规格（mm）	材质	单个合计	全桥共1个
t=40	Q355D	27715.2	27715.2
t=36		16034.6	16034.6
t=32		8668.9	8668.9
t=24		24077	24077
t=20		22469.6	22469.6
t=16		4458.8	4458.8
t=14		3765.6	3765.6
焊缝重（1.5%）		1608.0	1608.0
合计	Q355D	108807.7	108807.7
内表面涂装（㎡）		548.4	548.4
外表面涂装（㎡）		492.6	492.6

节段1～节段2拼接数量汇总表

规格（mm）	材质	单个合计	全桥共1个
t=44	Q355D	825.4	825.4
t=32		535	535
t=28		1202.4	1202.4
t=24		1541	1541
t=20		1856.4	1856.4
t=16		871.8	871.8
合计		6832.0	6832.0
M30x200	10.9S高强螺栓	2661.7	2661.7
外表面涂装（㎡）		36.9	36.9

注：

1. 本图适用于中桥架节段02，图中单位均以毫米计；

中交第二公路勘察设计研究院有限公司	狮子洋通道工程勘察设计 施 工 图 设 计	K6+418.3 新沙高架桥 中桥节段02设计图	设计	余汪千	复核	袁勤	一审	沈华	二审	李超	图号	SZYS/04/02/02/01/ 10

大样A（节段2~节段3）

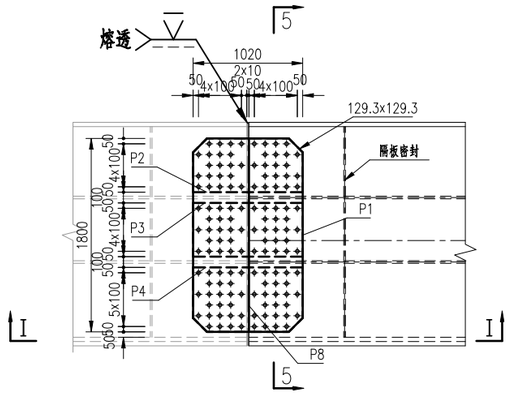

5-5

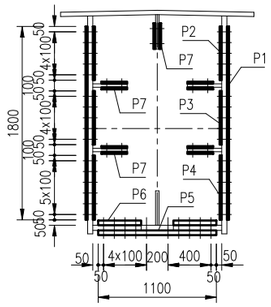

Ⅰ－Ⅰ

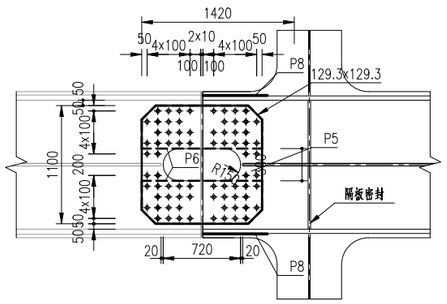

上弦杆顶板、腹板加劲肋拼接

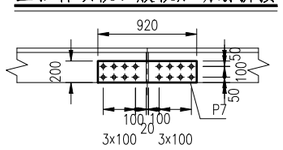

大样C（节段2~节段3）

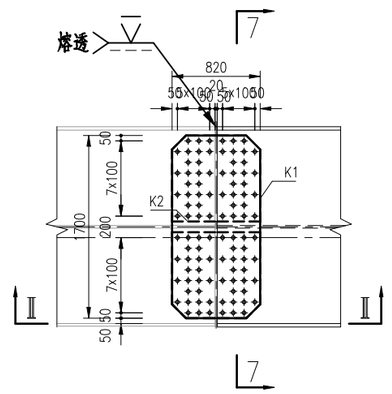

7-7

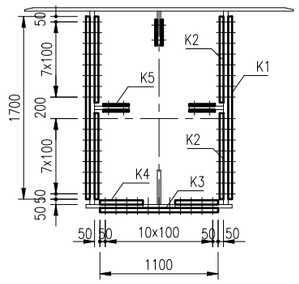

Ⅳ－Ⅳ

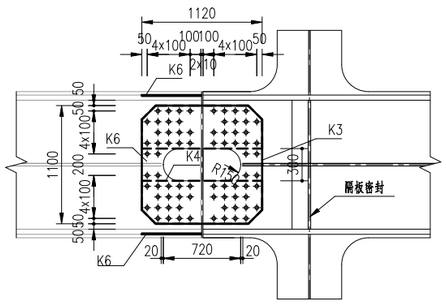

下弦杆顶板、腹板加劲肋拼接

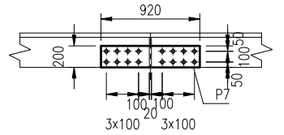

大样B（节段2~节段3）

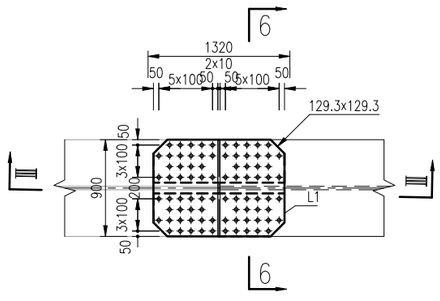

6-6

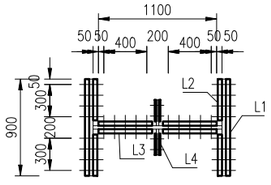

腹杆腹板加劲肋拼接

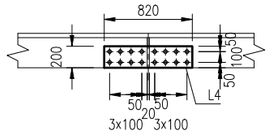

Ⅲ－Ⅲ

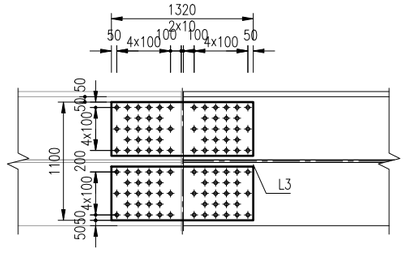

注：

1、本图尺寸均以mm计。

2、未注明的板件裁切边距M30螺栓不小50mm，M24螺栓不小40mm。

3、图中未注明的过焊孔圆弧切角半径为35mm。

4、图中未注明焊缝详见《钢梁焊缝及细节设计图》。

符号：

⊕ —— M30螺栓，开孔直径33mm

⊗ —— M24螺栓，开孔直径26mm

节段2~节段3拼接数量表

名称	编号	材质	规格	数量	单件重	共重（kg）	备注
上弦杆拼接	P1	Q355D	□1020×1800×16	2	231.1	462.2	
	P2		□1020×500×16	2	64.1	128.2	
	P3		□1020×500×16	2	64.1	128.2	
	P4		□1020×600×16	2	76.6	153.2	
	P5		□1420×1100×28	1	342.9	342.9	
	P6		□1420×400×28	2	125.3	250.6	
	P7		□920×200×20	10	28.3	283	
	P8		□600×1800×20	2	169.6	339.2	
	M30高强螺栓	10.9S	M30x200	508	1.94	985.5	
下弦杆拼接	K1	Q355D	□820×1700×20	2	218.2	436.4	
	K2		□820×800×20	4	103.6	414.4	
	K3		□1120×1100×32	1	309	309	
	K4		□1120×400×32	2	113	226	
	K5		□920×200×20	6	28.3	169.8	
	K6		□400×1700×20	2	106.8	213.6	
	M30高强螺栓	10.9S	M30x200	324	1.94	628.6	
腹杆拼接	L1	Q355D	□1320×900×28	2	261.6	523.2	
	L2		□1320×400×28	4	116.5	466	
	L3		□1320×500×28	4	145.1	580.4	
	L4		□820×200×20	4	25.1	100.4	
	M30高强螺栓	10.9S	M30x200	320	1.94	620.8	

节段03材料数量表

名称	编号	材质	规格	数量	单件重	共重（kg）	备注
上弦顶板	N11a	Q355D	t=20mm,A=15.29m2	1	2400.2	2400.2	
	N11b	Q355D	t=20mm,A=16.91m2	1	2654.2	2654.2	
上弦底板	N12a	Q355D	□7902×1200×20	1	1488.4	1488.4	
	N12b	Q355D	□8600×1200×20	1	1620.2	1620.2	
上弦节点板	N13	Q355D	t=40mm,A=22.42m2	2	7038.9	14077.8	
上弦腹板	N14	Q355D	□8800×2048×20	2	2829.1	5658.2	
上弦横隔板	N15	Q355D	□1980×1200×16	3	298.9	896.7	
	N15a	Q355D	□1980×1200×16	3	298.9	896.7	
	N15‘	Q355D	□2057×200×16	4	51.5	206	
	N15b	Q355B	□2057×40×4	4	2.5	10	
	N15c	Q355D	□800×400×16	4	40.2	160.8	
上弦加劲肋	N16a	Q355D	□7902×240×20	4	298.3	1193.2	
	N16b	Q355D	□8600×240×20	6	323.4	1940.4	
下弦顶板	N21a	Q355D	□7904×2500×24	1	3722.8	3722.8	
	N21b	Q355D	□7102×2500×24	1	3346	3346	
下弦底板	N22a	Q355D	t=24mm,A=12.96m2	1	2442.1	2442.1	
	N22b	Q355D	t=24mm,A=11.13m2	1	2097.6	2097.6	
下弦节点板	N23	Q355D	t=40mm,A=20.75m2	2	6516.8	13033.6	Z35钢
下弦腹板	N24	Q355D	□7302×1880×24	2	2586.7	5173.4	
下弦横隔板	N25	Q355D	□1800×1200×16	3	271.3	813.9	
	N25a	Q355D	□1800×1200×16	2	271.3	542.6	
	N25’	Q355D	□2057×200×16	5	51.5	257.5	
下弦加劲肋	N26a	Q355D	□7904×240×20	4	298.3	1193.2	
	N26b	Q355D	□7102×240×20	4	266.9	1067.6	
	N26c	Q355D	□15006×170×14	2	280.2	560.4	
斜腹杆	N31	Q355D	□9010×900×36	2	2291.9	4583.8	
	N32	Q355D	□13610×1200×32	1	4102.1	4102.1	
	N33	Q355D	□12210×240×24	2	552	1104	
	N41	Q355D	□4322×900×36	2	1099.3	2198.6	
	N42	Q355D	□6722×1200×32	1	2027.2	2027.2	
	N43	Q355D	□6022×240×24	2	273.2	546.4	
	N51	Q355D	□4796×900×36	2	1220.8	2441.6	
	N52	Q355D	□6996×1200×32	1	2110.1	2110.1	
	N53	Q355D	□6296×240×24	2	284.5	569	
横梁接头	N61	Q355D	□1980×610×14	6	133	798	
	N61a	Q355D	□1980×630×14	6	137.4	824.4	
	N62	Q355D	t=24mm,A=0.47m2	6	89.3	535.8	
	N62a	Q355D	t=24mm,A=0.48m2	6	90.4	542.4	
	N63	Q355D	□1800×610×14	6	120.9	725.4	
	N63a	Q355D	□1800×626×14	6	124.2	745.2	
小计						91307.5	
焊缝重1.5%						1370.0	
合计						92677.5	

节段03材料数量汇总表

规格（mm）	材质	单个合计	全桥共1个
t=40	Q355D	27111.4	27111.4
t=36		9224	9224
t=32		8239.4	8239.4
t=24		20079.5	20079.5
t=20		19215.6	19215.6
t=16		3774.2	3774.2
t=14		3653.4	3653.4
t=4		10	10
焊缝重（1.5%）		1369.6	1369.6
合计	Q355D	92677.1	92677.1
内表面涂装（m²）		403.1	403.1
外表面涂装（m²）		485.6	485.6

节段2~节段3拼接数量汇总表

规格（mm）	材质	单个合计	全桥共1个
t=32	Q355D	535	535
t=28		2163.1	2163.1
t=20		1956.8	1956.8
t=16		871.8	871.8
合计		5526.7	5526.7
M30×200	10.9S高强螺栓	2234.9	2234.9
外表面涂装（m²）		31.4	31.4

中交第二公路勘察设计研究院有限公司	狮子洋通道工程勘察设计 施 工 图 设 计	K6+418.3 新沙高架桥 中桥节段03设计图	设计	余汪千	复核	袁勤	一审	沈华	二审	李忠	图号	SZYS/04/02/02/01/ 11

72330075119308

大样A（节段3~节段4）

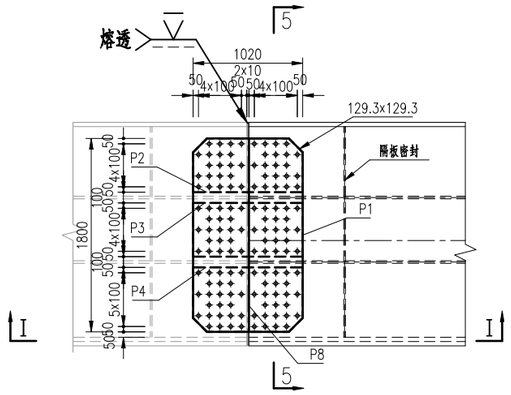

5-5

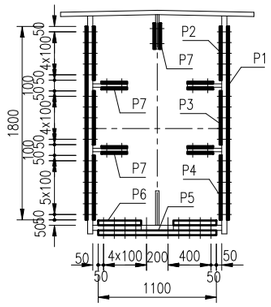

Ⅰ－Ⅰ

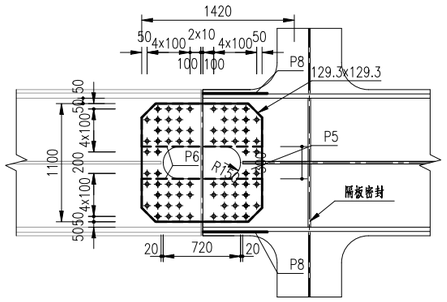

上弦杆顶板、腹板加劲肋拼接

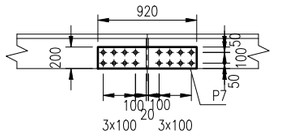

大样C（节段3~节段4）

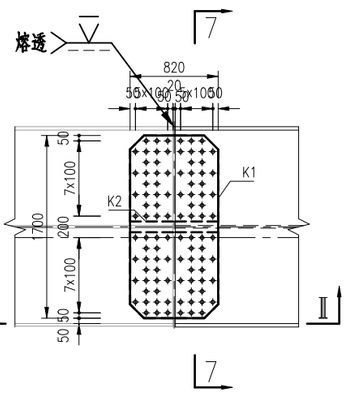

7-7

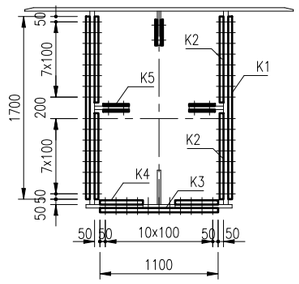

Ⅳ－Ⅳ

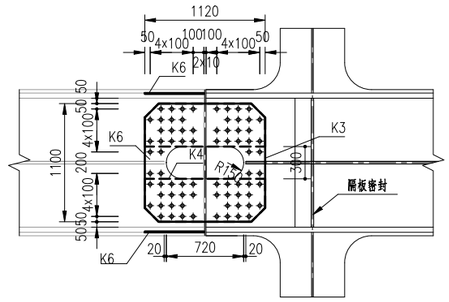

下弦杆顶板、腹板加劲肋拼接

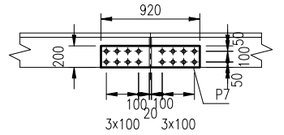

注：

1、本图尺寸均以mm计。

2、未注明的板件裁切边距M30螺栓不小50mm，M24螺栓不小40mm。

3、图中未注明的过焊孔圆弧切角半径为35mm。

4、图中未注明焊缝详见《钢梁焊缝及细节设计图》。

符号：

⊕ —— M30螺栓，开孔直径33mm

⊗ —— M24螺栓，开孔直径26mm

大样B（节段3~节段4）

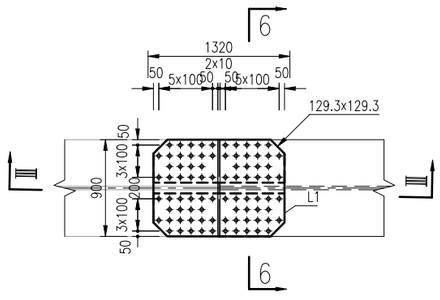

6-6

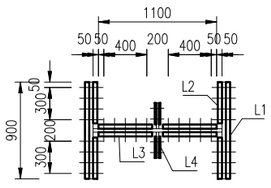

腹杆腹板加劲肋拼接

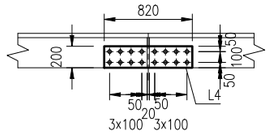

Ⅲ－Ⅲ

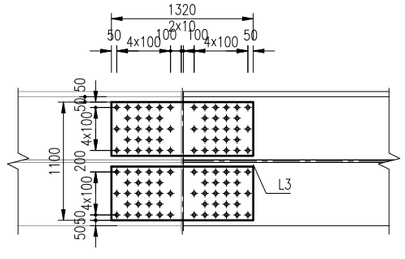

节段3~节段4拼接数量表

名称	编号	材质	规格	数量	单件重	共重（kg）	备注
上弦杆拼接	P1	Q355D	□1020×1800×16	2	231.1	462.2	
	P2		□1020×500×16	2	64.1	128.2	
	P3		□1020×500×16	2	64.1	128.2	
	P4		□1020×600×16	2	76.6	153.2	
	P5		□1420×1100×28	1	342.9	342.9	
	P6		□1420×400×28	2	125.3	250.6	
	P7		□920×200×20	10	28.3	283	
	P8		□600×1800×20	2	169.6	339.2	
	M30高强螺栓	10.9S	M30x200	508	1.94	985.5	
下弦杆拼接	K1	Q355D	□820×1700×20	2	218.2	436.4	
	K2		□820×800×20	4	103.6	414.4	
	K3		□1120×1100×32	1	309	309	
	K4		□1120×400×32	2	113	226	
	K5		□920×200×20	6	28.3	169.8	
	K6		□400×1700×20	2	106.8	213.6	
	M30高强螺栓	10.9S	M30x200	324	1.94	628.6	
腹杆拼接	L1	Q355D	□1320×900×28	2	261.6	523.2	
	L2		□1320×400×28	4	116.5	466	
	L3		□1320×500×28	4	145.1	580.4	
	L4		□820×200×20	4	25.1	100.4	
	M30高强螺栓	10.9S	M30x200	320	1.94	620.8	

中交第二公路勘察设计研究院有限公司	狮子洋通道工程勘察设计 施 工 图 设 计	K6+418.3 新沙高架桥 中桥节段04设计图	设计	余汪千	复核	袁勤	一审	沈华	二审	王忠	图号	SZYS/04/02/02/01/ 12

72510071135935

节段04材料数量表

名称	编号	材质	规格	数量	单件重	共重（kg）	备注
上弦顶板	N11a	Q355D	t=20mm,A=15.29m2	1	2399.9	2399.9	
	N11b	Q355D	t=20mm,A=13.73m2	1	2155.8	2155.8	
上弦底板	N12a	Q355D	□7901×1200×20	1	1488.4	1488.4	
	N12b	Q355D	□7101×1200×20	1	1337.6	1337.6	
上弦节点板	N13	Q355D	t=40mm,A=23.53m2	2	7387.4	14774.8	
上弦腹板	N14	Q355D	□7301×2048×32	2	3755.4	7510.8	
上弦横隔板	N15	Q355D	□1980×1200×16	3	298.9	896.7	
	N15a	Q355D	□1980×1200×16	2	298.9	597.8	
	N15‘	Q355D	□2057×200×16	3	51.5	154.5	
	N15b	Q355B	□2057×40×4	4	2.5	10	
	N15c	Q355D	□800×400×16	4	40.2	160.8	
上弦加劲肋	N16a	Q355D	□7901×240×20	6	298.3	1789.8	
	N16b	Q355D	□7101×240×20	6	266.9	1601.4	
下弦顶板	N21a	Q355D	□7903×2500×20	1	3102.3	3102.3	
	N21b	Q355D	□7102×2500×20	1	2788.3	2788.3	
下弦底板	N22a	Q355D	t=20mm,A=12.96m2	1	2034.9	2034.9	
	N22b	Q355D	t=20mm,A=11.13m2	1	1748	1748	
下弦节点板	N23	Q355D	t=40mm,A=20.85m2	2	6547.5	13095	Z35钢
下弦腹板	N24	Q355D	□7302×1880×24	2	2586.7	5173.4	
下弦横隔板	N25	Q355D	□1800×1200×16	3	271.3	813.9	
	N25a	Q355D	□1800×1200×16	2	271.3	542.6	
	N25’	Q355D	□2057×200×16	5	51.5	257.5	
下弦加劲肋	N26a	Q355D	□7903×240×20	4	298.3	1193.2	
	N26b	Q355D	□7102×240×20	4	266.9	1067.6	
	N26c	Q355D	□15005×170×14	2	280.2	560.4	
斜腹杆	N31	Q355D	□8788×900×36	2	2235.4	4470.8	
	N32	Q355D	□13288×1200×32	1	4006.6	4006.6	
	N33	Q355D	□11888×240×24	2	536.9	1073.8	
	N41	Q355D	□6225×1200×36	1	2111	2111	
	N41a	Q355D	□6225×1200×36	1	2111	2111	
	N42	Q355D	□4225×1360×36	2	1625	3250	
	N43	Q355D	□4225×320×32	2	339.1	678.2	
	N43a	Q355D	□5525×320×32	1	444.6	444.6	
	N43b	Q355D	□5525×320×32	1	444.6	444.6	
	N44	Q355D	□1200×1200×16	3	180.9	542.7	
节点板加劲	N51	Q355D	□4322×900×36	2	1099.3	2198.6	
	N52	Q355D	□6522×1200×32	1	1966.9	1966.9	
	N53	Q355D	□5122×240×24	2	231.7	463.4	
	N54	Q355D	□2300×320×32	2	185.9	371.8	
横梁接头	N61	Q355D	□1980×610×14	6	133	798	
	N61a	Q355D	□1980×618×14	4	134.1	536.4	
	N62	Q355D	t=24mm,A=0.47m2	6	89.3	535.8	
	N62a	Q355D	t=24mm,A=0.48m2	4	90.4	361.6	
	N63	Q355D	□1800×610×14	6	120.9	725.4	
	N63a	Q355D	□1800×626×14	4	124.2	496.8	
小计						94843.4	
焊缝重1.5%						1423.0	
合计						96266.4	

节段04材料数量汇总表

规格（mm）	材质	单个合计	全桥共1个
t=40	Q355D	27869.8	27869.8
t=36		14141.4	14141.4
t=32		15423.5	15423.5
t=24		7608	7608
t=20		22707.2	22707.2
t=16		3966.5	3966.5
t=14		3117	3117
t=4		10	10
焊缝重（1.5%）		1422.7	1422.7
合计	Q355D	96266.1	96266.1
内表面涂装（m²）		254.8	254.8
外表面涂装（m²）		636.2	636.2

节段3~节段4拼接数量汇总表

规格（mm）	材质	单个合计	全桥共1个
t=32	Q355D	535	535
t=28		2163.1	2163.1
t=20		1956.8	1956.8
t=16		871.8	871.8
合计		5526.7	5526.7
M30x200	10.9S高强螺栓	2234.9	2234.9
外表面涂装（m²）		31.4	31.4

大样A（节段4~节段5）

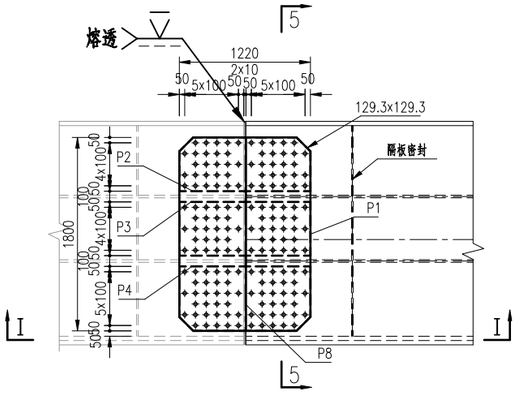

5-5

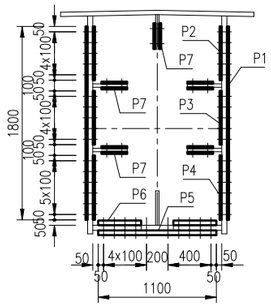

Ⅰ－Ⅰ

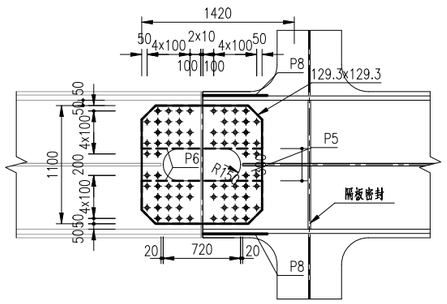

上弦杆顶板、腹板加劲肋拼接

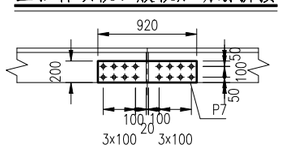

大样C（节段4~节段5）

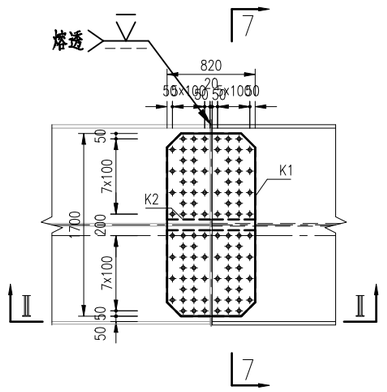

7-7

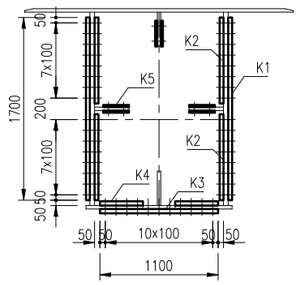

Ⅳ－Ⅳ

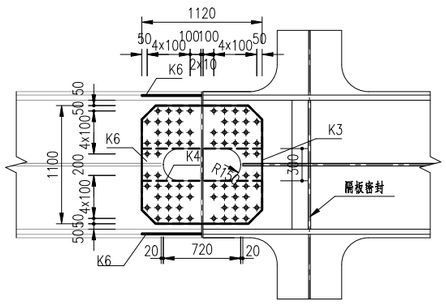

下弦杆顶板、腹板加劲肋拼接

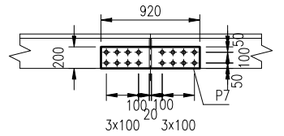

注：

1、本图尺寸均以mm计。

2、未注明的板件裁切边距M30螺栓不小50mm，M24螺栓不小40mm。

3、图中未注明的过焊孔圆弧切角半径为35mm。

4、图中未注明焊缝详见《钢梁焊缝及细节设计图》。

符号：

—— M30螺栓，开孔直径33mm

—— M24螺栓，开孔直径26mm

大样B（节段4~节段5）

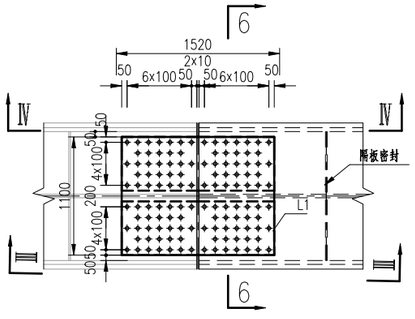

6-6

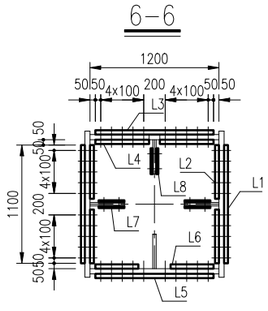

腹杆腹板加劲肋拼接

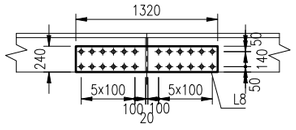

腹杆顶加劲肋拼接

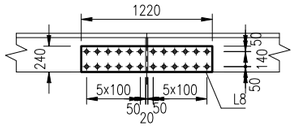

Ⅲ－Ⅲ

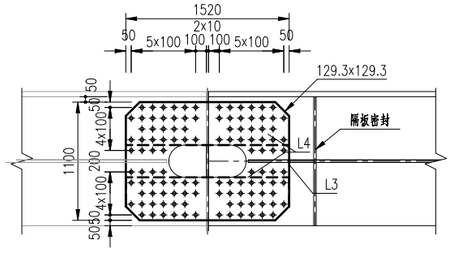

Ⅳ－Ⅳ

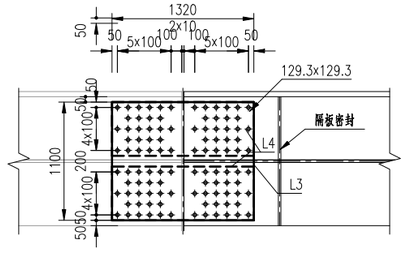

节段4~节段5拼接数量表

名称	编号	材质	规格	数量	单件重	共重（kg）	备注
上弦杆拼接	P1	Q355D	□1220×1800×28	2	483.6	967.2	
	P2		□1220×500×28	2	134.1	268.2	
	P3		□1220×500×28	2	134.1	268.2	
	P4		□1220×600×28	2	160.5	321	
	P5		□1420×1100×32	1	391.9	391.9	
	P6		□1420×400×32	2	143.2	286.4	
	P7		□920×200×20	10	28.3	283	
	P8		□600×1800×8	2	67.8	135.6	
	M30高强螺栓	10.9S	M30×200	508	1.94	985.5	
下弦杆拼接	K1	Q355D	□820×1700×20	2	218.2	436.4	
	K2		□820×800×20	4	103.6	414.4	
	K3		□1120×1100×32	1	309	309	
	K4		□1120×400×32	2	113	226	
	K5		□920×200×20	6	28.3	169.8	
	K6		□400×1700×16	2	85.4	170.8	
	M30高强螺栓	10.9S	M30×200	324	1.94	628.6	
腹杆拼接	L1	Q355D	□1320×1100×20	2	227.7	455.4	
	L2		□1320×500×20	4	103.6	414.4	
	L3		□1120×1100×24	1	231.7	231.7	
	L4		□1120×500×24	2	105.5	211	
	L5		□1320×1100×36	1	409.8	409.8	
	L6		□1320×240×36	2	90.4	180.8	
	L7		□1220×240×24	4	54.6	218.4	
	L8		□1221×240×24	2	54.6	109.2	
	M30高强螺栓	10.9S	M30×200	507	1.94	983.6	

中交第二公路勘察设计研究院有限公司	狮子洋通道工程勘察设计 施 工 图 设 计	K6+418.3 新沙高架桥 中桥节段05设计图	设计	余汪千	复核	袁勤	一审	张华	二审	李忠	图号	SZYS/04/02/02/01/ 13

节段05材料数量表

名称	编号	材质	规格	数量	单件重	共重（kg）	备注
上弦顶板	N11a	Q420D	t=40mm,A=15.29m2	1	4799.9	4799.9	
	N11b	Q355D	t=24mm,A=13.73m2	1	2587	2587	
上弦底板	N12a	Q420D	□7901×1200×40	1	2976.7	2976.7	
	N12b	Q355D	□7101×1200×24	1	1605.2	1605.2	
上弦节点板	N13	Q420D	t=48mm,A=24.57m2	2	9257.5	18515	
上弦腹板	N14	Q355D	□7301×2048×32	2	3755.4	7510.8	
上弦横隔板	N15	Q355D	□1960×1200×16	3	295.2	885.6	
	N15a	Q355D	□1976×1200×16	2	297.7	595.4	
	N15‘	Q355D	□2057×200×16	3	51.5	154.5	
	N15b	Q355B	□2057×40×4	4	2.5	10	
	N15c	Q355D	□800×400×16	4	40.2	160.8	
上弦加劲肋	N16a	Q420D	□7901×320×32	6	635.5	3813	
	N16b	Q355D	□7101×240×20	6	266.9	1601.4	
下弦顶板	N21a	Q355D	□7903×2500×20	1	3102.3	3102.3	
	N21b	Q355D	□7102×2500×24	1	3346	3346	
下弦底板	N22a	Q355D	t=24mm,A=12.96m2	1	2441.8	2441.8	
	N22b	Q355D	t=20mm,A=11.13m2	1	1748	1748	
下弦节点板	N23	Q355D	t=40mm,A=22.57m2	2	7087.2	14174.4	Z35钢
下弦腹板	N24	Q355D	□7302×1880×32	2	3449	6898	
下弦横隔板	N25	Q355D	□1800×1200×16	3	271.3	813.9	
	N25a	Q355D	□1800×1200×16	2	271.3	542.6	
	N25’	Q355D	□2057×200×16	5	51.5	257.5	
下弦加劲肋	N26a	Q355D	□7903×240×20	4	298.3	1193.2	
	N26b	Q355D	□7102×320×32	4	570.2	2280.8	
	N26c	Q355D	□15005×170×14	2	280.2	560.4	
斜腹杆	N31	Q355D	□12581×1200×36	1	4267.3	4267.3	
	N31a	Q355D	□12381×1200×36	1	4199.4	4199.4	
	N32	Q355D	□8581×1360×36	2	3297.9	6595.8	
	N33	Q355D	□8581×320×32	2	690.8	1381.6	
	N33a	Q355D	□11181×320×32	1	899.3	899.3	
	N33b	Q355D	□10981×320×32	1	881.7	881.7	
	N34	Q355D	□1200×1200×16	3	180.9	542.7	
	N41	Q355D	□6135×1200×36	1	2079.9	2079.9	
	N41a	Q355D	□6135×1200×36	1	2079.9	2079.9	
	N42	Q355D	□4135×1360×36	2	1588.2	3176.4	
	N43	Q355D	□4135×320×32	2	331.6	663.2	
	N43a	Q355D	□5435×320×32	1	437.1	437.1	
	N43b	Q355D	□5435×320×32	1	437.1	437.1	
	N44	Q355D	□1200×1200×16	3	180.9	542.7	
节点板加劲	N51	Q355D	□6425×1200×36	1	2178.8	2178.8	
	N51a	Q355D	□6025×1200×36	1	2043.2	2043.2	
	N52	Q355D	□4225×1360×36	2	1625	3250	
	N53	Q355D	□4225×320×32	2	339.1	678.2	
	N53a	Q355D	□5725×320×32	1	459.7	459.7	
	N53b	Q355D	□5325×320×32	1	427	427	
	N54	Q355D	□1200×1200×16	3	180.9	542.7	
	N55	Q355D	□2300×320×32	4	185.9	743.6	
	N56	Q355D	□2200×320×32	4	175.8	703.2	
横梁接头	N61	Q355D	□1960×602×14	6	129.7	778.2	
	N61a	Q355D	□1976×618×14	4	134.1	536.4	
	N62	Q355D	t=24mm,A=0.47m2	6	89.3	535.8	
	N62a	Q355D	t=24mm,A=0.48m2	4	90.4	361.6	
	N63	Q355D	□1800×610×14	6	120.9	725.4	
	N63a	Q355D	□1800×618×14	4	122	488	
小计						125210.1	
焊缝重1.5%						1878.0	
合计						127088.1	

节段05材料数量汇总表

规格（mm）	材质	单个合计	全桥共1个
t=48	Q420D	18515	18515.0
t=40		7776.6	7776.6
t=32		3813	3813.0
合计		30104.6	30104.6
t=40	Q355D	14174.4	14174.4
t=36		29870.7	29870.7
t=32		24401.3	24401.3
t=24		10877.4	10877.4
t=20		7644.9	7644.9
t=16		5038.4	5038.4
t=14		3088.4	3088.4
t=4		10	10.0
合计		95105.5	95105.5
焊缝重（1.5%）		1878.0	1878.0
内表面涂装（m²）		394.1	394.1
外表面涂装（m²）		629.9	629.9

节段4~节段5拼接数量汇总表

规格（mm）	材质	单个合计	全桥共1个
t=36	Q355D	590.6	590.6
t=32		1213.3	1213.3
t=28		1824.6	1824.6
t=24		770.3	770.3
t=20		2173.4	2173.4
t=16		170.8	170.8
t=8		135.6	135.6
合计		6878.6	6878.6
M30x200	10.9S高强螺栓	2597.7	2597.7
外表面涂装（m²）		36.7	36.7

中交第二公路勘察设计研究院有限公司	狮子洋通道工程勘察设计 施 工 图 设 计	K6+418.3 新沙高架桥 中桥节段05设计图	设计	余汪千	复核	袁勤	一审	沈华	二审	李忠	图号	SZYS/04/02/02/01/13

大样A（节段5~节段6）

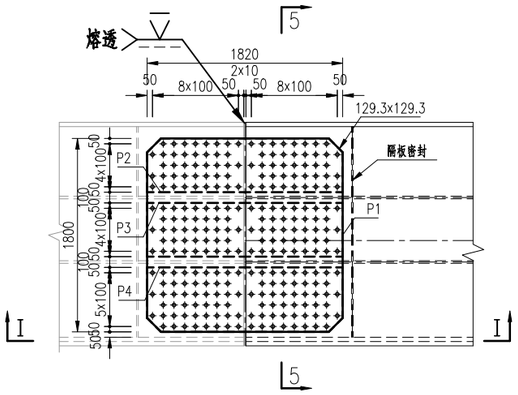

5-5

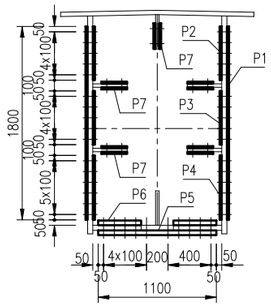

I－I

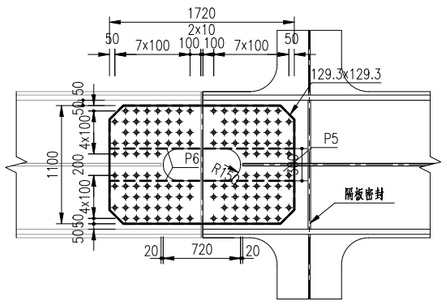

上弦杆顶板、腹板加劲肋拼接

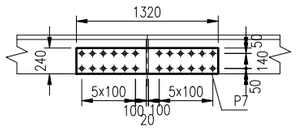

大样C（节段5~节段6）

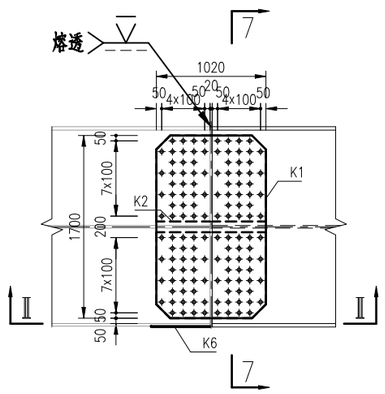

7-7

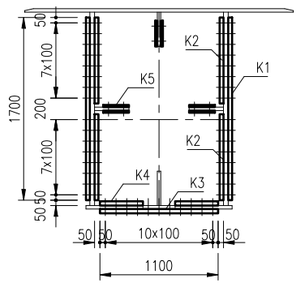

Ⅳ－Ⅳ

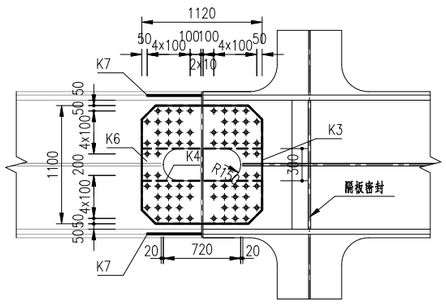

下弦杆顶板、腹板加劲肋拼接

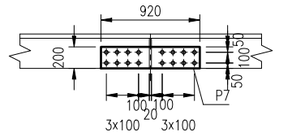

注：

1、本图尺寸均以mm计。

2、未注明的板件裁切边距M30螺栓不小50mm，M24螺栓不小40mm。

3、图中未注明的过焊孔圆弧切角半径为35mm。

4、图中未注明焊缝详见《钢梁焊缝及细节设计图》。

符号：

—— M30螺栓，开孔直径33mm

—— M24螺栓，开孔直径26mm

大样B（节段4~节段5）

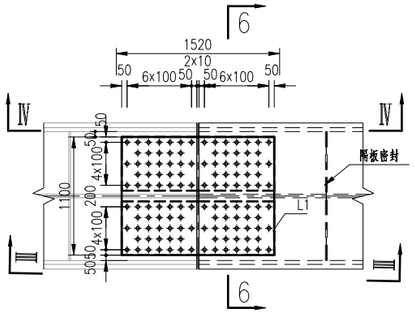

6-6

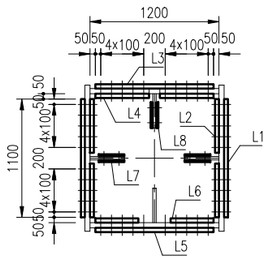

腹杆腹板加劲肋拼接

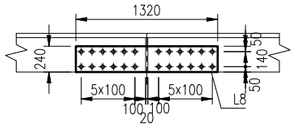

腹杆顶加劲肋拼接

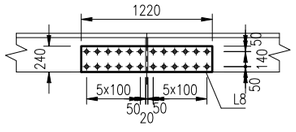

Ⅲ－Ⅲ

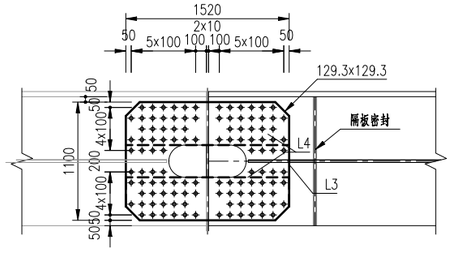

Ⅳ－Ⅳ

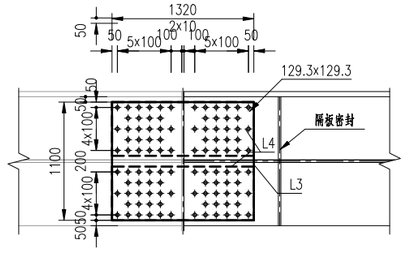

节段5~节段6拼接数量表

名称	编号	材质	规格	数量	单件重	共重（kg）	备注
上弦杆拼接	P1	Q420D	□1820×1800×40	2	1029.9	2059.8	
	P2		□1820×500×40	2	285.7	571.4	
	P3		□1820×500×40	2	285.7	571.4	
	P4		□1820×600×40	2	342.3	684.6	
	P5		□1720×1100×44	1	652.8	652.8	
	P6		□1720×400×44	2	238.3	476.6	
	P7		□1320×240×24	10	60.3	603	
	M30高强螺栓	10.9S	M30x200	780	1.94	1513.2	
下弦杆拼接	K1	Q355D	□1020×1700×20	2	271.6	543.2	
	K2		□1020×800×20	4	128.7	514.8	
	K3		□1120×1100×32	1	309	309	
	K4		□1120×400×32	2	113	226	
	K5		□920×200×14	6	19.8	118.8	
	K6		□550×1100×8	1	38.3	38.3	
	K7		□500×1700×16	2	106.8	213.6	
	M30高强螺栓	10.9S	M30x200	388	1.94	752.7	
腹杆拼接	L1	Q355D	□1520×1100×24	2	314.6	629.2	
	L2		□1520×500×24	4	143.2	572.8	
	L3		□1320×1100×28	1	318.7	318.7	
	L4		□1320×500×28	2	145.1	290.2	
	L5		□1520×1100×44	1	576.8	576.8	
	L6		□1520×240×44	2	124.3	248.6	
	L7		□1220×240×24	4	54.6	218.4	
	L8		□1320×240×24	2	60.3	120.6	
	M30高强螺栓	10.9S	M30x200	540	1.94	1047.6	

中交第二公路勘察设计研究院有限公司	狮子洋通道工程勘察设计 施 工 图 设 计	K6+418.3 新沙高架桥 中桥节段06设计图	设计	余汪千	复核	袁勤	一审	张华	二审	李忠	图号	SZYS/04/02/02/01/ 14

节段06材料数量表

名称	编号	材质	规格	数量	单件重	共重（kg）	备注
上弦顶板	N11a	Q420D	t=40mm,A=15.29m2	1	4799.9	4799.9	
	N11b	Q420D	t=40mm,A=13.73m2	1	4311.7	4311.7	
上弦底板	N12a	Q420D	□7901×1200×40	1	2976.7	2976.7	
	N12b	Q420D	□7101×1200×40	1	2675.3	2675.3	
上弦节点板	N13	Q420D	t=48mm,A=25.5m2	2	9608.4	19216.8	
上弦腹板	N14	Q420D	□7301×2048×48	2	5633.2	11266.4	
上弦横隔板	N15	Q420D	□1960×1200×16	3	295.2	885.6	
	N15a	Q420D	□1960×1200×16	2	295.2	590.4	
	N15 ‘	Q420D	□2057×200×16	3	51.5	154.5	
	N15b	Q355B	□2057×40×4	4	2.5	10	
	N15c	Q420D	□800×400×16	4	40.2	160.8	
上弦加劲肋	N16a	Q420D	□7901×320×32	6	635.5	3813	
	N16b	Q420D	□7101×320×32	6	570.2	3421.2	
下弦顶板	N21a	Q420D	□7903×2500×32	1	4963.7	4963.7	
	N21b	Q420D	□7102×2500×32	1	4461.3	4461.3	
下弦底板	N22a	Q420D	t=32mm,A=12.96m2	1	3255.8	3255.8	
	N22b	Q420D	t=32mm,A=11.13m2	1	2796.8	2796.8	
下弦节点板	N23	Q420D	t=48mm,A=22.56m2	2	8499.9	16999.8	Z35钢
下弦腹板	N24	Q420D	□7302×1880×44	2	4742.3	9484.6	
下弦横隔板	N25	Q420D	□1800×1200×16	3	271.3	813.9	
	N25a	Q420D	□1800×1200×16	2	271.3	542.6	
	N25’	Q420D	□2057×200×16	3	51.5	154.5	
下弦加劲肋	N26a	Q420D	□7903×320×32	4	635.5	2542	
	N26b	Q420D	□7102×320×32	4	570.2	2280.8	
	N26c	Q420D	□15005×170×14	2	280.2	560.4	
斜腹杆	N31	Q355D	□12189×1200×36	1	4134.4	4134.4	
	N31a	Q355D	□12189×1200×36	1	4134.4	4134.4	
	N32	Q355D	□8389×1360×36	2	3224.5	6449	
	N33	Q355D	□8389×320×32	2	673.2	1346.4	
	N33a	Q355D	□10789×320×32	1	866.6	866.6	
	N33b	Q355D	□10789×320×32	1	866.6	866.6	
	N34	Q355D	□1200×1200×16	3	180.9	542.7	
	N41	Q355D	□5843×1200×40	1	2201.1	2201.1	
	N41a	Q355D	□6043×1200×40	1	2276.5	2276.5	
	N42	Q355D	□4043×1360×40	2	1727	3454	
	N43	Q355D	□4043×320×32	4	324	1296	
	N43a	Q355D	□5143×320×32	1	414.5	414.5	
	N43b	Q355D	□5343×320×32	1	429.6	429.6	
	N44	Q355D	□1200×1200×16	2	180.9	361.8	
	N51	Q420D	□5925×1200×40	1	2232.5	2232.5	
	N51a	Q420D	□6125×1200×40	1	2307.9	2307.9	
	N52	Q420D	□4125×1360×40	2	1761.5	3523	
	N53	Q420D	□4125×320×32	4	331.6	1326.4	
	N53a	Q420D	□5225×320×32	1	419.5	419.5	
	N53b	Q420D	□5425×320×32	1	437.1	437.1	
	N54	Q420D	□1200×1200×16	2	180.9	361.8	
节点板加劲	N55	Q420D	□2100×320×32	6	168.3	1009.8	
	N56	Q420D	□2200×320×32	4	175.8	703.2	
横梁接头	N61	Q355D	□1960×602×14	6	129.7	778.2	
	N61a	Q355D	□1960×602×14	4	129.7	518.8	
	N62	Q355D	t=24mm,A=0.47m2	6	89.3	535.8	
	N62a	Q355D	t=24mm,A=0.48m2	4	90.4	361.6	
	N63	Q355D	□1800×602×14	6	118.7	712.2	
	N63a	Q355D	□1800×606×14	4	119.8	479.2	
小计						147619.1	
焊缝重1.5%						2214.0	
合计						149833.1	

节段06材料数量汇总表

规格（mm）	材质	单个合计	全桥共1个
t=48	Q420D	47483	47483.0
t=44		9484.6	9484.6
t=40		22827	22827.0
t=32		31430.6	31430.6
t=16		3664.1	3664.1
t=14		560.4	560.4
合计		115459.7	115459.7
t=40	Q355D	7931.6	7931.6
t=36		14717.8	14717.8
t=32		5219.7	5219.7
t=24		897.4	897.4
t=16		904.5	904.5
t=14		2488.4	2488.4
合计		32159.4	32159.4
焊缝重（1.5%）		2214.0	2214.0
内表面涂装（㎡）		411.5	411.5
外表面涂装（㎡）		625.7	625.7

节段5~节段6拼接数量表汇总

规格（mm）	材质	单个合计	全桥共1个
t=44	Q420D	1129.4	1129.4
t=40		3887.2	3887.2
t=24		603	603
合计		5619.6	5619.6
t=44	Q355D	825.4	825.4
t=32		535	535
t=28		608.9	608.9
t=24		1541	1541
t=20		1058	1058
t=16		213.6	213.6
t=14		118.8	118.8
t=8		38.3	38.3
合计		4939.0	4939.0
M30x200	10.9S高强螺栓	3313.5	3313.5
外表面涂装（㎡）		44.5	44.5

中交第二公路勘察设计研究院有限公司	狮子洋通道工程勘察设计 施 工 图 设 计	K6+418.3 新沙高架桥 中桥节段06设计图	设计	余汪千	复核	袁勤	一审	沈华	二审	王忠	图号	SZYS/04/02/02/01/ 14

大样A（节段6~节段7）

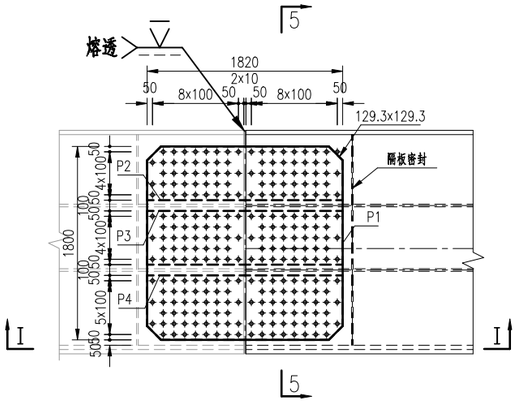

5-5

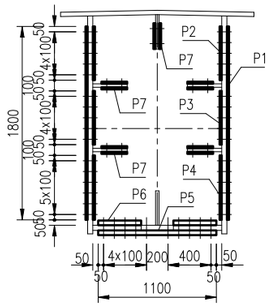

大样C（节段6~节段7）

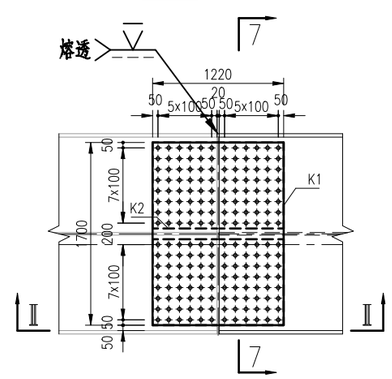

7-7

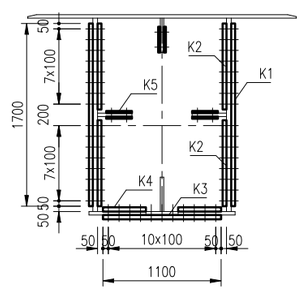

Ⅰ-Ⅰ

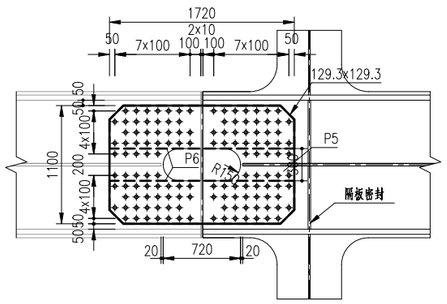

上弦杆顶板、腹板加劲肋拼接

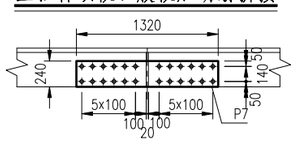

Ⅳ-Ⅳ

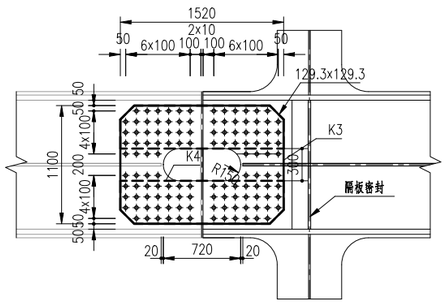

下弦杆顶板、腹板加劲肋拼接

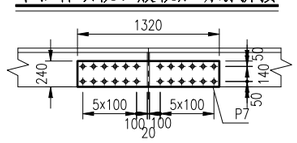

大样B（节段6~节段7）

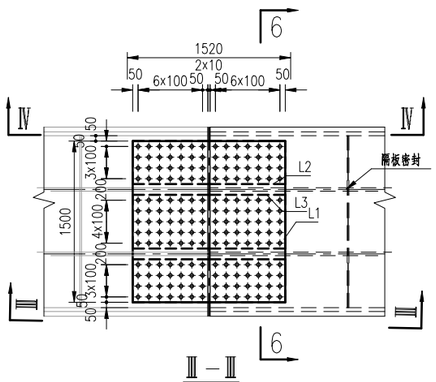

6-6

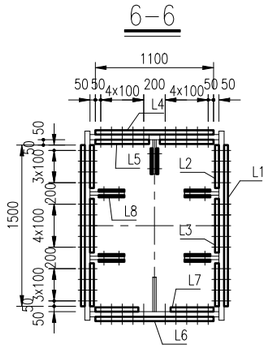

腹杆腹板加劲肋拼接

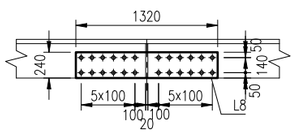

腹杆顶加劲肋拼接

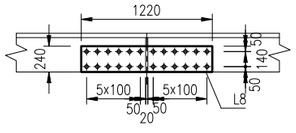

Ⅲ-Ⅲ

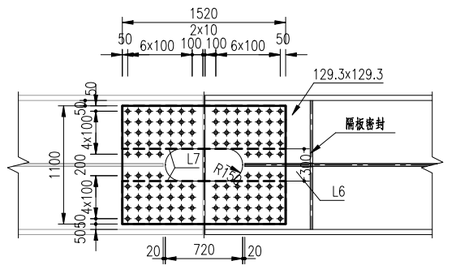

Ⅳ-Ⅳ

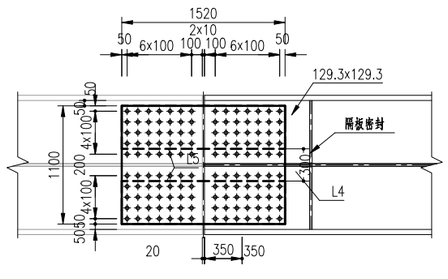

节段6~节段7拼接数量表

名称	编号	材质	规格	数量	单件重	共重（kg）	备注
上弦杆拼接	P1	Q420D	□1820×1800×40	2	1029.9	2059.8	
	P2		□1820×500×40	2	285.7	571.4	
	P3		□1820×500×40	2	285.7	571.4	
	P4		□1820×600×40	2	342.3	684.6	
	P5		□1720×1100×44	1	652.8	652.8	
	P6		□1720×400×44	2	238.3	476.6	
	P7		□1320×240×24	10	60.3	603	
	M30高强螺栓	10.9S	M30x200	780	1.94	1513.2	
下弦杆拼接	K1	Q420D	□1220×1700×28	2	455	910	
	K2		□1220×800×28	4	215.4	861.6	
	K3		□1520×1100×36	1	471.9	471.9	
	K4		□1520×400×36	2	172.4	344.8	
	K5		□1320×240×24	6	60.3	361.8	
	M30高强螺栓	10.9S	M30x200	580	1.94	1125.2	
腹杆拼接	L1	Q420D	□1520×1500×32	2	572.7	1145.4	
	L2		□1520×400×32	4	153.2	612.8	
	L3		□1520×500×32	2	190.9	381.8	
	L4		□1520×1100×28	1	367.1	367.1	
	L5		□1520×500×28	2	167	334	
	L6		□1520×1100×40	1	524.4	524.4	
	L7		□1520×400×40	2	191.5	383	
	L8		□1320×240×24	10	60.3	603	
	M30高强螺栓	10.9S	M30x200	752	1.94	1458.9	

中交第二公路勘察设计研究院有限公司	狮子洋通道工程勘察设计 施 工 图 设 计	K6+418.3 新沙高架桥 中桥节段07设计图	设计	余汪千	复核	李勤	一审	张华	二审	李忠	图号	SZYS/04/02/02/01/ 15

725000885555

节段07材料数量表

名称	编号	材质	规格	数量	单件重	共重(kg)	备注
上弦顶板	N11a	Q420D	t=40mm,A=15.55m2	1	4883	4883	
	N11b	Q420D	t=40mm,A=13.82m2	1	4338.5	4338.5	
上弦底板	N12a	Q420D	□8039×1200×40	2	3030.1	6060.2	
	N12b	Q420D	□6940×1200×40	1	2615.6	2615.6	
上弦节点板	N13	Q420D	t=44mm,A=26.09m2	2	9011.5	18023	
上弦腹板	N14	Q420D	□7140×2048×48	2	5508.8	11017.6	
上弦横隔板	N15	Q420D	□1960×1200×16	3	295.2	885.6	
	N15a	Q420D	□1960×1200×16	2	295.2	590.4	
	N15‘	Q420D	□2057×200×16	3	51.5	154.5	
	N15b	Q355B	□2057×40×4	4	2.5	10	
	N15c	Q420D	□800×400×16	4	40.2	160.8	
上弦加劲肋	N16a	Q420D	□8039×320×32	6	645.6	3873.6	
	N16b	Q420D	□6940×320×32	6	557.7	3346.2	
下弦顶板	N21a	Q420D	□8040×2500×32	1	5049.1	5049.1	
	N21b	Q420D	□6941×2500×32	1	4358.3	4358.3	
下弦底板	N22a	Q420D	t=40mm,A=17.43m2	1	5472.1	5472.1	
	N22b	Q420D	t=32mm,A=10.91m2	1	2741.5	2741.5	
下弦节点板	N23	Q420D	t=44mm,A=24.21m2	2	8362	16724	Z35钢
下弦腹板	N24	Q420D	□7141×1880×44	2	4638.7	9277.4	
下弦横隔板	N25	Q420D	□1800×1200×16	2	271.3	542.6	
	N25a	Q420D	□1800×1200×16	2	271.3	542.6	
	N25’	Q420D	□2057×200×16	2	51.5	103	
下弦加劲肋	N26a	Q420D	□8040×320×32	4	645.6	2582.4	
	N26b	Q420D	□6941×320×32	4	557.7	2230.8	
	N26c	Q420D	□14981×170×14	2	280.2	560.4	
斜腹杆	N31	Q420D	□11812×1200×40	1	4449.4	4449.4	
	N31a	Q420D	□12012×1200×40	1	4524.7	4524.7	
	N32	Q420D	□8212×1760×40	2	4537.3	9074.6	
	N33	Q420D	□8212×320×32	4	660.7	2642.8	
	N33a	Q420D	□10412×320×32	1	836.5	836.5	
	N33b	Q420D	□10612×320×32	1	854.1	854.1	
	N34	Q420D	□1200×1600×16	3	241.2	723.6	
	N41	Q420D	□5769×1200×40	1	2172.9	2172.9	
	N41a	Q420D	□5969×1200×40	1	2248.2	2248.2	
	N42	Q420D	□3969×1760×40	2	2194.9	4389.8	
	N43	Q420D	□3969×320×32	4	319	1276	
	N43a	Q420D	□5069×320×32	1	406.9	406.9	
	N43b	Q420D	□5269×320×32	1	424.5	424.5	
	N44	Q420D	□1200×1600×16	2	241.2	482.4	
	N51	Q420D	□5853×1200×40	1	2204.3	2204.3	
	N51a	Q420D	□6053×1200×40	1	2279.6	2279.6	
	N52	Q420D	□4053×1760×40	2	2238.8	4477.6	
	N53	Q420D	□4053×320×32	4	326.6	1306.4	
	N53a	Q420D	□5153×320×32	1	414.5	414.5	
	N53b	Q420D	□5353×320×32	1	429.6	429.6	
	N54	Q420D	□1200×1600×16	2	241.2	482.4	
节点板加劲	N55	Q420D	□2100×320×32	8	168.3	1346.4	
	N56	Q420D	□2000×320×32	8	160.8	1286.4	
横梁接头	N61	Q355D	□1960×606×14	6	130.8	784.8	
	N61a	Q355D	□1960×602×14	4	129.7	518.8	
	N62	Q355D	t=24mm,A=0.47m2	4	89.3	357.2	
	N62a	Q355D	t=24mm,A=0.48m2	4	90.4	361.6	
	N63	Q355D	□1800×606×14	4	119.8	479.2	
	N63a	Q355D	□1800×606×14	6	119.8	718.8	
支座加劲	N81	Q420D	□1800×1200×32	5	542.6	2713	
	N82	Q420D	□1800×602×44	6	373	2238	
	N83	Q420D	□2800×2650×100	1	5824.7	5824.7	
	N84	Q420D	□1000×568×32	4	143.2	572.8	
	N85	Q420D	□1350×570×32	4	193.4	773.6	
小计						170219.3	
焊缝重1.5%						2553.0	
合计						172772.3	

节段07材料数量汇总表

规格(mm)	材质	单个合计	全桥共1个
t=100	Q420D	5824.7	5824.7
t=48		11017.6	11017.6
t=44		46262.4	46262.4
t=40		59190.5	59190.5
t=32		38691.8	38691.8
t=16		4667.9	4667.9
t=14		560.4	560.4
t=4		10	10
合计		166225.3	166225.3
t=32	Q355D	773.6	773.6
t=24		718.8	718.8
t=14		2501.6	2501.6
合计		3994	3994
焊缝重(1.5%)		2553	2553
内表面涂装(m²)		410.4	410.4
外表面涂装(m²)		760.3	760.3

节段6~节段7拼接数量表汇总

规格(mm)	材质	单个合计	全桥共1个
t=44	Q420D	1129.4	1129.4
t=40		4794.6	4794.6
t=36		816.7	816.7
t=32		2140	2140
t=28		2472.7	2472.7
t=24		1567.8	1567.8
合计		12921.2	12921.2
M30x200	10.9S高强螺栓	4097.3	4097.3
外表面涂装(m²)		49.5	49.5

中交第二公路勘察设计研究院有限公司	狮子洋通道工程勘察设计 施 工 图 设 计	K6+418.3 新沙高架桥 中桥节段07设计图	设计	余汪千	复核	袁勤	一审	沈华	二审	李忠	图号	SZYS/04/02/02/01/15

大样A（节段7~节段8）

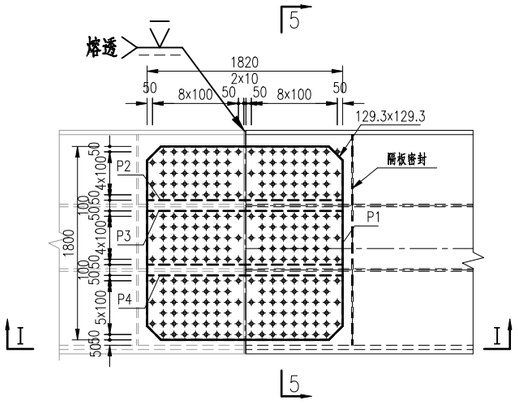

5-5

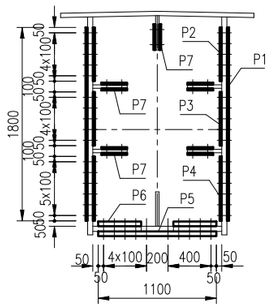

大样C（节段7~节段8）

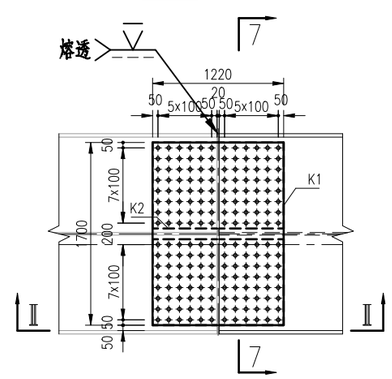

7-7

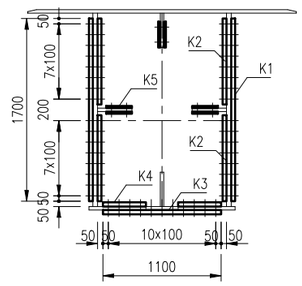

Ⅰ－Ⅰ

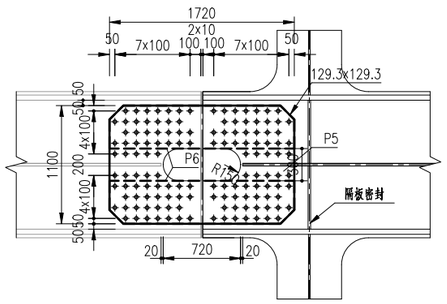

上弦杆顶板、腹板加劲肋拼接

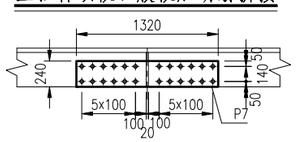

Ⅳ－Ⅳ

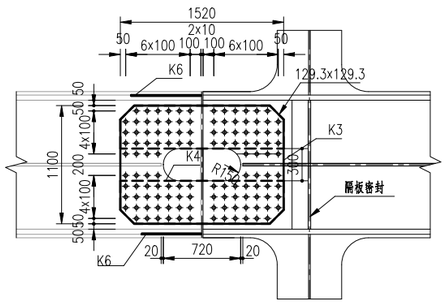

下弦杆顶板、腹板加劲肋拼接

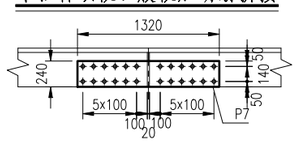

注：

1、本图尺寸均以mm计。

2、未注明的板件裁切边距M30螺栓不小50mm，M24螺栓不小40mm。

3、图中未注明的过焊孔圆弧切角半径为35mm。

4、图中未注明焊缝详见《钢梁焊缝及细节设计图》。

符号：

⊕ —— M30螺栓，开孔直径33mm

⊗ —— M24螺栓，开孔直径26mm

大样B（节段7~节段8）

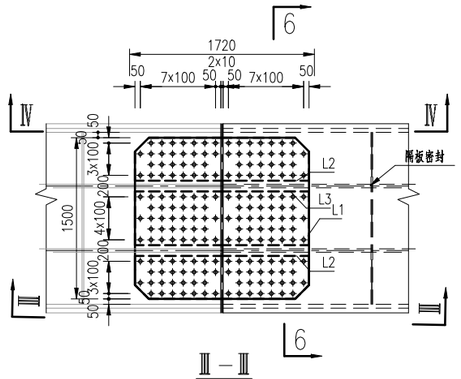

6-6

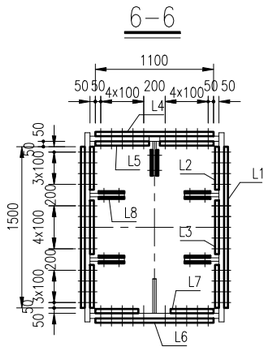

腹杆腹板加劲肋拼接

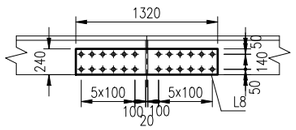

腹杆顶加劲肋拼接

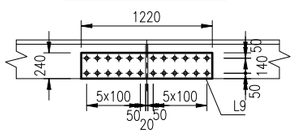

Ⅲ－Ⅲ

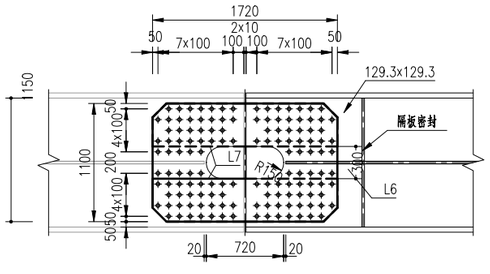

Ⅳ－Ⅳ

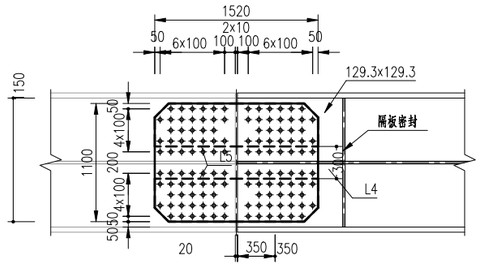

节段7~节段8拼接数量表

名称	编号	材质	规格	数量	单件重	共重（kg）	备注
上弦杆拼接	P1	Q420D	□1820×1800×40	2	1029.9	2059.8	
	P2		□1820×500×40	2	285.7	571.4	
	P3		□1820×500×40	2	285.7	571.4	
	P4		□1820×600×40	2	342.3	684.6	
	P5		□1720×1100×44	1	652.8	652.8	
	P6		□1720×400×44	2	238.3	476.6	
	P7		□1320×240×24	10	60.3	603	
	M30高强螺栓	10.9S	M30x200	780	1.94	1513.2	
下弦杆拼接	K1	Q420D	□1220×1700×28	2	455	910	
	K2		□1220×800×28	4	215.4	861.6	
	K3		□1520×1100×36	1	471.9	471.9	
	K4		□1520×400×36	2	172.4	344.8	
	K5		□1320×240×24	6	60.3	361.8	
	K6		□650×1100×4	1	22.6	22.6	填板
	M30高强螺栓	10.9S	M30x200	580	1.94	1125.2	
腹杆拼接	L1	Q420D	□1720×1500×36	2	729.1	1458.2	
	L2		□1720×400×36	4	195	780	
	L3		□1720×500×36	2	243	486	
	L4		□1720×1100×32	1	474.8	474.8	
	L5		□1720×500×32	2	216	432	
	L6		□1520×1100×48	1	629.3	629.3	
	L7		□1520×400×48	2	229.8	459.6	
	L8		□1320×240×24	8	60.3	482.4	
	L9		□1220×240×24	2	54.6	109.2	
	M30高强螺栓	10.9S	M30x200	752	1.94	1458.9	

中交第二公路勘察设计研究院有限公司	狮子洋通道工程勘察设计 施 工 图 设 计	K6+418.3 新沙高架桥 中桥节段08设计图	设计	余汪千	复核	袁勤	一审	张华	二审	李忠	图号	SZYS/04/02/02/01/ 16

72500008812611

节段08材料数量表

名称	编号	材质	规格	数量	单件重	共重（kg）	备注
上弦顶板	N11a	Q420D	t=40mm,A=15.28m2	1	4799.3	4799.3	
	N11b	Q420D	t=40mm,A=13.46m2	1	4226.3	4226.3	
上弦底板	N12a	Q420D	□7900×1200×40	1	2976.7	2976.7	
	N12b	Q420D	□6950×1200×40	1	2618.8	2618.8	
上弦节点板	N13	Q420D	t=44mm,A=25.76m2	2	8897.5	17795	
上弦腹板	N14	Q420D	□7150×2048×48	2	5516.4	11032.8	
上弦横隔板	N15	Q355D	□1960×1200×16	3	295.2	885.6	
	N15a	Q355D	□1960×1200×16	2	295.2	590.4	
	N15‘	Q355D	□2057×200×16	3	51.5	154.5	
	N15b	Q355B	□2057×40×4	4	2.5	10	
	N15c	Q355D	□800×400×16	4	40.2	160.8	
上弦加劲肋	N16a	Q420D	□7900×320×32	6	635.5	3813	
	N16b	Q420D	□6950×320×32	6	557.7	3346.2	
下弦顶板	N21a	Q420D	□8050×2500×32	1	5056.7	5056.7	
	N21b	Q355D	□7101×2500×24	1	3344.1	3344.1	
下弦底板	N22a	Q420D	t=32mm,A=13.16m2	1	3306	3306	
	N22b	Q355D	t=24mm,A=11.13m2	1	2097.4	2097.4	
下弦节点板	N23	Q420D	t=44mm,A=24.5m2	2	8462.3	16924.6	Z35钢
下弦腹板	N24	Q355D	□7301×1880×32	2	3449	6898	
下弦横隔板	N25	Q355D	□1800×1200×16	3	271.3	813.9	
	N25a	Q355D	□1800×1200×16	2	271.3	542.6	
	N25’	Q355D	□2057×200×16	3	51.5	154.5	
下弦加劲肋	N26a	Q420D	□8050×320×32	4	648.1	2592.4	
	N26b	Q355D	□7101×320×32	4	570.2	2280.8	
	N26c	Q355D	□15151×170×14	2	283.5	567	
斜腹杆	N31	Q355D	□11850×1200×40	1	4465.1	4465.1	
	N31a	Q355D	□11950×1200×40	1	4502.8	4502.8	
	N32	Q355D	□8050×1760×40	2	4449.4	8898.8	
	N33	Q355D	□8050×320×32	4	648.1	2592.4	
	N33a	Q355D	□10450×320×32	1	839	839	
	N33b	Q355D	□10550×320×32	1	849.1	849.1	
	N34	Q355D	□1200×1600×16	3	241.2	723.6	
	N41	Q355D	□5711×1200×36	1	1935.8	1935.8	
	N41a	Q355D	□6011×1200×36	1	2037.5	2037.5	
	N42	Q355D	□3911×1360×36	2	1503.4	3006.8	
	N43	Q355D	□3911×320×32	2	314	628	
	N43a	Q355D	□5011×320×32	1	401.9	401.9	
	N43b	Q355D	□5311×320×32	1	427	427	
	N44	Q355D	□1200×1200×16	2	180.9	361.8	
节点板加劲	N51	Q355D	□5979×1200×36	1	2026.2	2026.2	
	N51a	Q355D	□5779×1200×36	1	1958.4	1958.4	
	N52	Q355D	□3979×1760×36	2	1978.2	3956.4	
	N53	Q355D	□3979×320×32	4	319	1276	
	N53a	Q355D	□5279×320×32	1	424.5	424.5	
	N53b	Q355D	□5079×320×32	1	409.5	409.5	
	N54	Q355D	□1200×1600×16	2	241.2	482.4	
	N55	Q355D	□2100×320×32	6	168.3	1009.8	
	N56	Q355D	□2000×320×32	8	160.8	1286.4	
横梁接头	N61	Q355D	□1960×606×14	6	130.8	784.8	
	N61a	Q355D	□1960×602×14	4	129.7	518.8	
	N62	Q355D	t=24mm,A=0.47m2	6	89.3	535.8	
	N62a	Q355D	t=24mm,A=0.48m2	4	90.4	361.6	
	N63	Q355D	□1800×606×14	6	119.8	718.8	
	N63a	Q355D	□1800×618×14	4	122	488	
小计						144894.4	
焊缝重1.5%						2173.0	
合计						147067.4	

节段08材料数量汇总表

规格（mm）	材质	单个合计	全桥共1个
t=48	Q420D	11032.8	11032.8
t=44		34719.6	34719.6
t=40		14621.1	14621.1
t=32		18114.3	18114.3
合计		78487.8	78487.8
t=40	Q355D	17866.7	17866.7
t=36		14921.1	14921.1
t=32		19322.4	19322.4
t=24		6338.9	6338.9
t=16		4870.1	4870.1
t=14		3077.4	3077.4
t=4		10	10.0
合计		66406.6	66406.6
焊缝重（1.5%）		2173.0	2173.0
内表面涂装（㎡）		428.6	428.6
外表面涂装（㎡）		643.1	643.1

节段7~节段8拼接汇总表

规格（mm）	材质	单个合计	全桥共1个
t=48	Q420D	1088.9	1088.9
t=44		1129.4	1129.4
t=40		3887.2	3887.2
t=36		3540.9	3540.9
t=32		906.8	906.8
t=28		1771.6	1771.6
t=24		1556.4	1556.4
t=4		22.6	22.6
合计		13903.8	13903.8
M30x200	10.9S高强螺栓	4097.3	4097.3
外表面涂装（㎡）		51.7	51.7

中交第二公路勘察设计研究院有限公司	狮子洋通道工程勘察设计 施 工 图 设 计	K6+418.3 新沙高架桥 中桥节段08设计图	设计	余汪千	复核	袁勤	一审	张华	二审	李忠	图号	SZYS/04/02/02/01/ 16

4230008187817833

大样A（节段8~节段9）

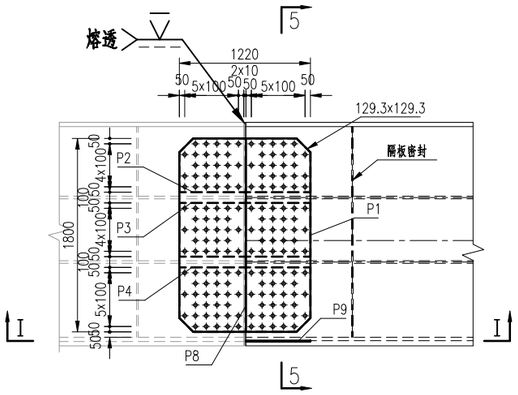

5-5

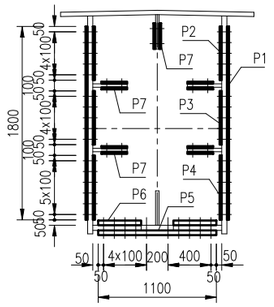

Ⅰ－Ⅰ

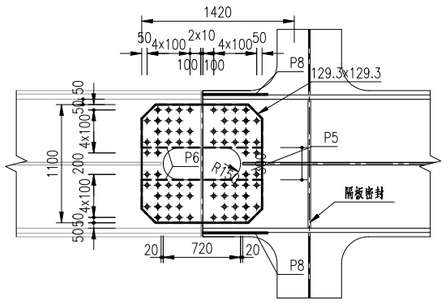

上弦杆顶板、腹板加劲肋拼接

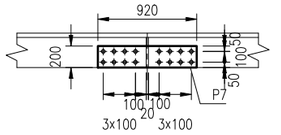

大样C（节段8~节段9）

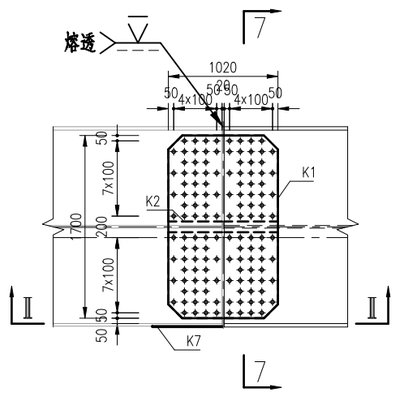

7-7

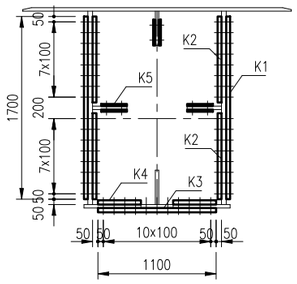

下弦杆顶板、腹板加劲肋拼接

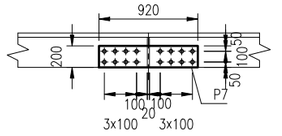

Ⅳ－Ⅳ

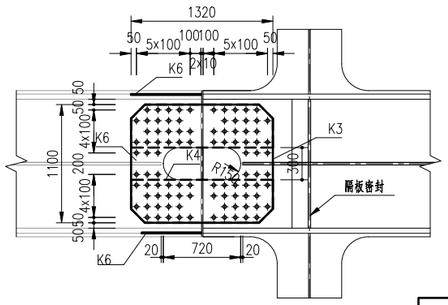

注：

1、本图尺寸均以mm计。

2、未注明的板件裁切边距M30螺栓不小50mm，M24螺栓不小40mm。

3、图中未注明的过焊孔圆弧切角半径为35mm。

4、图中未注明焊缝详见《钢梁焊缝及细节设计图》。

符号：

⊕ —— M30螺栓，开孔直径33mm

⊗ —— M24螺栓，开孔直径26mm

节段8~节段9拼接数量表

名称	编号	材质	规格	数量	单件重	共重（kg）	备注
上弦杆拼接	P1	Q355D	□1220×1800×28	2	483.6	967.2	
	P2		□1220×500×28	2	134.1	268.2	
	P3		□1220×500×28	2	134.1	268.2	
	P4		□1220×600×28	2	160.5	321	
	P5		□1420×1100×32	1	391.9	391.9	
	P6		□1420×400×32	2	143.2	286.4	
	P7		□920×200×20	10	28.3	283	
	P8		□600×1800×16	2	135.6	271.2	填板
	P9		□700×1100×16	1	96.7	96.7	填板
	M30高强螺栓	10.9S	M30×200	508	1.94	985.5	
下弦杆拼接	K1	Q355D	□1020×1700×24	2	325.9	651.8	
	K2		□1020×800×24	4	154.5	618	
	K3		□1320×1100×36	1	409.8	409.8	
	K4		□1320×400×36	2	149.8	299.6	
	K5		□920×200×20	6	28.3	169.8	
	K6		□500×1700×8	2	53.4	106.8	填板
	K7		□650×1100×4	1	22.6	22.6	填板
	M30高强螺栓	10.9S	M30×200	324	1.94	628.6	
腹杆拼接	L1	Q355D	□1520×1100×24	2	314.6	629.2	
	L2		□1520×500×24	4	143.2	572.8	
	L3		□1320×1100×28	1	318.7	318.7	
	L4		□1320×500×28	2	145.1	290.2	
	L5		□1520×1100×44	1	576.8	576.8	
	L6		□1520×240×44	2	124.3	248.6	
	L7		□1220×240×24	4	54.6	218.4	
	L8		□1320×240×24	2	60.3	120.6	
	M30高强螺栓	10.9S	M30×200	540	1.94	1047.6	

大样B（节段8~节段9）

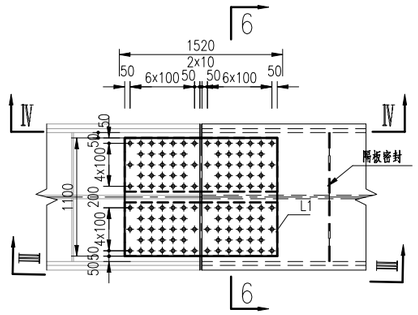

6-6

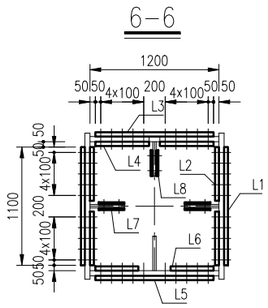

腹杆腹板加劲肋拼接

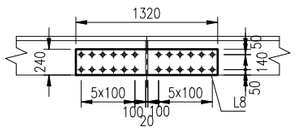

腹杆顶加劲肋拼接

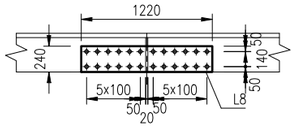

Ⅲ－Ⅲ

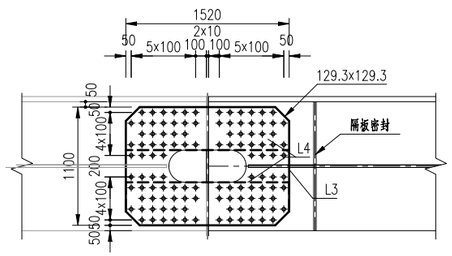

Ⅳ－Ⅳ

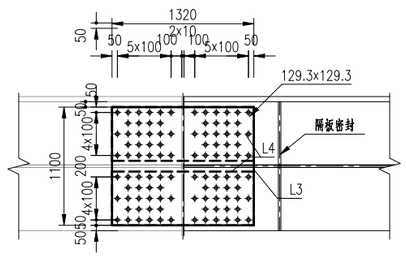

中交第二公路勘察设计研究院有限公司	狮子洋通道工程勘察设计 施 工 图 设 计	K6+418.3 新沙高架桥 中桥节段09设计图	设计	余汪千	复核	袁勤	一审	沈华	二审	李忠	图号	SZYS/04/02/02/01/ 17

节段09材料数量表

名称	编号	材质	规格	数量	单件重	共重（kg）	备注
上弦顶板	N11a	Q355D	t=20mm,A=15.28m2	1	2399.7	2399.7	
	N11b	Q355D	t=24mm,A=13.73m2	1	2586.7	2586.7	
上弦底板	N12a	Q355D	□7900×1200×20	1	1488.4	1488.4	
	N12b	Q355D	□7100×1200×24	1	1605.2	1605.2	
上弦节点板	N13	Q355D	t=40mm,A=24.54m2	2	7705.6	15411.2	
上弦腹板	N14	Q355D	□7300×2048×32	2	3755.4	7510.8	
上弦横隔板	N15	Q355D	□1980×1200×16	3	298.9	896.7	
	N15a	Q355D	□1976×1200×16	2	297.7	595.4	
	N15 ‘	Q355D	□2057×200×16	3	51.5	154.5	
	N15b	Q355B	□2057×40×4	4	2.5	10	
	N15c	Q355D	□800×400×16	4	40.2	160.8	
上弦加劲肋	N16a	Q355D	□7900×280×24	6	416.4	2498.4	
	N16b	Q355D	□7100×320×32	6	570.2	3421.2	
下弦顶板	N21a	Q355D	□7901×2500×24	1	3720.9	3720.9	
	N21b	Q355D	□7101×2500×24	1	3344.1	3344.1	
下弦底板	N22a	Q355D	t=24mm,A=12.96m2	1	2441.3	2441.3	
	N22b	Q355D	t=24mm,A=11.13m2	1	2097.4	2097.4	
下弦节点板	N23	Q355D	t=48mm,A=22.53m2	2	8490.1	16980.2	Z35钢
下弦腹板	N24	Q355D	□7301×1880×32	2	3449	6898	
下弦横隔板	N25	Q355D	□1800×1200×16	3	271.3	813.9	
	N25a	Q355D	□1800×1200×16	2	271.3	542.6	
	N25’	Q355D	□2057×200×16	3	51.5	154.5	
下弦加劲肋	N26a	Q355D	□7901×320×32	4	635.5	2542	
	N26b	Q355D	□7101×280×24	4	374.9	1499.6	
	N26c	Q355D	□15002×170×14	2	280.2	560.4	
斜腹杆	N31	Q355D	□11903×1200×36	1	4035.5	4035.5	
	N31a	Q355D	□11803×1200×36	1	4001.6	4001.6	
	N32	Q355D	□7903×1360×36	2	3038	6076	
	N33	Q355D	□7903×320×32	2	635.5	1271	
	N33a	Q355D	□10503×320×32	1	844	844	
	N33b	Q355D	□10403×320×32	1	836.5	836.5	
	N34	Q355D	□1200×1200×16	3	180.9	542.7	
	N41	Q355D	□5651×1200×36	1	1916	1916	
	N41a	Q355D	□5951×1200×36	1	2017.8	2017.8	
	N42	Q355D	□3851×1360×36	2	1480.8	2961.6	
	N43	Q355D	□3851×320×32	2	309	618	
	N43a	Q355D	□4951×320×32	1	396.9	396.9	
	N43b	Q355D	□5251×320×32	1	422	422	
	N44	Q355D	□1200×1200×16	3	180.9	542.7	
节点板加劲	N51	Q355D	□6111×1200×36	1	2071.5	2071.5	
	N51a	Q355D	□5711×1200×36	1	1935.8	1935.8	
	N52	Q355D	□3911×1360×36	2	1503.4	3006.8	
	N53	Q355D	□3911×320×32	2	314	628	
	N53a	Q355D	□5411×320×32	1	434.6	434.6	
	N53b	Q355D	□5011×320×32	1	401.9	401.9	
	N54	Q355D	□1200×1200×16	2	180.9	361.8	
	N55	Q355D	□2300×320×32	4	185.9	743.6	
	N56	Q355D	□2200×320×32	4	175.8	703.2	
横梁接头	N61	Q355D	□1980×610×14	6	133	798	
	N61a	Q355D	□1976×618×14	4	134.1	536.4	
	N62	Q355D	t=24mm,A=0.47m2	6	89.3	535.8	
	N62a	Q355D	t=24mm,A=0.48m2	4	90.4	361.6	
	N63	Q355D	□1800×602×14	6	118.7	712.2	
	N63a	Q355D	□1800×618×14	4	122	488	
小计						120535.4	
焊缝重1.5%						1808.0	
合计						122343.4	

节段09材料数量汇总表

规格（mm）	材质	单个合计	全桥共1个
t=48	Q355D	16980.2	16980.2
t=40		15411.2	15411.2
t=36		28022.6	28022.6
t=32		27671.7	27671.7
t=24		20691	20691
t=20		3888.1	3888.1
t=16		4765.6	4765.6
t=14		3095	3095
t=4		10	10
焊缝重（1.5%）		1808.0	1808.0
合计		122343.4	122343.4
内表面涂装（㎡）		399.8	399.8
外表面涂装（㎡）		609.1	609.1

节段8~节段9拼接数量汇总表

规格（mm）	材质	单个合计	全桥共1个
t=44	Q355D	825.4	825.4
t=36		709.4	709.4
t=32		678.3	678.3
t=28		2433.5	2433.5
t=24		2810.8	2810.8
t=20		452.8	452.8
t=16		367.9	367.9
t=8		106.8	106.8
t=4		22.6	22.6
合计		8407.5	8407.5
M30x200	10.9S高强螺栓	2661.7	2661.7
外表面涂装（㎡）		41.8	41.8

中交第二公路勘察设计研究院有限公司	狮子洋通道工程勘察设计 施 工 图 设 计	K6+418.3 新沙高架桥 中桥节段09设计图	设计	余汪千	复核	袁勤	一审	沈华	二审	李忠	图号	SZYS/04/02/02/01/ 17

大样A(节段9~节段10)

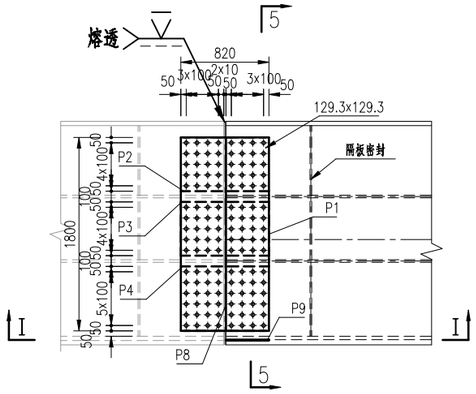

5-5

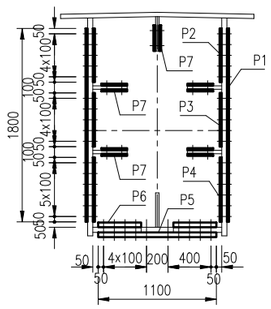

大样C(节段9~节段10)

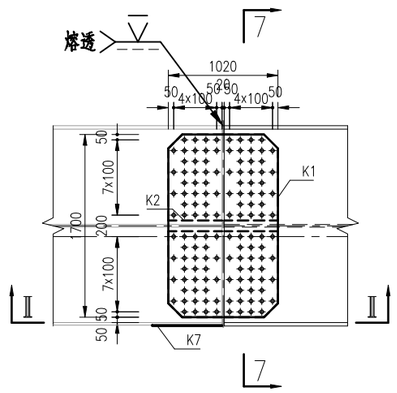

7-7

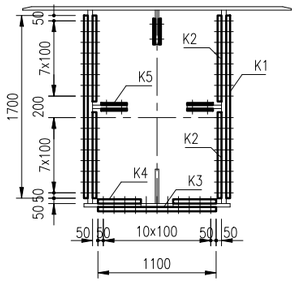

注：

1、本图尺寸均以mm计。

2、未注明的板件裁切边距M30螺栓不小50mm，M24螺栓不小40mm。

3、图中未注明的过焊孔圆弧切角半径为35mm。

4、图中未注明焊缝详见《钢梁焊缝及细节设计图》。

符号：

—— M30螺栓，开孔直径33mm

—— M24螺栓，开孔直径26mm

Ⅰ－Ⅰ

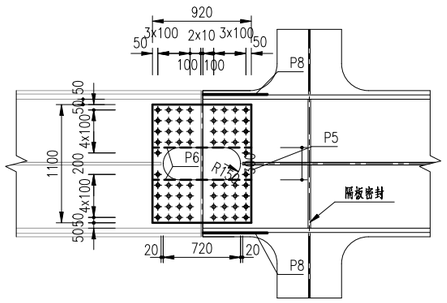

上弦杆顶板、腹板加劲肋拼接

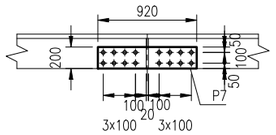

Ⅳ－Ⅳ

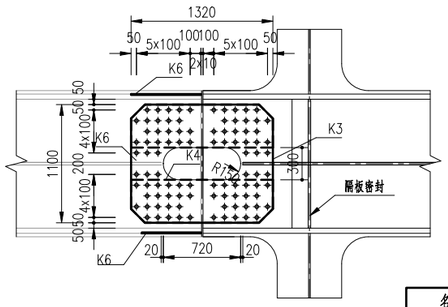

下弦杆顶板、腹板加劲肋拼接

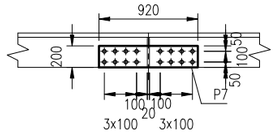

大样B(节段9~节段10)

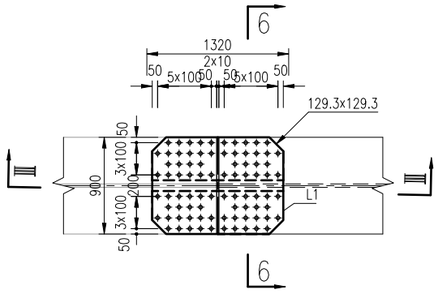

6-6

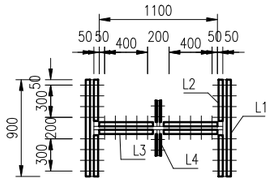

腹杆腹板加劲肋拼接

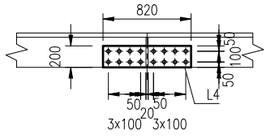

Ⅱ－Ⅱ

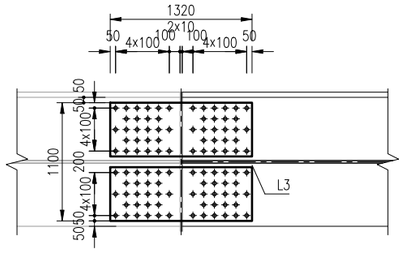

节段9~节段10拼接数量表

名称	编号	材质	规格	数量	单件重	共重(kg)	备注
上弦杆拼接	P1	Q355D	□820×1800×24	2	278.8	557.6	
	P2		□820×500×24	2	77.2	154.4	
	P3		□820×500×24	2	77.2	154.4	
	P4		□820×600×24	2	92.3	184.6	
	P5		□920×1100×28	1	222	222	
	P6		□920×400×28	2	81.3	162.6	
	P7		□920×200×14	10	19.8	198	
	P8		□600×1800×12	2	101.7	203.4	填板
	P9		□700×1100×4	0	24.2	0	填板
	M30高强螺栓	10.9S	M30×200	424	1.94	822.6	
下弦杆拼接	K1	Q355D	□1020×1700×24	2	325.9	651.8	
	K2		□1020×800×24	4	154.5	618	
	K3		□1320×1100×36	1	409.8	409.8	
	K4		□1320×400×36	2	149.8	299.6	
	K5		□920×200×20	6	28.3	169.8	
	K6		□500×1700×12	2	80.1	160.2	填板
	K7		□650×1100×4	0	22.6	0	填板
	M30高强螺栓	10.9S	M30×200	324	1.94	628.6	
腹杆拼接	L1	Q355D	□1520×1100×24	2	314.6	629.2	
	L2		□1520×500×24	4	143.2	572.8	
	L3		□1320×1100×28	1	318.7	318.7	
	L4		□1320×500×28	2	145.1	290.2	
	L5		□1520×1100×44	1	576.8	576.8	
	L6		□1520×240×44	2	124.3	248.6	
	L7		□1220×240×24	4	54.6	218.4	
	L8		□1320×240×24	2	60.3	120.6	
	M30高强螺栓	10.9S	M30×200	540	1.94	1047.6	

中交第二公路勘察设计研究院有限公司	狮子洋通道工程勘察设计 施 工 图 设 计	K6+418.3 新沙高架桥 中桥节段10设计图	设计	余汪千	复核	袁勤	一审	张华	二审	李忠	图号	SZYS/04/02/02/01/ 18

节段10材料数量表

名称	编号	材质	规格	数量	单件重	共重（kg）	备注
上弦顶板	N11a	Q355D	t=20mm,A=15.28m2	1	2399.7	2399.7	
	N11b	Q355D	t=20mm,A=13.73m2	1	2155.5	2155.5	
上弦底板	N12a	Q355D	□7900×1200×20	1	1488.4	1488.4	
	N12b	Q355D	□7100×1200×20	1	1337.6	1337.6	
上弦节点板	N13	Q355D	t=40mm,A=23.47m2	2	7369.6	14739.2	
上弦腹板	N14	Q355D	□7300×2048×28	2	3286	6572	
上弦横隔板	N15	Q355D	□1980×1200×16	3	298.9	896.7	
	N15a	Q355D	□1980×1200×16	2	298.9	597.8	
	N15‘	Q355D	□2057×200×16	3	51.5	154.5	
	N15b	Q355B	□2057×40×4	4	2.5	10	
	N15c	Q355D	□800×400×16	4	40.2	160.8	
上弦加劲肋	N16a	Q355D	□7900×280×24	6	416.4	2498.4	
	N16b	Q355D	□7100×280×24	6	374.9	2249.4	
下弦顶板	N21a	Q355D	□7901×2500×24	1	3720.9	3720.9	
	N21b	Q355D	□7101×2500×24	1	3344.1	3344.1	
下弦底板	N22a	Q355D	t=24mm,A=12.96m2	1	2441.3	2441.3	
	N22b	Q355D	t=24mm,A=11.13m2	1	2097.4	2097.4	
下弦节点板	N23	Q355D	t=44mm,A=22.52m2	2	7778.4	15556.8	Z35钢
下弦腹板	N24	Q355D	□7301×1880×32	2	3449	6898	
下弦横隔板	N25	Q355D	□1800×1200×16	3	271.3	813.9	
	N25a	Q355D	□1800×1200×16	2	271.3	542.6	
	N25’	Q355D	□2057×200×16	5	51.5	257.5	
下弦加劲肋	N26a	Q355D	□7901×280×24	4	416.4	1665.6	
	N26b	Q355D	□7101×280×24	4	374.9	1499.6	
	N26c	Q355D	□15002×170×14	2	280.2	560.4	
斜腹杆	N31	Q355D	□11770×1200×36	1	3990.3	3990.3	
	N31a	Q355D	□11670×1200×36	1	3956.4	3956.4	
	N32	Q355D	□7770×1360×36	2	2987.1	5974.2	
	N33	Q355D	□7770×320×32	2	625.5	1251	
	N33a	Q355D	□10370×320×32	1	834	834	
	N33b	Q355D	□10270×320×32	1	826.4	826.4	
	N34	Q355D	□1200×1200×16	3	180.9	542.7	
	N41	Q355D	□3798×900×36	2	966.5	1933	
	N42	Q355D	□6098×1200×32	1	1838.8	1838.8	
	N43	Q355D	□5398×240×24	2	244.9	489.8	
节点板加劲	N51	Q355D	□6051×1200×36	1	2051.7	2051.7	
	N51a	Q355D	□4651×1200×36	1	1576.9	1576.9	
	N52	Q355D	□3851×1360×36	2	1480.8	2961.6	
	N53	Q355D	□3851×320×32	2	309	618	
	N53a	Q355D	□4651×320×32	1	374.3	374.3	
	N53b	Q355D	□3251×320×32	1	261.2	261.2	
	N54	Q355D	□1200×1200×16	2	180.9	361.8	
	N55	Q355D	□2300×320×32	2	185.9	371.8	
	N56	Q355D	□2200×320×32	4	175.8	703.2	
横梁接头	N61	Q355D	□1980×610×14	6	133	798	
	N61a	Q355D	□1980×622×14	4	135.2	540.8	
	N62	Q355D	t=24mm,A=0.47m2	6	89.3	535.8	
	N62a	Q355D	t=24mm,A=0.48m2	4	90.4	361.6	
	N63	Q355D	□1800×606×14	6	119.8	718.8	
	N63a	Q355D	□1800×618×14	4	122	488	
小计						109018.2	
焊缝重1.5%						1635.0	
合计						110653.2	

节段10材料数量汇总表

规格（mm）	材质	单个合计	全桥共1个
t=44	Q355D	15556.8	15556.8
t=40		14739.2	14739.2
t=36		22444.1	22444.1
t=32		13976.7	13976.7
t=28		6572	6572
t=24		20903.9	20903.9
t=20		7381.2	7381.2
t=16		4328.3	4328.3
t=14		3106	3106
t=4		10	10
焊缝重（1.5%）		1635.3	1635.3
合计	Q355D	110653.5	110653.5
内表面涂装（m²）		368.1	368.1
外表面涂装（m²）		587.8	587.8

节段9~节段10拼接数量汇总表

规格（mm）	材质	单个合计	全桥共1个
t=44	Q355D	825.4	825.4
t=36		709.4	709.4
t=28		993.5	993.5
t=24		3861.8	3861.8
t=20		169.8	169.8
t=14		198	198
t=12		363.6	363.6
合计		7121.5	7121.5
M30x200	10.9S高强螺栓	2498.8	2498.8
外表面涂装（m²）		36.7	36.7

中交第二公路勘察设计研究院有限公司	狮子洋通道工程勘察设计 施 工 图 设 计	K6+418.3 新沙高架桥 中桥节段10设计图	设计	余汪千	复核	袁勤	一审	沈华	二审	王忠	图号	SZYS/04/02/02/01/ 18

4225500607075718

大样A（节段10~节段11）

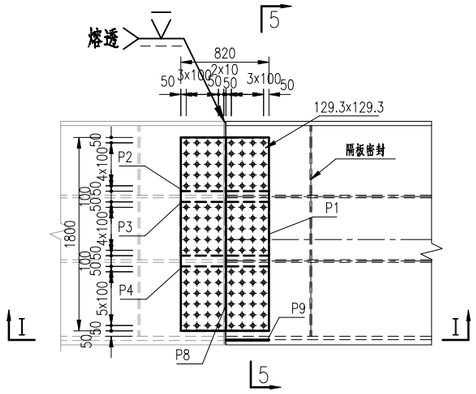

5-5

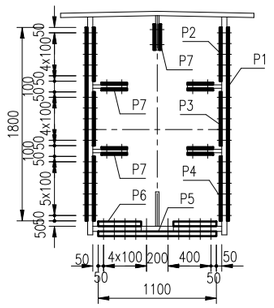

I－I

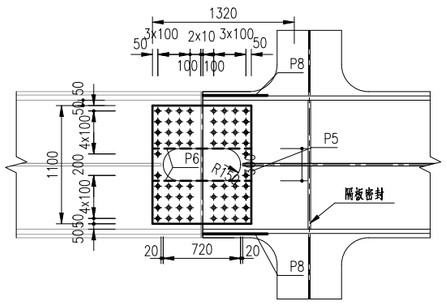

上弦杆顶板、腹板加劲肋拼接

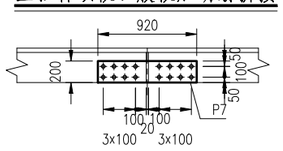

大样C（节段10~节段11）

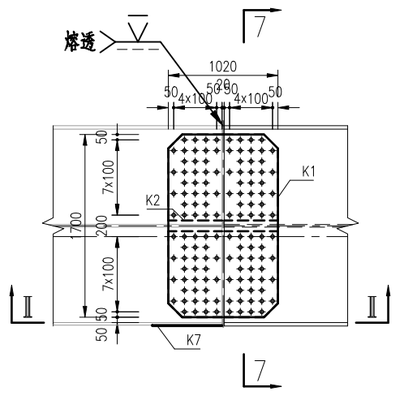

7-7

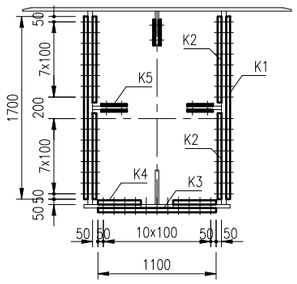

Ⅳ－Ⅳ

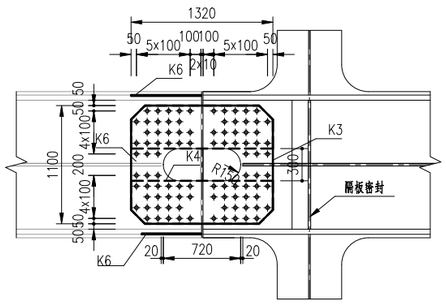

下弦杆顶板、腹板加劲肋拼接

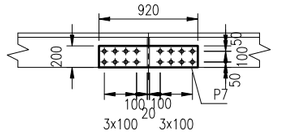

大样B（节段10~节段11）

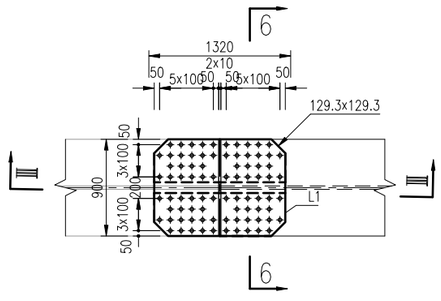

6-6

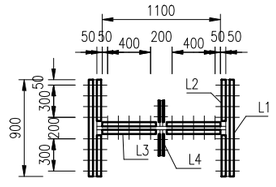

腹杆腹板加劲肋拼接

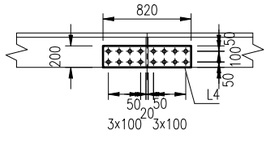

Ⅲ－Ⅲ

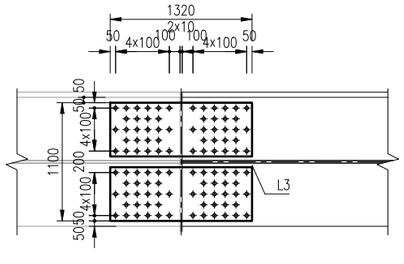

注：

1、本图尺寸均以mm计。

2、未注明的板件裁切边距M30螺栓不小50mm，M24螺栓不小40mm。

3、图中未注明的过焊孔圆弧切角半径为35mm。

4、图中未注明焊缝详见《钢梁焊缝及细节设计图》。

符号：

⊕ —— M30螺栓，开孔直径33mm

⊗ —— M24螺栓，开孔直径26mm

节段10~节段11拼接数量表

名称	编号	材质	规格	数量	单件重	共重（kg）	备注
上弦杆拼接	P1	Q355D	□820×1800×24	2	278.8	557.6	
	P2		□820×500×24	2	77.2	154.4	
	P3		□820×500×24	2	77.2	154.4	
	P4		□820×600×24	2	92.3	184.6	
	P5		□920×1100×28	1	222	222	
	P6		□920×400×28	2	81.3	162.6	
	P7		□920×200×14	10	19.8	198	
	P8		□600×1800×12	2	101.7	203.4	填板
	P9		□700×1100×4	0	24.2	0	填板
	M30高强螺栓	10.9S	M30x200	424	1.94	822.6	
下弦杆拼接	K1	Q355D	□1020×1700×24	2	325.9	651.8	
	K2		□1020×800×24	4	154.5	618	
	K3		□1320×1100×36	1	409.8	409.8	
	K4		□1320×400×36	2	149.8	299.6	
	K5		□920×200×20	6	28.3	169.8	
	K6		□500×1700×12	2	80.1	160.2	填板
	K7		□650×1100×4	0	22.6	0	填板
	M30高强螺栓	10.9S	M30x200	324	1.94	628.6	
腹杆拼接	L1	Q355D	□1320×900×28	2	261.6	523.2	
	L2		□1320×400×28	4	116.5	466	
	L3		□1320×500×28	4	145.1	580.4	
	L4		□820×200×20	4	25.1	100.4	
	M30高强螺栓	10.9S	M30x200	320	1.94	620.8	

中交第二公路勘察设计研究院有限公司	狮子洋通道工程勘察设计 施 工 图 设 计	K6+418.3 新沙高架桥 中桁节段11设计图	设计	余汪千	复核	袁勤	一审	沈华	二审	李忠	图号	SZYS/04/02/02/01/ 19

节段11材料数量表

名称	编号	材质	规格	数量	单件重	共重（kg）	备注
上弦顶板	N11a	Q355D	t=20mm,A=15.28m2	1	2399.7	2399.7	
	N11b	Q355D	t=20mm,A=13.73m2	1	2155.5	2155.5	
上弦底板	N12a	Q355D	□7900×1200×20	1	1488.4	1488.4	
	N12b	Q355D	□7100×1200×20	1	1337.6	1337.6	
上弦节点板	N13	Q355D	t=40mm,A=22.62m2	2	7102.7	14205.4	
上弦腹板	N14	Q355D	□7300×2048×28	2	3286	6572	
上弦横隔板	N15	Q355D	□1980×1200×16	3	298.9	896.7	
	N15a	Q355D	□1980×1200×16	2	298.9	597.8	
	N15 ‘	Q355D	□2057×200×16	3	51.5	154.5	
	N15b	Q355B	□2057×40×4	4	2.5	10	
	N15c	Q355D	□800×400×16	4	40.2	160.8	
上弦加劲肋	N16a	Q355D	□7900×280×24	6	416.4	2498.4	
	N16b	Q355D	□7100×280×24	6	374.9	2249.4	
下弦顶板	N21a	Q355D	□7901×2500×24	1	3720.9	3720.9	
	N21b	Q355D	□7101×2500×24	1	3344.1	3344.1	
下弦底板	N22a	Q355D	t=24mm,A=12.96m2	1	2441.3	2441.3	
	N22b	Q355D	t=24mm,A=11.13m2	1	2097.4	2097.4	
下弦节点板	N23	Q355D	t=44mm,A=20.79m2	2	7180.9	14361.8	Z35钢
下弦腹板	N24	Q355D	□7301×1880×32	2	3449	6898	
下弦横隔板	N25	Q355D	□1800×1200×16	3	271.3	813.9	
	N25a	Q355D	□1800×1200×16	2	271.3	542.6	
	N25’	Q355D	□2057×200×16	3	51.5	154.5	
下弦加劲肋	N26a	Q355D	□7901×280×24	4	416.4	1665.6	
	N26b	Q355D	□7101×280×24	4	374.9	1499.6	
	N26c	Q355D	□15002×170×14	2	280.2	560.4	
斜腹杆	N31	Q355D	□7651×900×36	2	1947.1	3894.2	
	N32	Q355D	□12151×1200×32	1	3662.5	3662.5	
	N33	Q355D	□10751×240×24	2	486.1	972.2	
	N41	Q355D	□3752×900×36	2	955.2	1910.4	
	N42	Q355D	□6052×1200×32	1	1823.7	1823.7	
	N43	Q355D	□5352×240×24	2	241.2	482.4	
	N51	Q355D	□3789×900×36	2	963.7	1927.4	
	N52	Q355D	□5989×1200×32	1	1806.1	1806.1	
	N53	Q355D	□5289×240×24	2	239.3	478.6	
节点板加劲	N54	Q355D	□1123×1200×20	1	212	212	
	N55	Q355D	□1032×1200×20	2	194.7	389.4	
横梁接头	N61	Q355D	□1980×610×14	6	133	798	
	N61a	Q355D	□1980×622×14	4	135.2	540.8	
	N62	Q355D	t=24mm,A=0.47m2	6	89.3	535.8	
	N62a	Q355D	t=24mm,A=0.48m2	4	90.4	361.6	
	N63	Q355D	□1800×606×14	6	119.8	718.8	
	N63a	Q355D	□1800×618×14	4	122	488	
小计						93828.2	
焊缝重1.5%						1407.0	
合计						95235.2	

节段11材料数量汇总表

规格（mm）	材质	单个合计	全桥共1个
t=44	Q355D	14361.8	14361.8
t=40		14205.4	14205.4
t=36		7732	7732
t=32		14190.3	14190.3
t=28		6572	6572
t=24		22347.3	22347.3
t=20		7982.6	7982.6
t=16		3320.8	3320.8
t=14		3106	3106
t=4		10	10
焊缝重（1.5%）		1407.4	1407.4
合计		95235.6	95235.6
内表面涂装（m²）		252.8	252.8
外表面涂装（m²）		597.3	597.3

节段10~节段11拼接数量汇总表

规格（mm）	材质	单个合计	全桥共1个
t=36	Q355D	709.4	709.4
t=28		1954.2	1954.2
t=24		2320.8	2320.8
t=20		270.2	270.2
t=14		198	198
t=12		363.6	363.6
合计		5816.2	5816.2
M30x200	10.9S高强螺栓	2072.0	2072.0
外表面涂装（m²）		31.1	31.1

中交第二公路勘察设计研究院有限公司	狮子洋通道工程勘察设计 施 工 图 设 计	K6+418.3 新沙高架桥 中桁节段11设计图	设计	余汪千	复核	袁勤	一审	沈华	二审	李忠	图号	SZYS/04/02/02/01/ 19

大样A（节段11~节段12）

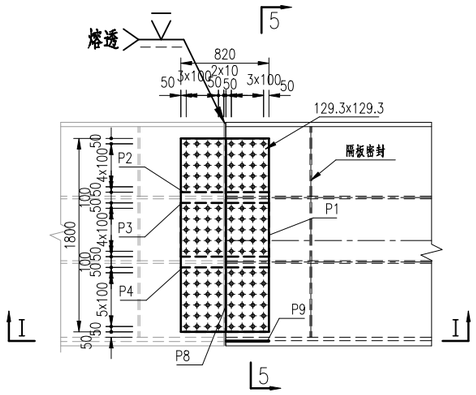

5-5

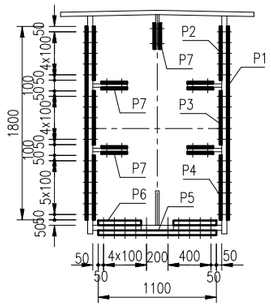

Ⅰ－Ⅰ

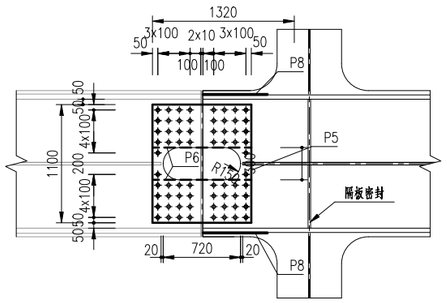

上弦杆顶板、腹板加劲肋拼接

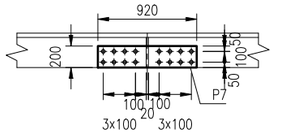

大样C（节段11~节段12）

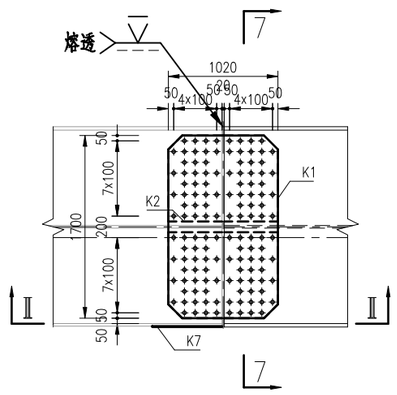

7-7

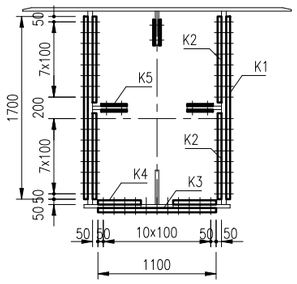

下弦杆顶板、腹板加劲肋拼接

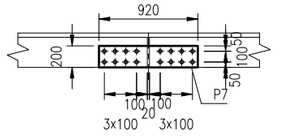

Ⅳ－Ⅳ

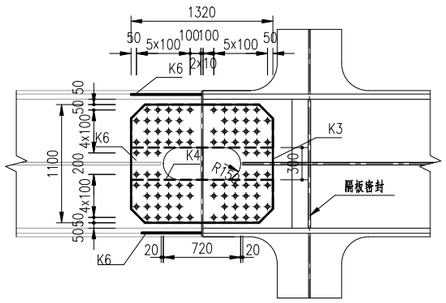

注：

1、本图尺寸均以mm计。

2、未注明的板件裁切边距M30螺栓不小50mm，M24螺栓不小40mm。

3、图中未注明的过焊孔圆弧切角半径为35mm。

4、图中未注明焊缝详见《钢梁焊缝及细节设计图》。

符号：

⊕ —— M30螺栓，开孔直径33mm

⊗ —— M24螺栓，开孔直径26mm

大样B（节段11~节段12）

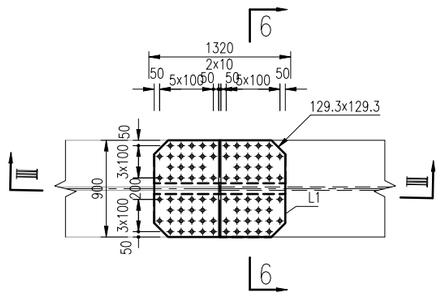

6-6

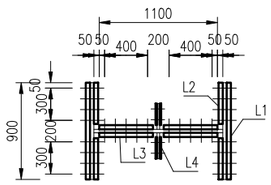

腹杆腹板加劲肋拼接

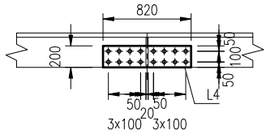

Ⅱ－Ⅱ

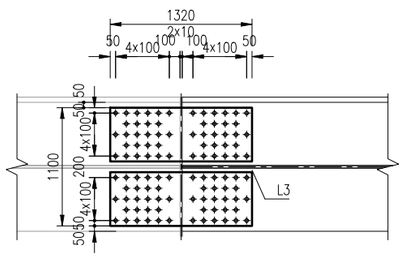

节段11~节段12拼接数量表

名称	编号	材质	规格	数量	单件重	共重（kg）	备注
上弦杆拼接	P1	Q355D	□820×1800×24	2	278.8	557.6	
	P2		□820×500×24	2	77.2	154.4	
	P3		□820×500×24	2	77.2	154.4	
	P4		□820×600×24	2	92.3	184.6	
	P5		□920×1100×28	1	222	222	
	P6		□920×400×28	2	81.3	162.6	
	P7		□920×200×14	10	19.8	198	
	P8		□600×1800×12	2	101.7	203.4	填板
	P9		□700×1100×4	0	24.2	0	填板
	M30高强螺栓	10.9S	M30x200	424	1.94	822.6	
下弦杆拼接	K1	Q355D	□1020×1700×24	2	325.9	651.8	
	K2		□1020×800×24	4	154.5	618	
	K3		□1320×1100×36	1	409.8	409.8	
	K4		□1320×400×36	2	149.8	299.6	
	K5		□920×200×20	6	28.3	169.8	
	K6		□500×1700×12	2	80.1	160.2	填板
	K7		□650×1100×4	0	22.6	0	填板
	M30高强螺栓	10.9S	M30x200	324	1.94	628.6	
腹杆拼接	L1	Q355D	□1320×900×28	2	261.6	523.2	
	L2		□1320×400×28	4	116.5	466	
	L3		□1320×500×28	4	145.1	580.4	
	L4		□820×200×20	4	25.1	100.4	
	M30高强螺栓	10.9S	M30x200	320	1.94	620.8	

中交第二公路勘察设计研究院有限公司	狮子洋通道工程勘察设计 施 工 图 设 计	K6+418.3 新沙高架桥 中桥节段12设计图	设计	余汪千	复核	袁勤	一审	沈华	二审	李忠	图号	SZYS/04/02/02/01/ 20

节段12材料数量表

名称	编号	材质	规格	数量	单件重	共重（kg）	备注
上弦顶板	N11a	Q355D	t=20mm,A=15.28m2	1	2399.7	2399.7	
	N11b	Q355D	t=20mm,A=13.73m2	1	2155.5	2155.5	
上弦底板	N12a	Q355D	□7900×1200×20	1	1488.4	1488.4	
	N12b	Q355D	□7100×1200×20	1	1337.6	1337.6	
上弦节点板	N13	Q355D	t=40mm,A=22.58m2	2	7090.1	14180.2	
上弦腹板	N14	Q355D	□7300×2048×28	2	3286	6572	
上弦横隔板	N15	Q355D	□1980×1200×16	3	298.9	896.7	
	N15a	Q355D	□1980×1200×16	2	298.9	597.8	
	N15 ‘	Q355D	□2057×200×16	3	51.5	154.5	
	N15b	Q355B	□2057×40×4	4	2.5	10	
	N15c	Q355D	□800×400×16	4	40.2	160.8	
上弦加劲肋	N16a	Q355D	□7900×280×24	6	416.4	2498.4	
	N16b	Q355D	□7100×280×24	6	374.9	2249.4	
下弦顶板	N21a	Q355D	□7901×2500×24	1	3720.9	3720.9	
	N21b	Q355D	□7101×2500×24	1	3344.1	3344.1	
下弦底板	N22a	Q355D	t=24mm,A=12.96m2	1	2441.3	2441.3	
	N22b	Q355D	t=24mm,A=11.13m2	1	2097.4	2097.4	
下弦节点板	N23	Q355D	t=44mm,A=20.81m2	2	7187.8	14375.6	Z35钢
下弦腹板	N24	Q355D	□7301×1880×32	2	3449	6898	
下弦横隔板	N25	Q355D	□1800×1200×16	3	271.3	813.9	
	N25a	Q355D	□1800×1200×16	2	271.3	542.6	
	N25’	Q355D	□2057×200×16	3	51.5	154.5	
下弦加劲肋	N26a	Q355D	□7901×280×24	4	416.4	1665.6	
	N26b	Q355D	□7101×280×24	4	374.9	1499.6	
	N26c	Q355D	□15002×170×14	2	280.2	560.4	
斜腹杆	N31	Q355D	□7548×900×36	2	1918.9	3837.8	
	N32	Q355D	□12048×1200×32	1	3632.4	3632.4	
	N33	Q355D	□10648×240×24	2	482.3	964.6	
	N41	Q355D	□3714×900×36	2	943.9	1887.8	
	N42	Q355D	□6014×1200×32	1	1813.7	1813.7	
	N43	Q355D	□5314×240×24	2	241.2	482.4	
	N51	Q355D	□3752×900×36	2	955.2	1910.4	
	N52	Q355D	□5952×1200×32	1	1793.6	1793.6	
	N53	Q355D	□5252×240×24	2	237.4	474.8	
节点板加劲	N54	Q355D	□1100×1200×20	1	207.2	207.2	
	N55	Q355D	□1010×1200×20	1	190	190	
横梁接头	N61	Q355D	□1980×610×14	6	133	798	
	N61a	Q355D	□1980×622×14	4	135.2	540.8	
	N62	Q355D	t=24mm,A=0.47m2	6	89.3	535.8	
	N62a	Q355D	t=24mm,A=0.48m2	4	90.4	361.6	
	N63	Q355D	□1800×606×14	6	119.8	718.8	
	N63a	Q355D	□1800×618×14	4	122	488	
小计						93452.6	
焊缝重1.5%						1402.0	
合计						94854.6	

节段12材料数量汇总表

规格（mm）	材质	单个合计	全桥共1个
t=44	Q355D	14375.6	14375.6
t=40		14180.2	14180.2
t=36		7636	7636
t=32		14137.7	14137.7
t=28		6572	6572
t=24		22335.9	22335.9
t=20		7778.4	7778.4
t=16		3320.8	3320.8
t=14		3106	3106
t=4		10	10
焊缝重（1.5%）		1401.8	1401.8
合计		94854.4	94854.4
内表面涂装（㎡）		252.7	252.7
外表面涂装（㎡）		593.5	593.5

节段11~节段12拼接数量汇总表

规格（mm）	材质	单个合计	全桥共1个
t=36	Q355D	709.4	709.4
t=28		1954.2	1954.2
t=24		2320.8	2320.8
t=20		270.2	270.2
t=14		198	198
t=12		363.6	363.6
合计		5816.2	5816.2
M30x200	10.9S高强螺栓	2072.0	2072.0
外表面涂装（㎡）		31.1	31.1

中交第二公路勘察设计研究院有限公司	狮子洋通道工程勘察设计 施 工 图 设 计	K6+418.3 新沙高架桥 中桥节段12设计图	设计	余汪千	复核	袁勤	一审	沈华	二审	李忠	图号	SZYS/04/02/02/01/ 20

大样A（节段12~节段13）

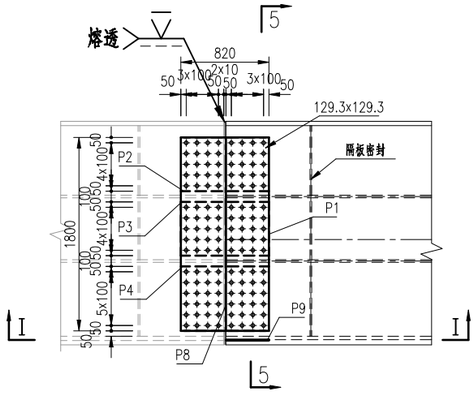

5-5

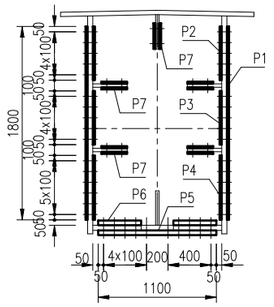

Ⅰ－Ⅰ

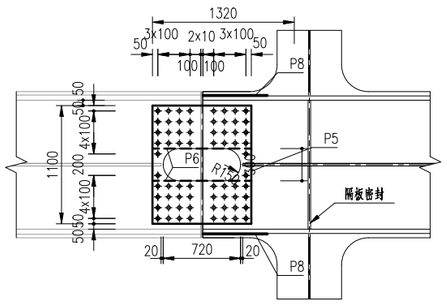

上弦杆顶板、腹板加劲肋拼接

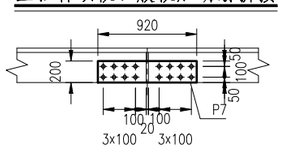

大样C（节段12~节段13）

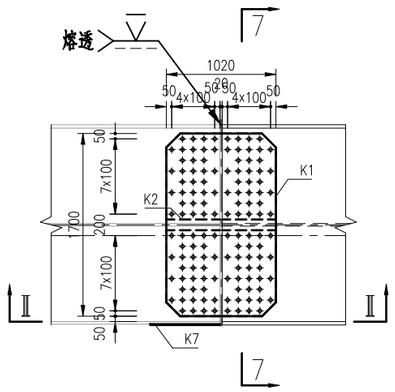

7-7

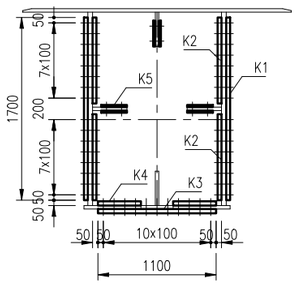

Ⅳ－Ⅳ

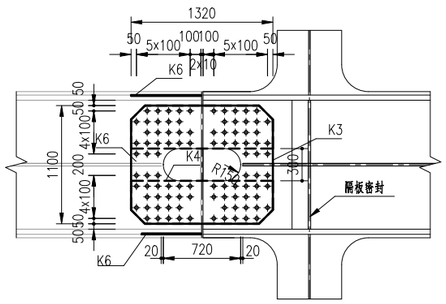

下弦杆顶板、腹板加劲肋拼接

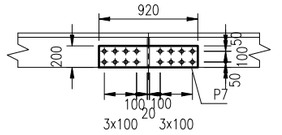

注：

1、本图尺寸均以mm计。

2、未注明的板件裁切边距M30螺栓不小50mm，M24螺栓不小40mm。

3、图中未注明的过焊孔圆弧切角半径为35mm。

4、图中未注明焊缝详见《钢梁焊缝及细节设计图》。

符号：

—— M30螺栓，开孔直径33mm

—— M24螺栓，开孔直径26mm

大样B（节段12~节段13）

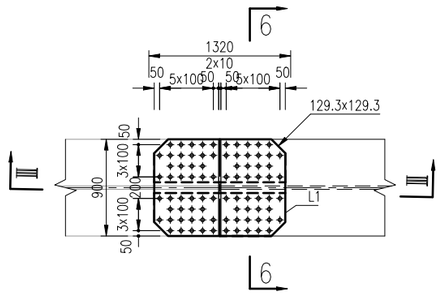

6-6

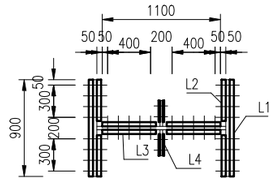

腹杆腹板加劲肋拼接

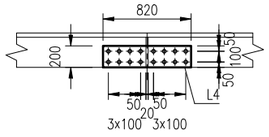

Ⅲ－Ⅲ

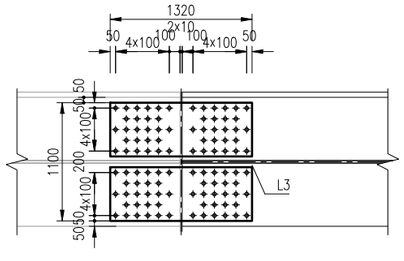

节段12~节段13拼接数量表

名称	编号	材质	规格	数量	单件重	共重（kg）	备注
上弦杆拼接	P1	Q355D	□820×1800×24	2	278.8	557.6	
	P2		□820×500×24	2	77.2	154.4	
	P3		□820×500×24	2	77.2	154.4	
	P4		□820×600×24	2	92.3	184.6	
	P5		□920×1100×28	1	222	222	
	P6		□920×400×28	2	81.3	162.6	
	P7		□920×200×14	10	19.8	198	
	P8		□600×1800×12	2	101.7	203.4	填板
	P9		□700×1100×4	0	24.2	0	填板
	M30高强螺栓	10.9S	M30x200	424	1.94	822.6	
下弦杆拼接	K1	Q355D	□1020×1700×24	2	325.9	651.8	
	K2		□1020×800×24	4	154.5	618	
	K3		□1320×1100×36	1	409.8	409.8	
	K4		□1320×400×36	2	149.8	299.6	
	K5		□920×200×20	6	28.3	169.8	
	K6		□500×1700×12	2	80.1	160.2	填板
	K7		□650×1100×4	0	22.6	0	填板
	M30高强螺栓	10.9S	M30x200	324	1.94	628.6	
腹杆拼接	L1	Q355D	□1320×900×28	2	261.6	523.2	
	L2		□1320×400×28	4	116.5	466	
	L3		□1320×500×28	4	145.1	580.4	
	L4		□820×200×20	4	25.1	100.4	
	M30高强螺栓	10.9S	M30x200	320	1.94	620.8	

中交第二公路勘察设计研究院有限公司	狮子洋通道工程勘察设计 施 工 图 设 计	K6+418.3 新沙高架桥 中桥节段13设计图	设计	余汪千	复核	袁勤	一审	沈华	二审	李忠	图号	SZYS/04/02/02/01/ 21

7250010136425

节段13材料数量表

名称	编号	材质	规格	数量	单件重	共重（kg）	备注
上弦顶板	N11a	Q355D	t=20mm,A=15.28m2	1	2399.7	2399.7	
	N11b	Q355D	t=20mm,A=13.73m2	1	2155.5	2155.5	
上弦底板	N12a	Q355D	□7900×1200×20	1	1488.4	1488.4	
	N12b	Q355D	□7100×1200×20	1	1337.6	1337.6	
上弦节点板	N13	Q355D	t=40mm,A=23.46m2	2	7365.5	14731	
上弦腹板	N14	Q355D	□7300×2048×28	2	3286	6572	
上弦横隔板	N15	Q355D	□1980×1200×16	3	298.9	896.7	
	N15a	Q355D	□1980×1200×16	2	298.9	597.8	
	N15 ‘	Q355D	□2057×200×16	3	51.5	154.5	
	N15b	Q355B	□2057×40×4	4	2.5	10	
	N15c	Q355D	□800×400×16	4	40.2	160.8	
上弦加劲肋	N16a	Q355D	□7900×280×24	6	416.4	2498.4	
	N16b	Q355D	□7100×280×24	6	374.9	2249.4	
下弦顶板	N21a	Q355D	□7901×2500×24	1	3720.9	3720.9	
	N21b	Q355D	□7101×2500×24	1	3344.1	3344.1	
下弦底板	N22a	Q355D	t=24mm,A=12.96m2	1	2441.3	2441.3	
	N22b	Q355D	t=24mm,A=11.13m2	1	2097.4	2097.4	
下弦节点板	N23	Q355D	t=44mm,A=20.36m2	2	7031.7	14063.4	Z35钢
下弦腹板	N24	Q355D	□7301×1880×32	2	3449	6898	
下弦横隔板	N25	Q355D	□1800×1200×16	3	271.3	813.9	
	N25a	Q355D	□1800×1200×16	2	271.3	542.6	
	N25’	Q355D	□2057×200×16	3	51.5	154.5	
下弦加劲肋	N26a	Q355D	□7901×280×24	4	416.4	1665.6	
	N26b	Q355D	□7101×280×24	4	374.9	1499.6	
	N26c	Q355D	□15002×170×14	2	280.2	560.4	
斜腹杆	N31	Q355D	□7458×900×36	2	1896.2	3792.4	
	N32	Q355D	□11958×1200×32	1	3604.7	3604.7	
	N33	Q355D	□10558×240×24	2	476.7	953.4	
	N41	Q355D	□5482×1200×36	1	1859.5	1859.5	
	N41a	Q355D	□5782×1200×36	1	1961.2	1961.2	
	N42	Q355D	□3682×1360×36	2	1415.8	2831.6	
	N43	Q355D	□3682×320×32	2	296.4	592.8	
	N43a	Q355D	□4782×320×32	1	384.3	384.3	
	N43b	Q355D	□5082×320×32	1	409.5	409.5	
	N44	Q355D	□1200×1200×16	3	180.9	542.7	
	N51	Q355D	□3714×900×36	2	943.9	1887.8	
	N52	Q355D	□5914×1200×32	1	1783.5	1783.5	
	N53	Q355D	□4514×240×24	2	203.5	407	
节点板加劲	N54	Q355D	□2300×320×32	2	185.9	371.8	
	N55	Q355D	□980×1200×20	1	185.3	185.3	
横梁接头	N61	Q355D	□1980×610×14	6	133	798	
	N61a	Q355D	□1980×622×14	4	135.2	540.8	
	N62	Q355D	t=24mm,A=0.47m2	6	89.3	535.8	
	N62a	Q355D	t=24mm,A=0.48m2	4	90.4	361.6	
	N63	Q355D	□1800×606×14	6	119.8	718.8	
	N63a	Q355D	□1800×618×14	4	122	488	
小计						98064	
焊缝重1.5%						1471.0	
合计						99535.0	

节段13材料数量汇总表

规格（mm）	材质	单个合计	全桥共1个
t=44	Q355D	14063.4	14063.4
t=40		14731	14731
t=36		12332.5	12332.5
t=32		14044.6	14044.6
t=28		6572	6572
t=24		21774.5	21774.5
t=20		7566.5	7566.5
t=16		3863.5	3863.5
t=14		3106	3106
t=4		10	10
焊缝重（1.5%）		1471.0	1471.0
合计		99535.0	99535.0
内表面涂装（m²）		253.6	253.6
外表面涂装（m²）		626.8	626.8

节段12~节段13拼接数量汇总表

规格（mm）	材质	单个合计	全桥共1个
t=36	Q355D	709.4	709.4
t=28		1954.2	1954.2
t=24		2320.8	2320.8
t=20		270.2	270.2
t=14		198	198
t=12		363.6	363.6
合计		5816.2	5816.2
M30×200	10.9S高强螺栓	2072.0	2072.0
外表面涂装（m²）		31.1	31.1

中交第二公路勘察设计研究院有限公司	狮子洋通道工程勘察设计 施 工 图 设 计	K6+418.3 新沙高架桥 中桥节段13设计图	设计	余汪千	复核	袁勤	一审	沈华	二审	王忠	图号	SZYS/04/02/02/01/ 21

725301010 2077696

大样A（节段13~节段14）

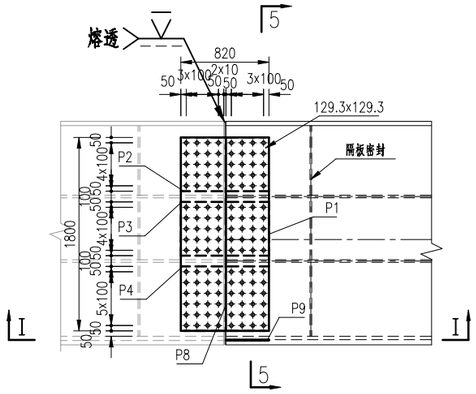

5-5

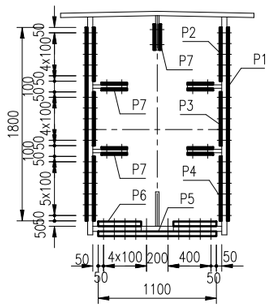

Ⅰ－Ⅰ

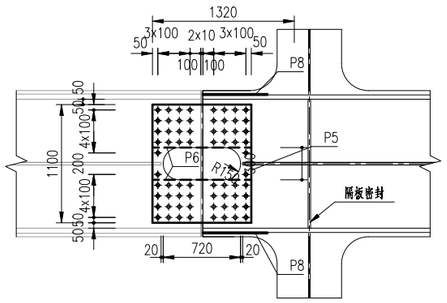

上弦杆顶板、腹板加劲肋拼接

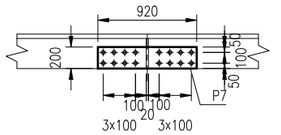

大样C（节段13~节段14）

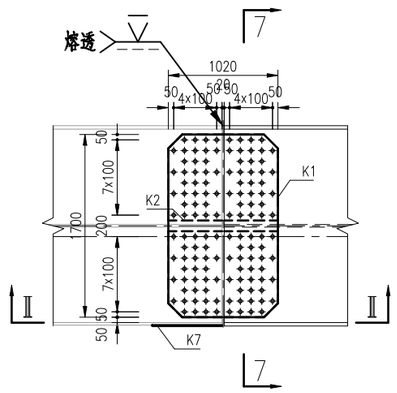

7-7

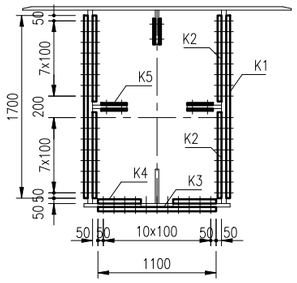

下弦杆顶板、腹板加劲肋拼接

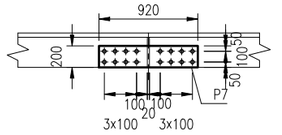

Ⅳ－Ⅳ

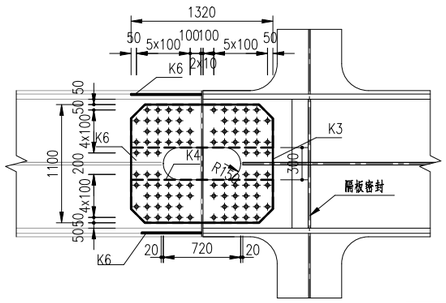

注：

1、本图尺寸均以mm计。

2、未注明的板件裁切边距M30螺栓不小50mm，M24螺栓不小40mm。

3、图中未注明的过焊孔圆弧切角半径为35mm。

4、图中未注明焊缝详见《钢梁焊缝及细节设计图》。

符号：

—— M30螺栓，开孔直径33mm

—— M24螺栓，开孔直径26mm

大样B（节段13~节段14）

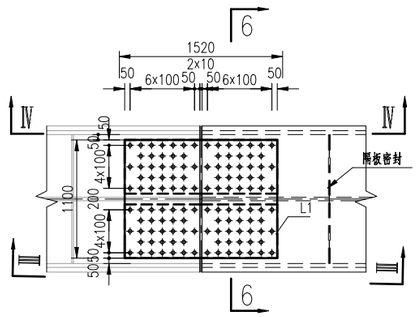

6-6

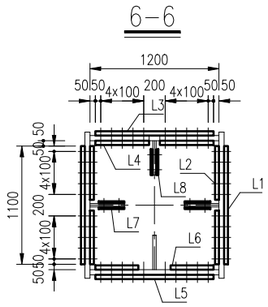

腹杆腹板加劲肋拼接

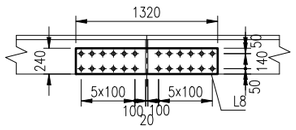

腹杆顶加劲肋拼接

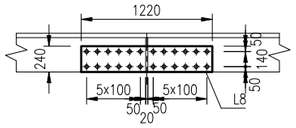

Ⅲ－Ⅲ

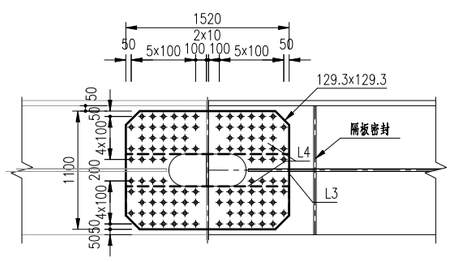

Ⅳ－Ⅳ

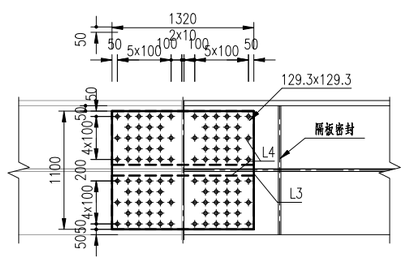

节段13~节段14拼接数量表

名称	编号	材质	规格	数量	单件重	共重（kg）	备注
上弦杆拼接	P1	Q355D	□820×1800×24	2	278.8	557.6	
	P2		□820×500×24	2	77.2	154.4	
	P3		□820×500×24	2	77.2	154.4	
	P4		□820×600×24	2	92.3	184.6	
	P5		□920×1100×28	1	222	222	
	P6		□920×400×28	2	81.3	162.6	
	P7		□920×200×14	10	19.8	198	
	P8		□600×1800×12	2	101.7	203.4	填板
	P9		□700×1100×4	0	24.2	0	填板
	M30高强螺栓	10.9S	M30x200	424	1.94	822.6	
下弦杆拼接	K1	Q355D	□1020×1700×24	2	325.9	651.8	
	K2		□1020×800×24	4	154.5	618	
	K3		□1320×1100×36	1	409.8	409.8	
	K4		□1320×400×36	2	149.8	299.6	
	K5		□920×200×20	6	28.3	169.8	
	K6		□500×1700×12	2	80.1	160.2	填板
	K7		□650×1100×4	0	22.6	0	填板
	M30高强螺栓	10.9S	M30x200	324	1.94	628.6	
腹杆拼接	L1	Q355D	□1520×1100×24	2	314.6	629.2	
	L2		□1520×500×24	4	143.2	572.8	
	L3		□1320×1100×28	1	318.7	318.7	
	L4		□1320×500×28	2	145.1	290.2	
	L5		□1520×1100×44	1	576.8	576.8	
	L6		□1520×240×44	2	124.3	248.6	
	L7		□1220×240×24	4	54.6	218.4	
	L8		□1320×240×24	2	60.3	120.6	
	M30高强螺栓	10.9S	M30x200	540	1.94	1047.6	

中交第二公路勘察设计研究院有限公司	狮子洋通道工程勘察设计 施 工 图 设 计	K6+418.3 新沙高架桥 中桥节段14设计图	设计	余汪千	复核	袁勤	一审	沈华	二审	李忠	图号	SZYS/04/02/02/01/ 22

节段14材料数量表

名称	编号	材质	规格	数量	单件重	共重(kg)	备注
上弦顶板	N11a	Q355D	t=20mm,A=15.28m2	1	2399.7	2399.7	
	N11b	Q355D	t=20mm,A=13.73m2	1	2155.5	2155.5	
上弦底板	N12a	Q355D	□7900×1200×20	1	1488.4	1488.4	
	N12b	Q355D	□7100×1200×20	1	1337.6	1337.6	
上弦节点板	N13	Q355D	t=40mm,A=24.52m2	2	7699.3	15398.6	
上弦腹板	N14	Q355D	□7300×2048×28	2	3286	6572	
上弦横隔板	N15	Q355D	□1980×1200×16	3	298.9	896.7	
	N15a	Q355D	□1980×1200×16	2	298.9	597.8	
	N15 '	Q355D	□2057×200×16	3	51.5	154.5	
	N15b	Q355B	□2057×40×4	4	2.5	10	
	N15c	Q355D	□800×400×16	4	40.2	160.8	
上弦加劲肋	N16a	Q355D	□7900×280×24	6	416.4	2498.4	
	N16b	Q355D	□7100×280×24	6	374.9	2249.4	
下弦顶板	N21a	Q355D	□7901×2500×24	1	3720.9	3720.9	
	N21b	Q355D	□7101×2500×24	1	3344.1	3344.1	
下弦底板	N22a	Q355D	t=24mm,A=12.96m2	1	2441.3	2441.3	
	N22b	Q355D	t=24mm,A=11.13m2	1	2097.4	2097.4	
下弦节点板	N23	Q355D	t=44mm,A=22.5m2	2	7771.5	15543	Z35钢
下弦腹板	N24	Q355D	□7301×1880×32	2	3449	6898	
下弦横隔板	N25	Q355D	□1800×1200×16	3	271.3	813.9	
	N25a	Q355D	□1800×1200×16	2	271.3	542.6	
	N25'	Q355D	□2057×200×16	3	51.5	154.5	
下弦加劲肋	N26a	Q355D	□7901×280×24	4	416.4	1665.6	
	N26b	Q355D	□7101×280×24	4	374.9	1499.6	
	N26c	Q355D	□15002×170×14	2	280.2	560.4	
斜腹杆	N31	Q355D	□11383×1200×36	1	3860.3	3860.3	
	N31a	Q355D	□11283×1200×36	1	3826.4	3826.4	
	N32	Q355D	□7383×1360×36	2	2837.3	5674.6	
	N33	Q355D	□7383×320×32	2	592.8	1185.6	
	N33a	Q355D	□9983×320×32	1	801.3	801.3	
	N33b	Q355D	□9883×320×32	1	793.8	793.8	
	N34	Q355D	□1200×1200×16	3	180.9	542.7	
	N41	Q355D	□5458×1200×36	1	1851	1851	
	N41a	Q355D	□5758×1200×36	1	1952.8	1952.8	
	N42	Q355D	□3658×1360×36	2	1404.5	2809	
	N43	Q355D	□3658×320×32	2	293.9	587.8	
	N43a	Q355D	□4758×320×32	1	381.8	381.8	
	N43b	Q355D	□5058×320×32	1	406.9	406.9	
	N44	Q355D	□1200×1200×16	2	180.9	361.8	
节点板加劲	N51	Q355D	□5883×1200×36	1	1995.2	1995.2	
	N51a	Q355D	□5483×1200×36	1	1859.5	1859.5	
	N52	Q355D	□3683×1360×36	2	1415.8	2831.6	
	N53	Q355D	□3683×320×32	2	296.4	592.8	
	N53a	Q355D	□5183×320×32	1	417	417	
	N53b	Q355D	□4783×320×32	1	384.3	384.3	
	N54	Q355D	□1200×1200×16	2	180.9	361.8	
	N55	Q355D	□2300×320×32	4	185.9	743.6	
	N56	Q355D	□2200×320×32	4	175.8	703.2	
横梁接头	N61	Q355D	□1980×610×14	6	133	798	
	N61a	Q355D	□1980×622×14	4	135.2	540.8	
	N62	Q355D	t=24mm,A=0.47m2	6	89.3	535.8	
	N62a	Q355D	t=24mm,A=0.48m2	4	90.4	361.6	
	N63	Q355D	□1800×606×14	6	119.8	718.8	
	N63a	Q355D	□1800×618×14	4	122	488	
小计						113568.5	
焊缝重1.5%						1704.0	
合计						115272.5	

节段14材料数量汇总表

规格(mm)	材质	单个合计	全桥共1个
t=44	Q355D	15543	15543
t=40		15398.6	15398.6
t=36		26660.4	26660.4
t=32		13896.1	13896.1
t=28		6572	6572
t=24		20414.1	20414.1
t=20		7381.2	7381.2
t=16		4587.1	4587.1
t=14		3106	3106
t=4		10	10
焊缝重(1.5%)		1703.5	1703.5
合计		115272.0	115272.0
内表面涂装(m²)		395.7	395.7
外表面涂装(m²)		592.4	592.4

节段13~节段14拼接数量汇总表

规格(mm)	材质	单个合计	全桥共1个
t=44	Q355D	825.4	825.4
t=36	Q355D	709.4	709.4
t=28	Q355D	993.5	993.5
t=24	Q355D	3861.8	3861.8
t=20	Q355D	169.8	169.8
t=14	Q355D	198	198
t=12	Q355D	363.6	363.6
合计	Q355D	7121.5	7121.5
M30x200	10.9S高强螺栓	2498.8	2498.8
外表面涂装(m²)		36.7	36.7

中交第二公路勘察设计研究院有限公司	狮子洋通道工程勘察设计 施 工 图 设 计	K6+418.3 新沙高架桥 中桥节段14设计图	设计	余汪千	复核	袁勤	一审	张华	二审	李忠	图号	SZYS/04/02/02/01/ 22

大样A（节段14~节段15）

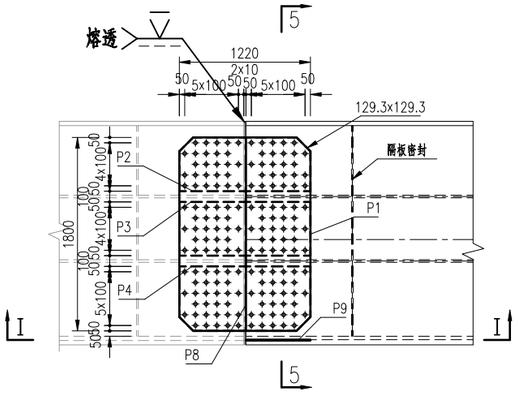

5-5

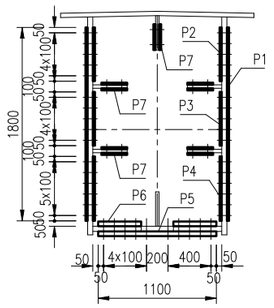

Ⅰ－Ⅰ

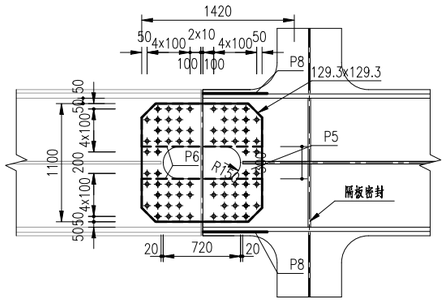

上弦杆顶板、腹板加劲肋拼接

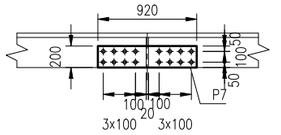

大样C（节段14~节段15）

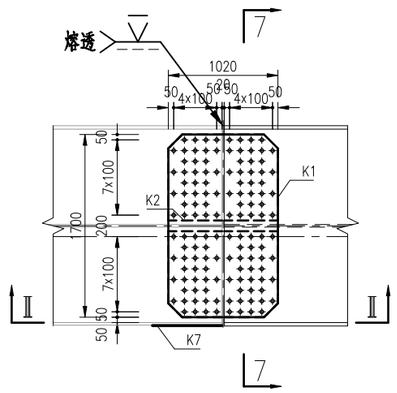

7-7

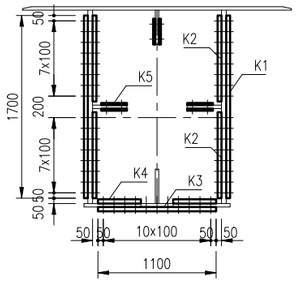

下弦杆顶板、腹板加劲肋拼接

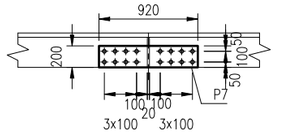

Ⅳ－Ⅳ

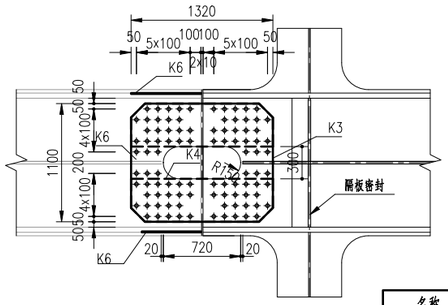

注：

1、本图尺寸均以mm计。

2、未注明的板件裁切边距M30螺栓不小50mm，M24螺栓不小40mm。

3、图中未注明的过焊孔圆弧切角半径为35mm。

4、图中未注明焊缝详见《钢梁焊缝及细节设计图》。

符号：

⊕ —— M30螺栓，开孔直径33mm

⊗ —— M24螺栓，开孔直径26mm

大样B（节段14~节段15）

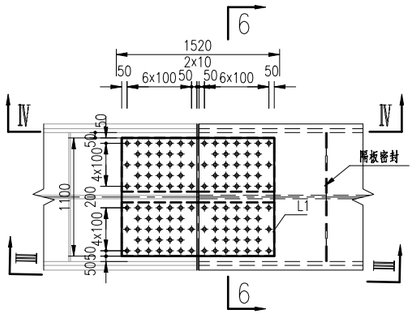

6-6

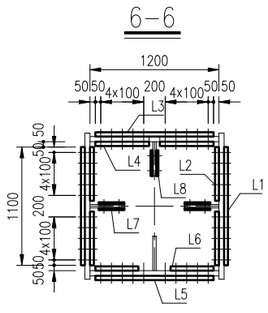

腹杆腹板加劲肋拼接

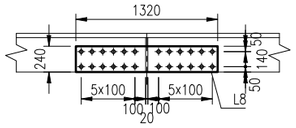

腹杆顶加劲肋拼接

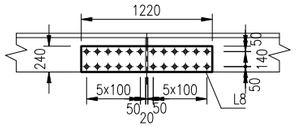

Ⅲ－Ⅲ

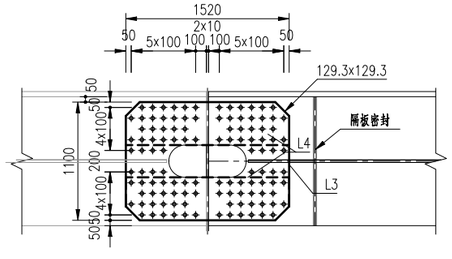

Ⅳ－Ⅳ

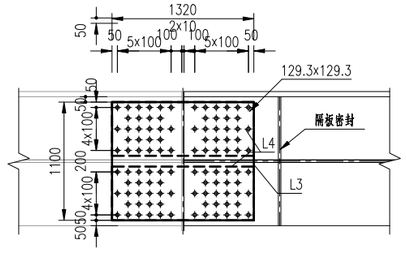

节段14~节段15拼接数量表

名称	编号	材质	规格	数量	单件重	共重（kg）	备注
上弦杆拼接	P1	Q355D	□1220×1800×28	2	483.6	967.2	
	P2		□1220×500×28	2	134.1	268.2	
	P3		□1220×500×28	2	134.1	268.2	
	P4		□1220×600×28	2	160.5	321	
	P5		□1420×1100×32	1	391.9	391.9	
	P6		□1420×400×32	2	143.2	286.4	
	P7		□920×200×20	10	28.3	283	
	P8		□600×1800×8	2	67.8	135.6	填板
	P9		□700×1100×4	1	24.2	24.2	填板
	M30高强螺栓	10.9S	M30x200	508	1.94	985.5	
下弦杆拼接	K1	Q355D	□1020×1700×24	2	325.9	651.8	
	K2		□1020×800×24	4	154.5	618	
	K3		□1320×1100×36	1	409.8	409.8	
	K4		□1320×400×36	2	149.8	299.6	
	K5		□920×200×20	6	28.3	169.8	
	K6		□500×1700×12	2	80.1	160.2	填板
	K7		□650×1100×4	0	22.6	0	填板
	M30高强螺栓	10.9S	M30x200	324	1.94	628.6	
腹杆拼接	L1	Q355D	□1520×1100×24	2	314.6	629.2	
	L2		□1520×500×24	4	143.2	572.8	
	L3		□1320×1100×28	1	318.7	318.7	
	L4		□1320×500×28	2	145.1	290.2	
	L5		□1520×1100×44	1	576.8	576.8	
	L6		□1520×240×44	2	124.3	248.6	
	L7		□1220×240×24	4	54.6	218.4	
	L8		□1320×240×24	2	60.3	120.6	
	M30高强螺栓	10.9S	M30x200	540	1.94	1047.6	

中交第二公路勘察设计研究院有限公司	狮子洋通道工程勘察设计 施 工 图 设 计	K6+418.3 新沙高架桥 中桥节段15设计图	设计	余汪千	复核	袁勤	一审	张华	二审	李忠	图号	SZYS/04/02/02/01/ 23

节段15材料数量表

名称	编号	材质	规格	数量	单件重	共重（kg）	备注
上弦顶板	N11a	Q420D	t=40mm,A=15.28m2	1	4799.3	4799.3	
	N11b	Q355D	t=24mm,A=13.73m2	1	2586.7	2586.7	
上弦底板	N12a	Q420D	□7900×1200×40	1	2976.7	2976.7	
	N12b	Q355D	□7100×1200×24	1	1605.2	1605.2	
上弦节点板	N13	Q420D	t=48mm,A=25.71m2	2	9687.5	19375	
上弦腹板	N14	Q355D	□7300×2048×32	2	3755.4	7510.8	
上弦横隔板	N15	Q355D	□1960×1200×16	3	295.2	885.6	
	N15a	Q355D	□1976×1200×16	2	297.7	595.4	
	N15‘	Q355D	□2057×200×16	3	51.5	154.5	
	N15b	Q355B	□2057×40×4	4	2.5	10	
	N15c	Q355D	□800×400×16	4	40.2	160.8	
上弦加劲肋	N16a	Q420D	□7900×320×32	6	635.5	3813	
	N16b	Q355D	□7100×280×24	6	374.9	2249.4	
下弦顶板	N21a	Q355D	□7900×2500×24	1	3720.9	3720.9	
	N21b	Q355D	□7100×2500×24	1	3344.1	3344.1	
下弦底板	N22a	Q355D	t=24mm,A=12.96m2	1	2441.1	2441.1	
	N22b	Q355D	t=24mm,A=11.13m2	1	2097.1	2097.1	
下弦节点板	N23	Q355D	t=44mm,A=22.5m2	2	7771.5	15543	Z35钢
下弦腹板	N24	Q355D	□7300×1880×32	2	3446.5	6893	
下弦横隔板	N25	Q355D	□1800×1200×16	3	271.3	813.9	
	N25a	Q355D	□1800×1200×16	2	271.3	542.6	
	N25’	Q355D	□2057×200×16	5	51.5	257.5	
下弦加劲肋	N26a	Q355D	□7900×280×24	4	416.4	1665.6	
	N26b	Q355D	□7100×320×32	4	570.2	2280.8	
	N26c	Q355D	□15000×170×14	2	280.2	560.4	
斜腹杆	N31	Q355D	□11322×1200×36	1	3840.5	3840.5	
	N31a	Q355D	□11222×1200×36	1	3806.6	3806.6	
	N32	Q355D	□7322×1360×36	2	2814.7	5629.4	
	N33	Q355D	□7322×320×32	2	587.8	1175.6	
	N33a	Q355D	□9922×320×32	1	798.8	798.8	
	N33b	Q355D	□9822×320×32	1	788.8	788.8	
	N34	Q355D	□1200×1200×16	3	180.9	542.7	
	N41	Q355D	□5440×1200×48	1	2460.5	2460.5	
	N41a	Q355D	□5740×1200×48	1	2596.2	2596.2	
	N42	Q355D	□3640×1760×48	2	2415.3	4830.6	
	N43	Q355D	□3640×320×32	4	291.4	1165.6	
	N43a	Q355D	□4740×320×32	1	381.8	381.8	
	N43b	Q355D	□5040×320×32	1	404.4	404.4	
	N44	Q355D	□1200×1600×16	2	241.2	482.4	
节点板加劲	N51	Q355D	□5858×1200×48	1	2648.9	2648.9	
	N51a	Q355D	□5458×1200×48	1	2468	2468	
	N52	Q355D	□3658×1360×48	2	1872.7	3745.4	
	N53	Q355D	□3658×320×32	2	293.9	587.8	
	N53a	Q355D	□5158×320×32	1	414.5	414.5	
	N53b	Q355D	□4758×320×32	1	381.8	381.8	
	N54	Q355D	□1200×1200×16	2	180.9	361.8	
	N55	Q355D	□2100×320×32	6	168.3	1009.8	
	N56	Q355D	□2200×320×32	4	175.8	703.2	
横梁接头	N61	Q355D	□1960×602×14	6	129.7	778.2	
	N61a	Q355D	□1976×618×14	4	134.1	536.4	
	N62	Q355D	t=24mm,A=0.47m2	6	89.3	535.8	
	N62a	Q355D	t=24mm,A=0.48m2	4	90.4	361.6	
	N63	Q355D	□1800×606×14	6	119.8	718.8	
	N63a	Q355D	□1800×618×14	4	122	488	
小计						131526.3	
焊缝重1.5%						1973.0	
合计						133499.3	

节段15材料数量汇总表

规格（mm）	材质	单个合计	全桥共1个
t=48	Q420D	19375	19375.0
t=40		7776	7776.0
t=32		3813	3813.0
合计		30964	30964.0
t=48	Q355D	18749.6	18749.6
t=44		15543	15543.0
t=36		13276.5	13276.5
t=32		24496.7	24496.7
t=24		20607.5	20607.5
t=16		4797.2	4797.2
t=14		3081.8	3081.8
t=4		10	10.0
合计		100562.3	100562.3
焊缝重（1.5%）		1973.0	1973.0
内表面涂装（m²）		382.6	382.6
外表面涂装（m²）		630.5	630.5

节段14~节段15拼接数量汇总表

规格（mm）	材质	单个合计	全桥共1个
t=44	Q355D	825.4	825.4
t=36		709.4	709.4
t=32		678.3	678.3
t=28		2433.5	2433.5
t=24		2810.8	2810.8
t=20		452.8	452.8
t=12		160.2	160.2
t=8		135.6	135.6
t=4		24.2	24.2
合计		8230.2	8230.2
M30x200	10.9S高强螺栓	2661.7	2661.7
外表面涂装（m²）		41.1	41.1

中交第二公路勘察设计研究院有限公司	狮子洋通道工程勘察设计 施 工 图 设 计	K6+418.3 新沙高架桥 中桥节段15设计图	设计	余汪千	复核	袁勤	一审	沈华	二审	李忠	图号	SZYS/04/02/02/01/ 23

大样A（节段15~节段16）

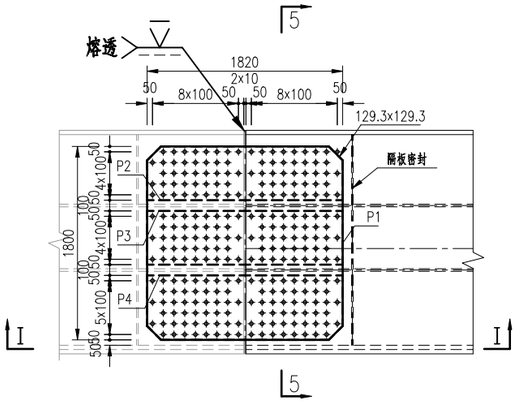

5-5

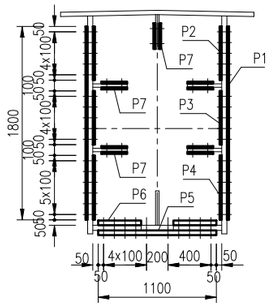

Ⅰ－Ⅰ

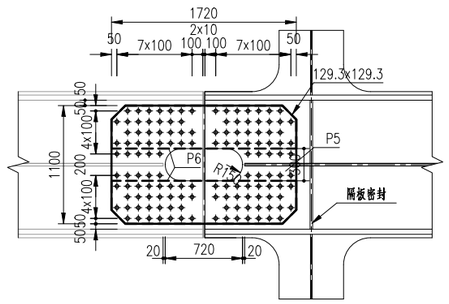

上弦杆顶板、腹板加劲肋拼接

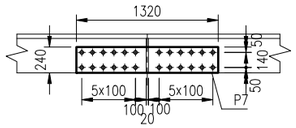

大样C（节段15~节段16）

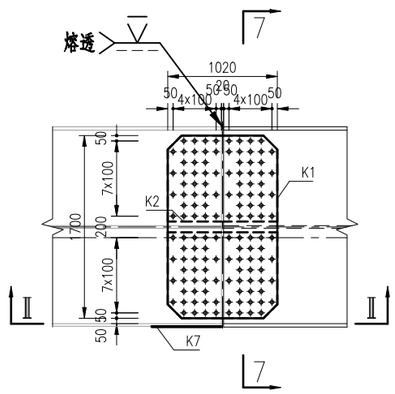

7-7

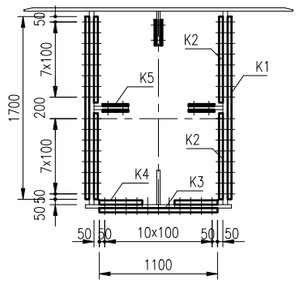

下弦杆顶板、腹板加劲肋拼接

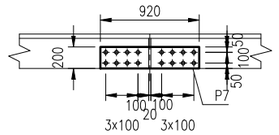

Ⅳ－Ⅳ

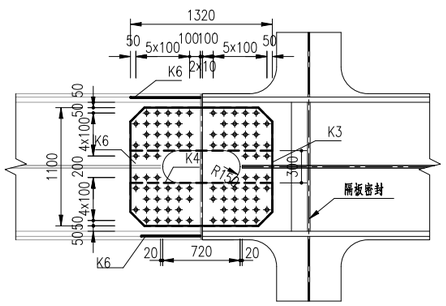

注：

1、本图尺寸均以mm计。

2、未注明的板件裁切边距M30螺栓不小50mm，M24螺栓不小40mm。

3、图中未注明的过焊孔圆弧切角半径为35mm。

4、图中未注明焊缝详见《钢梁焊缝及细节设计图》。

符号：

⊕ —— M30螺栓，开孔直径33mm

⊗ —— M24螺栓，开孔直径26mm

大样B（节段15~节段16）

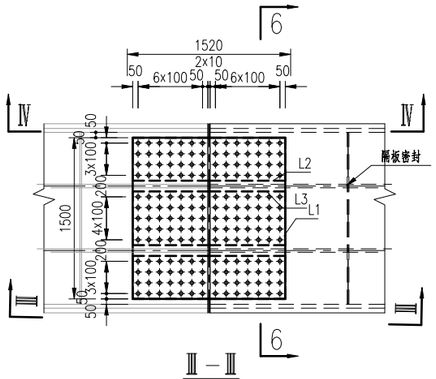

6-6

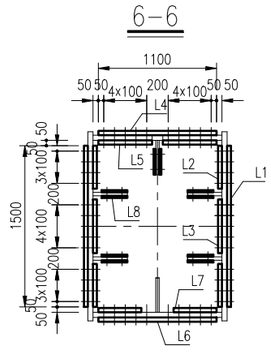

腹杆腹板加劲肋拼接

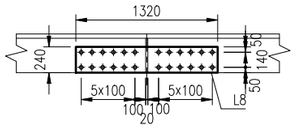

腹杆顶加劲肋拼接

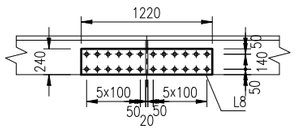

Ⅲ－Ⅲ

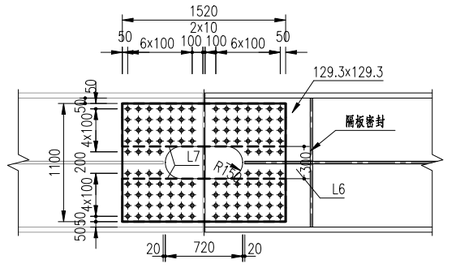

Ⅳ－Ⅳ

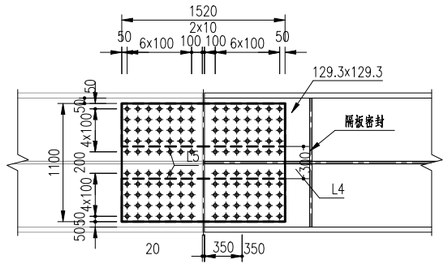

节段15~节段16拼接数量表

名称	编号	材质	规格	数量	单件重	共重（kg）	备注
上弦杆拼接	P1	Q420D	□1820×1800×40	2	1029.9	2059.8	
	P2		□1820×500×40	2	285.7	571.4	
	P3		□1820×500×40	2	285.7	571.4	
	P4		□1820×600×40	2	342.3	684.6	
	P5		□1720×1100×44	1	652.8	652.8	
	P6		□1720×400×44	2	238.3	476.6	
	P7		□1320×240×24	10	60.3	603	
	M30高强螺栓	10.9S	M30×200	780	1.94	1513.2	
下弦杆拼接	K1	Q355D	□1020×1700×24	2	325.9	651.8	
	K2		□1020×800×24	4	154.5	618	
	K3		□1320×1100×36	1	409.8	409.8	
	K4		□1320×400×36	2	149.8	299.6	
	K5		□920×200×20	6	28.3	169.8	
	K6		□500×1700×16	2	106.8	213.6	填板
	K7		□650×1100×8	1	45.2	45.2	填板
	M30高强螺栓	10.9S	M30×200	324	1.94	628.6	
腹杆拼接	L1	Q420D	□1520×1500×32	2	572.7	1145.4	
	L2		□1520×400×32	4	153.2	612.8	
	L3		□1520×500×32	2	190.9	381.8	
	L4		□1520×1100×28	1	367.1	367.1	
	L5		□1520×500×28	2	167	334	
	L6		□1520×1100×40	1	524.4	524.4	
	L7		□1520×400×40	2	191.5	383	
	L8		□1320×240×24	10	60.3	603	
	M30高强螺栓	10.9S	M30×200	752	1.94	1458.9	

中交第二公路勘察设计研究院有限公司	狮子洋通道工程勘察设计 施 工 图 设 计	K6+418.3 新沙高架桥 中桥节段16设计图	设计	余汪千	复核	李勤	一审	张华	二审	李忠	图号	SZYS/04/02/02/01/ 24

72550101493268

节段16材料数量表

名称	编号	材质	规格	数量	单件重	共重(kg)	备注
上弦顶板	N11a	Q420D	t=40mm,A=15.28m2	1	4799.3	4799.3	
	N11b	Q420D	t=40mm,A=13.46m2	1	4226.3	4226.3	
上弦底板	N12a	Q420D	□7900×1200×40	1	2976.7	2976.7	
	N12b	Q420D	□6950×1200×40	1	2618.8	2618.8	
上弦节点板	N13	Q420D	t=44mm,A=26.55m2	2	9170.4	18340.8	
上弦腹板	N14	Q420D	□7150×2048×48	2	5516.4	11032.8	
上弦横隔板	N15	Q420D	□1960×1200×16	3	295.2	885.6	
	N15a	Q420D	□1960×1200×16	2	295.2	590.4	
	N15 '	Q420D	□2057×200×16	3	51.5	154.5	
	N15b	Q355B	□2057×40×4	4	2.5	10	
	N15c	Q420D	□800×400×16	4	40.2	160.8	
上弦加劲肋	N16a	Q420D	□7900×320×32	6	635.5	3813	
	N16b	Q420D	□6950×320×32	6	557.7	3346.2	
下弦顶板	N21a	Q420D	□7900×2500×32	1	4961.2	4961.2	
	N21b	Q420D	□7100×2500×32	1	4458.8	4458.8	
下弦底板	N22a	Q420D	t=32mm,A=12.96m2	1	3254.7	3254.7	
	N22b	Q420D	t=32mm,A=11.13m2	1	2796.2	2796.2	
下弦节点板	N23	Q420D	t=44mm,A=24.17m2	2	8348.3	16696.6	Z35钢
下弦腹板	N24	Q420D	□7300×1880×44	2	4738.9	9477.8	
下弦横隔板	N25	Q420D	□1800×1200×16	3	271.3	813.9	
	N25a	Q420D	□1800×1200×16	2	271.3	542.6	
	N25'	Q420D	□2057×200×16	3	51.5	154.5	
下弦加劲肋	N26a	Q420D	□7900×320×32	4	635.5	2542	
	N26b	Q420D	□7100×320×32	4	570.2	2280.8	
	N26c	Q420D	□15000×170×14	2	280.2	560.4	
斜腹杆	N31	Q420D	□10875×1200×40	1	4097.7	4097.7	
	N31a	Q420D	□11075×1200×40	1	4173.1	4173.1	
	N32	Q420D	□7275×1760×40	2	4019.2	8038.4	
	N33	Q420D	□7275×320×32	4	585.3	2341.2	
	N33a	Q420D	□9475×320×32	1	761.1	761.1	
	N33b	Q420D	□9675×320×32	1	778.7	778.7	
	N34	Q420D	□1200×1600×16	3	241.2	723.6	
	N41	Q420D	□5429×1200×40	1	2044.1	2044.1	
	N41a	Q420D	□5629×1200×40	1	2119.5	2119.5	
	N42	Q420D	□3629×1760×40	2	2006.5	4013	
	N43	Q420D	□3629×320×32	4	291.4	1165.6	
	N43a	Q420D	□4729×320×32	1	379.3	379.3	
	N43b	Q420D	□4929×320×32	1	396.9	396.9	
	N44	Q420D	□1200×1600×16	3	241.2	723.6	
节点板加劲	N51	Q420D	□5440×1200×40	1	2050.4	2050.4	
	N51a	Q420D	□5640×1200×40	1	2125.8	2125.8	
	N52	Q420D	□3640×1760×40	2	2012.7	4025.4	
	N53	Q420D	□3640×320×32	4	291.4	1165.6	
	N53a	Q420D	□4740×320×32	1	381.8	381.8	
	N53b	Q420D	□4940×320×32	1	396.9	396.9	
	N54	Q420D	□1200×1600×16	3	241.2	723.6	
	N55	Q420D	□2100×320×32	8	168.3	1346.4	
	N56	Q420D	□2000×320×32	8	160.8	1286.4	
横梁接头	N61	Q355D	□1960×606×14	6	130.8	784.8	
	N61a	Q355D	□1960×602×14	4	129.7	518.8	
	N62	Q355D	t=24mm,A=0.47m2	6	89.3	535.8	
	N62a	Q355D	t=24mm,A=0.48m2	4	90.4	361.6	
	N63	Q355D	□1800×606×14	6	119.8	718.8	
	N63a	Q355D	□1800×606×14	4	119.8	479.2	
小计						150151.8	
焊缝重1.5%						2252.0	
合计						152403.8	

节段16材料数量汇总表

规格(mm)	材质	单个合计	全桥共1个
t=48	Q420D	11032.8	11032.8
t=44		44515.2	44515.2
t=40		47308.5	47308.5
t=32		37852.8	37852.8
t=16		5473.1	5473.1
t=14		560.4	560.4
t=4		10	10.0
合计	Q355D	146752.8	146752.8
t=24		897.4	897.4
t=14		2501.6	2501.6
合计		3399	3399.0
焊缝重(1.5%)		2252.0	2252.0
内表面涂装(㎡)		429.1	429.1
外表面涂装(㎡)		643.0	643.0

节段15~节段16拼接数量汇总表

规格(mm)	材质	单个合计	全桥共1个
t=44	Q420D	1129.4	1129.4
t=40		4794.6	4794.6
t=32		2140	2140
t=28		701.1	701.1
t=24		1206	1206
合计		9971.1	9971.1
t=36	Q355D	709.4	709.4
t=24		1269.8	1269.8
t=20		169.8	169.8
t=16		213.6	213.6
t=8		45.2	45.2
合计		2407.8	2407.8
M30x200	10.9S高强螺栓	3600.7	3600.7
外表面涂装(㎡)		49.4	49.4

大样A（节段16~节段17）

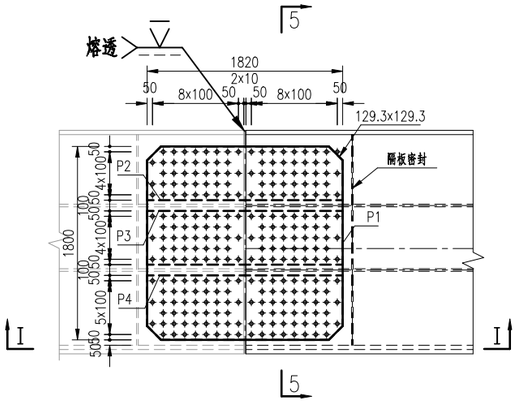

5-5

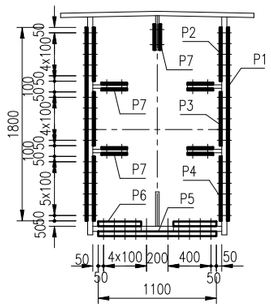

大样C（节段16~节段17）

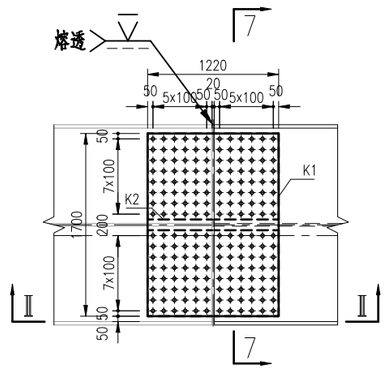

7-7

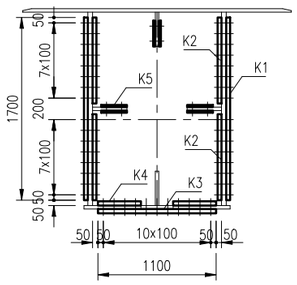

注：

1、本图尺寸均以mm计。

2、未注明的板件裁切边距M30螺栓不小50mm，M24螺栓不小40mm。

3、图中未注明的过焊孔圆弧切角半径为35mm。

4、图中未注明焊缝详见《钢梁焊缝及细节设计图》。

符号：

—— M30螺栓，开孔直径33mm

—— M24螺栓，开孔直径26mm

Ⅰ－Ⅰ

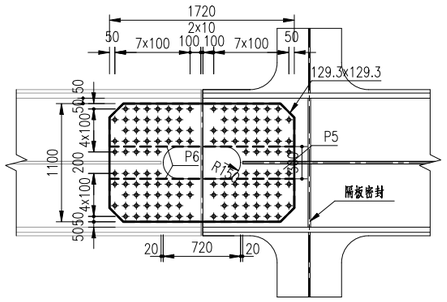

上弦杆顶板、腹板加劲肋拼接

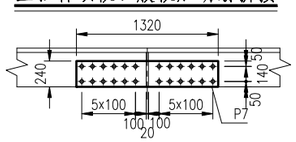

Ⅳ－Ⅳ

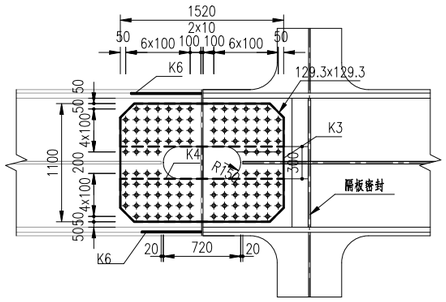

下弦杆顶板、腹板加劲肋拼接

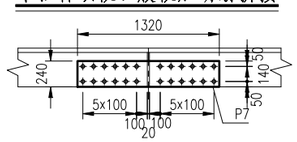

大样B（节段16~节段17）

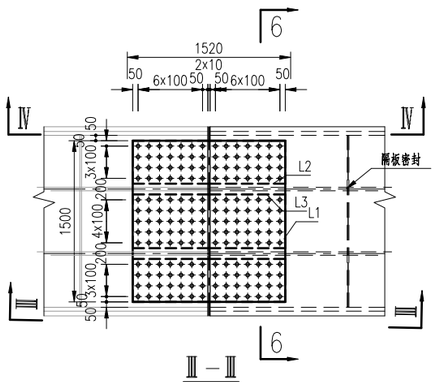

6-6

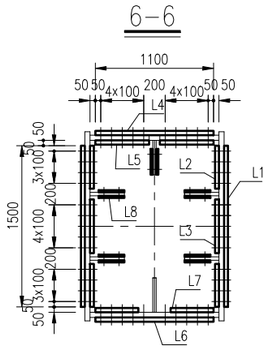

腹杆腹板加劲肋拼接

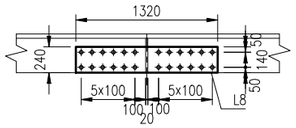

腹杆顶加劲肋拼接

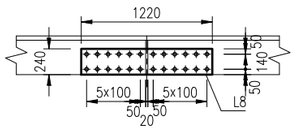

Ⅲ－Ⅲ

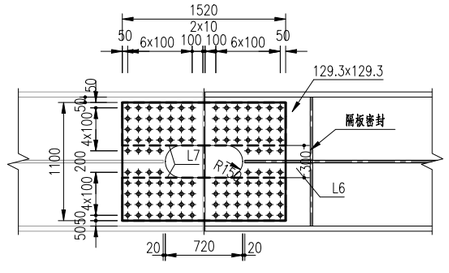

Ⅳ－Ⅳ

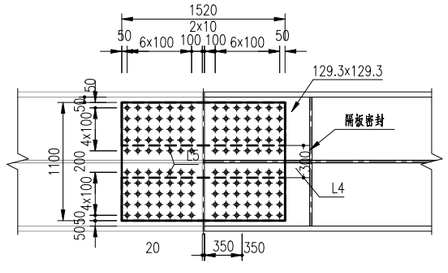

节段16~节段17拼接数量表

名称	编号	材质	规格	数量	单件重	共重（kg）	备注
上弦杆拼接	P1	Q420D	□1820×1800×40	2	1029.9	2059.8	
	P2		□1820×500×40	2	285.7	571.4	
	P3		□1820×500×40	2	285.7	571.4	
	P4		□1820×600×40	2	342.3	684.6	
	P5		□1720×1100×44	1	652.8	652.8	
	P6		□1720×400×44	2	238.3	476.6	
	P7		□1320×240×24	10	60.3	603	
	M30高强螺栓	10.9S	M30x200	780	1.94	1513.2	
下弦杆拼接	K1	Q420D	□1220×1700×28	2	455	910	
	K2		□1220×800×28	4	215.4	861.6	
	K3		□1520×1100×36	1	471.9	471.9	
	K4		□1520×400×36	2	172.4	344.8	
	K5		□1320×240×24	6	60.3	361.8	
	K6		□650×1100×4	1	22.6	22.6	填板
	M30高强螺栓	10.9S	M30x200	580	1.94	1125.2	
腹杆拼接	L1	Q420D	□1520×1500×32	2	572.7	1145.4	
	L2		□1520×400×32	4	153.2	612.8	
	L3		□1520×500×32	2	190.9	381.8	
	L4		□1520×1100×28	1	367.1	367.1	
	L5		□1520×500×28	2	167	334	
	L6		□1520×1100×40	1	524.4	524.4	
	L7		□1520×400×40	2	191.5	383	
	L8		□1320×240×24	10	60.3	603	
	M30高强螺栓	10.9S	M30x200	752	1.94	1458.9	

中交第二公路勘察设计研究院有限公司	狮子洋通道工程勘察设计 施 工 图 设 计	K6+418.3 新沙高架桥 中桥节段17设计图	设计	余汪千	复核	袁勤	一审	张华	二审	李忠	图号	SZYS/04/02/02/01/ 25

72510111725690

节段17材料数量表

名称	编号	材质	规格	数量	单件重	共重(kg)	备注
上弦顶板	N11a	Q420D	t=40mm,A=15.28m2	1	4799.3	4799.3	
	N11b	Q420D	t=40mm,A=13.73m2	1	4311.1	4311.1	
上弦底板	N12a	Q420D	□7900×1200×40	1	2976.7	2976.7	
	N12b	Q420D	□7100×1200×40	1	2675.3	2675.3	
上弦节点板	N13	Q420D	t=44mm,A=26.09m2	2	9011.5	18023	
上弦腹板	N14	Q420D	□7300×2048×48	2	5633.2	11266.4	
上弦横隔板	N15	Q420D	□1960×1200×16	3	295.2	885.6	
	N15a	Q420D	□1960×1200×16	2	295.2	590.4	
	N15 ‘	Q420D	□2057×200×16	3	51.5	154.5	
	N15b	Q355B	□2057×40×4	4	2.5	10	
	N15c	Q420D	□800×400×16	4	40.2	160.8	
上弦加劲肋	N16a	Q420D	□7900×320×32	6	635.5	3813	
	N16b	Q420D	□7100×320×32	6	570.2	3421.2	
下弦顶板	N21a	Q420D	□7901×2500×32	1	4961.2	4961.2	
	N21b	Q420D	□6950×2500×32	1	4365.9	4365.9	
下弦底板	N22a	Q420D	t=40mm,A=17.24m2	1	5413.4	5413.4	
	N22b	Q420D	t=32mm,A=10.93m2	1	2744.9	2744.9	
下弦节点板	N23	Q420D	t=44mm,A=25.5m2	2	8807.7	17615.4	Z35钢
下弦腹板	N24	Q420D	□7150×1880×44	2	4642.2	9284.4	
下弦横隔板	N25	Q420D	□1800×1200×16	3	271.3	813.9	
	N25a	Q420D	□1800×1200×16	2	271.3	542.6	
	N25’	Q420D	□2057×200×16	3	51.5	154.5	
下弦加劲肋	N26a	Q420D	□7901×320×32	4	635.5	2542	
	N26b	Q420D	□6950×320×32	4	557.7	2230.8	
	N26c	Q420D	□14851×170×14	2	276.9	553.8	
斜腹杆	N31	Q420D	□10842×1200×40	1	4085.1	4085.1	
	N31a	Q420D	□11042×1200×40	1	4160.5	4160.5	
	N32	Q420D	□7242×1760×40	2	4003.5	8007	
	N33	Q420D	□7242×320×32	4	582.8	2331.2	
	N33a	Q420D	□9442×320×32	1	758.6	758.6	
	N33b	Q420D	□9642×320×32	1	776.2	776.2	
	N34	Q420D	□1200×1600×16	3	241.2	723.6	
	N41	Q420D	□5426×1200×36	1	1839.7	1839.7	
	N41a	Q420D	□5726×1200×36	1	1941.5	1941.5	
	N42	Q420D	□3626×1360×36	2	1393.2	2786.4	
	N43	Q420D	□3626×320×32	2	291.4	582.8	
	N43a	Q420D	□4726×320×32	1	379.3	379.3	
	N43b	Q420D	□5026×320×32	1	404.4	404.4	
	N44	Q420D	□1200×1200×16	2	180.9	361.8	
节点板加劲	N51	Q420D	□5629×1200×40	1	2119.5	2119.5	
	N51a	Q420D	□5229×1200×40	1	1968.8	1968.8	
	N52	Q420D	□3629×1760×40	2	2006.5	4013	
	N53	Q420D	□3629×320×32	4	291.4	1165.6	
	N53a	Q420D	□4229×320×32	1	339.1	339.1	
	N53b	Q420D	□3829×320×32	1	309	309	
	N54	Q420D	□1200×1600×16	2	241.2	482.4	
	N55	Q420D	□2100×320×32	6	168.3	1009.8	
	N56	Q420D	□2000×320×32	8	160.8	1286.4	
横梁接头	N61	Q355D	□1960×606×14	6	130.8	784.8	
	N61a	Q355D	□1960×602×14	4	129.7	518.8	
	N62	Q355D	t=24mm,A=0.47m2	6	89.3	535.8	
	N62a	Q355D	t=24mm,A=0.48m2	4	90.4	361.6	
	N63	Q355D	□1800×606×14	4	119.8	479.2	
	N63a	Q355D	□1800×606×14	4	119.8	479.2	
支座加劲	N81	Q420D	□1800×1200×32	5	542.6	2713	
	N82	Q420D	□1800×602×44	6	373	2238	
	N83	Q420D	□2800×2650×80	1	4659.8	4659.8	
	N84	Q420D	□1000×568×32	4	143.2	572.8	
	N85	Q420D	□1350×570×32	4	193.4	773.6	
小计						160258.4	
焊缝重1.5%						2404.0	
合计						162662.4	

节段17材料数量汇总表

规格(mm)	材质	单个合计	全桥共1个
t=80	Q420D	4659.8	4659.8
t=48		11266.4	11266.4
t=44		47160.8	47160.8
t=40		44529.7	44529.7
t=36		6567.6	6567.6
t=32		37480.8	37480.8
t=16		4870.1	4870.1
t=14		553.8	553.8
t=4		10.0	10.0
合计		157099.0	157099.0
t=24	Q355D	897.4	897.4
t=14		2262.0	2262.0
合计		3159.4	3159.4
焊缝重(1.5%)		2404.0	2404.0
内表面涂装(m²)		502.2	502.2
外表面涂装(m²)		613.0	613.0

节段16~节段17拼接数量汇总表

规格(mm)	材质	单个合计	全桥共1个
t=44	Q420D	1129.4	1129.4
t=40		4794.6	4794.6
t=36		816.7	816.7
t=32		2140	2140
t=28		2472.7	2472.7
t=24		1567.8	1567.8
t=4		22.6	22.6
合计		12943.8	12943.8
M30x200	10.9S高强螺栓	4097.3	4097.3
外表面涂装(m²)		50.2	50.2

中交第二公路勘察设计研究院有限公司	狮子洋通道工程勘察设计 施 工 图 设 计	K6+418.3 新沙高架桥 中桥节段17设计图	设计	余汪千	复核	袁勤	一审	沈华	二审	王忠	图号	SZYS/04/02/02/01/25

大样A（节段17~节段18）

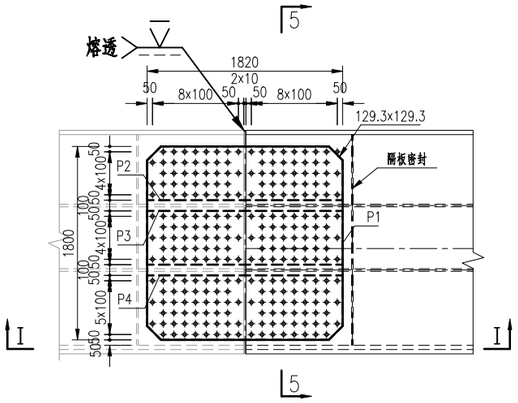

5-5

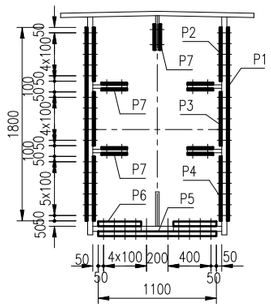

大样C（节段17~节段18）

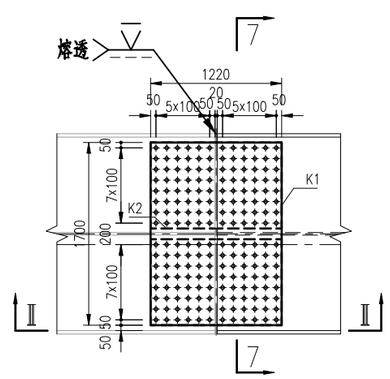

7-7

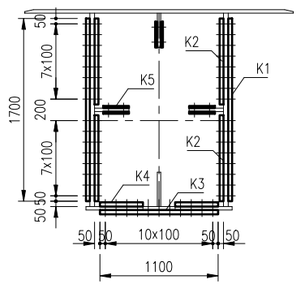

注：

1、本图尺寸均以mm计。

2、未注明的板件裁切边距M30螺栓不小50mm，M24螺栓不小40mm。

3、图中未注明的过焊孔圆弧切角半径为35mm。

4、图中未注明焊缝详见《钢梁焊缝及细节设计图》。

符号：

⊕ —— M30螺栓，开孔直径33mm

⊗ —— M24螺栓，开孔直径26mm

I－I

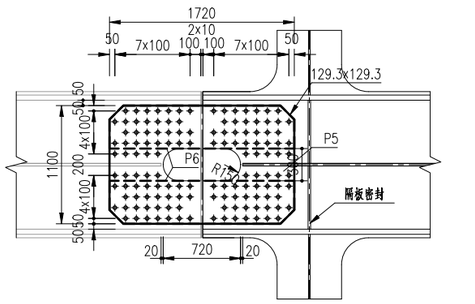

上弦杆顶板、腹板加劲肋拼接

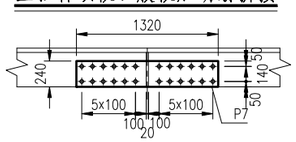

Ⅳ－Ⅳ

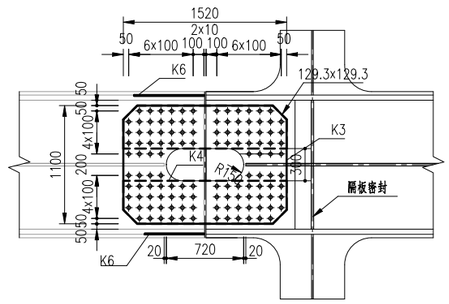

下弦杆顶板、腹板加劲肋拼接

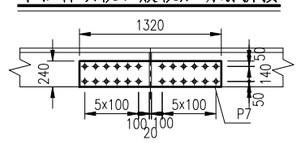

节段17~节段18拼接数量表

名称	编号	材质	规格	数量	单件重	共重（kg）	备注
上弦杆拼接	P1	Q420D	□1820×1800×40	2	1029.9	2059.8	
	P2		□1820×500×40	2	285.7	571.4	
	P3		□1820×500×40	2	285.7	571.4	
	P4		□1820×600×40	2	342.3	684.6	
	P5		□1720×1100×44	1	652.8	652.8	
	P6		□1720×400×44	2	238.3	476.6	
	P7		□1320×240×24	10	60.3	603	
	M30高强螺栓	10.9S	M30×200	780	1.94	1513.2	
下弦杆拼接	K1	Q420D	□1220×1700×28	2	455	910	
	K2		□1220×800×28	4	215.4	861.6	
	K3		□1520×1100×36	1	471.9	471.9	
	K4		□1520×400×36	2	172.4	344.8	
	K5		□1320×240×24	6	60.3	361.8	
	K6		□650×1100×4	1	22.6	22.6	填板
	M30高强螺栓	10.9S	M30×200	580	1.94	1125.2	
腹杆拼接	L1	Q355D	□1520×1100×24	2	314.6	629.2	
	L2		□1520×500×24	4	143.2	572.8	
	L3		□1320×1100×28	1	318.7	318.7	
	L4		□1320×500×28	2	145.1	290.2	
	L5		□1520×1100×44	1	576.8	576.8	
	L6		□1520×240×44	2	124.3	248.6	
	L7		□1220×240×24	4	54.6	218.4	
	L8		□1320×240×24	2	60.3	120.6	
	M30高强螺栓	10.9S	M30×200	540	1.94	1047.6	

大样B（节段17~节段18）

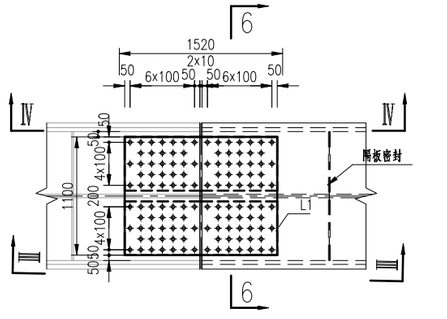

6-6

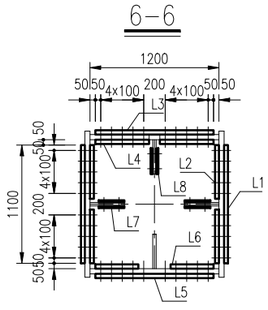

腹杆腹板加劲肋拼接

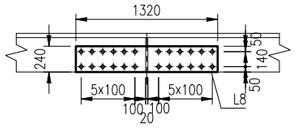

腹杆顶加劲肋拼接

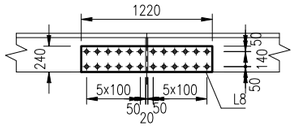

Ⅲ－Ⅲ

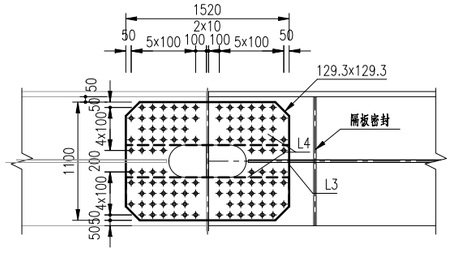

Ⅳ－Ⅳ

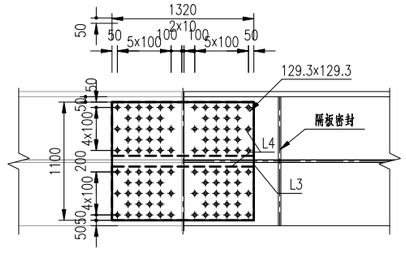

中交第二公路勘察设计研究院有限公司	狮子洋通道工程勘察设计 施 工 图 设 计	K6+418.3 新沙高架桥 中桥节段18设计图	设计	余汪千	复核	袁勤	一审	沈雁	二审	王忠	图号	SZYS/04/02/02/01/ 26

节段18材料数量表

名称	编号	材质	规格	数量	单件重	共重（kg）	备注
上弦顶板	N11a	Q420D	t=40mm,A=15.28m2	1	4799.3	4799.3	
	N11b	Q420D	t=40mm,A=13.73m2	1	4311.1	4311.1	
上弦底板	N12a	Q420D	□7900×1200×40	1	2976.7	2976.7	
	N12b	Q420D	□7100×1200×40	1	2675.3	2675.3	
上弦节点板	N13	Q420D	t=48mm,A=24.52m2	2	9239.1	18478.2	
上弦腹板	N14	Q420D	□7300×2048×48	2	5633.2	11266.4	
上弦横隔板	N15	Q420D	□1960×1200×16	3	295.2	885.6	
	N15a	Q420D	□1960×1200×16	2	295.2	590.4	
	N15＇	Q420D	□2057×200×16	3	51.5	154.5	
	N15b	Q355B	□2057×40×4	4	2.5	10	
	N15c	Q420D	□800×400×16	4	40.2	160.8	
上弦加劲肋	N16a	Q420D	□7900×320×32	6	635.5	3813	
	N16b	Q420D	□7100×320×32	6	570.2	3421.2	
下弦顶板	N21a	Q420D	□7900×2500×32	1	4961.2	4961.2	
	N21b	Q355D	□7100×2500×24	1	3344.1	3344.1	
下弦底板	N22a	Q420D	t=32mm,A=12.96m2	1	3254.7	3254.7	
	N22b	Q355D	t=24mm,A=11.13m2	1	2097.1	2097.1	
下弦节点板	N23	Q420D	t=48mm,A=22.49m2	2	8474.2	16948.4	Z35钢
下弦腹板	N24	Q355D	□7300×1880×32	2	3446.5	6893	
下弦横隔板	N25	Q355D	□1800×1200×16	3	271.3	813.9	
	N25a	Q355D	□1800×1200×16	2	271.3	542.6	
	N25'	Q355D	□2057×200×16	3	51.5	154.5	
下弦加劲肋	N26a	Q420D	□7900×320×32	4	635.5	2542	
	N26b	Q355D	□7100×320×32	4	570.2	2280.8	
	N26c	Q355D	□15000×170×14	2	280.2	560.4	
斜腹杆	N31	Q355D	□10823×1200×36	1	3671	3671	
	N31a	Q355D	□11023×1200×36	1	3738.8	3738.8	
	N32	Q355D	□7223×1360×36	2	2775.1	5550.2	
	N33	Q355D	□7223×320×32	2	580.3	1160.6	
	N33a	Q355D	□9423×320×32	1	758.6	758.6	
	N33b	Q355D	□9623×320×32	1	773.7	773.7	
	N34	Q355D	□1200×1200×16	3	180.9	542.7	
	N41	Q355D	□5429×1200×36	1	1839.7	1839.7	
	N41a	Q355D	□5629×1200×36	1	1907.6	1907.6	
	N42	Q355D	□3629×1360×36	2	1396	2792	
	N43	Q355D	□3629×320×32	4	291.4	1165.6	
	N43a	Q355D	□4729×320×32	1	379.3	379.3	
	N43b	Q355D	□4929×320×32	1	396.9	396.9	
	N44	Q355D	□1200×1200×16	3	180.9	542.7	
节点板加劲	N51	Q355D	□5426×1200×36	1	1839.7	1839.7	
	N51a	Q355D	□5626×1200×36	1	1907.6	1907.6	
	N52	Q355D	□3626×1360×36	2	1393.2	2786.4	
	N53	Q355D	□3626×320×32	4	291.4	1165.6	
	N53a	Q355D	□4726×320×32	1	379.3	379.3	
	N53b	Q355D	□4926×320×32	1	396.9	396.9	
	N54	Q355D	□1200×1200×16	3	180.9	542.7	
	N55	Q355D	□2300×320×32	4	185.9	743.6	
	N56	Q355D	□2200×320×32	4	175.8	703.2	
横梁接头	N61	Q355D	□1960×602×14	6	129.7	778.2	
	N61a	Q355D	□1960×602×14	4	129.7	518.8	
	N62	Q355D	t=24mm,A=0.47m2	6	89.3	535.8	
	N62a	Q355D	t=24mm,A=0.48m2	4	90.4	361.6	
	N63	Q355D	□1800×602×14	6	118.7	712.2	
	N63a	Q355D	□1800×618×14	4	122	488	
小计						137014.2	
焊缝重1.5%						2055.0	
合计						139069.2	

节段18材料数量汇总表

规格（mm）	材质	单个合计	全桥共1个
t=48	Q420D	46693	46693.0
t=40		14762.4	14762.4
t=32		17992.1	17992.1
t=16		1791.3	1791.3
t=4		10	10.0
合计		81248.8	81248.8
t=36	Q355D	26033	26033.0
t=32		17197.1	17197.1
t=24		6338.6	6338.6
t=16		3139.1	3139.1
t=14		3057.6	3057.6
合计		55765.4	55765.4
焊缝重（1.5%）		2055.0	2055.0
内表面涂装（m²）		476.7	476.7
外表面涂装（m²）		531.7	531.7

节段17~节段18拼接数量汇总表

规格（mm）	材质	单个合计	全桥共1个
t=44	Q420D	1129.4	1129.4
t=40		3887.2	3887.2
t=36		816.7	816.7
t=28		1771.6	1771.6
t=24		964.8	964.8
t=4		22.6	22.6
合计		8592.3	8592.3
t=44	Q355D	825.4	825.4
t=28		608.9	608.9
t=24		1541	1541
合计		2975.3	2975.3
M30×200	10.9S高强螺栓	3686.0	3686.0
外表面涂装（m²）		45.8	45.8

中交第二公路勘察设计研究院有限公司	狮子洋通道工程勘察设计 施 工 图 设 计	K6+418.3 新沙高架桥 中桥节段18设计图	设计	余汪千	复核	袁勤	一审	沈雁	二审	李忠	图号	SZYS/04/02/02/01/ 26

大样A（节段18~节段19）

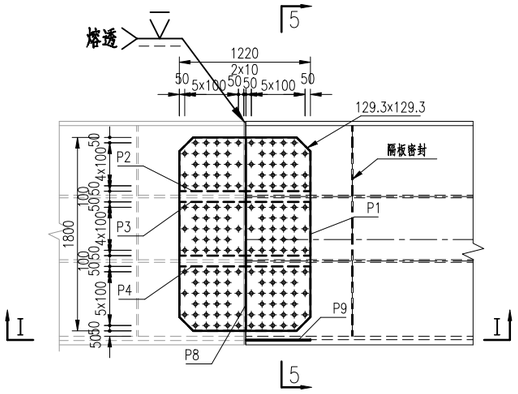

5-5

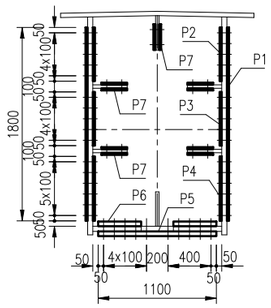

Ⅰ－Ⅰ

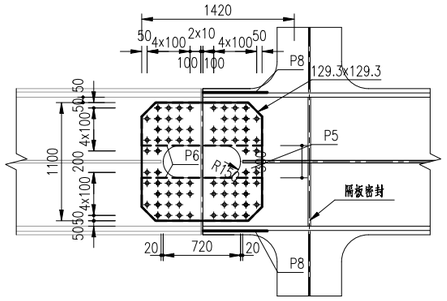

上弦杆顶板、腹板加劲肋拼接

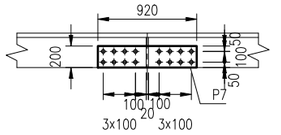

大样C（节段18~节段19）

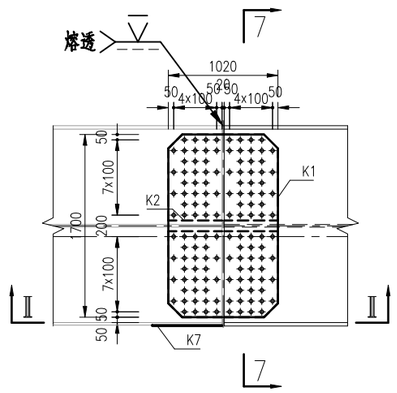

7-7

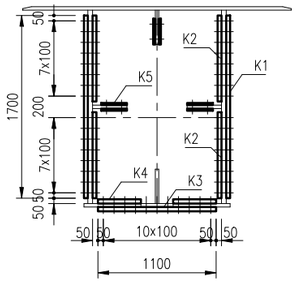

Ⅳ－Ⅳ

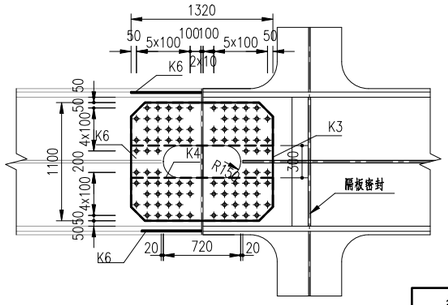

下弦杆顶板、腹板加劲肋拼接

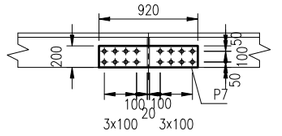

大样B（节段18~节段19）

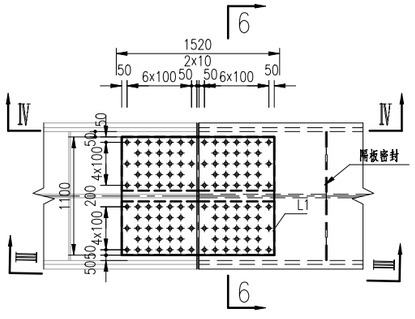

6-6

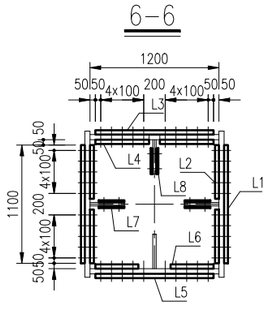

腹杆腹板加劲肋拼接

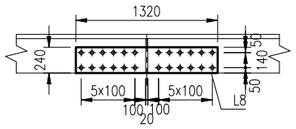

腹杆顶加劲肋拼接

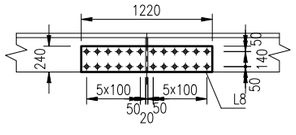

Ⅲ－Ⅲ

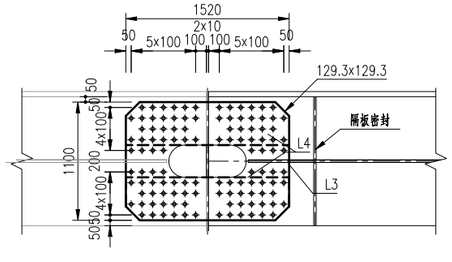

Ⅳ－Ⅳ

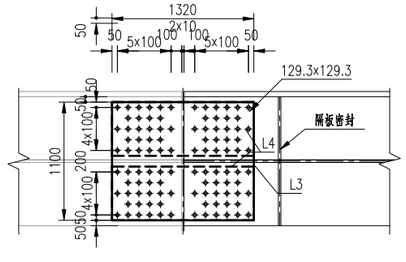

注：

1、本图尺寸均以mm计。

2、未注明的板件裁切边距M30螺栓不小50mm，M24螺栓不小40mm。

3、图中未注明的过焊孔圆弧切角半径为35mm。

4、图中未注明焊缝详见《钢梁焊缝及细节设计图》。

符号：

⊕ —— M30螺栓，开孔直径33mm

⊗ —— M24螺栓，开孔直径26mm

节段18~节段19拼接数量表

名称	编号	材质	规格	数量	单件重	共重（kg）	备注
上弦杆拼接	P1	Q355D	□1220×1800×28	2	483.6	967.2	
	P2		□1220×500×28	2	134.1	268.2	
	P3		□1220×500×28	2	134.1	268.2	
	P4		□1220×600×28	2	160.5	321	
	P5		□1420×1100×32	1	391.9	391.9	
	P6		□1420×400×32	2	143.2	286.4	
	P7		□920×200×20	10	28.3	283	
	P8		□600×1800×16	2	135.6	271.2	填板
	P9		□700×1100×16	1	96.7	96.7	填板
	M30高强螺栓	10.9S	M30x200	508	1.94	985.5	
下弦杆拼接	K1	Q355D	□1020×1700×24	2	325.9	651.8	
	K2		□1020×800×24	4	154.5	618	
	K3		□1320×1100×36	1	409.8	409.8	
	K4		□1320×400×36	2	149.8	299.6	
	K5		□920×200×20	6	28.3	169.8	
	K6		□500×1700×8	2	53.4	106.8	填板
	K7		□650×1100×4	1	22.6	22.6	填板
	M30高强螺栓	10.9S	M30x200	324	1.94	628.6	
腹杆拼接	L1	Q355D	□1520×1100×24	2	314.6	629.2	
	L2		□1520×500×24	4	143.2	572.8	
	L3		□1320×1100×28	1	318.7	318.7	
	L4		□1320×500×28	2	145.1	290.2	
	L5		□1520×1100×44	1	576.8	576.8	
	L6		□1520×240×44	2	124.3	248.6	
	L7		□1220×240×24	4	54.6	218.4	
	L8		□1320×240×24	2	60.3	120.6	
	M30高强螺栓	10.9S	M30x200	540	1.94	1047.6	

中交第二公路勘察设计研究院有限公司	狮子洋通道工程勘察设计 施 工 图 设 计	K6+418.3 新沙高架桥 中桥节段19设计图	设计	余汪千	复核	袁勤	一审	张华	二审	李忠	图号	SZYS/04/02/02/01/ 27

节段19材料数量表

名称	编号	材质	规格	数量	单件重	共重（kg）	备注
上弦顶板	N11a	Q355D	t=20mm,A=15.28m2	1	2399.7	2399.7	
	N11b	Q355D	t=24mm,A=13.73m2	1	2586.7	2586.7	
上弦底板	N12a	Q355D	□7900×1200×20	1	1488.4	1488.4	
	N12b	Q355D	□7100×1200×24	1	1605.2	1605.2	
上弦节点板	N13	Q355D	t=40mm,A=23.45m2	2	7363.3	14726.6	
上弦腹板	N14	Q355D	□7300×2048×32	2	3755.4	7510.8	
上弦横隔板	N15	Q355D	□1980×1200×16	3	298.9	896.7	
	N15a	Q355D	□1976×1200×16	2	297.7	595.4	
	N15‘	Q355D	□2057×200×16	3	51.5	154.5	
	N15b	Q355B	□2057×40×4	4	2.5	10	
	N15c	Q355D	□800×400×16	4	40.2	160.8	
上弦加劲肋	N16a	Q355D	□7900×240×20	6	298.3	1789.8	
	N16b	Q355D	□7100×320×32	6	570.2	3421.2	
下弦顶板	N21a	Q355D	□7900×2500×20	1	3100.8	3100.8	
	N21b	Q355D	□7100×2500×20	1	2786.8	2786.8	
下弦底板	N22a	Q355D	t=20mm,A=12.96m2	1	2034.2	2034.2	
	N22b	Q355D	t=20mm,A=11.13m2	1	1747.6	1747.6	
下弦节点板	N23	Q355D	t=40mm,A=22.49m2	2	7061.9	14123.8	Z35钢
下弦腹板	N24	Q355D	□7300×1880×24	2	2584.8	5169.6	
下弦横隔板	N25	Q355D	□1800×1200×16	3	271.3	813.9	
	N25a	Q355D	□1800×1200×16	2	271.3	542.6	
	N25’	Q355D	□2057×200×16	5	51.5	257.5	
下弦加劲肋	N26a	Q355D	□7900×320×32	4	635.5	2542	
	N26b	Q355D	□7100×240×20	4	266.9	1067.6	
	N26c	Q355D	□15000×170×14	2	280.2	560.4	
斜腹杆	N31	Q355D	□10818×1200×36	1	3668.1	3668.1	
	N31a	Q355D	□11018×1200×36	1	3736	3736	
	N32	Q355D	□7218×1360×36	2	2775.1	5550.2	
	N33	Q355D	□7218×320×32	2	580.3	1160.6	
	N33a	Q355D	□9418×320×32	1	756.1	756.1	
	N33b	Q355D	□9618×320×32	1	773.7	773.7	
	N34	Q355D	□1200×1200×16	3	180.9	542.7	
	N41	Q355D	□3640×900×36	2	926.9	1853.8	
	N42	Q355D	□5940×1200×32	1	1791.1	1791.1	
	N43	Q355D	□5240×240×24	2	237.4	474.8	
节点板加劲	N51	Q355D	□5829×1200×36	1	1975.4	1975.4	
	N51a	Q355D	□5429×1200×36	1	1839.7	1839.7	
	N52	Q355D	□3629×1360×36	2	1396	2792	
	N53	Q355D	□3629×320×32	2	291.4	582.8	
	N53a	Q355D	□5129×320×32	1	412	412	
	N53b	Q355D	□4729×320×32	1	379.3	379.3	
	N54	Q355D	□1200×1200×16	3	180.9	542.7	
	N55	Q355D	□2300×320×32	2	185.9	371.8	
	N56	Q355D	□2200×320×32	4	175.8	703.2	
横梁接头	N61	Q355D	□1980×610×14	6	133	798	
	N61a	Q355D	□1976×618×14	4	134.1	536.4	
	N62	Q355D	t=24mm,A=0.47m2	6	89.3	535.8	
	N62a	Q355D	t=24mm,A=0.48m2	4	90.4	361.6	
	N63	Q355D	□1800×610×14	6	120.9	725.4	
	N63a	Q355D	□1800×626×14	4	124.2	496.8	
小计						105452.6	
焊缝重1.5%						1582.0	
合计						107034.6	

节段19材料数量汇总表

规格（mm）	材质	单个合计	全桥共1个
t=40	Q355D	28850.4	28850.4
t=36		21415.2	21415.2
t=32		20404.6	20404.6
t=24		10733.7	10733.7
t=20		16414.9	16414.9
t=16		4506.8	4506.8
t=14		3117	3117
t=4		10	10
焊缝重（1.5%）		1581.8	1581.8
合计	Q355D	107034.4	107034.4
内表面涂装（m²）		426.4	426.4
外表面涂装（m²）		523.5	523.5

节段18~节段19拼接数量汇总表

规格（mm）	材质	单个合计	全桥共1个
t=44	Q355D	825.4	825.4
t=36		709.4	709.4
t=32		678.3	678.3
t=28		2433.5	2433.5
t=24		2810.8	2810.8
t=20		452.8	452.8
t=16		367.9	367.9
t=8		106.8	106.8
t=4		22.6	22.6
合计		8407.5	8407.5
M30x200	10.9S高强螺栓	2661.7	2661.7
外表面涂装（m²）		41.8	41.8

中交第二公路勘察设计研究院有限公司	狮子洋通道工程勘察设计 施 工 图 设 计	K6+418.3 新沙高架桥 中桥节段19设计图	设计	余旺千	复核	袁勤	一审	沈华	二审	王忠	图号	SZYS/04/02/02/01/ 27

大样A（节段19~节段20）

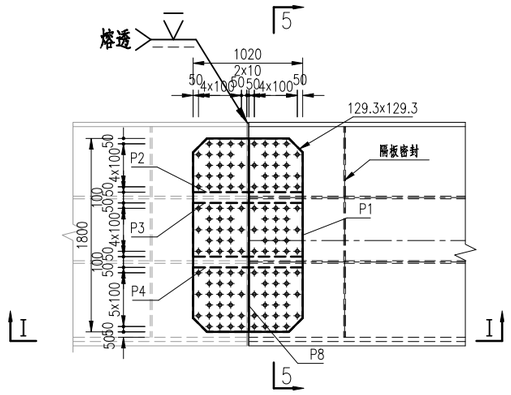

5-5

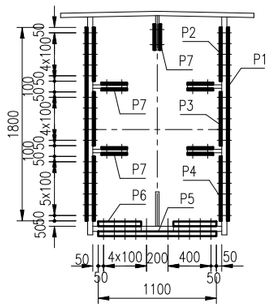

Ⅰ－Ⅰ

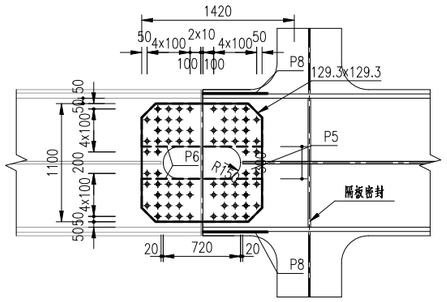

上弦杆顶板、腹板加劲肋拼接

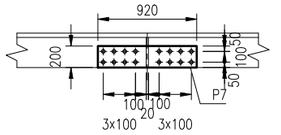

大样C（节段19~节段20）

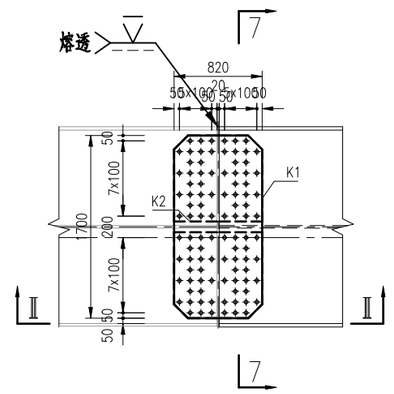

7-7

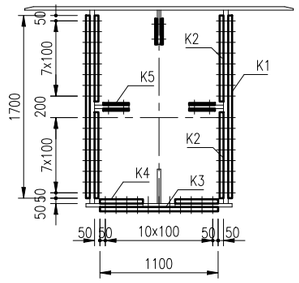

Ⅳ－Ⅳ

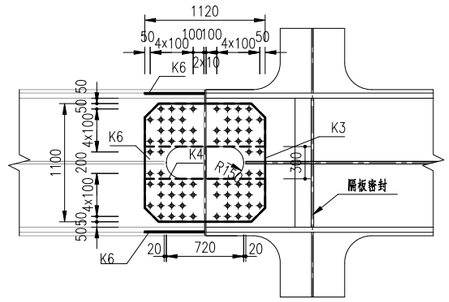

下弦杆顶板、腹板加劲肋拼接

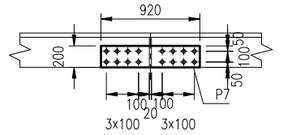

注：

1、本图尺寸均以mm计。

2、未注明的板件裁切边距M30螺栓不小50mm，M24螺栓不小40mm。

3、图中未注明的过焊孔圆弧切角半径为35mm。

4、图中未注明焊缝详见《钢梁焊缝及细节设计图》。

符号：

⊕ —— M30螺栓，开孔直径33mm

⊗ —— M24螺栓，开孔直径26mm

大样B（节段19~节段20）

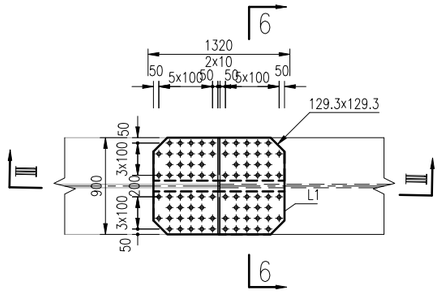

6-6

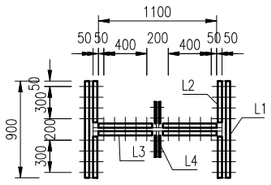

腹杆腹板加劲肋拼接

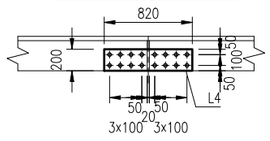

Ⅱ－Ⅱ

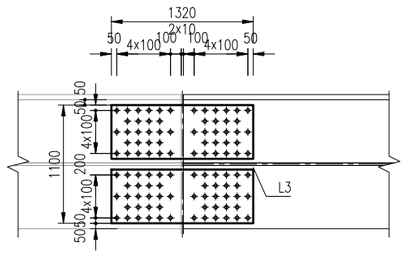

节段19~节段20拼接数量表

名称	编号	材质	规格	数量	单件重	共重（kg）	备注
上弦杆拼接	P1	Q355D	□1020×1800×16	2	231.1	462.2	
	P2		□1020×500×16	2	64.1	128.2	
	P3		□1020×500×16	2	64.1	128.2	
	P4		□1020×600×16	2	76.6	153.2	
	P5		□1420×1100×28	1	342.9	342.9	
	P6		□1420×400×28	2	125.3	250.6	
	P7		□920×200×20	10	28.3	283	
	P8		□600×1800×20	2	169.6	339.2	
	M30高强螺栓	10.9S	M30x200	508	1.94	985.5	
下弦杆拼接	K1	Q355D	□820×1700×20	2	218.2	436.4	
	K2		□820×800×20	4	103.6	414.4	
	K3		□1120×1100×32	1	309	309	
	K4		□1120×400×32	2	113	226	
	K5		□920×200×20	6	28.3	169.8	
	K6		□400×1700×20	2	106.8	213.6	
	M30高强螺栓	10.9S	M30x200	324	1.94	628.6	
腹杆拼接	L1	Q355D	□1320×900×28	2	261.6	523.2	
	L2		□1320×400×28	4	116.5	466	
	L3		□1320×500×28	4	145.1	580.4	
	L4		□820×200×20	4	25.1	100.4	
	M30高强螺栓	10.9S	M30x200	320	1.94	620.8	

中交第二公路勘察设计研究院有限公司	狮子洋通道工程勘察设计 施 工 图 设 计	K6+418.3 新沙高架桥 中桥节段20设计图	设计	余汪千	复核	袁勤	一审	张华	二审	李忠	图号	SZYS/04/02/02/01/ 28

节段20材料数量表

名称	编号	材质	规格	数量	单件重	共重（kg）	备注
上弦顶板	N11a	Q355D	t=20mm,A=15.28m2	1	2399.7	2399.7	
	N11b	Q355D	t=20mm,A=13.73m2	1	2155.5	2155.5	
上弦底板	N12a	Q355D	□7900×1200×20	1	1488.4	1488.4	
	N12b	Q355D	□7100×1200×20	1	1337.6	1337.6	
上弦节点板	N13	Q355D	t=40mm,A=22.3m2	2	7002.2	14004.4	
上弦腹板	N14	Q355D	□7300×2048×20	2	2347.2	4694.4	
上弦横隔板	N15	Q355D	□1980×1200×16	3	298.9	896.7	
	N15a	Q355D	□1980×1200×16	2	298.9	597.8	
	N15‘	Q355D	□2057×200×16	3	51.5	154.5	
	N15b	Q355B	□4113×40×4	4	5	20	
	N15c	Q355D	□800×400×16	4	40.2	160.8	
上弦加劲肋	N16a	Q355D	□7900×240×20	6	298.3	1789.8	
	N16b	Q355D	□7100×240×20	6	266.9	1601.4	
下弦顶板	N21a	Q355D	□7900×2500×20	1	3100.8	3100.8	
	N21b	Q355D	□7100×2500×20	1	2786.8	2786.8	
下弦底板	N22a	Q355D	t=20mm,A=12.96m2	1	2034.2	2034.2	
	N22b	Q355D	t=20mm,A=11.13m2	1	1747.6	1747.6	
下弦节点板	N23	Q355D	t=40mm,A=20.36m2	2	6393	12786	Z35钢
下弦腹板	N24	Q355D	□7300×1880×24	2	2584.8	5169.6	
下弦横隔板	N25	Q355D	□1800×1200×16	3	271.3	813.9	
	N25a	Q355D	□1800×1200×16	2	271.3	542.6	
	N25’	Q355D	□2057×200×16	5	51.5	257.5	
下弦加劲肋	N26a	Q355D	□7900×240×20	4	298.3	1193.2	
	N26b	Q355D	□7100×240×20	4	266.9	1067.6	
	N26c	Q355D	□15000×170×14	2	280.2	560.4	
斜腹杆	N31	Q355D	□7227×900×36	2	1836.9	3673.8	
	N32	Q355D	□11727×1200×32	1	3534.4	3534.4	
	N33	Q355D	□10327×240×24	2	467.2	934.4	
	N41	Q355D	□3657×900×36	2	929.8	1859.6	
	N42	Q355D	□5957×1200×32	1	1796.1	1796.1	
	N43	Q355D	□5257×240×24	2	237.4	474.8	
	N51	Q355D	□3640×900×36	2	926.9	1853.8	
	N52	Q355D	□5940×1200×32	1	1791.1	1791.1	
	N53	Q355D	□5240×240×24	2	237.4	474.8	
横梁接头	N61	Q355D	□1980×610×14	6	133	798	
	N61a	Q355D	□1980×630×14	4	137.4	549.6	
	N62	Q355D	t=24mm,A=0.47m2	6	89.3	535.8	
	N62a	Q355D	t=24mm,A=0.48m2	4	90.4	361.6	
	N63	Q355D	□1800×610×14	6	120.9	725.4	
	N63a	Q355D	□1800×626×14	4	124.2	496.8	
小计						83221.2	
焊缝重1.5%						1248.0	
合计						84469.2	

节段20材料数量汇总表

规格（mm）	材质	单个合计	全桥共1个
t=40	Q355D	26790.4	26790.4
t=36		7387.2	7387.2
t=32		7121.6	7121.6
t=24		7951	7951
t=20		27397	27397
t=16		3423.8	3423.8
t=14		3130.2	3130.2
t=4		20	20
焊缝重（1.5%）		1248.3	1248.3
合计	Q355D	84469.5	84469.5
内表面涂装（㎡）		384.8	384.8
外表面涂装（㎡）		441.0	441.0

节段19~节段20拼接数量汇总表

规格（mm）	材质	单个合计	全桥共1个
t=32	Q355D	535	535
t=28		2163.1	2163.1
t=20		1956.8	1956.8
t=16		871.8	871.8
合计		5526.7	5526.7
M30x200	10.9S高强螺栓	2234.9	2234.9
外表面涂装（㎡）		31.4	31.4

中交第二公路勘察设计研究院有限公司	狮子洋通道工程勘察设计 施 工 图 设 计	K6+418.3 新沙高架桥 中桥节段20设计图	设计	余汪千	复核	袁勤	一审	沈华	二审	李忠	图号	SZYS/04/02/02/01/ 28

7 1263012 151117

大样A（节段20~节段21）

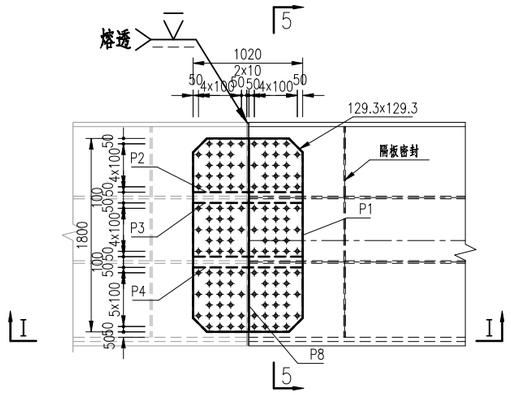

5-5

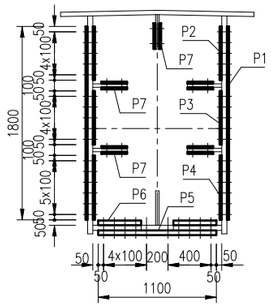

I－I

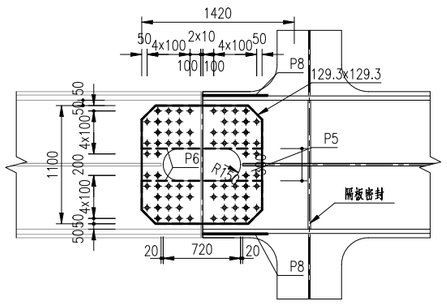

上弦杆顶板、腹板加劲肋拼接

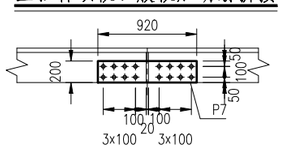

大样C（节段20~节段21）

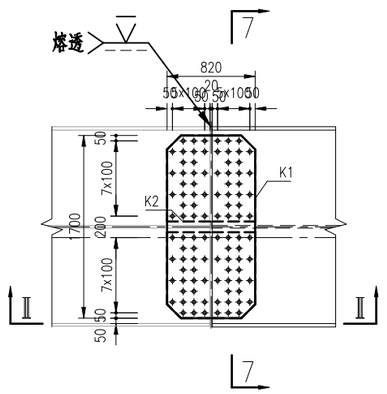

7-7

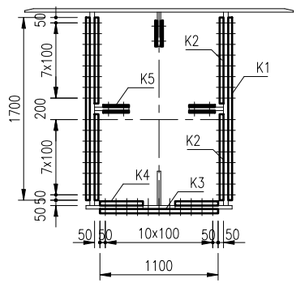

Ⅳ－Ⅳ

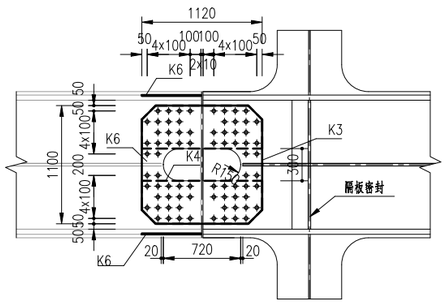

下弦杆顶板、腹板加劲肋拼接

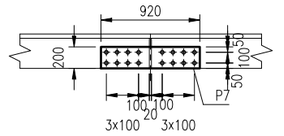

注：

1、本图尺寸均以mm计。

2、未注明的板件裁切边距M30螺栓不小50mm，M24螺栓不小40mm。

3、图中未注明的过焊孔圆弧切角半径为35mm。

4、图中未注明焊缝详见《钢梁焊缝及细节设计图》。

符号：

—— M30螺栓，开孔直径33mm

—— M24螺栓，开孔直径26mm

大样B（节段20~节段21）

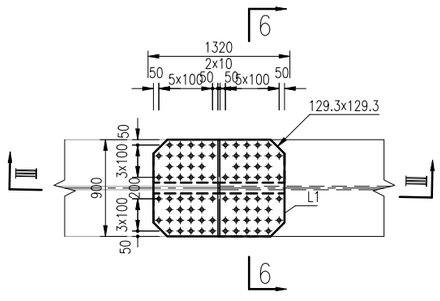

6-6

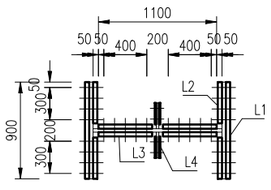

腹杆腹板加劲肋拼接

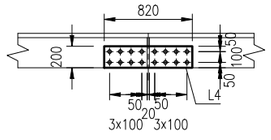

Ⅲ－Ⅲ

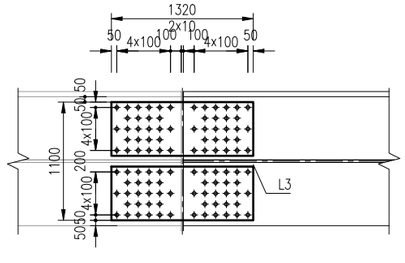

节段20~节段21拼接数量表

名称	编号	材质	规格	数量	单件重	共重（kg）	备注
上弦杆拼接	P1	Q355D	□1020×1800×16	2	231.1	462.2	
	P2		□1020×500×16	2	64.1	128.2	
	P3		□1020×500×16	2	64.1	128.2	
	P4		□1020×600×16	2	76.6	153.2	
	P5		□1420×1100×28	1	342.9	342.9	
	P6		□1420×400×28	2	125.3	250.6	
	P7		□920×200×20	10	28.3	283	
	P8		□600×1800×20	2	169.6	339.2	
	M30高强螺栓	10.9S	M30x200	508	1.94	985.5	
下弦杆拼接	K1	Q355D	□820×1700×20	2	218.2	436.4	
	K2		□820×800×20	4	103.6	414.4	
	K3		□1120×1100×32	1	309	309	
	K4		□1120×400×32	2	113	226	
	K5		□920×200×20	6	28.3	169.8	
	K6		□400×1700×20	2	106.8	213.6	
	M30高强螺栓	10.9S	M30x200	324	1.94	628.6	
腹杆拼接	L1	Q355D	□1320×900×28	2	261.6	523.2	
	L2		□1320×400×28	4	116.5	466	
	L3		□1320×500×28	4	145.1	580.4	
	L4		□820×200×20	4	25.1	100.4	
	M30高强螺栓	10.9S	M30x200	320	1.94	620.8	

中交第二公路勘察设计研究院有限公司	狮子洋通道工程勘察设计 施 工 图 设 计	K6+418.3 新沙高架桥 中桥节段21设计图	设计	余汪千	复核	袁勤	一审	沈雄	二审	李忠	图号	SZYS/04/02/02/01/ 29

72550112733918074

节段21材料数量表

名称	编号	材质	规格	数量	单件重	共重（kg）	备注
上弦顶板	N11a	Q355D	t=20mm,A=15.28m2	1	2399.7	2399.7	
	N11b	Q355D	t=20mm,A=16.43m2	1	2579.4	2579.4	
上弦底板	N12a	Q355D	□7900×1200×20	1	1488.4	1488.4	
	N12b	Q355D	□8600×1200×20	1	1620.2	1620.2	
上弦节点板	N13	Q355D	t=40mm,A=22.28m2	2	6995.9	13991.8	
上弦腹板	N14	Q355D	□8800×2048×20	2	2829.1	5658.2	
上弦横隔板	N15	Q355D	□1980×1200×16	3	298.9	896.7	
	N15a	Q355D	□1980×1200×16	3	298.9	896.7	
	N15‘	Q355D	□2057×200×16	4	51.5	206	
	N15b	Q355B	□2057×40×4	4	2.5	10	
	N15c	Q355D	□800×400×16	4	40.2	160.8	
上弦加劲肋	N16a	Q355D	□7900×240×20	6	298.3	1789.8	
	N16b	Q355D	□8600×240×20	6	323.4	1940.4	
下弦顶板	N21a	Q355D	□7900×2500×20	1	3100.8	3100.8	
	N21b	Q355D	□10100×2500×20	1	3964.3	3964.3	
下弦底板	N22a	Q355D	t=20mm,A=12.96m2	1	2034.2	2034.2	
	N22b	Q355D	t=20mm,A=15.21m2	1	2388.2	2388.2	
下弦节点板	N23	Q355D	t=40mm,A=20.31m2	2	6377.3	12754.6	Z35钢
下弦腹板	N24	Q355D	□10300×1880×24	2	3647.4	7294.8	
下弦横隔板	N25	Q355D	□1800×1200×16	3	271.3	813.9	
	N25a	Q355D	□1800×1200×16	2	271.3	542.6	
	N25’	Q355D	□2057×200×16	3	51.5	154.5	
下弦加劲肋	N26a	Q355D	□7900×240×20	4	298.3	1193.2	
	N26b	Q355D	□10100×240×20	4	379.9	1519.6	
	N26c	Q355D	□18000×170×14	2	336.3	672.6	
斜腹杆	N31	Q355D	□8075×900×36	2	2054.5	4109	
	N32	Q355D	□12575×1200×32	1	3790.6	3790.6	
	N33	Q355D	□11175×240×24	2	504.9	1009.8	
	N41	Q355D	□4104×900×36	2	1042.8	2085.6	
	N42	Q355D	□6404×1200×32	1	1929.2	1929.2	
	N43	Q355D	□5704×240×24	2	258.1	516.2	
	N51	Q355D	□3657×900×36	2	929.8	1859.6	
	N52	Q355D	□5857×1200×32	1	1765.9	1765.9	
	N53	Q355D	□5157×240×24	2	233.6	467.2	
横梁接头	N61	Q355D	□1980×610×14	6	133	798	
	N61a	Q355D	□1980×630×14	6	137.4	824.4	
	N62	Q355D	t=24mm,A=0.47m2	6	89.3	535.8	
	N62a	Q355D	t=24mm,A=0.48m2	6	90.4	542.4	
	N63	Q355D	□1800×610×14	6	120.9	725.4	
	N63a	Q355D	□1800×626×14	4	124.2	496.8	
小计						91527.3	
焊缝重1.5%						1373.0	
合计						92900.3	

节段21材料数量汇总表

规格（mm）	材质	单个合计	全桥共1个
t=40	Q355D	26746.4	26746.4
t=36		8054.2	8054.2
t=32		7485.7	7485.7
t=24		10366.2	10366.2
t=20		31676.4	31676.4
t=16		3671.2	3671.2
t=14		3517.2	3517.2
t=4		10	10
焊缝重（1.5%）		1372.9	1372.9
合计		92900.2	92900.2
内表面涂装（㎡）		361.3	361.3
外表面涂装（㎡）		562.3	562.3

节段20~节段21拼接数量汇总表

规格（mm）	材质	单个合计	全桥共1个
t=32	Q355D	535	535
t=28		2163.1	2163.1
t=20		1956.8	1956.8
t=16		871.8	871.8
合计		5526.7	5526.7
M30x200	10.9S高强螺栓	2234.9	2234.9
外表面涂装（㎡）		31.4	31.4

中交第二公路勘察设计研究院有限公司	狮子洋通道工程勘察设计 施 工 图 设 计	K6+418.3 新沙高架桥 中桥节段21设计图	设计	余汪千	复核	袁勤	一审	沈华	二审	李忠	图号	SZYS/04/02/02/01/ 29

72550112740476

大样A（节段21~节段22）

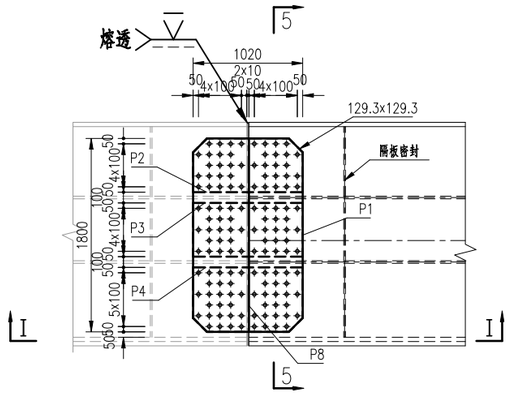

5-5

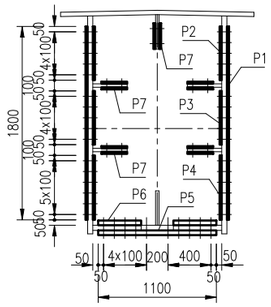

I－I

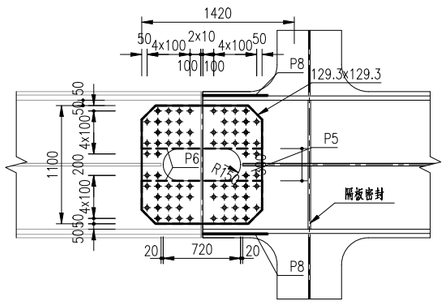

上弦杆顶板、腹板加劲肋拼接

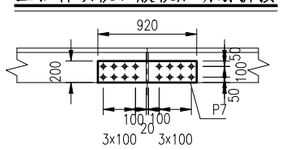

大样C（节段21~节段22）

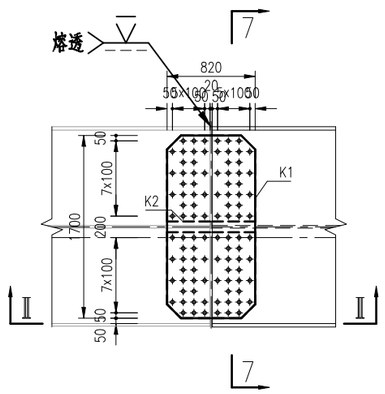

7-7

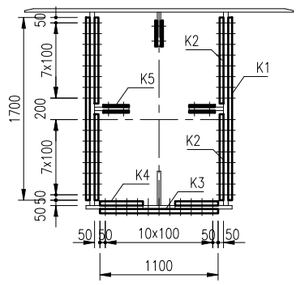

Ⅳ－Ⅳ

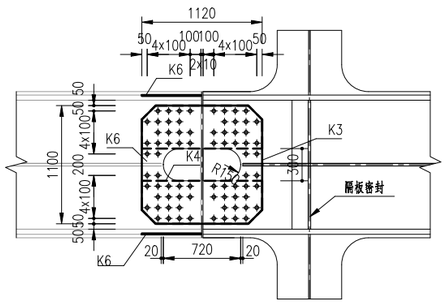

下弦杆顶板、腹板加劲肋拼接

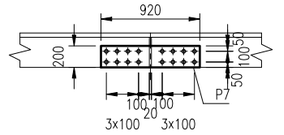

注：

1、本图尺寸均以mm计。

2、未注明的板件裁切边距M30螺栓不小50mm，M24螺栓不小40mm。

3、图中未注明的过焊孔圆弧切角半径为35mm。

4、图中未注明焊缝详见《钢梁焊缝及细节设计图》。

符号：

⊕ —— M30螺栓，开孔直径33mm

⊗ —— M24螺栓，开孔直径26mm

大样B（节段21~节段22）

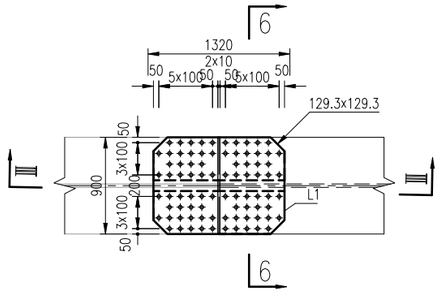

6-6

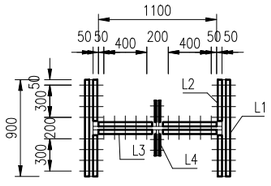

腹杆腹板加劲肋拼接

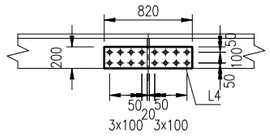

Ⅲ－Ⅲ

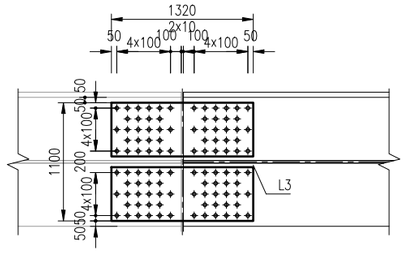

节段21~节段22拼接数量表

名称	编号	材质	规格	数量	单件重	共重（kg）	备注
上弦杆拼接	P1	Q355D	□1020×1800×16	2	231.1	462.2	
	P2		□1020×500×16	2	64.1	128.2	
	P3		□1020×500×16	2	64.1	128.2	
	P4		□1020×600×16	2	76.6	153.2	
	P5		□1420×1100×28	1	342.9	342.9	
	P6		□1420×400×28	2	125.3	250.6	
	P7		□920×200×20	10	28.3	283	
	P8		□600×1800×20	2	169.6	339.2	
	M30高强螺栓	10.9S	M30×200	508	1.94	985.5	
下弦杆拼接	K1	Q355D	□820×1700×20	2	218.2	436.4	
	K2		□820×800×20	4	103.6	414.4	
	K3		□1120×1100×32	1	309	309	
	K4		□1120×400×32	2	113	226	
	K5		□920×200×20	6	28.3	169.8	
	K6		□400×1700×20	2	106.8	213.6	
	M30高强螺栓	10.9S	M30×200	324	1.94	628.6	
腹杆拼接	L1	Q355D	□1320×900×28	2	261.6	523.2	
	L2		□1320×400×28	4	116.5	466	
	L3		□1320×500×28	4	145.1	580.4	
	L4		□820×200×20	4	25.1	100.4	
	M30高强螺栓	10.9S	M30×200	507	1.94	983.6	

节段22材料数量表

名称	编号	材质	规格	数量	单件重	共重（kg）	备注
上弦顶板	N11	Q355D	t=20mm,A=46.82m2	1	7350.7	7350.7	
上弦底板	N12	Q355D	□23690x1200x20	1	4463.5	4463.5	
上弦腹板	N13	Q355D	□10300x1200x20	2	1940.5	3881	
上弦节点板	N14	Q355D	t=28mm,A=13.05m2	2	2868.4	5736.8	
	N14a	Q355D	t=40mm,A=24.91m2	2	7821.7	15643.4	
上弦横隔板	N15	Q355D	□1980x1200x16	9	298.9	2690.1	
	N15‘	Q355D	□2057x200x16	10	51.5	515	
	N15b	Q355B	□2057×40×4	4	2.5	10	
	N15c	Q355D	□800×400×16	4	40.2	160.8	
上弦加劲肋	N16a	Q355D	□5651x320x32	4	454.7	1818.8	
	N16b	Q355D	□10300x240x20	4	387.8	1551.2	
	N16c	Q355D	□7700x320x32	4	618	2472	
	N16d	Q355D	□23640x240x20	1	890.2	890.2	
	N16e	Q355D	□23640x240x20	1	890.2	890.2	
下弦顶板	N21	Q355D	□4809x2500x20	1	1887.1	1887.1	
	N21a	Q355D	□17804x2500x20	1	6988.1	6988.1	
下弦底板	N22	Q355D	t=36mm,A=9.36m2	1	2645.1	2645.1	
	N22a	Q355D	t=20mm,A=28.36m2	1	4452.8	4452.8	
下弦腹板	N23	Q355D	□10103x1880x24	2	3577.7	7155.4	
下弦节点板	N24	Q355D	t=40mm,A=17.54m2	2	5506.3	11012.6	Z35钢
	N24a	Q355D	t=40mm,A=20.07m2	2	6303.2	12606.4	Z35钢
下弦横隔板	N25	Q355D	□1800x1200x16	7	271.3	1899.1	
	N25’	Q355D	□2057x200x16	6	51.5	309	
	N15b	Q355D	□4113x40x4	1	5	5	
下弦加劲肋	N26a	Q355D	□2792x320x32	2	223.6	447.2	
	N26b	Q355D	□10103x240x20	2	379.9	759.8	
	N26c	Q355D	□7700x240x20	2	290.5	581	
	N26d	Q355D	□20592x240x20	2	775.6	1551.2	
	N26e	Q355D	□20592x170x14	2	384.7	769.4	
斜腹杆	N31	Q355D	□11768×1200×36	1	3990.3	3990.3	
	N31a	Q355D	□11968×1200×36	1	4058.1	4058.1	
	N32	Q355D	□7568×1360×36	2	2908	5816	
	N33	Q355D	□7568×320×32	2	607.9	1215.8	
	N33a	Q355D	□10368×320×32	1	834	834	
	N33b	Q355D	□10568×320×32	1	849.1	849.1	
	N34	Q355D	□1200×1200×16	3	180.9	542.7	
	N41	Q355D	□11917×1200×36	1	4041.2	4041.2	
	N41a	Q355D	□11917×1200×36	1	4041.2	4041.2	
	N42	Q355D	□7717×1360×36	2	2967.3	5934.6	
	N43	Q355D	□7717×320×32	2	620.5	1241	
	N43a	Q355D	□11217×320×32	1	901.8	901.8	
	N43b	Q355D	□11217×320×32	1	901.8	901.8	
	N44	Q355D	□1200×1200×16	3	180.9	542.7	
竖腹杆顶底板	N51	Q355D	□11022x1200x20	1	2077.1	2077.1	
	N51a	Q355D	□9422x1200x20	1	1775.7	1775.7	
竖腹杆腹板	N52	Q355D	□6737x1500x20	2	1587.3	3174.6	
竖腹杆横隔板	N54	Q355D	□1400x1200x16	3	211	633	
竖腹杆加劲肋	N53	Q355D	□6737x190x16	2	160.8	321.6	
	N53a	Q355D	□9622x190x16	1	229.8	229.8	
	N53b	Q355D	□8022x190x16	1	190.9	190.9	

名称	编号	材质	规格	数量	单件重	共重（kg）	备注
下弦节点板加劲	N61	Q355D	□2800x320x32	2	226.1	452.2	
	N62	Q355D	□2400x320x32	2	193.4	386.8	
	N63	Q355D	□750x320x28	2	52.8	105.6	
	N64	Q355D	□2300x320x32	2	185.9	371.8	
	N65	Q355D	□2300x320x32	2	185.9	371.8	
	N66	Q355D	□2400x320x32	3	193.4	580.2	
斜腹杆	N67	Q355D	□4322×900×36	2	1099.3	2198.6	
	N68	Q355D	□6522×1200×32	1	1966.9	1966.9	
	N69	Q355D	□5822×240×24	2	263.8	527.6	
横梁接头	N71	Q355D	□1980x610x16	6	152	912	
	N71a	Q355D	□1980x622x16	6	154.5	927	
	N71b	Q355D	□1980x626x16	6	155.7	934.2	
	N72	Q355D	t=24mm,A=0.47m2	12	88.4	1060.8	
	N72’	Q355D	t=24mm,A=0.48m2	2	90.4	180.8	
	N72a	Q355D	t=24mm,A=0.97m2	2	182	364	
	N73	Q355D	□1800x626x16	6	141.9	851.4	
	N73a	Q355D	□1800x610x16	8	138.2	1105.6	
	N73b	Q355D	□1800x610x28	4	241.8	967.2	
支承加劲肋	N81	Q355D	□1800x1200x32	4	542.6	2170.4	
	N82	Q355D	□502x240x20	2	18.8	37.6	
	N83	Q355D	□1800x1800x80	1	2034.7	2034.7	
	N84	Q355D	□1000x568x32	3	143.2	429.6	
	N85	Q355D	□1350x570x32	4	193.4	773.6	
小计						164166.3	
焊缝重1.5%						2462.5	
合计						166628.8	

节段22材料数量汇总表

规格（mm）	材质	单个合计	全桥共1个
t=80	Q355D	2034.7	2034.7
t=40		39262.4	39262.4
t=36		32725.1	32725.1
t=32		18184.8	18184.8
t=28		6809.6	6809.6
t=24		9288.6	9288.6
t=20		42311.8	42311.8
t=16		12764.9	12764.9
t=14		769.4	769.4
t=4		15	15
焊缝重（1.5%）		2462.5	2462.5
合计		166628.8	166628.8
内表面涂装（m²）		709.4	709.4
外表面涂装（m²）		841.3	841.3

节段21~节段22拼接数量汇总表

规格（mm）	材质	单个合计	全桥共1个
t=32	Q355D	535	535
t=28		2163.1	2163.1
t=20		1956.8	1956.8
t=16		871.8	871.8
合计		5526.7	5526.7
M30x200	10.9S高强螺栓	2597.7	2597.7
外表面涂装（m²）		31.4	31.4

中交第二公路勘察设计研究院有限公司	狮子洋通道工程勘察设计 施 工 图 设 计	K6+418.3 新沙高架桥 中桥节段22设计图	设计	余汪千	复核	袁勤	一审	沈华	二审	李忠	图号	SZYS/04/02/02/01/ 30

节段01材料数量表

名称	编号	材质	规格	数量	单件重	共重（kg）	备注
上弦顶板	N11	Q355D	t=20mm,A=20.5m2	1	3218.5	3218.5	
上弦底板	N12	Q355D	□13350x1200x20	1	2515.1	2515.1	
上弦腹板	N13	Q355D	□10350x1648x20	0	2678.4	0	
上弦节点板	N14	Q355D	t=28mm,A=10.77m2	2	2366.1	4732.2	
	N14a	Q355D	t=40mm,A=21.37m2	2	6710.2	13420.4	
上弦横隔板	N15	Q355D	□1580x1200x16	3	238.6	715.8	
	N15a	Q355D	□1580x1200x16	3	238.6	715.8	
	N15 ‘	Q355D	□2057×200×16	4	51.5	206	
	N15b	Q355D	□1782×40×4	4	2.2	8.8	
	N15c	Q355D	□600×400×16	4	30.1	120.4	
上弦加劲肋	N16a	Q355D	□5651x240x20	4	213.5	854	
	N16b	Q355D	□10351x240x20	0	389.4	0	
	N16b	Q355D	□7650x240x20	4	288.9	1155.6	
	N16c	Q355D	□13300x240x20	1	500.8	500.8	
	N16d	Q355D	□13300x240x20	1	500.8	500.8	
下弦顶板	N21	Q355D	□4790x1850x20	1	1391	1391	
	N21a	Q355D	□10105x1850x20	1	2934.3	2934.3	
下弦底板	N22	Q355D	t=36mm,A=9.36m2	1	2645.7	2645.7	
	N22a	Q355D	t=24mm,A=14.57m2	1	2745	2745	
下弦腹板	N23	Q355D	□10105x1530x24	2	2912.7	5825.4	
下弦节点板	N24	Q355D	t=40mm,A=16.42m2	2	5155.9	10311.8	Z35钢
下弦横隔板	N25	Q355D	□1450x1200x16	1	218.5	218.5	
	N25’	Q355D	□2057x200x16	2	51.5	103	
	N25a	Q355D	□1450x1200x16	3	218.5	655.5	
下弦加劲肋	N26a	Q355D	□2792x240x20	2	105.2	210.4	
	N26b	Q355D	□10105x240x20	2	381.5	763	
	N26c	Q355D	□12897x240x20	1	486.7	486.7	
	N26d	Q355D	□10105x240x20	1	381.5	381.5	
	N26d'	Q355D	□2792x320x32	1	223.6	223.6	
	N26e	Q355D	□12897x170x14	1	240.7	240.7	
斜腹杆	N31	Q355D	□14038×1200×36	1	4761.8	4761.8	
	N31a	Q355D	□14338×1200×36	1	4863.5	4863.5	
	N32	Q355D	□9838×1360×36	2	3781.2	7562.4	
	N33	Q355D	□9838×320×32	2	791.3	1582.6	
	N33a	Q355D	□12638×320×32	1	1014.8	1014.8	
	N33b	Q355D	□12938×320×32	1	1040	1040	
	N34	Q355D	□1200×1200×16	4	180.9	723.6	
	N41	Q355D	□6725×1200×36	1	2280.6	2280.6	
	N41a	Q355D	□6925×1200×36	1	2348.4	2348.4	
	N42	Q355D	□4925×1360×36	2	1893.4	3786.8	
	N43	Q355D	□4925×320×32	2	396.9	793.8	
	N43a	Q355D	□6025×320×32	1	484.8	484.8	
	N43b	Q355D	□6225×320×32	1	499.9	499.9	
	N44	Q355D	□1200×1200×16	4	180.9	723.6	
竖腹杆顶底板	N51	Q355D	□13718x1200x20	1	2584.2	2584.2	
	N51a	Q355D	□11818x1200x20	1	2226.3	2226.3	
竖腹杆腹板	N52	Q355D	□9133x1500x20	2	2150.9	4301.8	
竖腹杆横隔板	N54	Q355D	□1400x1200x16	3	211	633	
竖腹杆加劲肋	N53	Q355D	□9133x190x16	2	218.5	437	
	N53a	Q355D	□12318x190x16	1	293.9	293.9	
	N53b	Q355D	□10418x190x16	1	248.7	248.7	

名称	编号	材质	规格	数量	单件重	共重（kg）	备注
节点板加劲	N61	Q355D	□3100x320x32	2	248.7	497.4	
	N62	Q355D	□2900x320x32	2	233.6	467.2	
	N63	Q355D	□750x320x28	2	52.8	105.6	
	N64	Q355D	□2100x320x32	2	168.3	336.6	
	N65	Q355D	□2100x320x32	2	168.3	336.6	
横梁接头	N71	Q355D	□1580x610x16	3	120.6	361.8	
	N71’	Q355D	□1580x630x16	3	125.6	376.8	
	N71a	Q355D	□1580x622x16	3	123.1	369.3	
	N72	Q355D	t=24mm,A=0.47m2	3	88.4	265.2	
	N72’	Q355D	t=24mm,A=0.48m2	3	90.4	271.2	
	N72a	Q355D	t=24mm,A=0.97m2	1	182	182	
	N73	Q355D	□1450x626x16	3	114.3	342.9	
	N73’	Q355D	□1450x610x16	1	110.5	110.5	
	N73a	Q355D	□1450x610x28	4	193.4	773.6	
支承加劲肋	N81	Q355D	□1450x1200x32	4	437.1	1748.4	
	N82	Q355D	□502x240x20	1	18.8	18.8	
	N83	Q355D	□1800x1800x100	1	2543.4	2543.4	
	N84	Q355D	□1000x568x32	3	143.2	429.6	
	N85	Q355D	□1350x570x32	6	193.4	1160.4	
	N86	Q355D	□2200x650x32	1	359.2	359.2	
小计						112048.3	
焊缝重1.5%						1680.7	
合计						113729.0	

节段01材料数量汇总表

规格（mm）	材质	单个合计	全桥共2个
t=100	Q355D	2543.4	5086.8
t=40	Q355D	23732.2	47464.4
t=36	Q355D	28249.2	56498.4
t=32	Q355D	10974.9	21949.8
t=28	Q355D	5611.4	11222.8
t=24	Q355D	9288.8	18577.6
t=20	Q355D	24042.8	48085.6
t=16	Q355D	7356.1	14712.2
t=14	Q355D	240.7	481.4
t=4	Q355D	8.8	17.6
焊缝重（1.5%）		1680.7	3361.4
	Q355D	113729.0	227458.0
内表面涂装（m²）		634.1	1268.2
外表面涂装（m²）		388.9	777.8

大样A（节段1~节段2）

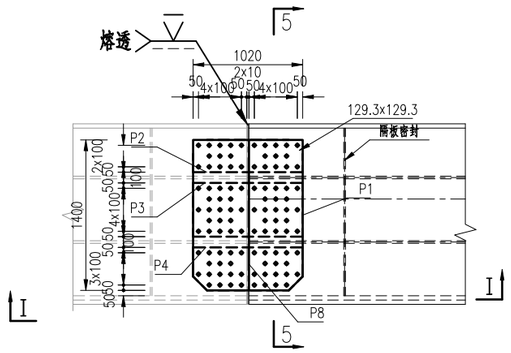

5-5

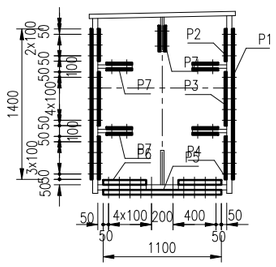

Ⅰ－Ⅰ

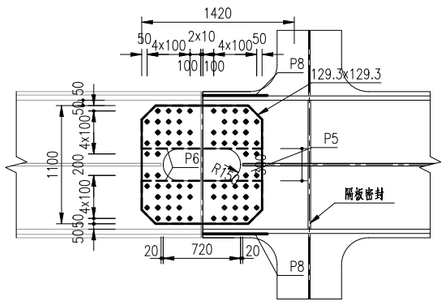

上弦杆顶板、腹板加劲肋拼接

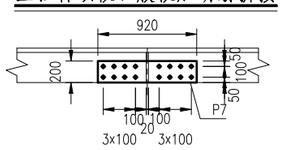

大样C（节段1~节段2）

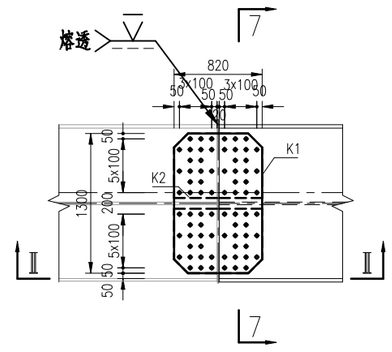

7-7

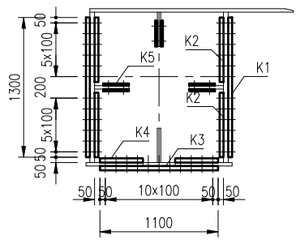

Ⅳ－Ⅳ

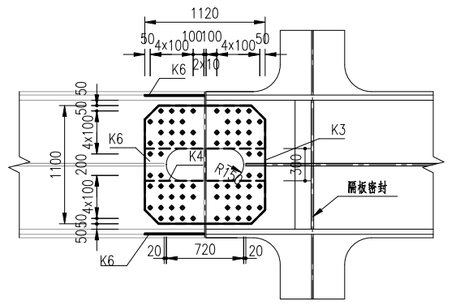

下弦杆顶板、腹板加劲肋拼接

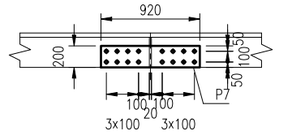

注：

1、本图尺寸均以mm计。

2、未注明的板件裁切边距M30螺栓不小50mm，M24螺栓不小40mm。

3、图中未注明的过焊孔圆弧切角半径为35mm。

4、图中未注明焊缝详见《钢梁焊缝及细节设计图》。

符号：

⊕ —— M30螺栓，开孔直径33mm

⊗ —— M24螺栓，开孔直径26mm

节段1~节段2拼接数量表

名称	编号	材质	规格	数量	单件重	共重（kg）	备注
上弦杆拼接	P1	Q355D	□1020×1400×16	2	179.6	359.2	
	P2		□1020×300×16	2	38.9	77.8	
	P3		□1020×500×16	2	64.1	128.2	
	P4		□1020×400×16	2	51.5	103	
	P5		□1420×1100×28	1	342.9	342.9	
	P6		□1420×400×28	2	125.3	250.6	
	P7		□920×200×20	10	28.3	283	
	P8		□500×1800×20	2	141.3	282.6	填板
	M30高强螺栓	10.9S	M30x200	380	1.94	737.2	
下弦杆拼接	K1	Q355D	□820×1300×20	2	168	336	
	K2		□820×600×20	4	76.9	307.6	
	K3		□1120×1100×32	1	309	309	
	K4		□1120×400×32	2	113	226	
	K5		□920×200×20	6	28.3	169.8	
	K6		□400×1700×16	2	85.4	170.8	填板
	M30高强螺栓	10.9S	M30x200	276	1.94	535.4	
腹杆拼接	L1	Q355D	□1520×1100×24	2	314.6	629.2	
	L2		□1520×500×24	4	143.2	572.8	
	L3		□1320×1100×28	1	318.7	318.7	
	L4		□1320×500×28	2	145.1	290.2	
	L5		□1520×1100×44	1	576.8	576.8	
	L6		□1520×240×44	2	124.3	248.6	
	L7		□1220×240×24	4	54.6	218.4	
	L8		□1320×240×24	2	60.3	120.6	
	M30高强螺栓	10.9S	M30x200	540	1.94	1047.6	

大样B（节段1~节段2）

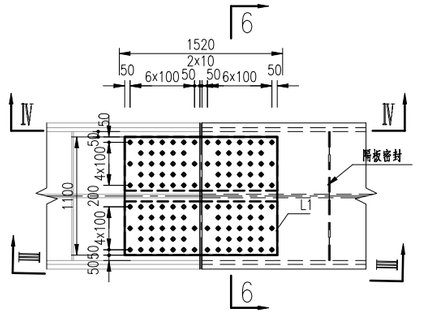

6-6

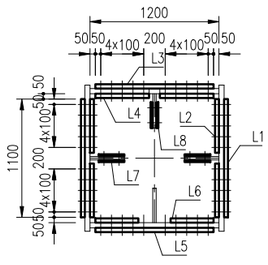

腹杆腹板加劲肋拼接

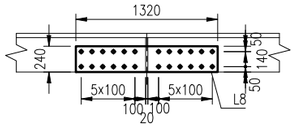

腹杆顶加劲肋拼接

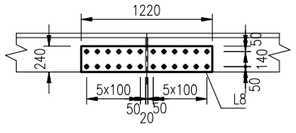

Ⅲ－Ⅲ

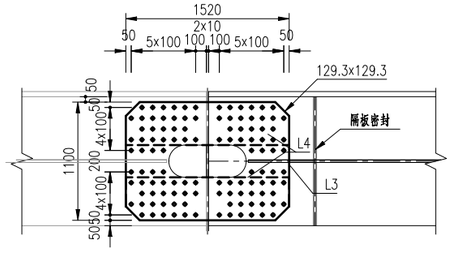

Ⅳ－Ⅳ

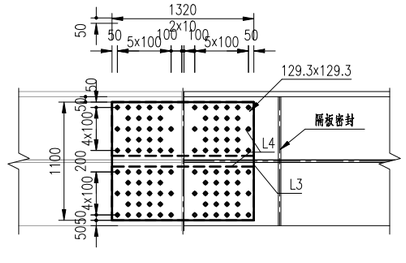

中交第二公路勘察设计研究院有限公司	狮子洋通道工程勘察设计 施 工 图 设 计	K6+418.3 新沙高架桥 边桁节段02设计图	设计	余汪千	复核	袁勤	一审	张华	二审	李忠	图号	SZYS/04/02/02/01/ 32

节段02材料数量表

名称	编号	材质	规格	数量	单件重	共重（kg）	备注
上弦顶板	N11a	Q355D	t=20mm,A=11.85m2	1	1860.5	1860.5	
	N11b	Q355D	t=20mm,A=12.8m2	1	2010	2010	
上弦底板	N12a	Q355D	□7902×1200×20	1	1488.4	1488.4	
	N12b	Q355D	□10150×1200×20	1	1912.3	1912.3	
上弦节点板	N13	Q355D	t=40mm,A=19.24m2	2	6041.5	12083	
上弦腹板	N14	Q355D	□10350×1648×20	2	2678.4	5356.8	
上弦横隔板	N15	Q355D	□1580×1200×16	3	238.6	715.8	
	N15a	Q355D	□1580×1200×16	3	238.6	715.8	
	N15‘	Q355D	□2057×200×16	4	51.5	206	
	N15b	Q355D	□1782×40×4	4	2.2	8.8	
	N15c	Q355D	□600×400×16	4	30.1	120.4	
上弦加劲肋	N16a	Q355D	□7902×240×20	6	298.3	1789.8	
	N16b	Q355D	□10150×240×20	6	383.1	2298.6	
下弦顶板	N21a	Q355D	□7902×1850×20	1	2295.3	2295.3	
	N21b	Q355D	□10105×1850×20	1	2934.3	2934.3	
下弦底板	N22a	Q355D	t=20mm,A=12.53m2	1	1967.3	1967.3	
	N22b	Q355D	t=20mm,A=13.79m2	1	2165.6	2165.6	
下弦节点板	N23	Q355D	t=40mm,A=19.59m2	2	6151.3	12302.6	Z35钢
下弦腹板	N24	Q355D	□10305×1470×24	2	2854.3	5708.6	
下弦横隔板	N25	Q355D	□1450×1200×16	3	218.5	655.5	
	N25a	Q355D	□1450×1200×16	3	218.5	655.5	
	N25’	Q355D	□1657×200×16	4	41.4	165.6	
下弦加劲肋	N26a	Q355D	□7902×240×20	4	298.3	1193.2	
	N26b	Q355D	□10105×240×20	4	381.5	1526	
	N26c	Q355D	□18007×170×14	1	336.3	336.3	
斜腹杆	N31	Q355D	□10047×900×36	2	2554.7	5109.4	
	N32	Q355D	□14947×1200×32	1	4506.5	4506.5	
	N33	Q355D	□13547×240×24	2	612.3	1224.6	
	N41	Q355D	□4796×900×36	2	1220.8	2441.6	
	N42	Q355D	□7096×1200×32	1	2140.2	2140.2	
	N43	Q355D	□6396×240×24	2	290.1	580.2	
	N51	Q355D	□7925×1200×36	1	2687.5	2687.5	
	N51a	Q355D	□7125×1200×36	1	2416.2	2416.2	
	N52	Q355D	□4925×1360×36	2	1893.4	3786.8	
节点板加劲	N53	Q355D	□4925×320×32	2	396.9	793.8	
	N53a	Q355D	□7225×320×32	1	580.3	580.3	
	N53b	Q355D	□6425×320×32	1	517.5	517.5	
	N54	Q355D	□1200×1200×16	2	180.9	361.8	
	N55	Q355D	□991×1200×20	1	186.8	186.8	
	N56	Q355D	□2600×320×32	2	208.5	417	
横梁接头	N61	Q355D	□1580×610×14	3	105.5	316.5	
	N61a	Q355D	□1580×630×14	3	109.9	329.7	
	N62	Q355D	t=24mm,A=0.47m2	3	87.8	263.4	
	N62a	Q355D	t=24mm,A=0.48m2	3	90.4	271.2	
	N63	Q355D	□1450×610×14	3	96.7	290.1	
	N63a	Q355D	□1450×626×14	3	100	300	
小计						91993.1	
焊缝重1.5%						1379.9	
合计						93373.0	

节段02材料数量汇总表

规格（mm）	材质	单个合计	全桥共2个
t=40	Q355D	24385.6	48771.2
t=36	Q355D	16441.5	32883
t=32	Q355D	8955.3	17910.6
t=24	Q355D	8048	16096
t=20	Q355D	28984.9	57969.8
t=16	Q355D	3596.4	7192.8
t=14	Q355D	1572.6	3145.2
t=4	Q355D	8.8	17.6
焊缝重（1.5%）		1379.9	2759.793
	Q355D	93373.0	186745.993
内表面涂装（㎡）		272.2	544.4
外表面涂装（㎡）		611.9	1223.8

节段1~节段2拼接数量汇总表

规格（mm）	材质	单个合计	全桥共2个
t=44	Q355D	825.4	1650.8
t=32	Q355D	535	1070
t=28	Q355D	1202.4	2404.8
t=24	Q355D	1541	3082
t=20	Q355D	1379	2758
t=16	Q355D	839	1678
合计	Q355D	6321.8	12643.6
M30x200	10.9S高强螺栓	2320.2	4640.4
外表面涂装（㎡）		33.6	67.26

中交第二公路勘察设计研究院有限公司	狮子洋通道工程勘察设计 施 工 图 设 计	K6+418.3 新沙高架桥 边桁节段02设计图	设计	余汪千	复核	袁勤	一审	沈华	二审	李忠	图号	SZYS/04/02/02/01/ 32

大样A（节段2~节段3）

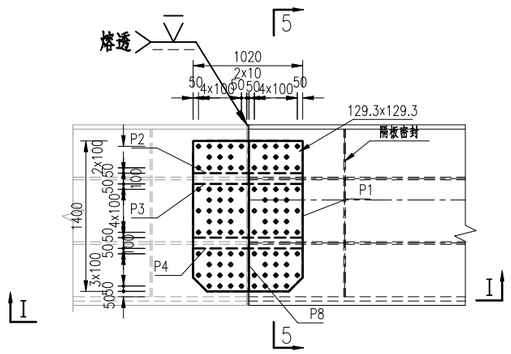

5-5

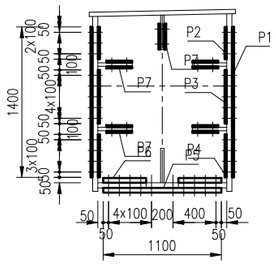

Ⅰ-Ⅰ

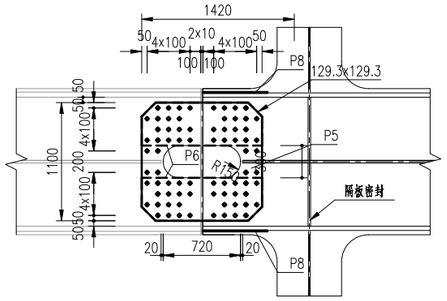

上弦杆顶板、腹板加劲肋拼接

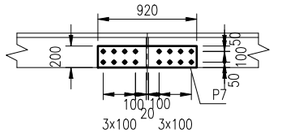

大样C（节段2~节段3）

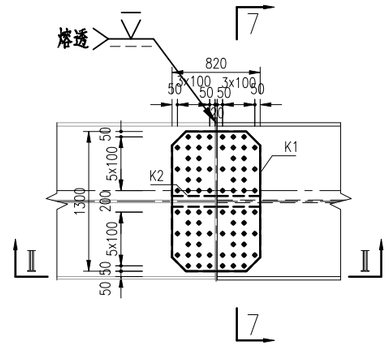

7-7

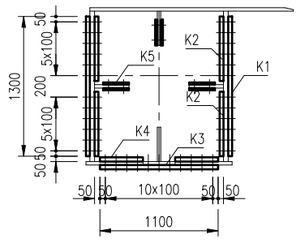

Ⅳ-Ⅳ

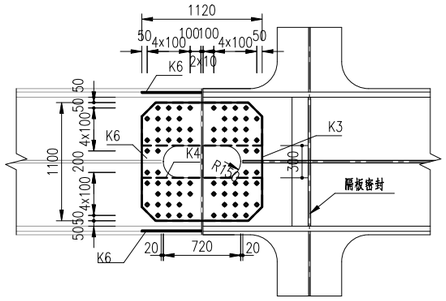

下弦杆顶板、腹板加劲肋拼接

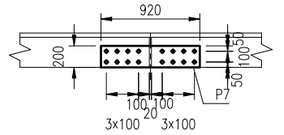

注：

1、本图尺寸均以mm计。

2、未注明的板件裁切边距M30螺栓不小50mm，M24螺栓不小40mm。

3、图中未注明的过焊孔圆弧切角半径为35mm。

4、图中未注明焊缝详见《钢梁焊缝及细节设计图》。

符号：

⊕ —— M30螺栓，开孔直径33mm

⊗ —— M24螺栓，开孔直径26mm

大样B（节段2~节段3）

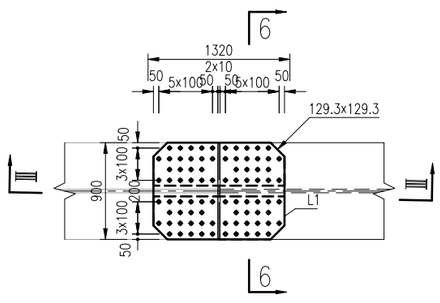

6-6

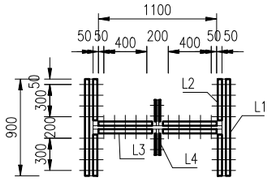

腹杆腹板加劲肋拼接

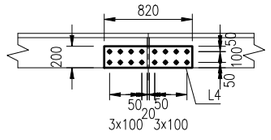

Ⅲ-Ⅲ

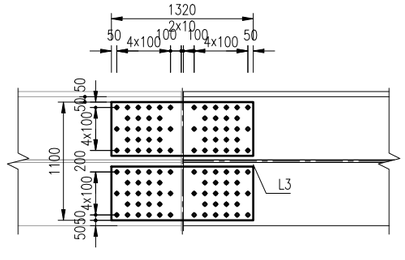

节段2~节段3拼接数量表

名称	编号	材质	规格	数量	单件重	共重（kg）	备注
上弦杆拼接	P1	Q355D	□1020×1400×16	2	179.6	359.2	
	P2		□1020×300×16	2	38.9	77.8	
	P3		□1020×500×16	2	64.1	128.2	
	P4		□1020×400×16	2	51.5	103	
	P5		□1420×1100×28	1	342.9	342.9	
	P6		□1420×400×28	2	125.3	250.6	
	P7		□920×200×20	10	28.3	283	
	P8		□500×1800×20	2	141.3	282.6	
	M30高强螺栓	10.9S	M30x200	380	1.94	737.2	
下弦杆拼接	K1	Q355D	□820×1300×20	2	168	336	
	K2		□820×600×20	4	76.9	307.6	
	K3		□1120×1100×32	1	309	309	
	K4		□1120×400×32	2	113	226	
	K5		□920×200×20	6	28.3	169.8	
	K6		□400×1700×16	2	85.4	170.8	
	M30高强螺栓	10.9S	M30x200	276	1.94	535.4	
腹杆拼接	L1	Q355D	□1320×900×28	2	261.6	523.2	
	L2		□1320×400×28	4	116.5	466	
	L3		□1320×500×28	4	145.1	580.4	
	L4		□820×200×20	4	25.1	100.4	
	M30高强螺栓	10.9S	M30x200	507	1.94	983.6	

中交第二公路勘察设计研究院有限公司	狮子洋通道工程勘察设计 施 工 图 设 计	K6+418.3 新沙高架桥 边桁节段03设计图	设计	余汪千	复核	袁勤	一审	张华	二审	李忠	图号	SZYS/04/02/02/01/ 33

节段03材料数量表

名称	编号	材质	规格	数量	单件重	共重（kg）	备注
上弦顶板	N11a	Q355D	t=20mm,A=11.85m2	1	1860.5	1860.5	
	N11b	Q355D	t=20mm,A=10.39m2	1	1631.8	1631.8	
上弦底板	N12a	Q355D	□7902×1200×20	1	1488.4	1488.4	
	N12b	Q355D	□8600×1200×20	1	1620.2	1620.2	
上弦节点板	N13	Q355D	t=40mm,A=19.34m2	2	6071.6	12143.2	
上弦腹板	N14	Q355D	□8800×1648×20	2	2276.5	4553	
上弦横隔板	N15	Q355D	□1580×1200×16	3	238.6	715.8	
	N15a	Q355D	□1580×1200×16	3	238.6	715.8	
	N15 ‘	Q355D	□2057×200×16	4	51.5	206	
	N15b	Q355D	□1782×40×4	4	2.2	8.8	
	N15c	Q355D	□600×400×16	4	30.1	120.4	
上弦加劲肋	N16a	Q355D	□7902×240×20	6	298.3	1789.8	
	N16b	Q355D	□8600×240×20	6	323.4	1940.4	
下弦顶板	N21a	Q355D	□7904×1850×20	1	2295.3	2295.3	
	N21b	Q355D	□7102×1850×20	1	2063	2063	
下弦底板	N22a	Q355D	t=20mm,A=12.53m2	1	1967.3	1967.3	
	N22b	Q355D	t=20mm,A=9.71m2	1	1525.1	1525.1	
下弦节点板	N23	Q355D	t=40mm,A=18.4m2	2	5776.6	11553.2	Z35钢
下弦腹板	N24	Q355D	□7302×1470×24	2	2021.5	4043	
下弦横隔板	N25	Q355D	□1450×1200×16	3	218.5	655.5	
	N25a	Q355D	□1450×1200×16	2	218.5	437	
	N25’	Q355D	□1657×200×16	3	41.4	124.2	
下弦加劲肋	N26a	Q355D	□7904×240×20	4	298.3	1193.2	
	N26b	Q355D	□7102×240×20	4	266.9	1067.6	
	N26c	Q355D	□15006×170×14	1	280.2	280.2	
斜腹杆	N31	Q355D	□9010×900×36	2	2291.9	4583.8	
	N32	Q355D	□14010×1200×32	1	4222.7	4222.7	
	N33	Q355D	□12610×240×24	2	570.9	1141.8	
	N41	Q355D	□4322×900×36	2	1099.3	2198.6	
	N42	Q355D	□6722×1200×32	1	2027.2	2027.2	
	N43	Q355D	□6022×240×24	2	273.2	546.4	
	N51	Q355D	□4796×900×36	2	1220.8	2441.6	
	N52	Q355D	□7396×1200×32	1	2230.7	2230.7	
	N53	Q355D	□6696×240×24	2	303.3	606.6	
	N54	Q355D	□1170×1200×20	1	219.8	219.8	
	N55	Q355D	□1132×1200×20	1	213.5	213.5	
横梁接头	N61	Q355D	□1580×610×14	3	105.5	316.5	
	N61a	Q355D	□1580×630×14	3	109.9	329.7	
	N62	Q355D	t=24mm,A=0.47m2	3	87.8	263.4	
	N62a	Q355D	t=24mm,A=0.48m2	3	90.4	271.2	
	N63	Q355D	□1450×610×14	3	96.7	290.1	
	N63a	Q355D	□1450×626×14	2	100	200	
小计						78102.3	
焊缝重1.5%						1171.5	
合计						79273.8	

节段03材料数量汇总表

规格（mm）	材质	单个合计	全桥共2个
t=40	Q355D	23696.4	47392.8
t=36	Q355D	9224	18448.0
t=32	Q355D	8480.6	16961.2
t=24	Q355D	6872.4	13744.8
t=20	Q355D	25428.9	50857.8
t=16	Q355D	2974.7	5949.4
t=14	Q355D	1416.5	2833.0
t=4	Q355D	8.8	17.6
焊缝重（1.5%）		1171.5	2343.1
	Q355D	79273.8	158547.7
内表面涂装（m²）		231.2	462.4
外表面涂装（m²）		523.2	1046.4

节段2~节段3拼接数量汇总表

规格（mm）	材质	单个合计	全桥共2个
t=32	Q355D	535	1070
t=28	Q355D	2163.1	4326.2
t=20	Q355D	1479.4	2958.8
t=16	Q355D	839	1678
合计	Q355D	5016.5	10033
M30x200	10.9S高强螺栓	2256.2	4512.4
外表面涂装（m²）		28.1	56.14

中交第二公路勘察设计研究院有限公司	狮子洋通道工程勘察设计 施 工 图 设 计	K6+418.3 新沙高架桥 边桁节段03设计图	设计	余汪千	复核	袁勤	一审	沈华	二审	李忠	图号	SZYS/04/02/02/01/ 33

大样A（节段3~节段4）

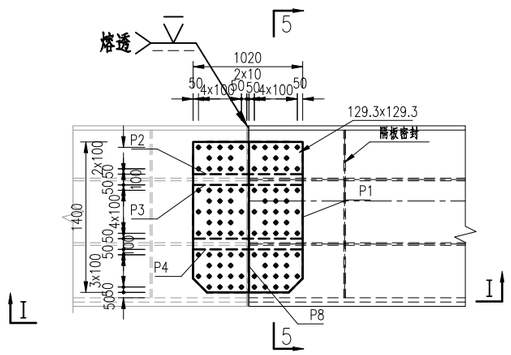

5-5

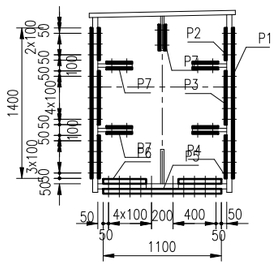

Ⅰ－Ⅰ

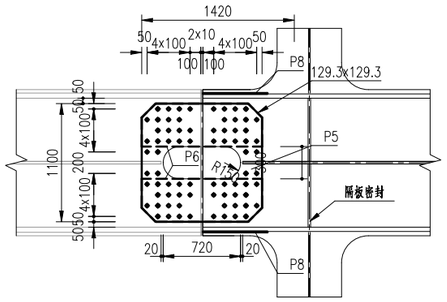

上弦杆顶板、腹板加劲肋拼接

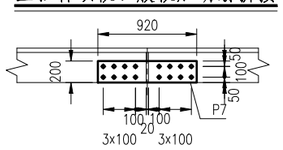

大样C（节段3~节段4）

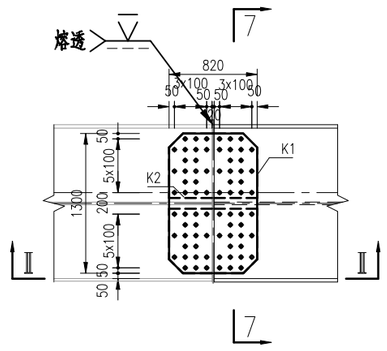

7-7

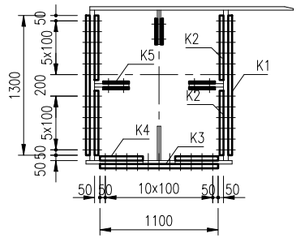

Ⅳ－Ⅳ

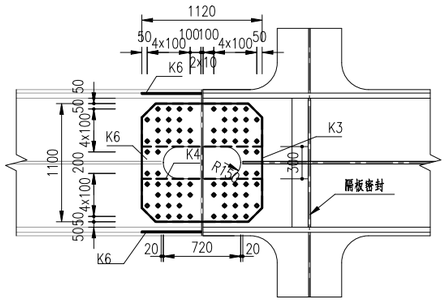

下弦杆顶板、腹板加劲肋拼接

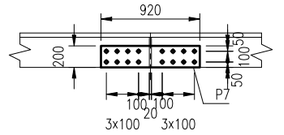

大样B（节段3~节段4）

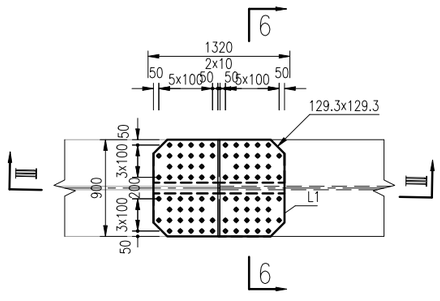

6-6

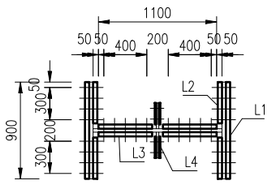

腹杆腹板加劲肋拼接

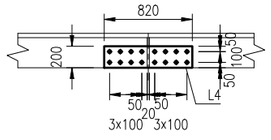

Ⅲ－Ⅲ

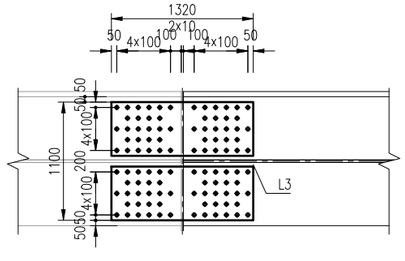

注：

1、本图尺寸均以mm计。

2、未注明的板件裁切边距M30螺栓不小50mm，M24螺栓不小40mm。

3、图中未注明的过焊孔圆弧切角半径为35mm。

4、图中未注明焊缝详见《钢梁焊缝及细节设计图》。

符号：

⊕ —— M30螺栓，开孔直径33mm

⊗ —— M24螺栓，开孔直径26mm

节段3~节段4拼接数量表

名称	编号	材质	规格	数量	单件重	共重（kg）	备注
上弦杆拼接	P1	Q355D	□1020×1400×16	2	179.6	359.2	
	P2		□1020×300×16	2	38.9	77.8	
	P3		□1020×500×16	2	64.1	128.2	
	P4		□1020×400×16	2	51.5	103	
	P5		□1420×1100×28	1	342.9	342.9	
	P6		□1420×400×28	2	125.3	250.6	
	P7		□920×200×20	10	28.3	283	
	P8		□500×1800×20	2	141.3	282.6	
	M30高强螺栓	10.9S	M30x200	380	1.94	737.2	
下弦杆拼接	K1	Q355D	□820×1300×20	2	168	336	
	K2		□820×600×20	4	76.9	307.6	
	K3		□1120×1100×32	1	309	309	
	K4		□1120×400×32	2	113	226	
	K5		□920×200×20	6	28.3	169.8	
	K6		□400×1700×16	2	85.4	170.8	
	M30高强螺栓	10.9S	M30x200	276	1.94	535.4	
腹杆拼接	L1	Q355D	□1320×900×28	2	261.6	523.2	
	L2		□1320×400×28	4	116.5	466	
	L3		□1320×500×28	4	145.1	580.4	
	L4		□820×200×20	4	25.1	100.4	
	M30高强螺栓	10.9S	M30x200	507	1.94	983.6	

中交第二公路勘察设计研究院有限公司	狮子洋通道工程勘察设计 施 工 图 设 计	K6+418.3 新沙高架桥 边桁节段04设计图	设计	余汪千	复核	袁勤	一审	沈雁	二审	李忠	图号	SZYS/04/02/02/01/ 34

2250013185293

节段04材料数量表

名称	编号	材质	规格	数量	单件重	共重（kg）	备注
上弦顶板	N11a	Q355D	t=20mm,A=11.85m2	1	1860.5	1860.5	
	N11b	Q355D	t=20mm,A=10.39m2	1	1631.8	1631.8	
上弦底板	N12a	Q355D	□7901×1200×20	1	1488.4	1488.4	
	N12b	Q355D	□7101×1200×20	1	1337.6	1337.6	
上弦节点板	N13	Q355D	t=40mm,A=20.42m2	2	6412.2	12824.4	
上弦腹板	N14	Q355D	□7301×1648×20	2	1888.7	3777.4	
上弦横隔板	N15	Q355D	□1580×1200×16	3	238.6	715.8	
	N15a	Q355D	□1568×1200×16	2	236.1	472.2	
	N15 '	Q355D	□2057×200×16	3	51.5	154.5	
	N15b	Q355D	□1782×40×4	4	2.2	8.8	
	N15c	Q355D	□600×400×16	4	30.1	120.4	
上弦加劲肋	N16a	Q355D	□7901×240×20	6	298.3	1789.8	
	N16b	Q355D	□7101×240×20	6	266.9	1601.4	
下弦顶板	N21a	Q355D	□7903×1850×20	1	2295.3	2295.3	
	N21b	Q355D	□7102×1850×20	1	2063	2063	
下弦底板	N22a	Q355D	t=20mm,A=12.53m2	1	1967.3	1967.3	
	N22b	Q355D	t=20mm,A=9.71m2	1	1525.1	1525.1	
下弦节点板	N23	Q355D	t=40mm,A=18.42m2	2	5784.3	11568.6	Z35钢
下弦腹板	N24	Q355D	□7302×1470×24	2	2021.5	4043	
下弦横隔板	N25	Q355D	□1450×1200×16	3	218.5	655.5	
	N25a	Q355D	□1450×1200×16	2	218.5	437	
	N25'	Q355D	□1657×200×16	3	41.4	124.2	
下弦加劲肋	N26a	Q355D	□7903×240×20	4	298.3	1193.2	
	N26b	Q355D	□7102×240×20	4	266.9	1067.6	
	N26c	Q355D	□15005×170×14	1	280.2	280.2	
斜腹杆	N31	Q355D	□8788×900×36	2	2235.4	4470.8	
	N32	Q355D	□13688×1200×32	1	4127.2	4127.2	
	N33	Q355D	□12288×240×24	2	555.8	1111.6	
	N41	Q355D	□6225×1200×36	1	2111	2111	
	N41a	Q355D	□6225×1200×36	1	2111	2111	
	N42	Q355D	□4225×1360×36	2	1625	3250	
	N43	Q355D	□4225×320×32	2	339.1	678.2	
	N43a	Q355D	□5525×320×32	1	444.6	444.6	
	N43b	Q355D	□5525×320×32	1	444.6	444.6	
	N44	Q355D	□1200×1200×16	2	180.9	361.8	
	N51	Q355D	□4322×900×36	2	1099.3	2198.6	
节点板加劲	N52	Q355D	□6922×1200×32	1	2087.5	2087.5	
	N53	Q355D	□5522×240×24	2	250.6	501.2	
	N54	Q355D	□2300×320×32	2	185.9	371.8	
横梁接头	N61	Q355D	□1580×610×14	3	105.5	316.5	
	N61a	Q355D	□1580×630×14	2	109.9	219.8	
	N62	Q355D	t=24mm,A=0.47m2	3	87.8	263.4	
	N62a	Q355D	t=24mm,A=0.47m2	2	88.8	177.6	
	N63	Q355D	□1450×610×14	3	96.7	290.1	
	N63a	Q355D	□1450×626×14	2	100	200	
小计						80740.3	
焊缝重1.5%						1211.1	
合计						81951.4	

节段04材料数量汇总表

规格（mm）	材质	单个合计	全桥共2个
t=40	Q355D	24393	48786
t=36	Q355D	14141.4	28282.8
t=32	Q355D	8153.9	16307.8
t=24	Q355D	6096.8	12193.6
t=20	Q355D	23598.4	47196.8
t=16	Q355D	3041.4	6082.8
t=14	Q355D	1306.6	2613.2
t=4	Q355D	8.8	17.6
焊缝重（1.5%）		1211.1	2422.209
	Q355D	81951.4	163902.8
内表面涂装（㎡）		296.6	593.2
外表面涂装（㎡）		461.9	923.8

节段3~节段4拼接数量汇总表

规格（mm）	材质	单个合计	全桥共2个
t=32	Q355D	535	1070
t=28	Q355D	2163.1	4326.2
t=20	Q355D	1479.4	2958.8
t=16	Q355D	839	1678
合计	Q355D	5016.5	10033
M30x200	10.9S高强螺栓	2256.2	4512.4
外表面涂装（㎡）		28.1	56.14

中交第二公路勘察设计研究院有限公司	狮子洋通道工程勘察设计 施 工 图 设 计	K6+418.3 新沙高架桥 边桁节段04设计图	设计	余汪千	复核	袁勤	一审	沈华	二审	李忠	图号	SZYS/04/02/02/01/ 34

7225013191712

大样A（节段4~节段5）

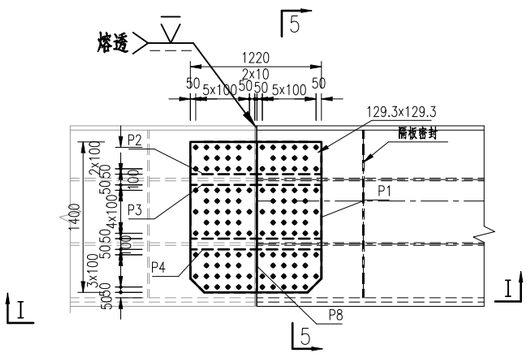

5-5

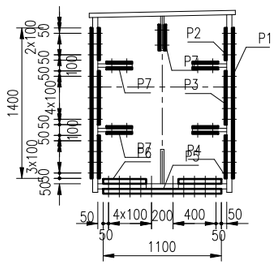

大样C（节段4~节段5）

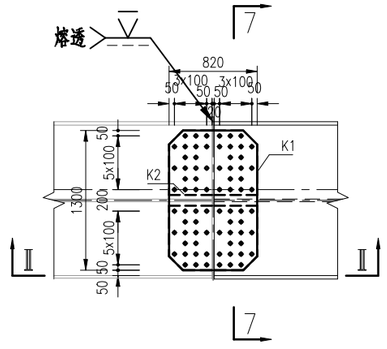

7-7

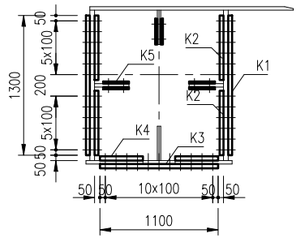

注：

1、本图尺寸均以mm计。

2、未注明的板件裁切边距M30螺栓不小50mm，M24螺栓不小40mm。

3、图中未注明的过焊孔圆弧切角半径为35mm。

4、图中未注明焊缝详见《钢梁焊缝及细节设计图》。

符号：

⊕ —— M30螺栓，开孔直径33mm

⊗ —— M24螺栓，开孔直径26mm

Ⅰ－Ⅰ

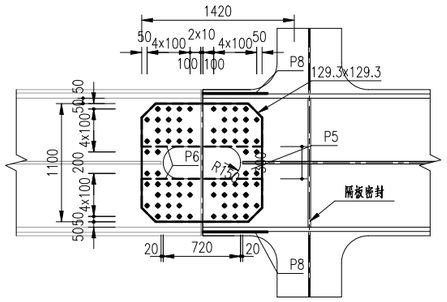

上弦杆顶板、腹板加劲肋拼接

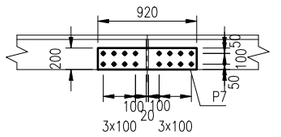

Ⅳ－Ⅳ

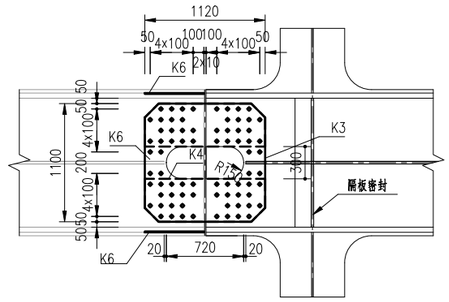

下弦杆顶板、腹板加劲肋拼接

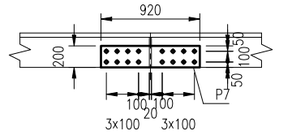

节段4~节段5拼接数量表

名称	编号	材质	规格	数量	单件重	共重（kg）	备注
上弦杆拼接	P1	Q355D	□1220×1400×28	2	375.9	751.8	
	P2		□1220×300×28	2	81.3	162.6	
	P3		□1220×500×28	2	134.1	268.2	
	P4		□1220×400×28	2	107.7	215.4	
	P5		□1420×1100×32	1	391.9	391.9	
	P6		□1420×400×32	2	143.2	286.4	
	P7		□920×200×20	10	28.3	283	
	P8		□600×1800×16	2	135.6	271.2	填板
	P9		□700×1100×16	1	96.7	96.7	填板
	M30高强螺栓	10.9S	M30×200	428	1.94	830.3	
下弦杆拼接	K1	Q355D	□820×1300×20	2	168	336	
	K2		□820×600×20	4	76.9	307.6	
	K3		□1120×1100×32	1	309	309	
	K4		□1120×400×32	2	113	226	
	K5		□920×200×20	6	28.3	169.8	
	K6		□400×1700×16	2	85.4	170.8	
	M30高强螺栓	10.9S	M30×200	276	1.94	535.4	
腹杆拼接	L1	Q355D	□1520×1100×24	2	314.6	629.2	
	L2		□1520×500×24	4	143.2	572.8	
	L3		□1320×1100×28	1	318.7	318.7	
	L4		□1320×500×28	2	145.1	290.2	
	L5		□1520×1100×44	1	576.8	576.8	
	L6		□1520×240×44	2	124.3	248.6	
	L7		□1220×240×24	4	54.6	218.4	
	L8		□1320×240×24	2	60.3	120.6	
	M30高强螺栓	10.9S	M30×200	540	1.94	1047.6	

大样B（节段4~节段5）

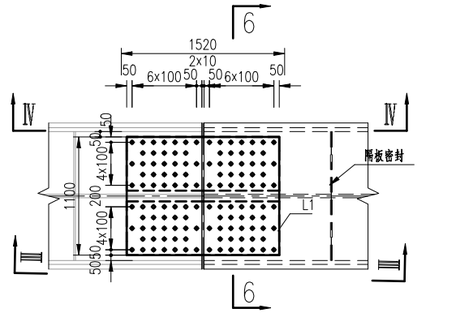

6-6

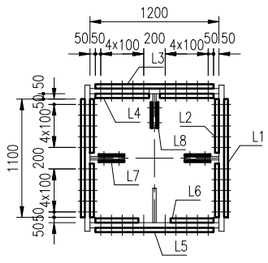

腹杆腹板加劲肋拼接

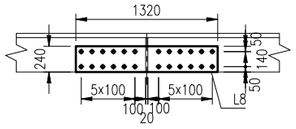

腹杆顶加劲肋拼接

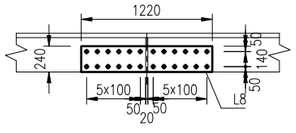

Ⅲ－Ⅲ

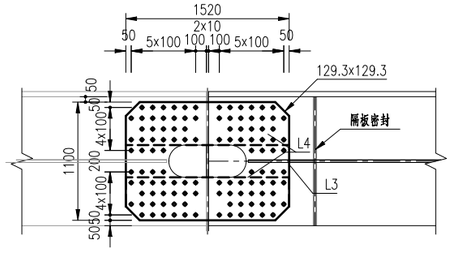

Ⅳ－Ⅳ

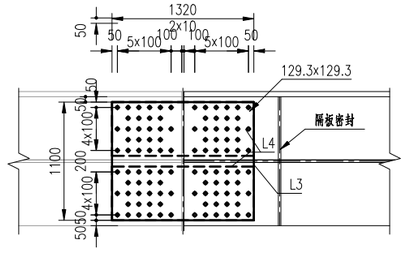

中交第二公路勘察设计研究院有限公司	狮子洋通道工程勘察设计 施 工 图 设 计	K6+418.3 新沙高架桥 边桁节段05设计图	设计	余汪千	复核	袁勤	一审	张华	二审	李忠	图号	SZYS/04/02/02/01/ 35

节段05材料数量表

名称	编号	材质	规格	数量	单件重	共重(kg)	备注
上弦顶板	N11a	Q420D	t=40mm,A=11.85m2	1	3721.1	3721.1	
	N11b	Q355D	t=24mm,A=10.39m2	1	1958.2	1958.2	
上弦底板	N12a	Q420D	□7901×1200×40	1	2976.7	2976.7	
	N12b	Q355D	□7101×1200×24	1	1605.2	1605.2	
上弦节点板	N13	Q420D	t=48mm,A=21.28m2	2	8017	16034	
上弦腹板	N14	Q355D	□7301×1644×32	2	3014.4	6028.8	
上弦横隔板	N15	Q355D	□1560×1200×16	3	234.9	704.7	
	N15a	Q355D	□1576×1200×16	2	237.4	474.8	
	N15‘	Q355D	□2057×200×16	3	51.5	154.5	
	N15b	Q355D	□1782×40×4	4	2.2	8.8	
	N15c	Q355D	□600×400×16	4	30.1	120.4	
上弦加劲肋	N16a	Q420D	□7901×320×32	6	635.5	3813	
	N16b	Q355D	□7101×240×24	6	320.3	1921.8	
下弦顶板	N21a	Q355D	□7903×1850×20	1	2295.3	2295.3	
	N21b	Q355D	□7102×1850×24	1	2475.6	2475.6	
下弦底板	N22a	Q355D	t=20mm,A=12.53m2	1	1967.3	1967.3	
	N22b	Q355D	t=24mm,A=9.71m2	1	1830.1	1830.1	
下弦节点板	N23	Q355D	t=40mm,A=20.72m2	2	6507.5	13015	Z35钢
下弦腹板	N24	Q355D	□7302×1474×32	2	2702.9	5405.8	
下弦横隔板	N25	Q355D	□1450×1200×16	3	218.5	655.5	
	N25a	Q355D	□1450×1200×16	2	218.5	437	
	N25’	Q355D	□1657×200×16	3	41.4	124.2	
下弦加劲肋	N26a	Q355D	□7903×240×20	4	298.3	1193.2	
	N26b	Q355D	□7102×320×32	4	570.2	2280.8	
	N26c	Q355D	□15005×170×14	1	280.2	280.2	
斜腹杆	N31	Q355D	□12781×1200×36	1	4335.1	4335.1	
	N31a	Q355D	□12781×1200×36	1	4335.1	4335.1	
	N32	Q355D	□8581×1360×36	2	3297.9	6595.8	
	N33	Q355D	□8581×320×32	2	690.8	1381.6	
	N33a	Q355D	□11381×320×32	1	914.4	914.4	
	N33b	Q355D	□11381×320×32	1	914.4	914.4	
	N34	Q355D	□1200×1200×16	3	180.9	542.7	
	N41	Q355D	□6135×1200×36	1	2079.9	2079.9	
	N41a	Q355D	□6135×1200×36	1	2079.9	2079.9	
	N42	Q355D	□4135×1360×36	2	1588.2	3176.4	
	N43	Q355D	□4135×320×32	2	331.6	663.2	
	N43a	Q355D	□5435×320×32	1	437.1	437.1	
	N43b	Q355D	□5435×320×32	1	437.1	437.1	
	N44	Q355D	□1200×1200×16	3	180.9	542.7	
节点板加劲	N51	Q355D	□6425×1200×36	1	2178.8	2178.8	
	N51a	Q355D	□6425×1200×36	1	2178.8	2178.8	
	N52	Q355D	□4225×1360×36	2	1625	3250	
	N53	Q355D	□4225×320×32	2	339.1	678.2	
	N53a	Q355D	□5725×320×32	1	459.7	459.7	
	N53b	Q355D	□5725×320×32	1	459.7	459.7	
	N54	Q355D	□1200×1200×16	3	180.9	542.7	
	N55	Q355D	□2300×320×32	4	185.9	743.6	
	N56	Q355D	□2600×320×32	4	208.5	834	
横梁接头	N61	Q355D	□1560×602×14	3	103.3	309.9	
	N61a	Q355D	□1576×618×14	2	106.6	213.2	
	N62	Q355D	t=24mm,A=0.46m2	3	86.7	260.1	
	N62a	Q355D	t=24mm,A=0.46m2	2	86.7	173.4	
	N63	Q355D	□1450×610×14	3	96.7	290.1	
	N63a	Q355D	□1450×618×14	2	98.9	197.8	
小计						112687.4	
焊缝重1.5%						1690.3	
合计						114377.7	

节段05材料数量汇总表

规格(mm)	材质	单个合计	全桥共2个
t=48	Q420D	16034	32068
t=40		6697.8	13395.6
t=32		3813	7626
合计		26544.8	53089.6
t=40	Q355D	13015	26030
t=36		30209.8	60419.6
t=32		21638.4	43276.8
t=24		10224.4	20448.8
t=20		5455.8	10911.6
t=16		4299.2	8598.4
t=14		1291.2	2582.4
t=4		8.8	17.6
合计		86142.6	172285.2
焊缝重(1.5%)		1690.3	3380.6
内表面涂装(㎡)		367.2	734.4
外表面涂装(㎡)		530.5	1061

节段4~节段5拼接数量汇总表

规格(mm)	材质	单个合计	全桥共2个
t=44	Q355D	825.4	1650.8
t=32	Q355D	1213.3	2426.6
t=28	Q355D	2006.9	4013.8
t=24	Q355D	1541	3082
t=20	Q355D	1096.4	2192.8
t=16	Q355D	538.7	1077.4
合计	Q355D	7221.7	14443.4
M30x200	10.9S高强螺栓	2413.3	4826.6
外表面涂装(㎡)		35.8	71.6

中交第二公路勘察设计研究院有限公司	狮子洋通道工程勘察设计 施 工 图 设 计	K6+418.3 新沙高架桥 边桁节段05设计图	设计	余汪千	复核	袁勤	一审	沈华	二审	李忠	图号	SZYS/04/02/02/01/ 35

7 785014 151027

大样A（节段5~节段6）

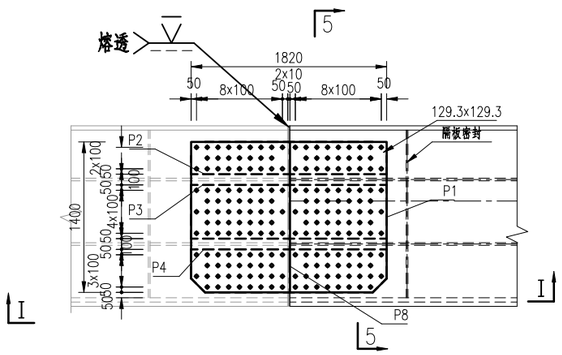

5-5

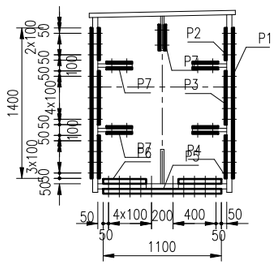

大样C（节段5~节段6）

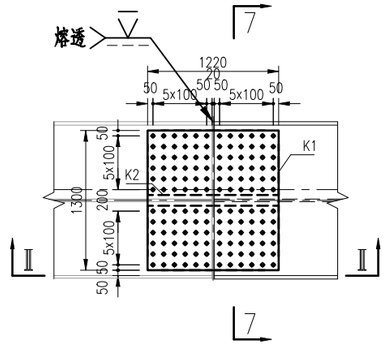

7-7

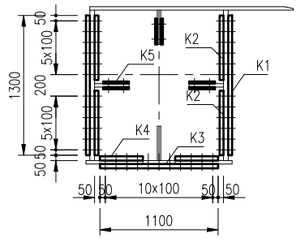

注：

1、本图尺寸均以mm计。

2、未注明的板件裁切边距M30螺栓不小50mm，M24螺栓不小40mm。

3、图中未注明的过焊孔圆弧切角半径为35mm。

4、图中未注明焊缝详见《钢梁焊缝及细节设计图》。

符号：

⊕ —— M30螺栓，开孔直径33mm

⊗ —— M24螺栓，开孔直径26mm

Ⅰ－Ⅰ

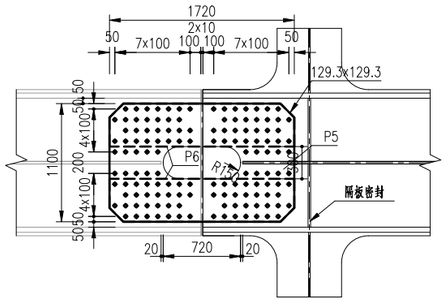

上弦杆顶板、腹板加劲肋拼接

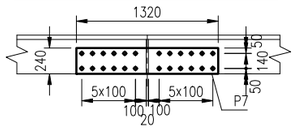

Ⅳ－Ⅳ

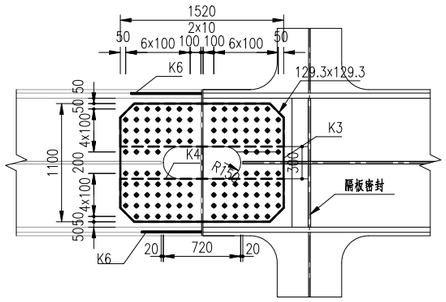

下弦杆顶板、腹板加劲肋拼接

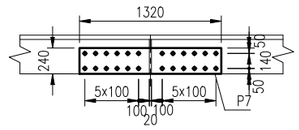

节段5~节段6拼接数量表

名称	编号	材质	规格	数量	单件重	共重（kg）	备注
上弦杆拼接	P1	Q420D	□1820×1400×40	2	800.7	1601.4	
	P2		□1820×300×40	2	172.7	345.4	
	P3		□1820×500×40	2	285.7	571.4	
	P4		□1820×400×40	2	229.2	458.4	
	P5		□1720×1100×44	1	652.8	652.8	
	P6		□1720×400×44	2	238.3	476.6	
	P7		□1320×240×24	10	60.3	603	
	M30高强螺栓	10.9S	M30x200	652	1.94	1264.9	
下弦杆拼接	K1	Q355D	□1020×1300×24	2	250.6	501.2	
	K2		□1020×600×24	4	114.9	459.6	
	K3		□1320×1100×36	1	409.8	409.8	
	K4		□1320×400×36	2	149.8	299.6	
	K5		□920×200×20	6	28.3	169.8	
	K6		□500×1700×8	2	53.4	106.8	填板
	K7		□650×1100×4	1	22.6	22.6	填板
	M30高强螺栓	10.9S	M30x200	344	1.94	667.4	
腹杆拼接	L1	Q355D	□1520×1100×24	2	314.6	629.2	
	L2		□1520×500×24	4	143.2	572.8	
	L3		□1320×1100×28	1	318.7	318.7	
	L4		□1320×500×28	2	145.1	290.2	
	L5		□1520×1100×44	1	576.8	576.8	
	L6		□1520×240×44	2	124.3	248.6	
	L7		□1220×240×24	4	54.6	218.4	
	L8		□1320×240×24	2	60.3	120.6	
	M30高强螺栓	10.9S	M30x200	540	1.94	1047.6	

大样B（节段5~节段6）

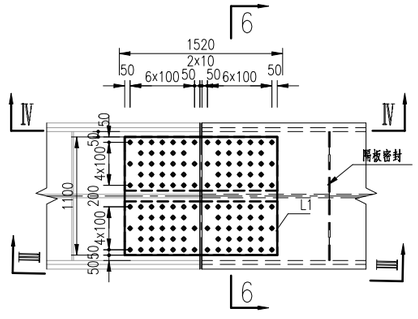

6-6

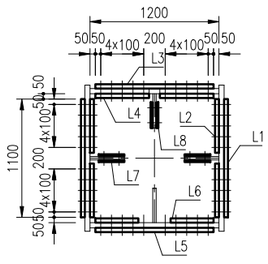

腹杆腹板加劲肋拼接

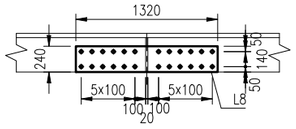

腹杆顶加劲肋拼接

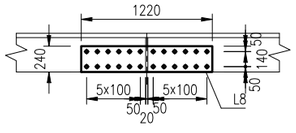

Ⅲ－Ⅲ

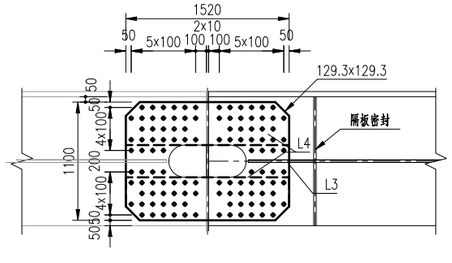

Ⅳ－Ⅳ

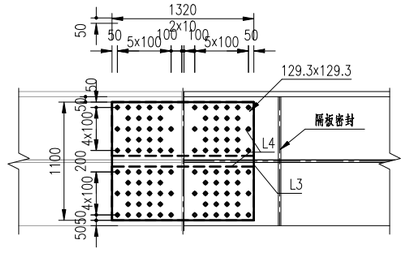

中交第二公路勘察设计研究院有限公司	狮子洋通道工程勘察设计 施 工 图 设 计	K6+418.3 新沙高架桥 边桁节段06设计图	设计	余汪千	复核	袁勤	一审	沈雁	二审	李忠	图号	SZYS/04/02/02/01/ 36

72501014325103

节段06材料数量表

名称	编号	材质	规格	数量	单件重	共重（kg）	备注
上弦顶板	N11a	Q420D	t=40mm,A=11.85m2	1	3721.1	3721.1	
	N11b	Q420D	t=40mm,A=10.39m2	1	3263.6	3263.6	
上弦底板	N12a	Q420D	□7901×1200×40	1	2976.7	2976.7	
	N12b	Q420D	□7101×1200×40	1	2675.3	2675.3	
上弦节点板	N13	Q420D	t=48mm,A=22.14m2	2	8343.1	16686.2	
上弦腹板	N14	Q420D	□7301×1628×48	2	4480.2	8960.4	
上弦横隔板	N15	Q420D	□1560×1200×16	3	234.9	704.7	
	N15a	Q420D	□1560×1200×16	2	234.9	469.8	
	N15‘	Q420D	□2057×200×16	3	51.5	154.5	
	N15b	Q420D	□1782×40×4	4	2.2	8.8	
	N15c	Q420D	□600×400×16	4	30.1	120.4	
上弦加劲肋	N16a	Q420D	□7901×320×32	6	635.5	3813	
	N16b	Q420D	□7101×320×32	6	570.2	3421.2	
下弦顶板	N21a	Q420D	□7903×1850×32	1	3672.5	3672.5	
	N21b	Q420D	□7102×1850×32	1	3300.8	3300.8	
下弦底板	N22a	Q420D	t=32mm,A=12.53m2	1	3147.7	3147.7	
	N22b	Q420D	t=32mm,A=9.71m2	1	2440.1	2440.1	
下弦节点板	N23	Q420D	t=48mm,A=20.72m2	2	7807.9	15615.8	Z35钢
下弦腹板	N24	Q420D	□7302×1482×44	2	3737.2	7474.4	
下弦横隔板	N25	Q420D	□1450×1200×16	3	218.5	655.5	
	N25a	Q420D	□1450×1200×16	2	218.5	437	
	N25’	Q420D	□1657×200×16	3	41.4	124.2	
下弦加劲肋	N26a	Q420D	□7903×320×32	4	635.5	2542	
	N26b	Q420D	□7102×320×32	4	570.2	2280.8	
	N26c	Q420D	□15005×170×14	1	280.2	280.2	
斜腹杆	N31	Q355D	□12589×1200×36	1	4270.1	4270.1	
	N31a	Q355D	□12589×1200×36	1	4270.1	4270.1	
	N32	Q355D	□8389×1360×36	2	3224.5	6449	
	N33	Q355D	□8389×320×32	2	673.2	1346.4	
	N33a	Q355D	□11189×320×32	1	899.3	899.3	
	N33b	Q355D	□11189×320×32	1	899.3	899.3	
	N34	Q355D	□1200×1200×16	3	180.9	542.7	
	N41	Q355D	□5853×1200×40	1	2204.3	2204.3	
	N41a	Q355D	□6053×1200×40	1	2279.6	2279.6	
	N42	Q355D	□4053×1760×40	2	2238.8	4477.6	
	N43	Q355D	□4053×320×32	4	326.6	1306.4	
	N43a	Q355D	□5153×320×32	1	414.5	414.5	
	N43b	Q355D	□5353×320×32	1	429.6	429.6	
	N44	Q355D	□1200×1600×16	2	241.2	482.4	
节点板加劲	N51	Q420D	□6335×1200×40	1	2386.4	2386.4	
	N51a	Q420D	□6335×1200×40	1	2386.4	2386.4	
	N52	Q420D	□4135×1360×40	2	1764.7	3529.4	
	N53	Q420D	□4135×320×32	4	331.6	1326.4	
	N53a	Q420D	□5635×320×32	1	452.2	452.2	
	N53b	Q420D	□5635×320×32	1	452.2	452.2	
	N54	Q420D	□1200×1200×16	2	180.9	361.8	
	N55	Q420D	□2100×320×32	6	168.3	1009.8	
	N56	Q420D	□2200×320×32	4	175.8	703.2	
横梁接头	N61	Q355D	□1560×602×14	3	103.3	309.9	
	N61a	Q355D	□1560×602×14	2	103.3	206.6	
	N62	Q355D	t=24mm,A=0.46m2	3	86.7	260.1	
	N62a	Q355D	t=24mm,A=0.46m2	2	86.7	173.4	
	N63	Q355D	□1350×602×14	3	89	267	
	N63a	Q355D	□1350×606×14	2	90.1	180.2	
小计						133223	
焊缝重1.5%						1998.3	
合计						135221.3	

节段06材料数量汇总表

规格（mm）	材质	单个合计	全桥共2个
t=48	Q420D	41262.4	82524.8
t=44		7474.4	14948.8
t=40		20938.9	41877.8
t=32		28561.9	57123.8
t=16		3027.9	6055.8
t=14		280.2	560.4
t=4		8.8	17.6
合计		101554.5	203109
t=40	Q355D	8961.5	17923
t=36		14989.2	29978.4
t=32		5295.5	10591
t=24		433.5	867
t=16		1025.1	2050.2
t=14		963.7	1927.4
合计		31668.5	63337
焊缝重（1.5%）		1998.3	3996.6
内表面涂装（m²）		373.5	747
外表面涂装（m²）		547.2	1094.4

节段5~节段6拼接数量汇总表

规格（mm）	材质	单个合计	全桥共2个
t=44	Q420D	1129.4	2258.8
t=40		2976.6	5953.2
t=24		603	1206
合计		4709.0	9418
t=44	Q355D	825.4	1650.8
t=36		709.4	1418.8
t=28		608.9	1217.8
t=24		2501.8	5003.6
t=20		169.8	339.6
t=8		106.8	213.6
t=4		22.6	45.2
合计		4944.7	9889.4
M30x200	10.9S高强螺栓	2979.9	5959.8
外表面涂装（m²）		40.4	80.8

中交第二公路勘察设计研究院有限公司	狮子洋通道工程勘察设计 施 工 图 设 计	K6+418.3 新沙高架桥 边桁节段06设计图	设计	余汪千	复核	袁勤	一审	沈华	二审	李忠	图号	SZYS/04/02/02/01/ 36

4350014388350

大样A（节段6~节段7）

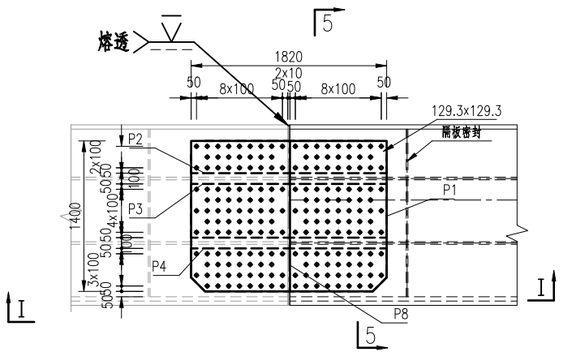

5-5

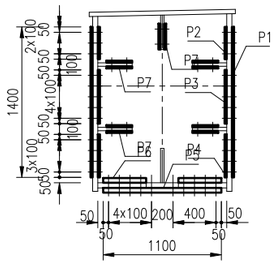

大样C（节段6~节段7）

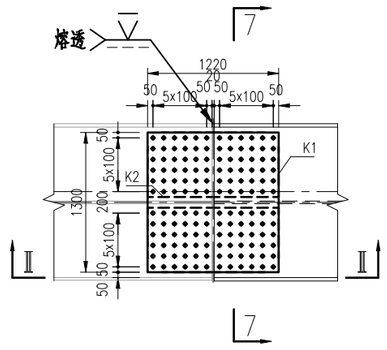

7-7

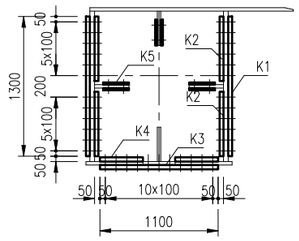

Ⅰ-Ⅰ

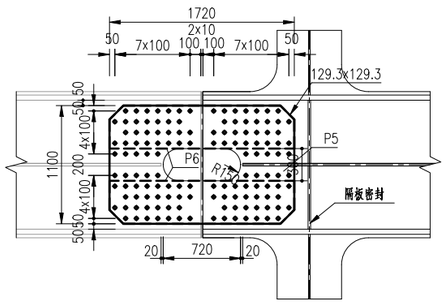

上弦杆顶板、腹板加劲肋拼接

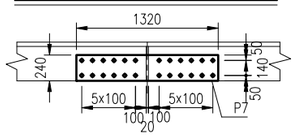

Ⅳ-Ⅳ

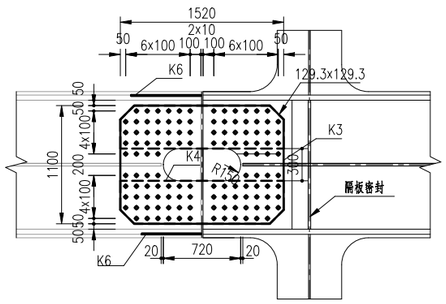

下弦杆顶板、腹板加劲肋拼接

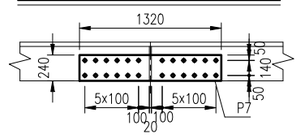

大样B（节段6~节段7）

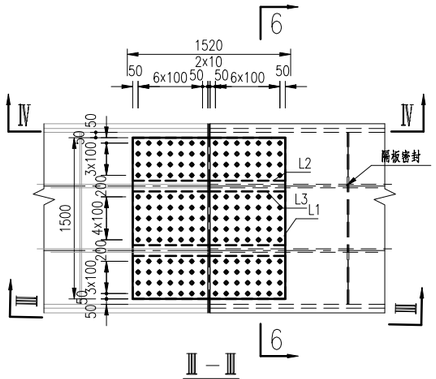

6-6

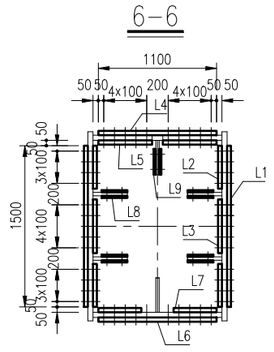

腹杆腹板加劲肋拼接

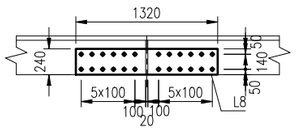

腹杆顶加劲肋拼接

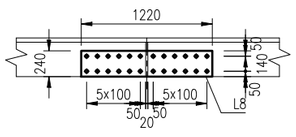

Ⅲ-Ⅲ

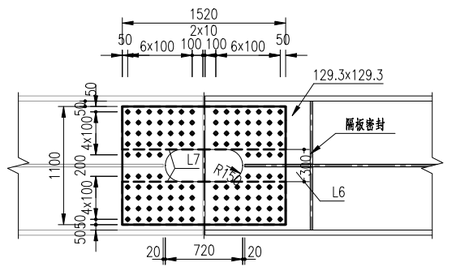

Ⅳ-Ⅳ

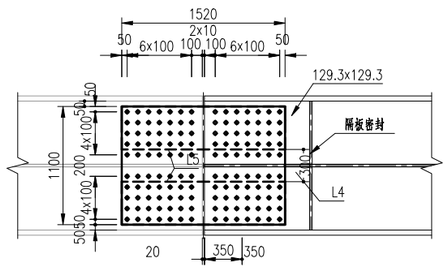

节段6~节段7拼接数量表

名称	编号	材质	规格	数量	单件重	共重（kg）	备注
上弦杆拼接	P1	Q420D	□1820×1400×40	2	800.7	1601.4	
	P2		□1820×300×40	2	172.7	345.4	
	P3		□1820×500×40	2	285.7	571.4	
	P4		□1820×400×40	2	229.2	458.4	
	P5		□1720×1100×44	1	652.8	652.8	
	P6		□1720×400×44	2	238.3	476.6	
	P7		□1320×240×24	10	60.3	603	
	M30高强螺栓	10.9S	M30x200	652	1.94	1264.9	
下弦杆拼接	K1	Q420D	□1220×1300×28	2	349.5	699	
	K2		□1220×600×28	4	160.5	642	
	K3		□1520×1100×36	1	471.9	471.9	
	K4		□1520×400×36	2	172.4	344.8	
	K5		□1320×240×24	6	60.3	361.8	
	K6		□600×1300×4	1	24.5	24.5	填板
	M30高强螺栓	10.9S	M30x200	484	1.94	939	
腹杆拼接	L1	Q420D	□1520×1500×32	2	572.7	1145.4	
	L2		□1520×400×32	4	153.2	612.8	
	L3		□1520×500×32	2	190.9	381.8	
	L4		□1520×1100×28	1	367.1	367.1	
	L5		□1520×500×28	2	167	334	
	L6		□1520×1100×40	1	524.4	524.4	
	L7		□1520×400×40	2	191.5	383	
	L8		□1320×240×24	10	60.3	603	
	M30高强螺栓	10.9S	M30x200	752	1.94	1458.9	

注：

1、本图尺寸均以mm计。

2、未注明的板件裁切边距M30螺栓不小50mm，M24螺栓不小40mm。

3、图中未注明的过焊孔圆弧切角半径为35mm。

4、图中未注明焊缝详见《钢梁焊缝及细节设计图》。

符号：

⊕ —— M30螺栓，开孔直径33mm

⊗ —— M24螺栓，开孔直径26mm

节段07材料数量表

名称	编号	材质	规格	数量	单件重	共重（kg）	备注
上弦顶板	N11a	Q420D	t=40mm,A=11.85m2	1	3720.9	3720.9	
	N11b	Q420D	t=40mm,A=10.4m2	1	3265.6	3265.6	
上弦底板	N12a	Q420D	□7900×1200×40	1	2976.7	2976.7	
	N12b	Q420D	□7100×1200×40	1	2675.3	2675.3	
上弦节点板	N13	Q420D	t=44mm,A=22.94m2	2	7923.5	15847	
上弦腹板	N14	Q420D	□7300×1628×48	2	4476.4	8952.8	
上弦横隔板	N15	Q420D	□1560×1200×16	3	234.9	704.7	
	N15a	Q420D	□1560×1200×16	2	234.9	469.8	
	N15 ‘	Q420D	□2057×200×16	3	51.5	154.5	
	N15b	Q420D	□1782×40×4	4	2.2	8.8	
	N15c	Q420D	□600×400×16	4	30.1	120.4	
上弦加劲肋	N16a	Q420D	□7900×320×32	6	635.5	3813	
	N16b	Q420D	□7100×320×32	6	570.2	3421.2	
下弦顶板	N21a	Q420D	□7901×1850×32	1	3672.5	3672.5	
	N21b	Q420D	□7101×1850×32	1	3300.8	3300.8	
下弦底板	N22a	Q420D	t=40mm,A=15.8m2	1	4961.2	4961.2	
	N22b	Q420D	t=32mm,A=10.4m2	1	2612.5	2612.5	
下弦节点板	N23	Q420D	t=44mm,A=22.56m2	2	7792.2	15584.4	Z35钢
下弦腹板	N24	Q420D	□7301×1482×44	2	3737.2	7474.4	
下弦横隔板	N25	Q420D	□1450×1200×16	3	218.5	655.5	
	N25a	Q420D	□1450×1200×16	2	218.5	437	
	N25’	Q420D	□1657×200×16	3	41.4	124.2	
下弦加劲肋	N26a	Q420D	□7901×320×32	4	635.5	2542	
	N26b	Q420D	□7101×320×32	4	570.2	2280.8	
	N26c	Q420D	□15002×170×14	2	280.2	560.4	
斜腹杆	N31	Q420D	□11812×1200×40	1	4449.4	4449.4	
	N31a	Q420D	□12212×1200×40	1	4600.1	4600.1	
	N32	Q420D	□8212×1760×40	2	4537.3	9074.6	
	N33	Q420D	□8212×320×32	4	660.7	2642.8	
	N33a	Q420D	□10412×320×32	1	836.5	836.5	
	N33b	Q420D	□10812×320×32	1	869.2	869.2	
	N34	Q420D	□1200×1600×16	3	241.2	723.6	
	N41	Q420D	□5769×1200×40	1	2172.9	2172.9	
	N41a	Q420D	□5969×1200×40	1	2248.2	2248.2	
	N42	Q420D	□3969×1760×40	2	2194.9	4389.8	
	N43	Q420D	□3969×320×32	4	319	1276	
	N43a	Q420D	□5069×320×32	1	406.9	406.9	
	N43b	Q420D	□5269×320×32	1	424.5	424.5	
	N44	Q420D	□1200×1600×16	2	241.2	482.4	
	N51	Q420D	□5853×1200×40	1	2204.3	2204.3	
节点板加劲	N51a	Q420D	□6053×1200×40	1	2279.6	2279.6	
	N52	Q420D	□4053×1760×40	2	2238.8	4477.6	
	N53	Q420D	□4053×320×32	4	326.6	1306.4	
	N53a	Q420D	□5153×320×32	1	414.5	414.5	
	N53b	Q420D	□5353×320×32	1	429.6	429.6	
	N54	Q420D	□1200×1600×16	2	241.2	482.4	
	N55	Q420D	□2100×320×32	8	168.3	1346.4	
	N56	Q420D	□2000×320×32	8	160.8	1286.4	
横梁接头	N61	Q355D	□1560×606×14	3	104.4	313.2	
	N61a	Q355D	□1560×602×14	2	103.3	206.6	
	N62	Q355D	t=24mm,A=0.47m2	3	89.3	267.9	
	N62a	Q355D	t=24mm,A=0.48m2	2	90.4	180.8	
	N63	Q355D	□1450×606×14	2	96.7	193.4	
	N63a	Q355D	□1450×606×14	2	96.7	193.4	
支座加劲	N81	Q420D	□1450×1200×32	5	437.1	2185.5	
	N82	Q420D	□1450×602×60	3	409.8	1229.4	
	N83	Q420D	□2800×2650×100	1	5824.7	5824.7	
	N84	Q420D	□1000×568×32	4	143.2	572.8	
	N85	Q420D	□1350×570×32	7	193.4	1353.8	
	N86	Q420D	□2960×650×32	1	482.3	482.3	
小计						152164.3	
焊缝重1.5%						2282.5	
合计						154446.8	

节段07材料数量汇总表

规格（mm）	材质	单个合计	全桥共2个
t=100	Q420D	5824.7	11649.4
t=60		1229.4	2458.8
t=48		8952.8	17905.6
t=44		38905.8	77811.6
t=40		53496.2	106992.4
t=32		36994.1	73988.2
t=16		4354.5	8709
t=14		560.4	1120.8
t=4		8.8	17.6
合计		150326.7	300653.4
t=24	Q355D	448.7	897.4
t=14		906.6	1813.2
合计		1355.3	2710.6
焊缝重（1.5%）		2275.2	4550.4
内表面涂装（㎡）		418.7	837.4
外表面涂装（㎡）		610.8	1221.6

节段6~节段7拼接数量汇总表

规格（mm）	材质	单个合计	全桥共2个
t=44	Q420D	1129.4	2258.8
t=40		3884	7768
t=36		816.7	1633.4
t=32		2140	4280
t=28		2042.1	4084.2
t=24		1567.8	3135.6
t=4		24.5	49
合计		11604.5	23209
M30x200	10.9S高强螺栓	3662.8	7325.6
外表面涂装（㎡）		45.4	90.88

中交第二公路勘察设计研究院有限公司	狮子洋通道工程勘察设计 施 工 图 设 计	K6+418.3 新沙高架桥 边桁节段07设计图	设计	余汪千	复核	袁勤	一审	张华	二审	李忠	图号	SZYS/04/02/02/01/ 37

大样A（节段7~节段8）

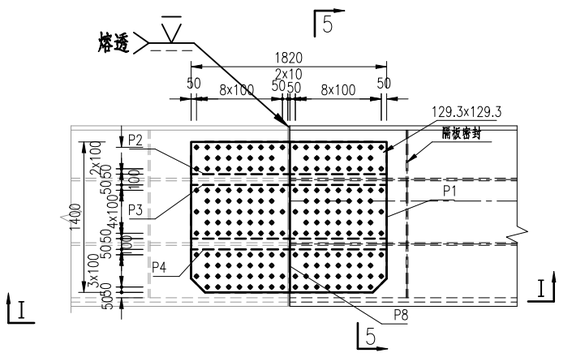

5-5

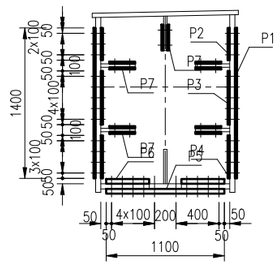

大样C（节段7~节段8）

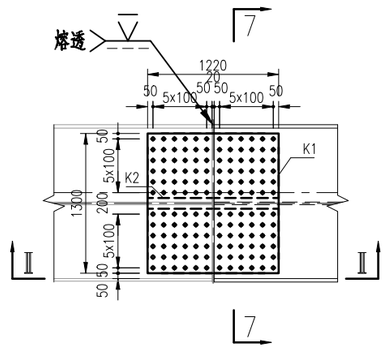

7-7

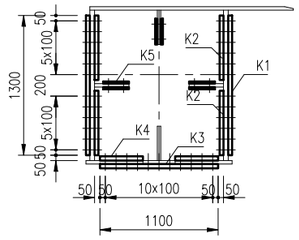

Ⅰ－Ⅰ

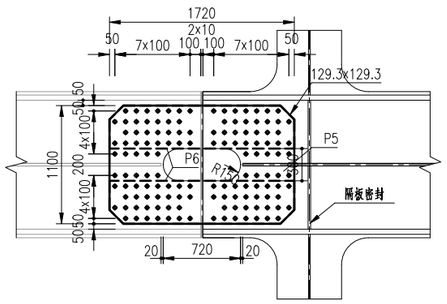

上弦杆顶板、腹板加劲肋拼接

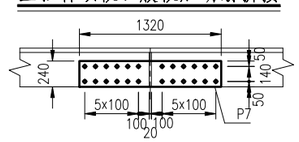

Ⅳ－Ⅳ

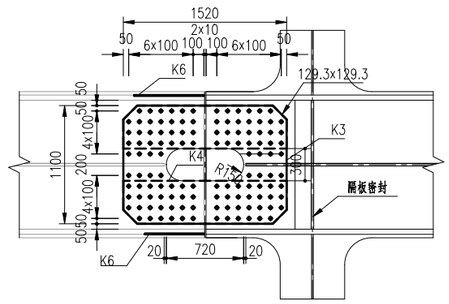

下弦杆顶板、腹板加劲肋拼接

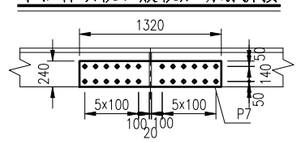

注：

1、本图尺寸均以mm计。

2、未注明的板件裁切边距M30螺栓不小50mm，M24螺栓不小40mm。

3、图中未注明的过焊孔圆弧切角半径为35mm。

4、图中未注明焊缝详见《钢梁焊缝及细节设计图》。

符号：

⊕ —— M30螺栓，开孔直径33mm

⊗ —— M24螺栓，开孔直径26mm

大样B（节段7~节段8）

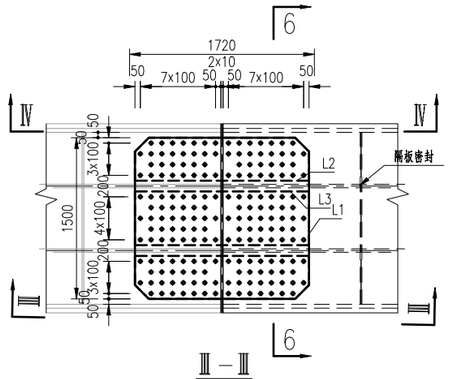

6-6

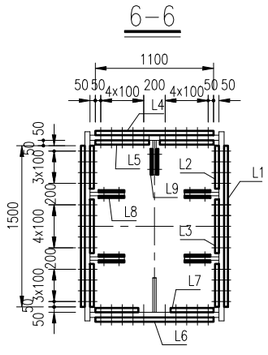

腹杆腹板加劲肋拼接

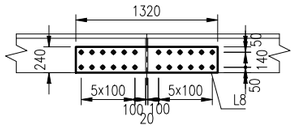

腹杆顶加劲肋拼接

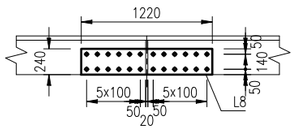

Ⅲ－Ⅲ

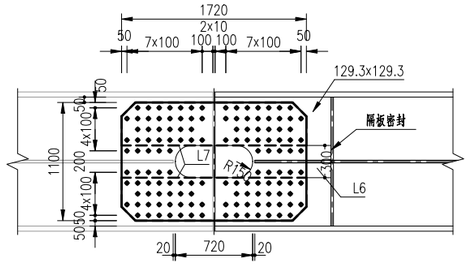

Ⅳ－Ⅳ

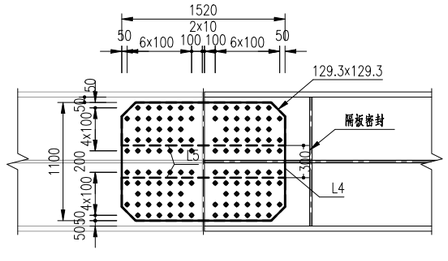

节段7~节段8拼接数量表

名称	编号	材质	规格	数量	单件重	共重（kg）	备注
上弦杆拼接	P1	Q420D	□1820×1400×40	2	800.7	1601.4	
	P2		□1820×300×40	2	172.7	345.4	
	P3		□1820×500×40	2	285.7	571.4	
	P4		□1820×400×40	2	229.2	458.4	
	P5		□1720×1100×44	1	652.8	652.8	
	P6		□1720×400×44	2	238.3	476.6	
	P7		□1320×240×24	10	60.3	603	
	M30高强螺栓	10.9S	M30x200	652	1.94	1264.9	
下弦杆拼接	K1	Q420D	□1220×1300×28	2	349.5	699	
	K2		□1220×600×28	4	160.5	642	
	K3		□1520×1100×36	1	471.9	471.9	
	K4		□1520×400×36	2	172.4	344.8	
	K5		□1320×240×24	6	60.3	361.8	
	K6		□600×1300×4	1	24.5	24.5	填板
	M30高强螺栓	10.9S	M30x200	484	1.94	939	
腹杆拼接	L1	Q420D	□1720×1500×36	2	729.1	1458.2	
	L2		□1720×400×36	4	195	780	
	L3		□1720×500×36	2	243	486	
	L4		□1720×1100×32	1	474.8	474.8	
	L5		□1720×500×32	2	216	432	
	L6		□1520×1100×48	1	629.3	629.3	
	L7		□1520×400×48	2	229.8	459.6	
	L8		□1320×240×24	8	60.3	482.4	
	L9		□1220×240×24	2	54.6	109.2	
	M30高强螺栓	10.9S	M30x200	752	1.94	1458.9	

中交第二公路勘察设计研究院有限公司	狮子洋通道工程勘察设计 施 工 图 设 计	K6+418.3 新沙高架桥 边桁节段08设计图	设计	余汪千	复核	李勤	一审	张华	二审	李忠	图号	SZYS/04/02/02/01/ 38

72550174 85505898

节段08材料数量表

名称	编号	材质	规格	数量	单件重	共重（kg）	备注
上弦顶板	N11a	Q420D	t=40mm,A=11.85m2	1	3721.1	3721.1	
	N11b	Q420D	t=40mm,A=10.39m2	1	3263.6	3263.6	
上弦底板	N12a	Q420D	□7900×1200×40	1	2976.7	2976.7	
	N12b	Q420D	□7100×1200×40	1	2675.3	2675.3	
上弦节点板	N13	Q420D	t=44mm,A=22.19m2	2	7665.4	15330.8	
上弦腹板	N14	Q420D	□7300×1628×48	2	4476.4	8952.8	
上弦横隔板	N15	Q355D	□1560×1200×16	3	234.9	704.7	
	N15a	Q355D	□1657×1200×16	2	249.9	499.8	
	N15‘	Q355D	□2057×200×16	3	51.5	154.5	
	N15b	Q355D	□1782×40×4	4	2.2	8.8	
	N15c	Q355D	□600×400×16	4	30.1	120.4	
上弦加劲肋	N16a	Q420D	□7900×320×32	6	635.5	3813	
	N16b	Q420D	□7100×320×32	6	570.2	3421.2	
下弦顶板	N21a	Q420D	□7901×1850×32	1	3672.5	3672.5	
	N21b	Q355D	□7101×1850×24	1	2475.6	2475.6	
下弦底板	N22a	Q420D	t=32mm,A=12.53m2	1	3147.7	3147.7	
	N22b	Q355D	t=24mm,A=9.71m2	1	1830.1	1830.1	
下弦节点板	N23	Q420D	t=44mm,A=22.54m2	2	7783.8	15567.6	Z35钢
下弦腹板	N24	Q355D	□7301×1474×32	2	2702.9	5405.8	
下弦横隔板	N25	Q355D	□1450×1200×16	3	218.5	655.5	
	N25a	Q355D	□1450×1200×16	2	218.5	437	
	N25'	Q355D	□1657×200×16	3	41.4	124.2	
下弦加劲肋	N26a	Q420D	□7901×320×32	4	635.5	2542	
	N26b	Q355D	□7101×320×32	4	570.2	2280.8	
	N26c	Q355D	□15002×170×14	1	280.2	280.2	
斜腹杆	N31	Q355D	□11850×1200×40	1	4465.1	4465.1	
	N31a	Q355D	□12250×1200×40	1	4615.8	4615.8	
	N32	Q355D	□8050×1760×40	2	4449.4	8898.8	
	N33	Q355D	□8050×320×32	4	648.1	2592.4	
	N33a	Q355D	□10450×320×32	1	839	839	
	N33b	Q355D	□10850×320×32	1	871.7	871.7	
	N34	Q355D	□1200×1600×16	3	241.2	723.6	
	N41	Q355D	□5711×1200×36	1	1935.8	1935.8	
	N41a	Q355D	□6011×1200×36	1	2037.5	2037.5	
	N42	Q355D	□3911×1360×36	2	1503.4	3006.8	
	N43	Q355D	□3911×320×32	2	314	628	
	N43a	Q355D	□5011×320×32	1	401.9	401.9	
	N43b	Q355D	□5311×320×32	1	427	427	
	N44	Q355D	□1200×1200×16	2	180.9	361.8	
节点板加劲	N51	Q355D	□5979×1200×36	1	2026.2	2026.2	
	N51a	Q355D	□6079×1200×36	1	2060.2	2060.2	
	N52	Q355D	□3979×1760×36	2	1978.2	3956.4	
	N53	Q355D	□3979×320×32	4	319	1276	
	N53a	Q355D	□5279×320×32	1	424.5	424.5	
	N53b	Q355D	□5379×320×32	1	432.1	432.1	
	N54	Q355D	□1200×1600×16	2	241.2	482.4	
	N55	Q355D	□2100×320×32	6	168.3	1009.8	
	N56	Q355D	□2400×320×32	8	193.4	1547.2	
横梁接头	N61	Q355D	□1560×606×14	3	104.4	313.2	
	N61a	Q355D	□1560×602×14	2	103.3	206.6	
	N62	Q355D	t=24mm,A=0.46m2	3	86.7	260.1	
	N62a	Q355D	t=24mm,A=0.47m2	2	88.8	177.6	
	N63	Q355D	□1450×606×14	3	96.7	290.1	
	N63a	Q355D	□1450×618×14	2	98.9	197.8	
小计						130527.1	
焊缝重1.5%						1957.9	
合计						132485.0	

节段08材料数量汇总表

规格（mm）	材质	单个合计	全桥共2个
t=48	Q420D	8952.8	17905.6
t=44		30898.4	61796.8
t=40		12636.7	25273.4
t=32		16596.4	33192.8
合计		69084.3	138168.6
t=40	Q355D	17979.7	35959.4
t=36		15022.9	30045.8
t=32		18136.2	36272.4
t=24		4743.4	9486.8
t=16		4263.9	8527.8
t=14		1287.9	2575.8
t=4		8.8	17.6
合计		61442.8	122885.6
焊缝重（1.5%）		1957.9	3915.8
内表面涂装（㎡）		387.6	775.2
外表面涂装（㎡）		558.9	1117.8

节段7~节段8拼接数量汇总表

规格（mm）	材质	单个合计	全桥共2个
t=48	Q420D	1088.9	2177.8
t=44		1129.4	2258.8
t=40		2976.6	5953.2
t=36		3540.9	7081.8
t=32		906.8	1813.6
t=28		1341	2682
t=24		1556.4	3112.8
t=4		24.5	49
合计		12564.5	25129
M30x200	10.9S高强螺栓	3662.8	7325.6
外表面涂装（㎡）		46.9	93.84

中交第二公路勘察设计研究院有限公司	狮子洋通道工程勘察设计 施 工 图 设 计	K6+418.3 新沙高架桥 边桁节段08设计图	设计	余汪千	复核	袁勤	一审	张华	二审	李忠	图号	SZYS/04/02/02/01/ 38

大样A（节段8~节段9）

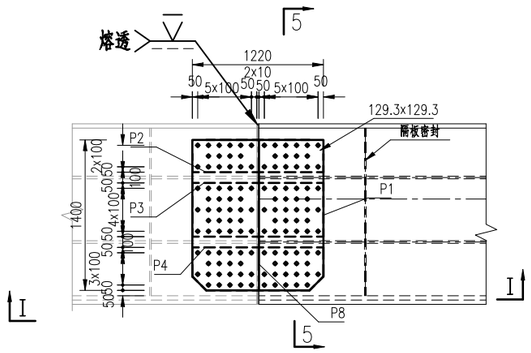

5-5

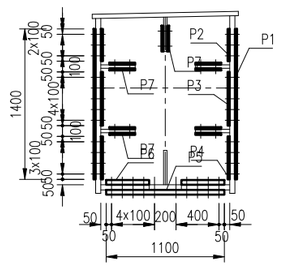

Ⅰ－Ⅰ

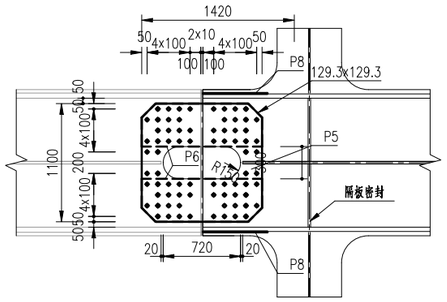

上弦杆顶板、腹板加劲肋拼接

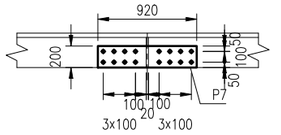

大样C（节段8~节段9）

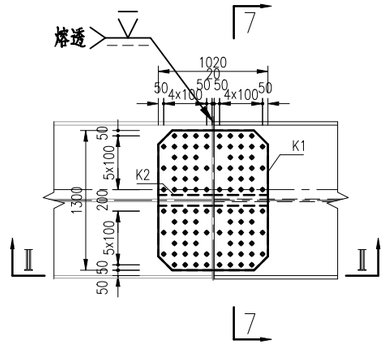

7-7

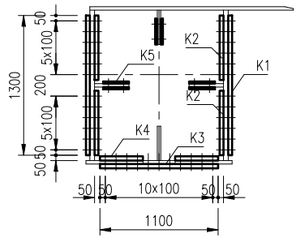

Ⅳ－Ⅳ

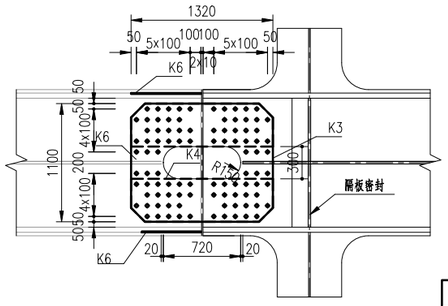

下弦杆顶板、腹板加劲肋拼接

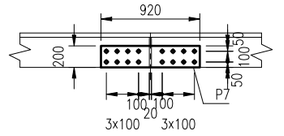

注：

1、本图尺寸均以mm计。

2、未注明的板件裁切边距M30螺栓不小50mm，M24螺栓不小40mm。

3、图中未注明的过焊孔圆弧切角半径为35mm。

4、图中未注明焊缝详见《钢梁焊缝及细节设计图》。

符号：

⊕ —— M30螺栓，开孔直径33mm

⊗ —— M24螺栓，开孔直径26mm

大样B（节段8~节段9）

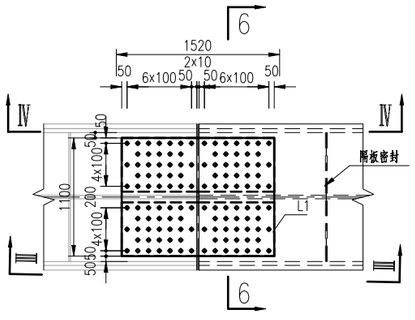

6-6

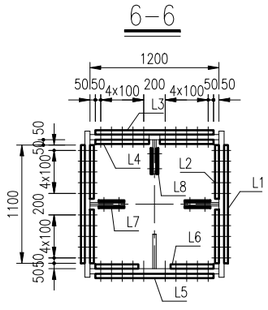

腹杆腹板加劲肋拼接

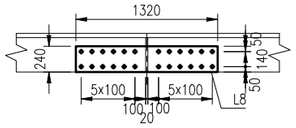

腹杆顶加劲肋拼接

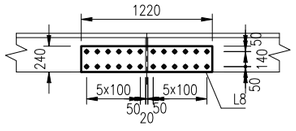

Ⅲ－Ⅲ

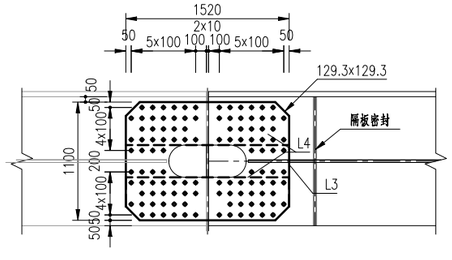

Ⅳ－Ⅳ

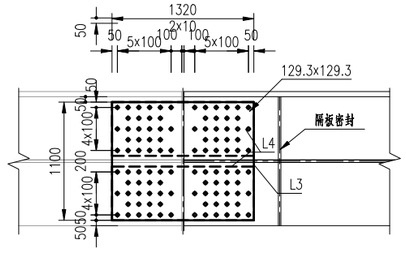

节段8~节段9拼接数量表

名称	编号	材质	规格	数量	单件重	共重（kg）	备注
上弦杆拼接	P1	Q355D	□1220×1400×28	2	375.9	751.8	
	P2		□1220×300×28	2	81.3	162.6	
	P3		□1220×500×28	2	134.1	268.2	
	P4		□1220×400×28	2	107.7	215.4	
	P5		□1420×1100×32	1	391.9	391.9	
	P6		□1420×400×32	2	143.2	286.4	
	P7		□920×200×20	10	28.3	283	
	P8		□600×1800×16	2	135.6	271.2	填板
	P9		□700×1100×16	1	96.7	96.7	填板
	M30高强螺栓	10.9S	M30x200	428	1.94	830.3	
下弦杆拼接	K1	Q355D	□1020×1300×24	2	250.6	501.2	
	K2		□1020×600×24	4	114.9	459.6	
	K3		□1320×1100×36	1	409.8	409.8	
	K4		□1320×400×36	2	149.8	299.6	
	K5		□920×200×20	6	28.3	169.8	
	K6		□500×1700×8	2	53.4	106.8	填板
	K7		□650×1100×4	1	22.6	22.6	填板
	M30高强螺栓	10.9S	M30x200	344	1.94	667.4	
腹杆拼接	L1	Q355D	□1520×1100×24	2	314.6	629.2	
	L2		□1520×500×24	4	143.2	572.8	
	L3		□1320×1100×28	1	318.7	318.7	
	L4		□1320×500×28	2	145.1	290.2	
	L5		□1520×1100×44	1	576.8	576.8	
	L6		□1520×240×44	2	124.3	248.6	
	L7		□1220×240×24	4	54.6	218.4	
	L8		□1320×240×24	2	60.3	120.6	
	M30高强螺栓	10.9S	M30x200	540	1.94	1047.6	

中交第二公路勘察设计研究院有限公司	狮子洋通道工程勘察设计 施 工 图 设 计	K6+418.3 新沙高架桥 边桁节段09设计图	设计	余汪千	复核	袁勤	一审	沈华	二审	李忠	图号	SZYS/04/02/02/01/ 39

节段09材料数量表

名称	编号	材质	规格	数量	单件重	共重（kg）	备注
上弦顶板	N11a	Q355D	t=20mm,A=11.85m2	1	1860.5	1860.5	
	N11b	Q355D	t=24mm,A=10.39m2	1	1958.2	1958.2	
上弦底板	N12a	Q355D	□7900×1200×20	1	1488.4	1488.4	
	N12b	Q355D	□7100×1200×24	1	1605.2	1605.2	
上弦节点板	N13	Q355D	t=40mm,A=21.41m2	2	6721.5	13443	
上弦腹板	N14	Q355D	□7300×1644×32	2	3014.4	6028.8	
上弦横隔板	N15	Q355D	□1580×1200×16	3	238.6	715.8	
	N15a	Q355D	□1576×1200×16	2	237.4	474.8	
	N15‘	Q355D	□1657×200×16	3	41.4	124.2	
	N15b	Q355D	□1782×40×4	4	2.2	8.8	
	N15c	Q355D	□600×400×16	4	30.1	120.4	
上弦加劲肋	N16a	Q355D	□7900×240×20	6	298.3	1789.8	
	N16b	Q355D	□7100×320×32	6	570.2	3421.2	
下弦顶板	N21a	Q355D	□7901×1850×24	1	2754.4	2754.4	
	N21b	Q355D	□7101×1850×24	1	2475.6	2475.6	
下弦底板	N22a	Q355D	t=24mm,A=12.53m2	1	2360.7	2360.7	
	N22b	Q355D	t=24mm,A=9.71m2	1	1830.1	1830.1	
下弦节点板	N23	Q355D	t=44mm,A=20.72m2	2	7155.4	14310.8	Z35钢
下弦腹板	N24	Q355D	□7301×1474×32	2	2702.9	5405.8	
下弦横隔板	N25	Q355D	□1450×1200×16	3	218.5	655.5	
	N25a	Q355D	□1450×1200×16	2	218.5	437	
	N25’	Q355D	□1657×200×16	3	41.4	124.2	
下弦加劲肋	N26a	Q355D	□7901×320×32	4	635.5	2542	
	N26b	Q355D	□7101×240×20	4	266.9	1067.6	
	N26c	Q355D	□15002×170×14	1	280.2	280.2	
斜腹杆	N31	Q355D	□11903×1200×36	1	4035.5	4035.5	
	N31a	Q355D	□12203×1200×36	1	4137.3	4137.3	
	N32	Q355D	□7903×1360×36	2	3038	6076	
	N33	Q355D	□7903×320×32	2	635.5	1271	
	N33a	Q355D	□10503×320×32	1	844	844	
	N33b	Q355D	□10803×320×32	1	869.2	869.2	
	N34	Q355D	□1200×1200×16	3	180.9	542.7	
	N41	Q355D	□5651×1200×36	1	1916	1916	
	N41a	Q355D	□5951×1200×36	1	2017.8	2017.8	
	N42	Q355D	□3851×1360×36	2	1480.8	2961.6	
	N43	Q355D	□3851×320×32	2	309	618	
	N43a	Q355D	□4951×320×32	1	396.9	396.9	
	N43b	Q355D	□5251×320×32	1	422	422	
	N44	Q355D	□1200×1200×16	3	180.9	542.7	
	N51	Q355D	□6111×1200×36	1	2071.5	2071.5	
节点板加劲	N51a	Q355D	□6111×1200×36	1	2071.5	2071.5	
	N52	Q355D	□3911×1360×36	2	1503.4	3006.8	
	N53	Q355D	□3911×320×32	2	314	628	
	N53a	Q355D	□5411×320×32	1	434.6	434.6	
	N53b	Q355D	□5411×320×32	1	434.6	434.6	
	N54	Q355D	□1200×1200×16	2	180.9	361.8	
	N55	Q355D	□2300×320×32	4	185.9	743.6	
	N56	Q355D	□2600×320×32	4	208.5	834	
横梁接头	N61	Q355D	□1580×610×14	3	105.5	316.5	
	N61a	Q355D	□1576×618×14	2	106.6	213.2	
	N62	Q355D	t=24mm,A=0.46m2	3	86.7	260.1	
	N62a	Q355D	t=24mm,A=0.47m2	2	89.3	178.6	
	N63	Q355D	□1450×606×14	3	96.7	290.1	
	N63a	Q355D	□1450×618×14	2	98.9	197.8	
小计						105976.4	
焊缝重1.5%						1589.6	
合计						107566.0	

节段09材料数量汇总表

规格（mm）	材质	单个合计	全桥共2个
t=44	Q355D	14310.8	28621.6
t=40	Q355D	13443	26886
t=36	Q355D	28294	56588
t=32	Q355D	24893.7	49787.4
t=24	Q355D	13422.9	26845.8
t=20	Q355D	6206.3	12412.6
t=16	Q355D	4099.1	8198.2
t=14	Q355D	1297.8	2595.6
t=4	Q355D	8.8	17.6
焊缝重（1.5%）		1589.6	3179.292
	Q355D	107566.0	215132.092
内表面涂装（㎡）		350.8	701.6
外表面涂装（㎡）		527.1	1054.2

节段8~节段9拼接数量汇总表

规格（mm）	材质	单个合计	全桥共2个
t=44	Q355D	825.4	1650.8
t=36	Q355D	709.4	1418.8
t=32	Q355D	678.3	1356.6
t=28	Q355D	2006.9	4013.8
t=24	Q355D	2501.8	5003.6
t=20	Q355D	452.8	905.6
t=16	Q355D	367.9	735.8
t=8	Q355D	106.8	213.6
t=4	Q355D	22.6	45.2
合计	Q355D	7671.9	15343.8
M30x200	10.9S高强螺栓	2545.3	5090.6
外表面涂装（㎡）		38.2	76.48

中交第二公路勘察设计研究院有限公司	狮子洋通道工程勘察设计 施 工 图 设 计	K6+418.3 新沙高架桥 边桁节段09设计图	设计	余旺千	复核	袁勤	一审	沈华	二审	韦忠	图号	SZYS/04/02/02/01/ 39

大样A(节段9~节段10)

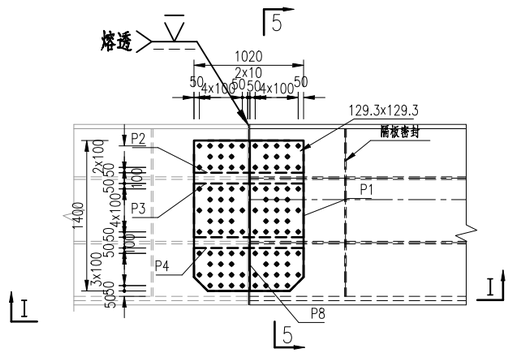

5-5

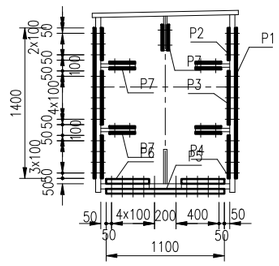

Ⅰ-Ⅰ

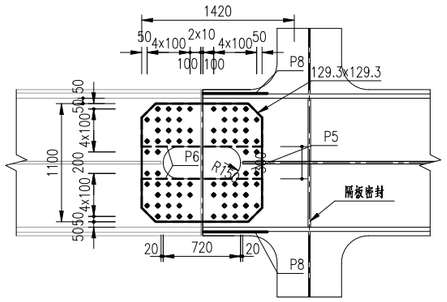

上弦杆顶板、腹板加劲肋拼接

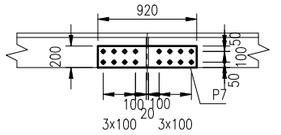

大样C(节段9~节段10)

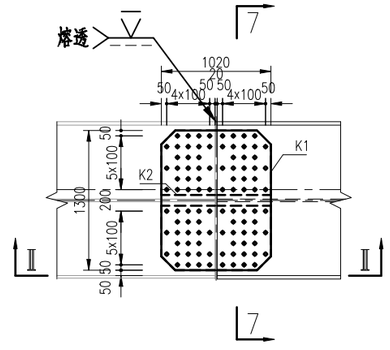

7-7

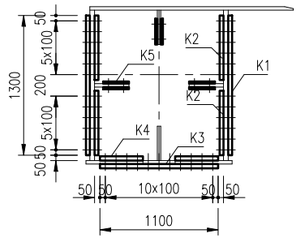

Ⅳ-Ⅳ

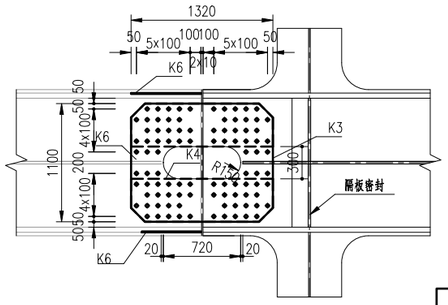

下弦杆顶板、腹板加劲肋拼接

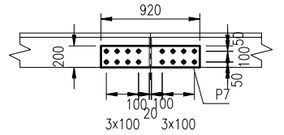

注:

1、本图尺寸均以mm计。

2、未注明的板件裁切边距M30螺栓不小50mm，M24螺栓不小40mm。

3、图中未注明的过焊孔圆弧切角半径为35mm。

4、图中未注明焊缝详见《钢梁焊缝及细节设计图》。

符号:

⊕ —— M30螺栓，开孔直径33mm

⊗ —— M24螺栓，开孔直径26mm

大样B(节段9~节段10)

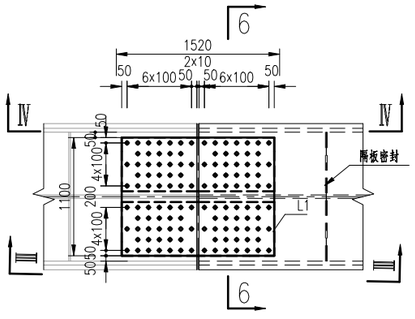

6-6

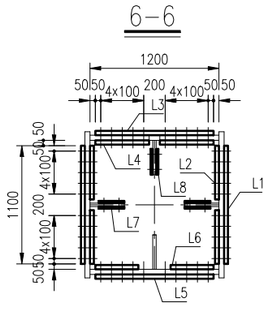

腹杆腹板加劲肋拼接

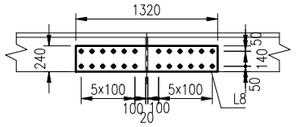

腹杆顶加劲肋拼接

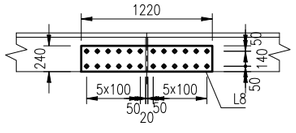

Ⅲ-Ⅲ

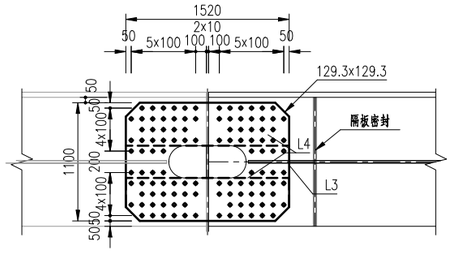

Ⅳ-Ⅳ

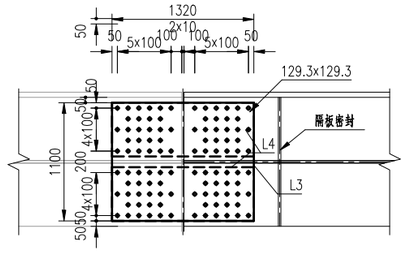

节段9~节段10拼接数量表

名称	编号	材质	规格	数量	单件重	共重(kg)	备注
上弦杆拼接	P1	Q355D	□1020×1400×24	2	269.4	538.8	
	P2		□1020×300×24	2	58.4	116.8	
	P3		□1020×500×24	2	96.1	192.2	
	P4		□1020×400×24	2	77.2	154.4	
	P5		□1420×1100×28	1	342.9	342.9	
	P6		□1420×400×28	2	125.3	250.6	
	P7		□920×200×20	10	28.3	283	
	P8		□600×1800×12	2	101.7	203.4	填板
	P9		□700×1100×4	1	24.2	24.2	填板
	M30高强螺栓	10.9S	M30x200	380	1.94	737.2	
下弦杆拼接	K1	Q355D	□1020×1300×24	2	250.6	501.2	
	K2		□1020×600×24	4	114.9	459.6	
	K3		□1320×1100×36	1	409.8	409.8	
	K4		□1320×400×36	2	149.8	299.6	
	K5		□920×200×20	6	28.3	169.8	
	K6		□500×1700×8	2	53.4	106.8	填板
	K7		□650×1100×4	1	22.6	22.6	填板
	M30高强螺栓	10.9S	M30x200	344	1.94	667.4	
腹杆拼接	L1	Q355D	□1520×1100×24	2	314.6	629.2	
	L2		□1520×500×24	4	143.2	572.8	
	L3		□1320×1100×28	1	318.7	318.7	
	L4		□1320×500×28	2	145.1	290.2	
	L5		□1520×1100×44	1	576.8	576.8	
	L6		□1520×240×44	2	124.3	248.6	
	L7		□1220×240×24	4	54.6	218.4	
	L8		□1320×240×24	2	60.3	120.6	
	M30高强螺栓	10.9S	M30x200	540	1.94	1047.6	

中交第二公路勘察设计研究院有限公司	狮子洋通道工程勘察设计 施 工 图 设 计	K6+418.3 新沙高架桥 边桁节段10设计图	设计	余汪千	复核	袁勤	一审	沈华	二审	韦忠	图号	SZYS/04/02/02/01/ 40

节段10材料数量表

名称	编号	材质	规格	数量	单件重	共重（kg）	备注
上弦顶板	N11a	Q355D	t=20mm,A=11.85m2	1	1860.5	1860.5	
	N11b	Q355D	t=20mm,A=10.39m2	1	1631.8	1631.8	
上弦底板	N12a	Q355D	□7900×1200×20	1	1488.4	1488.4	
	N12b	Q355D	□7100×1200×20	1	1337.6	1337.6	
上弦节点板	N13	Q355D	t=40mm,A=20.34m2	2	6385.3	12770.6	
上弦腹板	N14	Q355D	□7300×1648×28	2	2644.2	5288.4	
上弦横隔板	N15	Q355D	□1580×1200×16	3	238.6	715.8	
	N15a	Q355D	□1580×1200×16	2	238.6	477.2	
	N15‘	Q355D	□1657×200×16	3	41.4	124.2	
	N15b	Q355D	□1782×40×4	4	2.2	8.8	
	N15c	Q355D	□600×400×16	4	30.1	120.4	
上弦加劲肋	N16a	Q355D	□7900×240×20	6	298.3	1789.8	
	N16b	Q355D	□7100×240×20	6	266.9	1601.4	
下弦顶板	N21a	Q355D	□7901×1850×24	1	2754.4	2754.4	
	N21b	Q355D	□7101×1850×24	1	2475.6	2475.6	
下弦底板	N22a	Q355D	t=24mm,A=12.53m2	1	2360.7	2360.7	
	N22b	Q355D	t=24mm,A=9.71m2	1	1830.1	1830.1	
下弦节点板	N23	Q355D	t=44mm,A=20.72m2	2	7155.1	14310.2	Z35钢
下弦腹板	N24	Q355D	□7301×1474×32	2	2702.9	5405.8	
下弦横隔板	N25	Q355D	□1450×1200×16	3	218.5	655.5	
	N25a	Q355D	□1450×1200×16	2	218.5	437	
	N25’	Q355D	□1657×200×16	3	41.4	124.2	
下弦加劲肋	N26a	Q355D	□7901×240×20	4	298.3	1193.2	
	N26b	Q355D	□7101×240×20	4	266.9	1067.6	
	N26c	Q355D	□15002×170×14	1	280.2	280.2	
斜腹杆	N31	Q355D	□11770×1200×36	1	3990.3	3990.3	
	N31a	Q355D	□12070×1200×36	1	4092	4092	
	N32	Q355D	□7770×1360×36	2	2987.1	5974.2	
	N33	Q355D	□7770×320×32	2	625.5	1251	
	N33a	Q355D	□10370×320×32	1	834	834	
	N33b	Q355D	□10670×320×32	1	856.6	856.6	
	N34	Q355D	□1200×1200×16	3	180.9	542.7	
	N41	Q355D	□3798×900×36	2	966.5	1933	
	N42	Q355D	□6098×1200×32	1	1838.8	1838.8	
	N43	Q355D	□5398×240×24	2	244.9	489.8	
节点板加劲	N51	Q355D	□6051×1200×36	1	2051.7	2051.7	
	N51a	Q355D	□6051×1200×36	1	2051.7	2051.7	
	N52	Q355D	□3851×1360×36	2	1480.8	2961.6	
	N53	Q355D	□3851×320×32	2	309	618	
	N53a	Q355D	□4651×320×32	1	374.3	374.3	
	N53b	Q355D	□4651×320×32	1	374.3	374.3	
	N54	Q355D	□1200×1200×16	2	180.9	361.8	
	N55	Q355D	□2300×320×32	2	185.9	371.8	
	N56	Q355D	□3600×320×32	4	288.9	1155.6	
横梁接头	N61	Q355D	□1580×610×14	3	105.5	316.5	
	N61a	Q355D	□1580×622×14	2	107.7	215.4	
	N62	Q355D	t=24mm,A=0.47m2	3	87.8	263.4	
	N62a	Q355D	t=24mm,A=0.47m2	2	89.3	178.6	
	N63	Q355D	□1450×606×14	3	96.7	290.1	
	N63a	Q355D	□1450×618×14	2	98.9	197.8	
小计						95694.4	
焊缝重1.5%						1435.4	
合计						97129.8	

节段10材料数量汇总表

规格（mm）	材质	单个合计	全桥共2个
t=44	Q355D	14310.2	28620.4
t=40	Q355D	12770.6	25541.2
t=36	Q355D	23054.5	46109.0
t=32	Q355D	13080.2	26160.4
t=28	Q355D	5288.4	10576.8
t=24	Q355D	10352.6	20705.2
t=20	Q355D	11970.3	23940.6
t=16	Q355D	3558.8	7117.6
t=14	Q355D	1300	2600.0
t=4	Q355D	8.8	17.6
焊缝重（1.5%）		1435.4	2870.8
	Q355D	97129.8	194259.6
内表面涂装（㎡）		344.2	688.4
外表面涂装（㎡）		478.7	957.4

节段9~节段10拼接数量汇总表

规格（mm）	材质	单个合计	全桥共2个
t=44	Q355D	825.4	1650.8
t=36	Q355D	709.4	1418.8
t=28	Q355D	1202.4	2404.8
t=24	Q355D	3504	7008
t=20	Q355D	452.8	905.6
t=12	Q355D	203.4	406.8
t=8	Q355D	106.8	213.6
t=4	Q355D	46.8	93.6
合计	Q355D	7051.0	14102
M30x200	10.9S高强螺栓	2452.2	4904.4
外表面涂装（㎡）		37.2	74.4

中交第二公路勘察设计研究院有限公司	狮子洋通道工程勘察设计 施 工 图 设 计	K6+418.3 新沙高架桥 边桁节段10设计图	设计	余汪千	复核	袁勤	一审	张华	二审	李忠	图号	SZYS/04/02/02/01/ 40

大样A（节段10~节段11）

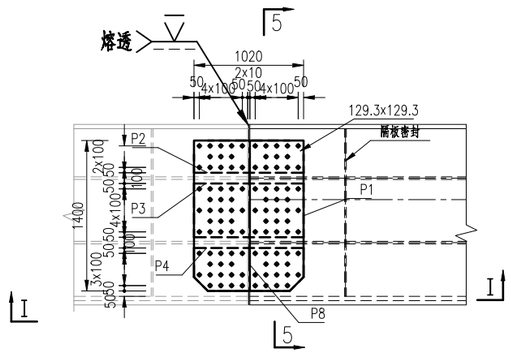

5-5

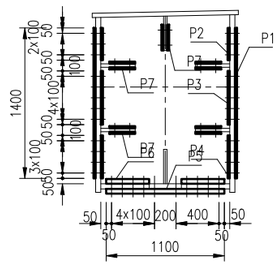

大样C（节段10~节段11）

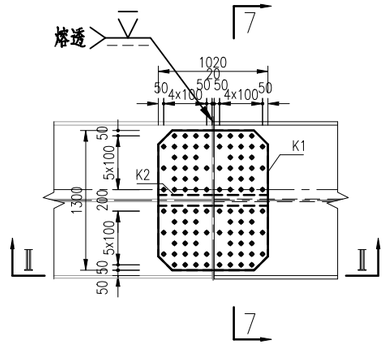

7-7

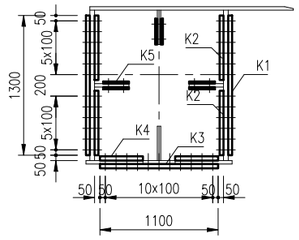

注：

1、本图尺寸均以mm计。

2、未注明的板件裁切边距M30螺栓不小50mm，M24螺栓不小40mm。

3、图中未注明的过焊孔圆弧切角半径为35mm。

4、图中未注明焊缝详见《钢梁焊缝及细节设计图》。

符号：

⊕ —— M30螺栓，开孔直径33mm

⊗ —— M24螺栓，开孔直径26mm

Ⅰ－Ⅰ

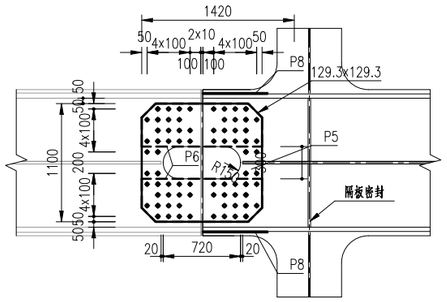

上弦杆顶板、腹板加劲肋拼接

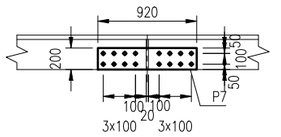

Ⅳ－Ⅳ

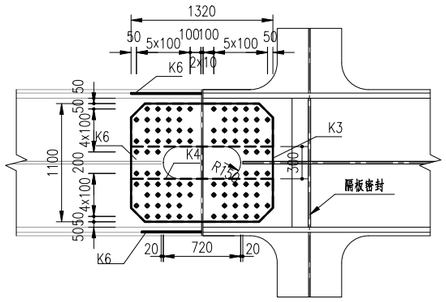

下弦杆顶板、腹板加劲肋拼接

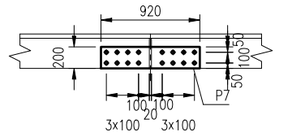

大样B（节段10~节段11）

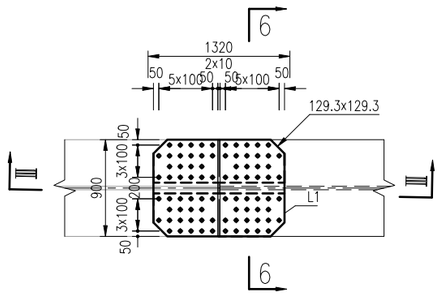

6-6

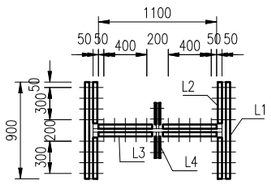

腹杆腹板加劲肋拼接

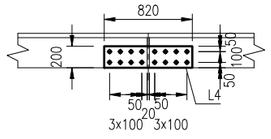

Ⅲ－Ⅲ

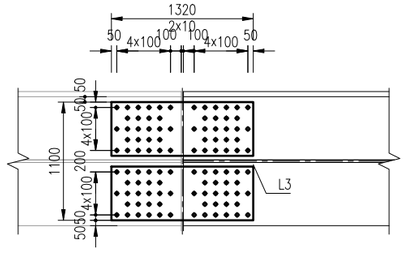

节段10~节段11拼接数量表

名称	编号	材质	规格	数量	单件重	共重（kg）	备注
上弦杆拼接	P1	Q355D	□1020×1400×24	2	269.4	538.8	
	P2		□1020×300×24	2	58.4	116.8	
	P3		□1020×500×24	2	96.1	192.2	
	P4		□1020×400×24	2	77.2	154.4	
	P5		□1420×1100×28	1	342.9	342.9	
	P6		□1420×400×28	2	125.3	250.6	
	P7		□920×200×20	10	28.3	283	
	P8		□600×1800×12	2	101.7	203.4	填板
	P9		□700×1100×4	1	24.2	24.2	填板
	M30高强螺栓	10.9S	M30x200	380	1.94	737.2	
下弦杆拼接	K1	Q355D	□1020×1300×24	2	250.6	501.2	
	K2		□1020×600×24	4	114.9	459.6	
	K3		□1320×1100×36	1	409.8	409.8	
	K4		□1320×400×36	2	149.8	299.6	
	K5		□920×200×20	6	28.3	169.8	
	K6		□500×1700×8	2	53.4	106.8	填板
	K7		□650×1100×4	1	22.6	22.6	填板
	M30高强螺栓	10.9S	M30x200	344	1.94	667.4	
腹杆拼接	L1	Q355D	□1320×900×28	2	261.6	523.2	
	L2		□1320×400×28	4	116.5	466	
	L3		□1320×500×28	4	145.1	580.4	
	L4		□820×200×20	4	25.1	100.4	
	M30高强螺栓	10.9S	M30x200	507	1.94	983.6	

中交第二公路勘察设计研究院有限公司	狮子洋通道工程勘察设计 施 工 图 设 计	K6+418.3 新沙高架桥 边桁节段11设计图	设计	余汪千	复核	袁勤	一审	张华	二审	李忠	图号	SZYS/04/02/02/01/ 41

72500115576178

节段11材料数量表

名称	编号	材质	规格	数量	单件重	共重（kg）	备注
上弦顶板	N11a	Q355D	t=20mm,A=11.85m2	1	1860.5	1860.5	
	N11b	Q355D	t=20mm,A=10.39m2	1	1631.8	1631.8	
上弦底板	N12a	Q355D	□7900×1200×20	1	1488.4	1488.4	
	N12b	Q355D	□7100×1200×20	1	1337.6	1337.6	
上弦节点板	N13	Q355D	t=40mm,A=19.2m2	2	6030.1	12060.2	
上弦腹板	N14	Q355D	□7300×1648×28	2	2644.2	5288.4	
上弦横隔板	N15	Q355D	□1580×1200×16	3	238.6	715.8	
	N15a	Q355D	□1580×1200×16	2	238.6	477.2	
	N15 ‘	Q355D	□1657×200×16	3	41.4	124.2	
	N15b	Q355D	□1782×40×4	4	2.2	8.8	
	N15c	Q355D	□600×400×16	4	30.1	120.4	
上弦加劲肋	N16a	Q355D	□7900×240×20	6	298.3	1789.8	
	N16b	Q355D	□7100×240×20	6	266.9	1601.4	
下弦顶板	N21a	Q355D	□7901×1850×24	1	2754.4	2754.4	
	N21b	Q355D	□7101×1850×24	1	2475.6	2475.6	
下弦底板	N22a	Q355D	t=24mm,A=12.53m2	1	2360.7	2360.7	
	N22b	Q355D	t=24mm,A=9.71m2	1	1830.1	1830.1	
下弦节点板	N23	Q355D	t=44mm,A=18.39m2	2	6350.5	12701	Z35钢
下弦腹板	N24	Q355D	□7301×1474×32	2	2702.9	5405.8	
下弦横隔板	N25	Q355D	□1450×1200×16	3	218.5	655.5	
	N25a	Q355D	□1450×1200×16	2	218.5	437	
	N25’	Q355D	□1657×200×16	3	41.4	124.2	
下弦加劲肋	N26a	Q355D	□7901×240×20	4	298.3	1193.2	
	N26b	Q355D	□7101×240×20	4	266.9	1067.6	
	N26c	Q355D	□15002×170×14	1	280.2	280.2	
斜腹杆	N31	Q355D	□7651×900×36	2	1947.1	3894.2	
	N32	Q355D	□12551×1200×32	1	3783.1	3783.1	
	N33	Q355D	□11151×240×24	2	504.9	1009.8	
	N41	Q355D	□3752×900×36	2	955.2	1910.4	
	N42	Q355D	□6052×1200×32	1	1823.7	1823.7	
	N43	Q355D	□5352×240×24	2	241.2	482.4	
	N51	Q355D	□3789×900×36	2	963.7	1927.4	
	N52	Q355D	□6389×1200×32	1	1926.7	1926.7	
	N53	Q355D	□5689×240×24	2	258.1	516.2	
节点板加劲	N54	Q355D	□1123×1200×20	1	212	212	
	N55	Q355D	□1089×1200×20	2	205.7	411.4	
横梁接头	N61	Q355D	□1580×610×14	3	105.5	316.5	
	N61a	Q355D	□1580×622×14	2	107.7	215.4	
	N62	Q355D	t=24mm,A=0.47m2	3	87.8	263.4	
	N62a	Q355D	t=24mm,A=0.47m2	2	89.3	178.6	
	N63	Q355D	□1450×606×14	3	96.7	290.1	
	N63a	Q355D	□1450×618×14	2	98.9	197.8	
小计						79148.9	
焊缝重1.5%						1187.2	
合计						80336.1	

节段11材料数量汇总表

规格（mm）	材质	单个合计	全桥共2个
t=44	Q355D	12701	25402
t=40	Q355D	12060.2	24120.4
t=36	Q355D	7732	15464
t=32	Q355D	12939.3	25878.6
t=28	Q355D	5288.4	10576.8
t=24	Q355D	11871.2	23742.4
t=20	Q355D	12593.7	25187.4
t=16	Q355D	2654.3	5308.6
t=14	Q355D	1300	2600
t=4	Q355D	8.8	17.6
焊缝重（1.5%）		1187.2	2374.467
	Q355D	80336.1	160672.267
内表面涂装（㎡）		276.0	552
外表面涂装（㎡）		433.1	866.2

节段10~节段11拼接数量汇总表

规格（mm）	材质	单个合计	全桥共2个
t=36	Q355D	709.4	1418.8
t=28	Q355D	2163.1	4326.2
t=24	Q355D	1963	3926
t=20	Q355D	553.2	1106.4
t=12	Q355D	203.4	406.8
t=8	Q355D	106.8	213.6
t=4	Q355D	46.8	93.6
合计	Q355D	5745.7	11491.4
M30x200	10.9S高强螺栓	2388.2	4776.4
外表面涂装（㎡）		31.6	63.28

中交第二公路勘察设计研究院有限公司	狮子洋通道工程勘察设计 施 工 图 设 计	K6+418.3 新沙高架桥 边桁节段11设计图	设计	余汪千	复核	袁勤	一审	张华	二审	李忠	图号	SZYS/04/02/02/01/ 41

7 2350115 937410

大样A（节段11~节段12）

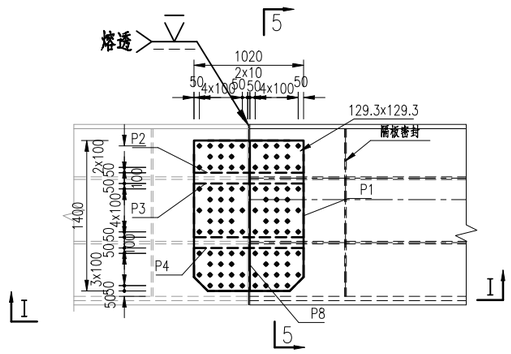

5-5

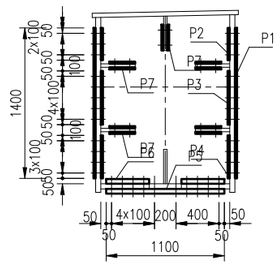

大样C（节段11~节段12）

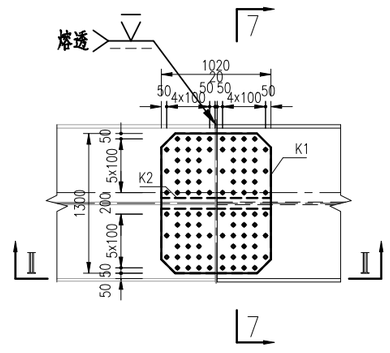

7-7

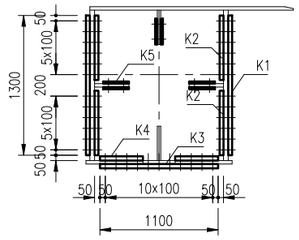

注：

1、本图尺寸均以mm计。

2、未注明的板件裁切边距M30螺栓不小50mm，M24螺栓不小40mm。

3、图中未注明的过焊孔圆弧切角半径为35mm。

4、图中未注明焊缝详见《钢梁焊缝及细节设计图》。

符号：

—— M30螺栓，开孔直径33mm

—— M24螺栓，开孔直径26mm

Ⅰ－Ⅰ

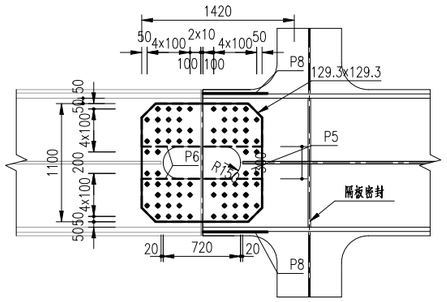

上弦杆顶板、腹板加劲肋拼接

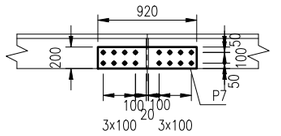

Ⅳ－Ⅳ

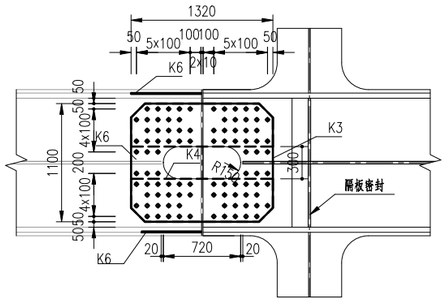

下弦杆顶板、腹板加劲肋拼接

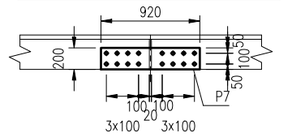

节段11~节段12拼接数量表

名称	编号	材质	规格	数量	单件重	共重（kg）	备注
上弦杆拼接	P1	Q355D	□1020×1400×24	2	269.4	538.8	
	P2		□1020×300×24	2	58.4	116.8	
	P3		□1020×500×24	2	96.1	192.2	
	P4		□1020×400×24	2	77.2	154.4	
	P5		□1420×1100×28	1	342.9	342.9	
	P6		□1420×400×28	2	125.3	250.6	
	P7		□920×200×20	10	28.3	283	
	P8		□600×1800×12	2	101.7	203.4	填板
	P9		□700×1100×4	1	24.2	24.2	填板
	M30高强螺栓	10.9S	M30x200	380	1.94	737.2	
下弦杆拼接	K1	Q355D	□1020×1300×24	2	250.6	501.2	
	K2		□1020×600×24	4	114.9	459.6	
	K3		□1320×1100×36	1	409.8	409.8	
	K4		□1320×400×36	2	149.8	299.6	
	K5		□920×200×20	6	28.3	169.8	
	K6		□500×1700×8	2	53.4	106.8	填板
	K7		□650×1100×4	1	22.6	22.6	填板
	M30高强螺栓	10.9S	M30x200	344	1.94	667.4	
腹杆拼接	L1	Q355D	□1320×900×28	2	261.6	523.2	
	L2		□1320×400×28	4	116.5	466	
	L3		□1320×500×28	4	145.1	580.4	
	L4		□820×200×20	4	25.1	100.4	
	M30高强螺栓	10.9S	M30x200	507	1.94	983.6	

大样B（节段11~节段12）

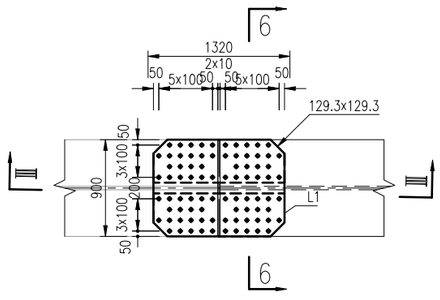

6-6

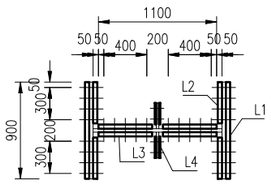

腹杆腹板加劲肋拼接

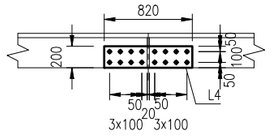

Ⅲ－Ⅲ

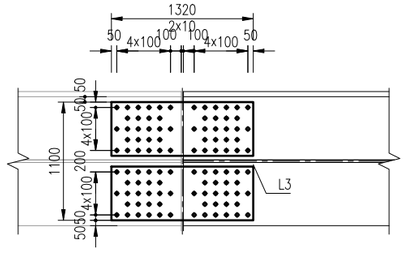

中交第二公路勘察设计研究院有限公司	狮子洋通道工程勘察设计 施 工 图 设 计	K6+418.3 新沙高架桥 边桁节段12设计图	设计	余汪千	复核	袁勤	一审	张华	二审	李忠	图号	SZYS/04/02/02/01/ 42

节段12材料数量表

名称	编号	材质	规格	数量	单件重	共重（kg）	备注
上弦顶板	N11a	Q355D	t=20mm,A=11.85m2	1	1860.5	1860.5	
	N11b	Q355D	t=20mm,A=10.39m2	1	1631.8	1631.8	
上弦底板	N12a	Q355D	□7900×1200×20	1	1488.4	1488.4	
	N12b	Q355D	□7100×1200×20	1	1337.6	1337.6	
上弦节点板	N13	Q355D	t=40mm,A=19.2m2	2	6028.7	12057.4	
上弦腹板	N14	Q355D	□7300×1648×28	2	2644.2	5288.4	
上弦横隔板	N15	Q355D	□1580×1200×16	3	238.6	715.8	
	N15a	Q355D	□1580×1200×16	2	238.6	477.2	
	N15 ‘	Q355D	□1657×200×16	3	41.4	124.2	
	N15b	Q355D	□1782×40×4	4	2.2	8.8	
	N15c	Q355D	□600×400×16	4	30.1	120.4	
上弦加劲肋	N16a	Q355D	□7900×240×20	6	298.3	1789.8	
	N16b	Q355D	□7100×240×20	6	266.9	1601.4	
下弦顶板	N21a	Q355D	□7901×1850×24	1	2754.4	2754.4	
	N21b	Q355D	□7101×1850×24	1	2475.6	2475.6	
下弦底板	N22a	Q355D	t=24mm,A=12.53m2	1	2360.7	2360.7	
	N22b	Q355D	t=24mm,A=9.71m2	1	1830.1	1830.1	
下弦节点板	N23	Q355D	t=44mm,A=18.39m2	2	6351.6	12703.2	Z35钢
下弦腹板	N24	Q355D	□7301×1474×32	2	2702.9	5405.8	
下弦横隔板	N25	Q355D	□1450×1200×16	3	218.5	655.5	
	N25a	Q355D	□1450×1200×16	2	218.5	437	
	N25’	Q355D	□1657×200×16	3	41.4	124.2	
下弦加劲肋	N26a	Q355D	□7901×240×20	4	298.3	1193.2	
	N26b	Q355D	□7101×240×20	4	266.9	1067.6	
	N26c	Q355D	□15002×170×14	1	280.2	280.2	
斜腹杆	N31	Q355D	□7548×900×36	2	1918.9	3837.8	
	N32	Q355D	□12448×1200×32	1	3752.9	3752.9	
	N33	Q355D	□11048×240×24	2	499.3	998.6	
	N41	Q355D	□3714×900×36	2	943.9	1887.8	
	N42	Q355D	□6014×1200×32	1	1813.7	1813.7	
	N43	Q355D	□5314×240×24	2	241.2	482.4	
	N51	Q355D	□3752×900×36	2	955.2	1910.4	
	N52	Q355D	□6352×1200×32	1	1914.1	1914.1	
	N53	Q355D	□5652×240×24	2	256.2	512.4	
节点板加劲	N54	Q355D	□1103×1200×20	1	207.2	207.2	
	N55	Q355D	□1071×1200×20	1	202.5	202.5	
横梁接头	N61	Q355D	□1580×610×14	3	105.5	316.5	
	N61a	Q355D	□1580×622×14	2	107.7	215.4	
	N62	Q355D	t=24mm,A=0.47m2	3	87.8	263.4	
	N62a	Q355D	t=24mm,A=0.47m2	2	89.3	178.6	
	N63	Q355D	□1450×606×14	3	96.7	290.1	
	N63a	Q355D	□1450×618×14	2	98.9	197.8	
小计						78770.8	
焊缝重1.5%						1181.6	
合计						79952.4	

节段12材料数量汇总表

规格（mm）	材质	单个合计	全桥共2个
t=44	Q355D	12703.2	25406.4
t=40	Q355D	12057.4	24114.8
t=36	Q355D	7636	15272
t=32	Q355D	12886.5	25773
t=28	Q355D	5288.4	10576.8
t=24	Q355D	11856.2	23712.4
t=20	Q355D	12380	24760
t=16	Q355D	2654.3	5308.6
t=14	Q355D	1300	2600
t=4	Q355D	8.8	17.6
焊缝重（1.5%）		1181.6	2363.2
	Q355D	79952.4	159904.8
内表面涂装（m²）		274.2	548.4
外表面涂装（m²）		431.0	862

节段11～节段12拼接数量汇总表

规格（mm）	材质	单个合计	全桥共2个
t=36	Q355D	709.4	1418.8
t=28	Q355D	2163.1	4326.2
t=24	Q355D	1963	3926
t=20	Q355D	553.2	1106.4
t=12	Q355D	203.4	406.8
t=8	Q355D	106.8	213.6
t=4	Q355D	46.8	93.6
合计	Q355D	5745.7	11491.4
M30x200	10.9S高强螺栓	2388.2	4776.4
外表面涂装（m²）		31.6	63.28

中交第二公路勘察设计研究院有限公司	狮子洋通道工程勘察设计 施 工 图 设 计	K6+418.3 新沙高架桥 边桁节段12设计图	设计	余汪千	复核	袁勤	一审	沈华	二审	李忠	图号	SZYS/04/02/02/01/ 42

大样A（节段12~节段13）

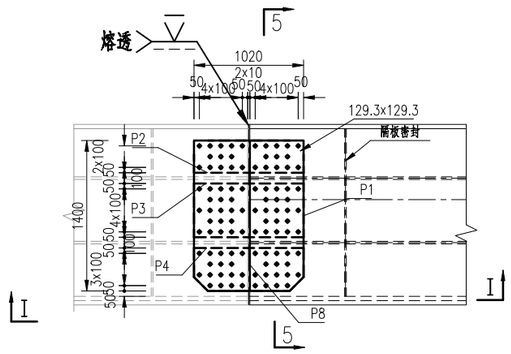

5-5

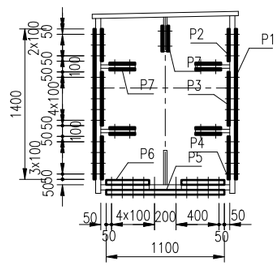

大样C（节段12~节段13）

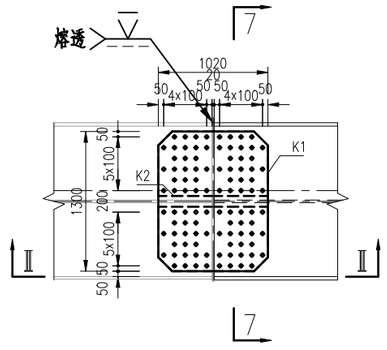

7-7

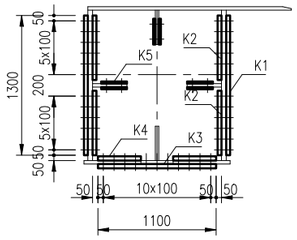

注：

1、本图尺寸均以mm计。

2、未注明的板件裁切边距M30螺栓不小50mm，M24螺栓不小40mm。

3、图中未注明的过焊孔圆弧切角半径为35mm。

4、图中未注明焊缝详见《钢梁焊缝及细节设计图》。

符号：

⊕ —— M30螺栓，开孔直径33mm

⊗ —— M24螺栓，开孔直径26mm

I－I

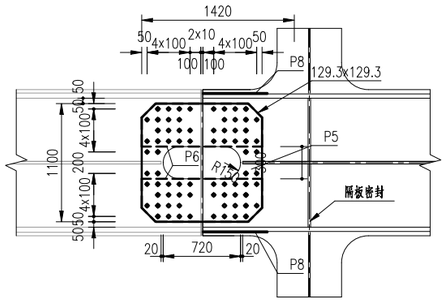

上弦杆顶板、腹板加劲肋拼接

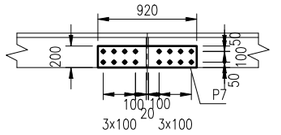

Ⅳ－Ⅳ

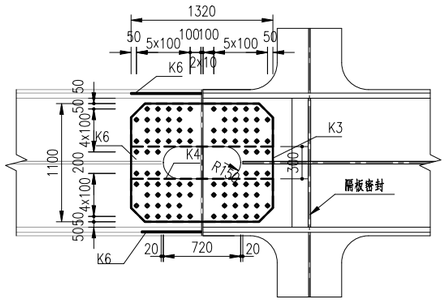

下弦杆顶板、腹板加劲肋拼接

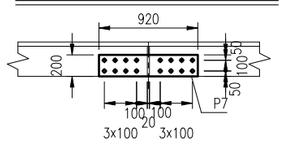

大样B（节段12~节段13）

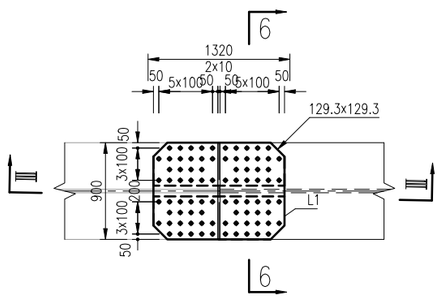

6-6

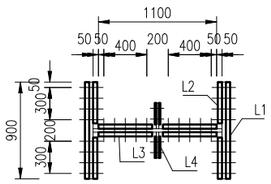

腹杆腹板加劲肋拼接

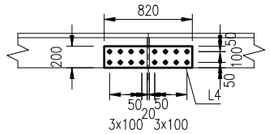

Ⅲ－Ⅲ

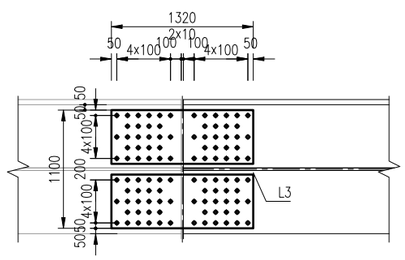

节段12~节段13拼接数量表

名称	编号	材质	规格	数量	单件重	共重（kg）	备注
上弦杆拼接	P1	Q355D	□1020×1400×24	2	269.4	538.8	
	P2		□1020×300×24	2	58.4	116.8	
	P3		□1020×500×24	2	96.1	192.2	
	P4		□1020×400×24	2	77.2	154.4	
	P5		□1420×1100×28	1	342.9	342.9	
	P6		□1420×400×28	2	125.3	250.6	
	P7		□920×200×20	10	28.3	283	
	P8		□600×1800×12	2	101.7	203.4	填板
	P9		□700×1100×4	1	24.2	24.2	填板
	M30高强螺栓	10.9S	M30x200	380	1.94	737.2	
下弦杆拼接	K1	Q355D	□1020×1300×24	2	250.6	501.2	
	K2		□1020×600×24	4	114.9	459.6	
	K3		□1320×1100×36	1	409.8	409.8	
	K4		□1320×400×36	2	149.8	299.6	
	K5		□920×200×20	6	28.3	169.8	
	K6		□500×1700×8	2	53.4	106.8	填板
	K7		□650×1100×4	1	22.6	22.6	填板
	M30高强螺栓	10.9S	M30x200	344	1.94	667.4	
腹杆拼接	L1	Q355D	□1320×900×28	2	261.6	523.2	
	L2		□1320×400×28	4	116.5	466	
	L3		□1320×500×28	4	145.1	580.4	
	L4		□820×200×20	4	25.1	100.4	
	M30高强螺栓	10.9S	M30x200	507	1.94	983.6	

中交第二公路勘察设计研究院有限公司	狮子洋通道工程勘察设计 施 工 图 设 计	K6+418.3 新沙高架桥 边桁节段13设计图	设计	余汪千	复核	袁勤	一审	沈华	二审	李忠	图号	SZYS/04/02/02/01/ 43

节段13材料数量表

名称	编号	材质	规格	数量	单件重	共重（kg）	备注
上弦顶板	N11a	Q355D	t=20mm,A=11.85m2	1	1860.5	1860.5	
	N11b	Q355D	t=20mm,A=10.39m2	1	1631.8	1631.8	
上弦底板	N12a	Q355D	□7900×1200×20	1	1488.4	1488.4	
	N12b	Q355D	□7100×1200×20	1	1337.6	1337.6	
上弦节点板	N13	Q355D	t=40mm,A=20.32m2	2	6382	12764	
上弦腹板	N14	Q355D	□7300×1648×28	2	2644.2	5288.4	
上弦横隔板	N15	Q355D	□1580×1200×16	3	238.6	715.8	
	N15a	Q355D	□1580×1200×16	2	238.6	477.2	
	N15 ‘	Q355D	□1657×200×16	3	41.4	124.2	
	N15b	Q355D	□1782×40×4	4	2.2	8.8	
	N15c	Q355D	□600×400×16	4	30.1	120.4	
上弦加劲肋	N16a	Q355D	□7900×240×20	6	298.3	1789.8	
	N16b	Q355D	□7100×240×20	6	266.9	1601.4	
下弦顶板	N21a	Q355D	□7901×1850×24	1	2754.4	2754.4	
	N21b	Q355D	□7101×1850×24	1	2475.6	2475.6	
下弦底板	N22a	Q355D	t=24mm,A=12.53m2	1	2360.7	2360.7	
	N22b	Q355D	t=24mm,A=9.71m2	1	1830.1	1830.1	
下弦节点板	N23	Q355D	t=44mm,A=18.38m2	2	6349.4	12698.8	Z35钢
下弦腹板	N24	Q355D	□7301×1474×32	2	2702.9	5405.8	
下弦横隔板	N25	Q355D	□1450×1200×16	3	218.5	655.5	
	N25a	Q355D	□1450×1200×16	2	218.5	437	
	N25’	Q355D	□1657×200×16	3	41.4	124.2	
下弦加劲肋	N26a	Q355D	□7901×240×20	4	298.3	1193.2	
	N26b	Q355D	□7101×240×20	4	266.9	1067.6	
	N26c	Q355D	□15002×170×14	1	280.2	280.2	
斜腹杆	N31	Q355D	□7458×900×36	2	1896.2	3792.4	
	N32	Q355D	□12358×1200×32	1	3725.3	3725.3	
	N33	Q355D	□10958×240×24	2	495.5	991	
	N41	Q355D	□5482×1200×36	1	1859.5	1859.5	
	N41a	Q355D	□5782×1200×36	1	1961.2	1961.2	
	N42	Q355D	□3682×1360×36	2	1415.8	2831.6	
	N43	Q355D	□3682×320×32	2	296.4	592.8	
	N43a	Q355D	□4782×320×32	1	384.3	384.3	
	N43b	Q355D	□5082×320×32	1	409.5	409.5	
	N44	Q355D	□1200×1200×16	3	180.9	542.7	
	N51	Q355D	□3714×900×36	2	943.9	1887.8	
	N52	Q355D	□6314×1200×32	1	1904.1	1904.1	
	N53	Q355D	□4914×240×24	2	222.3	444.6	
节点板加劲	N54	Q355D	□2300×320×32	2	185.9	371.8	
	N55	Q355D	□1056×1200×20	1	199.4	199.4	
横梁接头	N61	Q355D	□1580×610×14	3	105.5	316.5	
	N61a	Q355D	□1580×622×14	2	107.7	215.4	
	N62	Q355D	t=24mm,A=0.47m2	3	87.8	263.4	
	N62a	Q355D	t=24mm,A=0.47m2	2	89.3	178.6	
	N63	Q355D	□1450×606×14	3	96.7	290.1	
	N63a	Q355D	□1450×618×14	2	98.9	197.8	
小计						83851.2	
焊缝重1.5%						1257.8	
合计						85109.0	

节段13材料数量汇总表

规格（mm）	材质	单个合计	全桥共2个
t=44	Q355D	12698.8	25397.6
t=40	Q355D	12764	25528
t=36	Q355D	12332.5	24665
t=32	Q355D	12793.6	25587.2
t=28	Q355D	5288.4	10576.8
t=24	Q355D	11298.4	22596.8
t=20	Q355D	12169.7	24339.4
t=16	Q355D	3197	6394
t=14	Q355D	1300	2600
t=4	Q355D	8.8	17.6
焊缝重（1.5%）		1257.8	2515.536
	Q355D	85109.0	170217.936
内表面涂装（m²）		283.2	566.4
外表面涂装（m²）		459.0	918

节段12~节段13拼接数量汇总表

规格（mm）	材质	单个合计	全桥共2个
t=36	Q355D	709.4	1418.8
t=28	Q355D	2163.1	4326.2
t=24	Q355D	1963	3926
t=20	Q355D	553.2	1106.4
t=12	Q355D	203.4	406.8
t=8	Q355D	106.8	213.6
t=4	Q355D	46.8	93.6
合计	Q355D	5745.7	11491.4
M30x200	10.9S高强螺栓	2388.2	4776.4
外表面涂装（m²）		31.6	63.28

中交第二公路勘察设计研究院有限公司	狮子洋通道工程勘察设计 施 工 图 设 计	K6+418.3 新沙高架桥 边桁节段13设计图	设计	余汪千	复核	袁勤	一审	沈华	二审	王忠	图号	SZYS/04/02/02/01/ 43

22333716107

大样A（节段13~节段14）

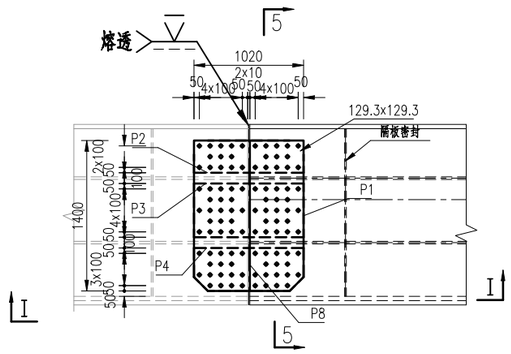

5-5

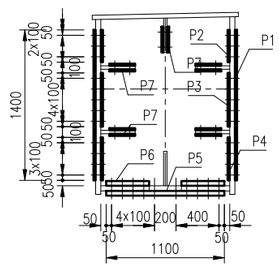

大样C（节段13~节段14）

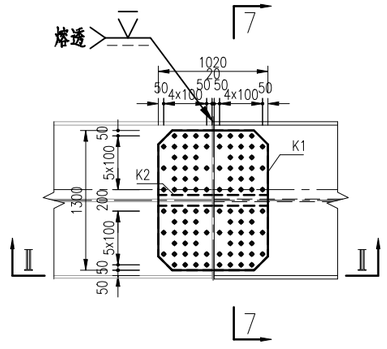

7-7

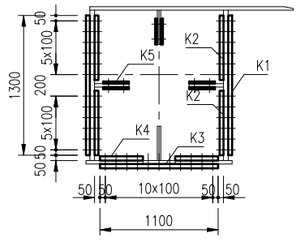

注：

1、本图尺寸均以mm计。

2、未注明的板件裁切边距M30螺栓不小50mm，M24螺栓不小40mm。

3、图中未注明的过焊孔圆弧切角半径为35mm。

4、图中未注明焊缝详见《钢梁焊缝及细节设计图》。

符号：

⊕ —— M30螺栓，开孔直径33mm

⊗ —— M24螺栓，开孔直径26mm

Ⅰ－Ⅰ

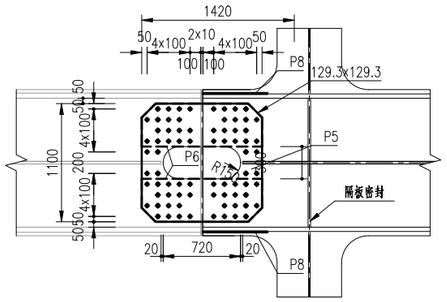

上弦杆顶板、腹板加劲肋拼接

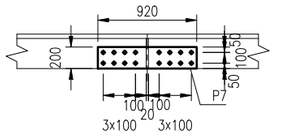

Ⅳ－Ⅳ

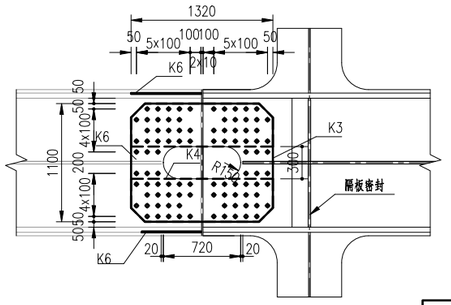

下弦杆顶板、腹板加劲肋拼接

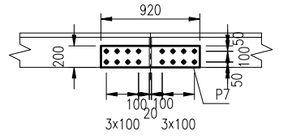

大样B（节段13~节段14）

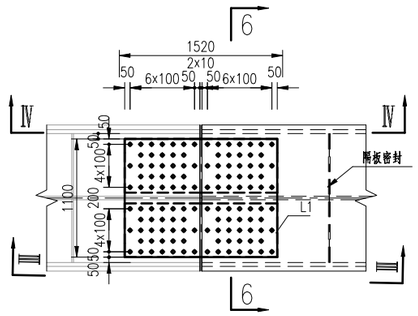

6-6

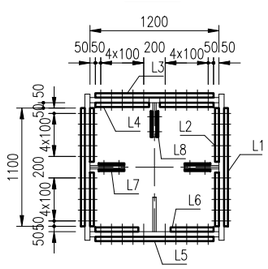

腹杆腹板加劲肋拼接

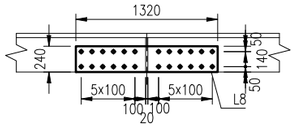

腹杆顶加劲肋拼接

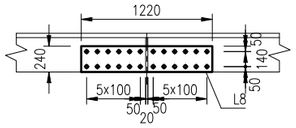

Ⅲ－Ⅲ

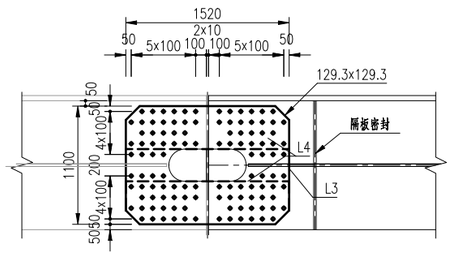

Ⅳ－Ⅳ

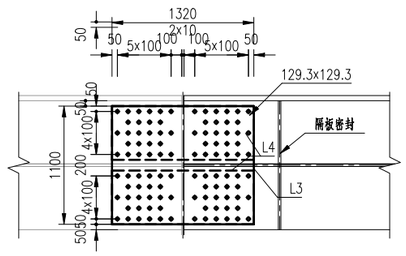

节段13~节段14拼接数量表

名称	编号	材质	规格	数量	单件重	共重(kg)	备注
上弦杆拼接	P1	Q355D	□1020×1400×24	2	269.4	538.8	
	P2		□1020×300×24	2	58.4	116.8	
	P3		□1020×500×24	2	96.1	192.2	
	P4		□1020×400×24	2	77.2	154.4	
	P5		□1420×1100×28	1	342.9	342.9	
	P6		□1420×400×28	2	125.3	250.6	
	P7		□920×200×20	10	28.3	283	
	P8		□600×1800×12	2	101.7	203.4	填板
	P9		□700×1100×4	1	24.2	24.2	填板
	M30高强螺栓	10.9S	M30x200	380	1.94	737.2	
下弦杆拼接	K1	Q355D	□1020×1300×24	2	250.6	501.2	
	K2		□1020×600×24	4	114.9	459.6	
	K3		□1320×1100×36	1	409.8	409.8	
	K4		□1320×400×36	2	149.8	299.6	
	K5		□920×200×20	6	28.3	169.8	
	K6		□500×1700×8	2	53.4	106.8	填板
	K7		□650×1100×4	1	22.6	22.6	填板
	M30高强螺栓	10.9S	M30x200	344	1.94	667.4	
腹杆拼接	L1	Q355D	□1520×1100×24	2	314.6	629.2	
	L2		□1520×500×24	4	143.2	572.8	
	L3		□1320×1100×28	1	318.7	318.7	
	L4		□1320×500×28	2	145.1	290.2	
	L5		□1520×1100×44	1	576.8	576.8	
	L6		□1520×240×44	2	124.3	248.6	
	L7		□1220×240×24	4	54.6	218.4	
	L8		□1320×240×24	2	60.3	120.6	
	M30高强螺栓	10.9S	M30x200	540	1.94	1047.6	

中交第二公路勘察设计研究院有限公司	狮子洋通道工程勘察设计 施 工 图 设 计	K6+418.3 新沙高架桥 边桁节段14设计图	设计	余汪千	复核	袁勤	一审	张华	二审	李忠	图号	SZYS/04/02/02/01/ 44

节段14材料数量表

名称	编号	材质	规格	数量	单件重	共重(kg)	备注
上弦顶板	N11a	Q355D	t=20mm,A=11.85m2	1	1860.5	1860.5	
	N11b	Q355D	t=20mm,A=10.39m2	1	1631.8	1631.8	
上弦底板	N12a	Q355D	□7900×1200×20	1	1488.4	1488.4	
	N12b	Q355D	□7100×1200×20	1	1337.6	1337.6	
上弦节点板	N13	Q355D	t=48mm,A=21.38m2	2	8054.2	16108.4	
上弦腹板	N14	Q355D	□7300×1648×28	2	2644.2	5288.4	
上弦横隔板	N15	Q355D	□1580×1200×16	3	238.6	715.8	
	N15a	Q355D	□1580×1200×16	2	238.6	477.2	
	N15 ‘	Q355D	□1657×200×16	3	41.4	124.2	
	N15b	Q355D	□1782×40×4	4	2.2	8.8	
	N15c	Q355D	□600×400×16	4	30.1	120.4	
上弦加劲肋	N16a	Q355D	□7900×240×20	6	298.3	1789.8	
	N16b	Q355D	□7100×240×20	6	266.9	1601.4	
下弦顶板	N21a	Q355D	□7901×1850×24	1	2754.4	2754.4	
	N21b	Q355D	□7101×1850×24	1	2475.6	2475.6	
下弦底板	N22a	Q355D	t=24mm,A=12.53m2	1	2360.7	2360.7	
	N22b	Q355D	t=24mm,A=9.71m2	1	1830.1	1830.1	
下弦节点板	N23	Q355D	t=44mm,A=20.71m2	2	7154.4	14308.8	Z35钢
下弦腹板	N24	Q355D	□7301×1474×32	2	2702.9	5405.8	
下弦横隔板	N25	Q355D	□1450×1200×16	3	218.5	655.5	
	N25a	Q355D	□1450×1200×16	2	218.5	437	
	N25’	Q355D	□1657×200×16	3	41.4	124.2	
下弦加劲肋	N26a	Q355D	□7901×240×20	4	298.3	1193.2	
	N26b	Q355D	□7101×240×20	4	266.9	1067.6	
	N26c	Q355D	□15002×170×14	1	280.2	280.2	
斜腹杆	N31	Q355D	□11383×1200×36	1	3860.3	3860.3	
	N31a	Q355D	□11683×1200×36	1	3962.1	3962.1	
	N32	Q355D	□7383×1360×36	2	2837.3	5674.6	
	N33	Q355D	□7383×320×32	2	592.8	1185.6	
	N33a	Q355D	□9983×320×32	1	801.3	801.3	
	N33b	Q355D	□10283×320×32	1	826.4	826.4	
	N34	Q355D	□1200×1200×16	3	180.9	542.7	
	N41	Q355D	□5458×1200×36	1	1851	1851	
	N41a	Q355D	□5758×1200×36	1	1952.8	1952.8	
	N42	Q355D	□3658×1360×36	2	1404.5	2809	
	N43	Q355D	□3658×320×32	2	293.9	587.8	
	N43a	Q355D	□4758×320×32	1	381.8	381.8	
	N43b	Q355D	□5058×320×32	1	406.9	406.9	
	N44	Q355D	□1200×1200×16	2	180.9	361.8	
节点板加劲	N51	Q355D	□5883×1200×36	1	1995.2	1995.2	
	N51a	Q355D	□5883×1200×36	1	1995.2	1995.2	
	N52	Q355D	□3683×1360×36	2	1415.8	2831.6	
	N53	Q355D	□3683×320×32	2	296.4	592.8	
	N53a	Q355D	□5183×320×32	1	417	417	
	N53b	Q355D	□5183×320×32	1	417	417	
	N54	Q355D	□1200×1200×16	2	180.9	361.8	
	N55	Q355D	□2300×320×32	4	185.9	743.6	
	N56	Q355D	□2600×320×32	4	208.5	834	
横梁接头	N61	Q355D	□1580×602×14	3	104.4	313.2	
	N61a	Q355D	□1580×622×14	2	107.7	215.4	
	N62	Q355D	t=24mm,A=0.46m2	3	86.7	260.1	
	N62a	Q355D	t=24mm,A=0.47m2	2	88.8	177.6	
	N63	Q355D	□1450×606×14	3	96.7	290.1	
	N63a	Q355D	□1450×618×14	2	98.9	197.8	
小计						102292.3	
焊缝重1.5%						1534.4	
合计						103826.7	

节段14材料数量汇总表

规格(mm)	材质	单个合计	全桥共2个
t=48	Q355D	16108.4	32216.8
t=44	Q355D	14308.8	28617.6
t=36	Q355D	26931.8	53863.6
t=32	Q355D	12600	25200
t=28	Q355D	5288.4	10576.8
t=24	Q355D	9858.5	19717
t=20	Q355D	11970.3	23940.6
t=16	Q355D	3920.6	7841.2
t=14	Q355D	1296.7	2593.4
t=4	Q355D	8.8	17.6
焊缝重(1.5%)		1534.4	3068.769
	Q355D	103826.7	207653.369
内表面涂装(㎡)		350.2	700.4
外表面涂装(㎡)		501.0	1002

节段13~节段14拼接数量汇总表

规格(mm)	材质	单个合计	全桥共2个
t=44	Q355D	825.4	1650.8
t=36	Q355D	709.4	1418.8
t=28	Q355D	1202.4	2404.8
t=24	Q355D	3504	7008
t=20	Q355D	452.8	905.6
t=12	Q355D	203.4	406.8
t=8	Q355D	106.8	213.6
t=4	Q355D	46.8	93.6
合计	Q355D	7051.0	14102
M30x200	10.9S高强螺栓	2452.2	4904.4
外表面涂装(㎡)		37.2	74.4

中交第二公路勘察设计研究院有限公司	狮子洋通道工程勘察设计 施 工 图 设 计	K6+418.3 新沙高架桥 边桁节段14设计图	设计	余汪千	复核	袁勤	一审	沈华	二审	李超	图号	SZYS/04/02/02/01/ 44

大样A（节段14~节段15）

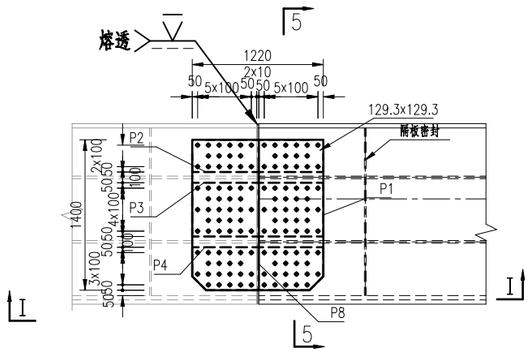

5-5

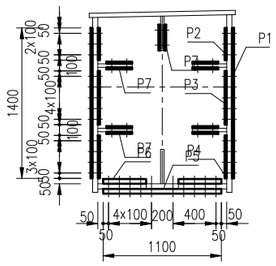

大样C（节段14~节段15）

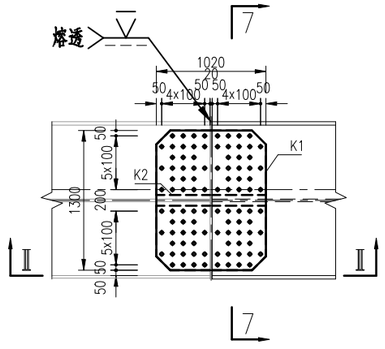

7-7

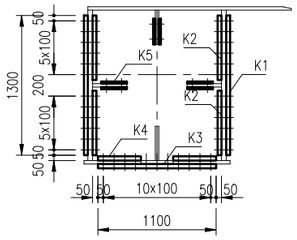

Ⅰ－Ⅰ

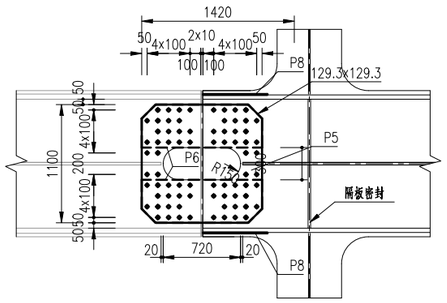

上弦杆顶板、腹板加劲肋拼接

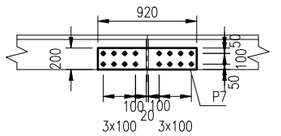

Ⅳ－Ⅳ

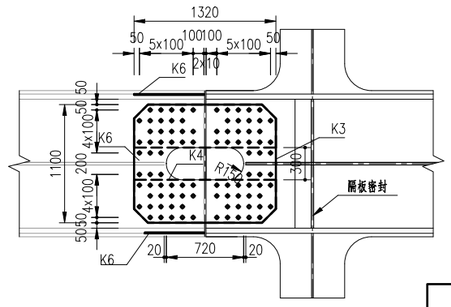

下弦杆顶板、腹板加劲肋拼接

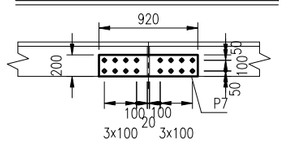

注：

1、本图尺寸均以mm计。

2、未注明的板件裁切边距M30螺栓不小50mm，M24螺栓不小40mm。

3、图中未注明的过焊孔圆弧切角半径为35mm。

4、图中未注明焊缝详见《钢梁焊缝及细节设计图》。

符号：

⊕ —— M30螺栓，开孔直径33mm

⊗ —— M24螺栓，开孔直径26mm

大样B（节段14~节段15）

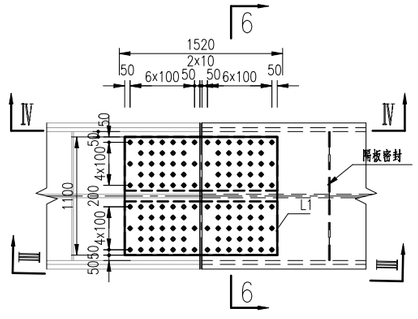

6-6

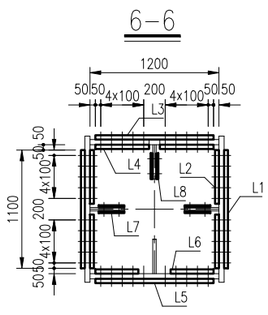

腹杆腹板加劲肋拼接

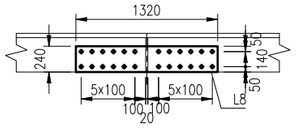

腹杆顶加劲肋拼接

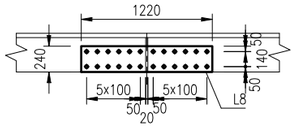

Ⅲ－Ⅲ

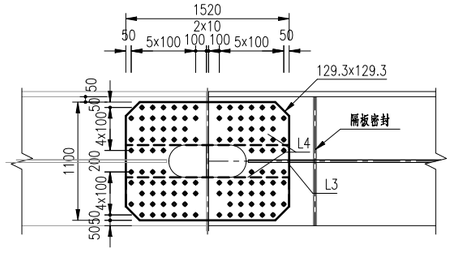

Ⅳ－Ⅳ

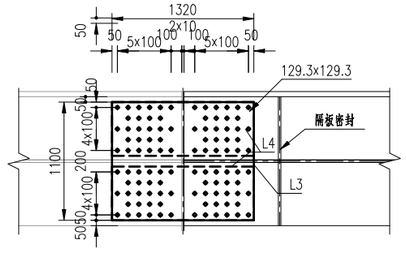

节段14~节段15拼接数量表

名称	编号	材质	规格	数量	单件重	共重（kg）	备注
上弦杆拼接	P1	Q355D	□1220×1400×28	2	375.9	751.8	
	P2		□1220×300×28	2	81.3	162.6	
	P3		□1220×500×28	2	134.1	268.2	
	P4		□1220×400×28	2	107.7	215.4	
	P5		□1420×1100×32	1	391.9	391.9	
	P6		□1420×400×32	2	143.2	286.4	
	P7		□920×200×20	10	28.3	283	
	P8		□600×1800×16	2	135.6	271.2	填板
	P9		□700×1100×16	1	96.7	96.7	填板
	M30高强螺栓	10.9S	M30x200	428	1.94	830.3	
下弦杆拼接	K1	Q355D	□1020×1300×24	2	250.6	501.2	
	K2		□1020×600×24	4	114.9	459.6	
	K3		□1320×1100×36	1	409.8	409.8	
	K4		□1320×400×36	2	149.8	299.6	
	K5		□920×200×20	6	28.3	169.8	
	K6		□500×1700×8	2	53.4	106.8	填板
	K7		□650×1100×4	1	22.6	22.6	填板
	M30高强螺栓	10.9S	M30x200	344	1.94	667.4	
腹杆拼接	L1	Q355D	□1520×1100×24	2	314.6	629.2	
	L2		□1520×500×24	4	143.2	572.8	
	L3		□1320×1100×28	1	318.7	318.7	
	L4		□1320×500×28	2	145.1	290.2	
	L5		□1520×1100×44	1	576.8	576.8	
	L6		□1520×240×44	2	124.3	248.6	
	L7		□1220×240×24	4	54.6	218.4	
	L8		□1320×240×24	2	60.3	120.6	
	M30高强螺栓	10.9S	M30x200	540	1.94	1047.6	

中交第二公路勘察设计研究院有限公司	狮子洋通道工程勘察设计 施 工 图 设 计	K6+418.3 新沙高架桥 边桁节段15设计图	设计	余汪千	复核	袁勤	一审	沈华	二审	韦忠	图号	SZYS/04/02/02/01/ 45

节段15材料数量表

名称	编号	材质	规格	数量	单件重	共重（kg）	备注
上弦顶板	N11a	Q420D	t=40mm,A=11.85m2	1	3721.1	3721.1	
	N11b	Q355D	t=24mm,A=10.39m2	1	1958.2	1958.2	
上弦底板	N12a	Q420D	□7900×1200×40	1	2976.7	2976.7	
	N12b	Q355D	□7100×1200×24	1	1605.2	1605.2	
上弦节点板	N13	Q420D	t=48mm,A=22.12m2	2	8333.2	16666.4	
上弦腹板	N14	Q355D	□7300×1644×32	2	3014.4	6028.8	
上弦横隔板	N15	Q355D	□1560×1200×16	3	234.9	704.7	
	N15a	Q355D	□1576×1200×16	2	237.4	474.8	
	N15‘	Q355D	□1657×200×16	3	41.4	124.2	
	N15b	Q355D	□1782×40×4	4	2.2	8.8	
	N15c	Q355D	□600×400×16	4	30.1	120.4	
上弦加劲肋	N16a	Q420D	□7900×320×32	6	635.5	3813	
	N16b	Q355D	□7100×240×20	6	266.9	1601.4	
下弦顶板	N21a	Q355D	□7900×1850×24	1	2754.4	2754.4	
	N21b	Q355D	□7100×1850×24	1	2475.6	2475.6	
下弦底板	N22a	Q355D	t=24mm,A=12.53m2	1	2360.7	2360.7	
	N22b	Q355D	t=24mm,A=9.71m2	1	1830.1	1830.1	
下弦节点板	N23	Q355D	t=44mm,A=20.71m2	2	7154.2	14308.4	Z35钢
下弦腹板	N24	Q355D	□7300×1474×32	2	2702.9	5405.8	
下弦横隔板	N25	Q355D	□1450×1200×16	3	218.5	655.5	
	N25a	Q355D	□1450×1200×16	2	218.5	437	
	N25’	Q355D	□1657×200×16	5	41.4	207	
下弦加劲肋	N26a	Q355D	□7900×240×20	4	298.3	1193.2	
	N26b	Q355D	□7100×320×32	4	570.2	2280.8	
	N26c	Q355D	□15000×170×14	1	280.2	280.2	
斜腹杆	N31	Q355D	□11322×1200×36	1	3840.5	3840.5	
	N31a	Q355D	□11622×1200×36	1	3942.3	3942.3	
	N32	Q355D	□7322×1360×36	2	2814.7	5629.4	
	N33	Q355D	□7322×320×32	2	587.8	1175.6	
	N33a	Q355D	□9922×320×32	1	798.8	798.8	
	N33b	Q355D	□10222×320×32	1	821.4	821.4	
	N34	Q355D	□1200×1200×16	3	180.9	542.7	
	N41	Q355D	□5440×1200×40	1	2050.4	2050.4	
	N41a	Q355D	□5740×1200×40	1	2163.5	2163.5	
	N42	Q355D	□3640×1760×40	2	2012.7	4025.4	
	N43	Q355D	□3640×320×32	4	291.4	1165.6	
	N43a	Q355D	□4740×320×32	1	381.8	381.8	
	N43b	Q355D	□5040×320×32	1	404.4	404.4	
	N44	Q355D	□1200×1600×16	2	241.2	482.4	
节点板加劲	N51	Q420D	□5858×1200×40	1	2207.4	2207.4	
	N51a	Q420D	□5858×1200×40	1	2207.4	2207.4	
	N52	Q420D	□3658×1360×40	2	1560.6	3121.2	
	N53	Q420D	□3658×320×32	2	293.9	587.8	
	N53a	Q420D	□5158×320×32	1	414.5	414.5	
	N53b	Q420D	□5158×320×32	1	414.5	414.5	
	N54	Q420D	□1200×1200×16	2	180.9	361.8	
	N55	Q420D	□2100×320×32	4	168.3	673.2	
	N56	Q420D	□2600×320×32	4	208.5	834	
横梁接头	N61	Q355D	□1560×602×14	3	103.3	309.9	
	N61a	Q355D	□1576×618×14	2	106.6	213.2	
	N62	Q355D	t=24mm,A=0.46m2	3	86.7	260.1	
	N62a	Q355D	t=24mm,A=0.46m2	2	86.7	173.4	
	N63	Q355D	□1450×606×14	3	96.7	290.1	
	N63a	Q355D	□1450×618×14	2	98.9	197.8	
小计						113682.9	
焊缝重1.5%						1705.2	
合计						115388.1	

节段15材料数量汇总表

规格（mm）	材质	单个合计	全桥共2个
t=48	Q420D	16666.4	33332.8
t=40		14233.8	28467.6
t=32		6737	13474
t=16		361.8	723.6
合计		37999	75998
t=44		14308.4	28616.8
t=40		8239.3	16478.6
t=36		13412.2	26824.4
t=32		18463	36926
t=24		13417.7	26835.4
t=20		2794.6	5589.2
t=16		3748.7	7497.4
t=14		1291.2	2582.4
t=4		8.8	17.6
合计		75683.9	151367.8
焊缝重（1.5%）		1705.2	3410.4
内表面涂装（m²）		346.5	693
外表面涂装（m²）		531.0	1062

节段14~节段15拼接数量汇总表

规格（mm）	材质	单个合计	全桥共2个
t=44	Q355D	825.4	1650.8
t=36	Q355D	709.4	1418.8
t=32	Q355D	678.3	1356.6
t=28	Q355D	2006.9	4013.8
t=24	Q355D	2501.8	5003.6
t=20	Q355D	452.8	905.6
t=16	Q355D	367.9	735.8
t=8	Q355D	106.8	213.6
t=4	Q355D	22.6	45.2
合计	Q355D	7671.9	15343.8
M30x200	10.9S高强螺栓	2545.3	5090.6
外表面涂装（m²）		38.2	76.48

中交第二公路勘察设计研究院有限公司	狮子洋通道工程勘察设计 施 工 图 设 计	K6+418.3 新沙高架桥 边桁节段15设计图	设计	余汪千	复核	袁勤	一审	沈雁	二审	韦忠	图号	SZYS/04/02/02/01/ 45

4230119 0001741

大样A（节段15~节段16）

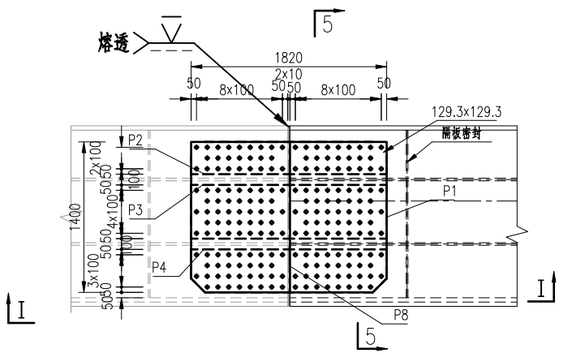

5-5

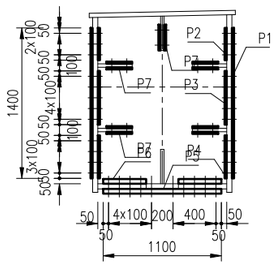

大样C（节段15~节段16）

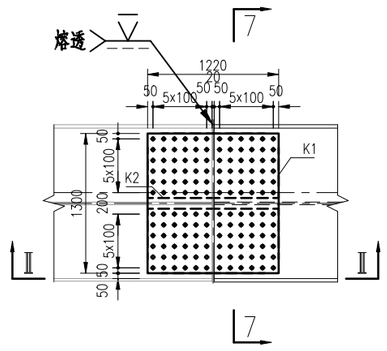

7-7

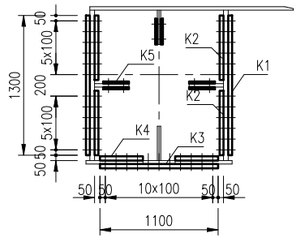

注：

1、本图尺寸均以mm计。

2、未注明的板件裁切边距M30螺栓不小50mm，M24螺栓不小40mm。

3、图中未注明的过焊孔圆弧切角半径为35mm。

4、图中未注明焊缝详见《钢梁焊缝及细节设计图》。

符号：

⊕ —— M30螺栓，开孔直径33mm

⊗ —— M24螺栓，开孔直径26mm

Ⅰ－Ⅰ

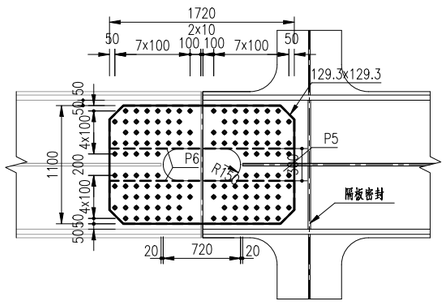

上弦杆顶板、腹板加劲肋拼接

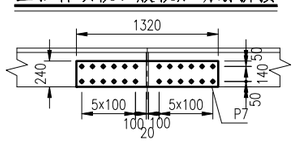

Ⅳ－Ⅳ

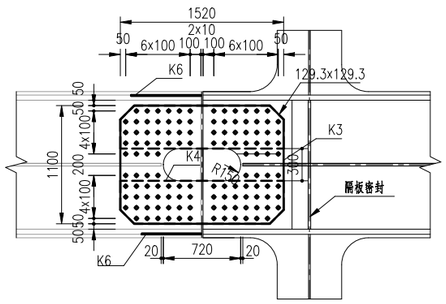

下弦杆顶板、腹板加劲肋拼接

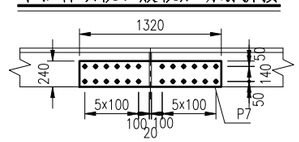

节段15~节段16拼接数量表

名称	编号	材质	规格	数量	单件重	共重（kg）	备注
上弦杆拼接	P1	Q420D	□1820×1400×40	2	800.7	1601.4	
	P2		□1820×300×40	2	172.7	345.4	
	P3		□1820×500×40	2	285.7	571.4	
	P4		□1820×400×40	2	229.2	458.4	
	P5		□1720×1100×44	1	652.8	652.8	
	P6		□1720×400×44	2	238.3	476.6	
	P7		□1320×240×24	10	60.3	603	
	M30高强螺栓	10.9S	M30×200	652	1.94	1264.9	
下弦杆拼接	K1	Q355D	□1020×1300×24	2	250.6	501.2	
	K2		□1020×600×24	4	114.9	459.6	
	K3		□1320×1100×36	1	409.8	409.8	
	K4		□1320×400×36	2	149.8	299.6	
	K5		□920×200×20	6	28.3	169.8	
	K6		□500×1700×8	2	53.4	106.8	填板
	K7		□650×1100×4	1	22.6	22.6	填板
	M30高强螺栓	10.9S	M30×200	344	1.94	667.4	
腹杆拼接	L1	Q420D	□1520×1500×32	2	572.7	1145.4	
	L2		□1520×400×32	4	153.2	612.8	
	L3		□1520×500×32	2	190.9	381.8	
	L4		□1520×1100×28	1	367.1	367.1	
	L5		□1520×500×28	2	167	334	
	L6		□1520×1100×40	1	524.4	524.4	
	L7		□1520×400×40	2	191.5	383	
	L8		□1320×240×24	10	60.3	603	
	M30高强螺栓	10.9S	M30×200	752	1.94	1458.9	

大样B（节段15~节段16）

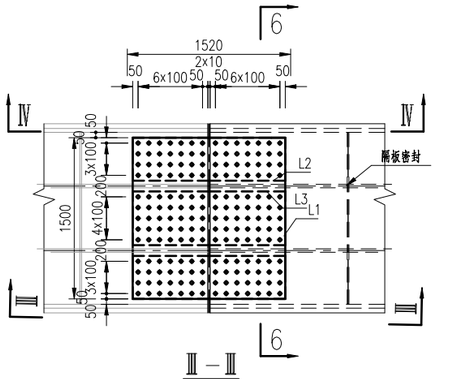

6-6

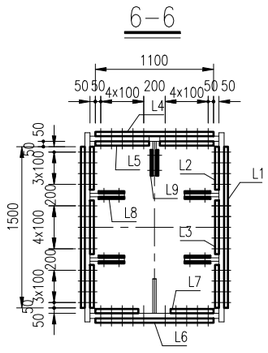

腹杆腹板加劲肋拼接

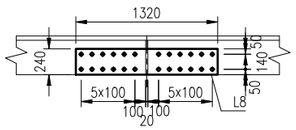

腹杆顶加劲肋拼接

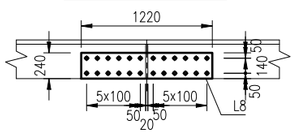

Ⅲ－Ⅲ

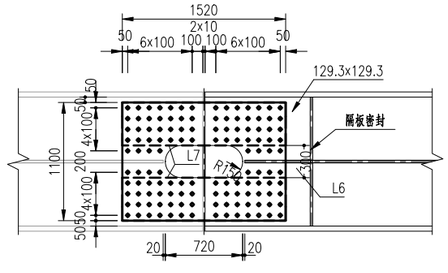

Ⅳ－Ⅳ

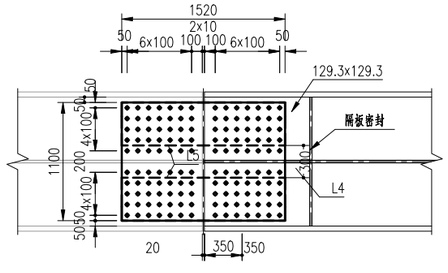

中交第二公路勘察设计研究院有限公司	狮子洋通道工程勘察设计 施 工 图 设 计	K6+418.3 新沙高架桥 边桁节段16设计图	设计	余汪千	复核	袁勤	一审	张华	二审	李忠	图号	SZYS/04/02/02/01/ 46

节段16材料数量表

名称	编号	材质	规格	数量	单件重	共重(kg)	备注
上弦顶板	N11a	Q420D	t=40mm,A=11.85m2	1	3721.1	3721.1	
	N11b	Q420D	t=40mm,A=10.39m2	1	3263.6	3263.6	
上弦底板	N12a	Q420D	□8050×1200×40	1	3033.2	3033.2	
	N12b	Q420D	□6950×1200×40	1	2618.8	2618.8	
上弦节点板	N13	Q420D	t=44mm,A=22.95m2	2	7927.4	15854.8	
上弦腹板	N14	Q420D	□7150×1628×48	2	4386	8772	
上弦横隔板	N15	Q420D	□1560×1200×16	3	234.9	704.7	
	N15a	Q420D	□1560×1200×16	2	234.9	469.8	
	N15 ‘	Q420D	□1657×200×16	3	41.4	124.2	
	N15b	Q420D	□1782×40×4	4	2.2	8.8	
	N15c	Q420D	□600×400×16	4	30.1	120.4	
上弦加劲肋	N16a	Q420D	□8050×320×32	6	648.1	3888.6	
	N16b	Q420D	□6950×320×32	6	557.7	3346.2	
下弦顶板	N21a	Q420D	□8050×1850×32	1	3740.4	3740.4	
	N21b	Q420D	□6950×1850×32	1	3230.4	3230.4	
下弦底板	N22a	Q420D	t=32mm,A=12.53m2	1	3147.7	3147.7	
	N22b	Q420D	t=32mm,A=9.71m2	1	2440.1	2440.1	
下弦节点板	N23	Q420D	t=44mm,A=22.55m2	2	7788	15576	Z35钢
下弦腹板	N24	Q420D	□7150×1482×44	2	3661.2	7322.4	
下弦横隔板	N25	Q420D	□1450×1200×16	3	218.5	655.5	
	N25a	Q420D	□1450×1200×16	2	218.5	437	
	N25’	Q420D	□1657×200×16	5	41.4	207	
下弦加劲肋	N26a	Q420D	□8050×320×32	4	648.1	2592.4	
	N26b	Q420D	□6950×320×32	4	557.7	2230.8	
	N26c	Q420D	□15000×170×14	1	280.2	280.2	
斜腹杆	N31	Q420D	□10875×1200×40	1	4097.7	4097.7	
	N31a	Q420D	□11375×1200×40	1	4286.1	4286.1	
	N32	Q420D	□7275×1360×40	2	3105.5	6211	
	N33	Q420D	□7275×320×32	4	585.3	2341.2	
	N33a	Q420D	□9475×320×32	1	761.1	761.1	
	N33b	Q420D	□9975×320×32	1	801.3	801.3	
	N34	Q420D	□1200×1200×16	3	180.9	542.7	
	N41	Q420D	□5429×1200×40	1	2044.1	2044.1	
	N41a	Q420D	□5629×1200×40	1	2119.5	2119.5	
	N42	Q420D	□3629×1760×40	2	2006.5	4013	
	N43	Q420D	□3629×320×32	4	291.4	1165.6	
	N43a	Q420D	□4729×320×32	1	379.3	379.3	
	N43b	Q420D	□4929×320×32	1	396.9	396.9	
	N44	Q420D	□1200×1600×16	3	241.2	723.6	
	N51	Q420D	□5640×1200×48	1	2550.9	2550.9	
节点板加劲	N51a	Q420D	□5740×1200×48	1	2596.2	2596.2	
	N52	Q420D	□3640×1760×48	2	2415.3	4830.6	
	N53	Q420D	□3640×320×32	4	291.4	1165.6	
	N53a	Q420D	□4940×320×32	1	396.9	396.9	
	N53b	Q420D	□5040×320×32	1	404.4	404.4	
	N54	Q420D	□1200×1600×16	3	241.2	723.6	
	N55	Q420D	□2100×320×32	8	168.3	1346.4	
	N56	Q420D	□2400×320×32	8	193.4	1547.2	
横梁接头	N61	Q355D	□1560×606×14	3	104.4	313.2	
	N61a	Q355D	□1560×602×14	2	103.3	206.6	
	N62	Q355D	t=24mm,A=0.46m2	3	86.7	260.1	
	N62a	Q355D	t=24mm,A=0.46m2	2	86.7	173.4	
	N63	Q355D	□1450×606×14	3	96.7	290.1	
	N63a	Q355D	□1450×606×14	2	96.7	193.4	
小计						134667.8	
焊缝重1.5%						2020.0	
合计						136687.8	

节段16材料数量汇总表

规格(mm)	材质	单个合计	全桥共2个
t=48	Q420D	18749.7	37499.4
t=44		38753.2	77506.4
t=40		35408.1	70816.2
t=32		35322.5	70645
t=16		4708.5	9417
t=14		280.2	560.4
t=4		8.8	17.6
合计		133231	266462
t=24		433.5	867
t=14		1003.3	2006.6
合计		1436.8	2873.6
焊缝重(1.5%)		2020.0	4040
内表面涂装(㎡)		367.5	735
外表面涂装(㎡)		566.7	1133.4

节段15~节段16拼接数量汇总表

规格(mm)	材质	单个合计	全桥共2个
t=44	Q420D	1129.4	2258.8
t=40	Q420D	3884	7768
t=32	Q420D	2140	4280
t=28	Q420D	701.1	1402.2
t=24	Q420D	1206	2412
合计	Q420D	9060.5	18121
t=36	Q355D	709.4	1418.8
t=24	Q355D	960.8	1921.6
t=20	Q355D	169.8	339.6
t=8	Q355D	106.8	213.6
t=4	Q355D	22.6	45.2
合计	Q355D	1969.4	3938.8
M30x200	10.9S高强螺栓	3391.2	6782.4
外表面涂装(㎡)		44.9	89.72

中交第二公路勘察设计研究院有限公司	狮子洋通道工程勘察设计 施 工 图 设 计	K6+418.3 新沙高架桥 边桁节段16设计图	设计	余汪千	复核	袁勤	一审	沈雁	二审	李忠	图号	SZYS/04/02/02/01/ 46

7255016 8488888

大样A（节段16~节段17）

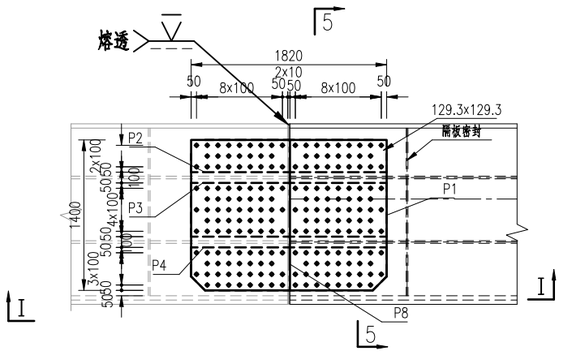

5-5

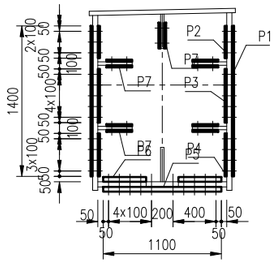

大样C（节段16~节段17）

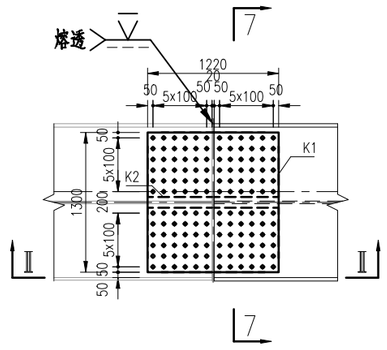

7-7

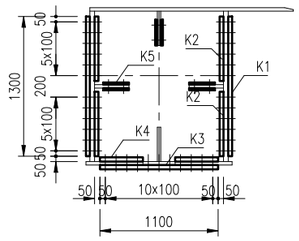

注：

1、本图尺寸均以mm计。

2、未注明的板件裁切边距M30螺栓不小50mm，M24螺栓不小40mm。

3、图中未注明的过焊孔圆弧切角半径为35mm。

4、图中未注明焊缝详见《钢梁焊缝及细节设计图》。

符号：

⊕ —— M30螺栓，开孔直径33mm

⊗ —— M24螺栓，开孔直径26mm

I－I

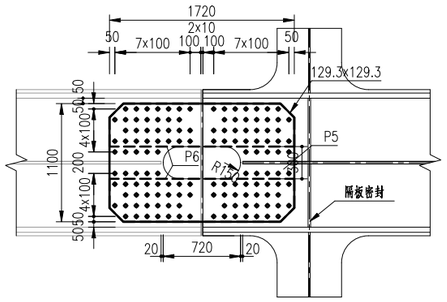

上弦杆顶板、腹板加劲肋拼接

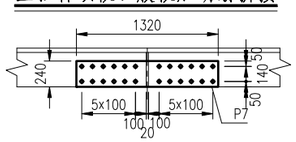

Ⅳ－Ⅳ

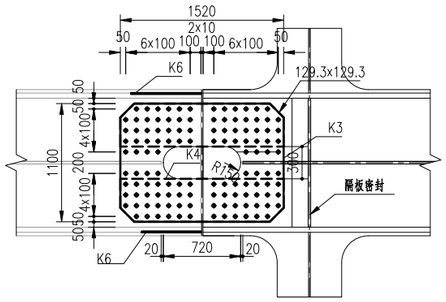

下弦杆顶板、腹板加劲肋拼接

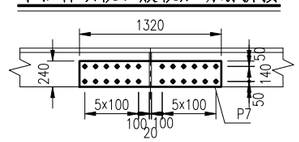

大样B（节段16~节段17）

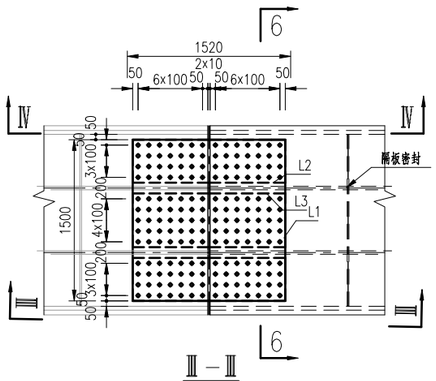

6-6

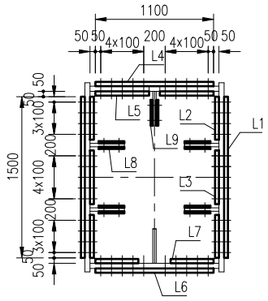

腹杆腹板加劲肋拼接

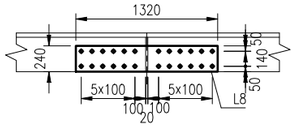

腹杆顶加劲肋拼接

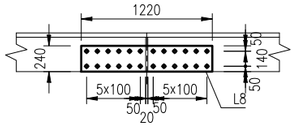

Ⅲ－Ⅲ

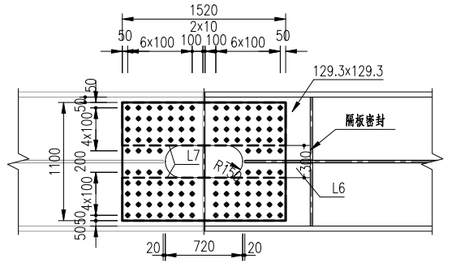

Ⅳ－Ⅳ

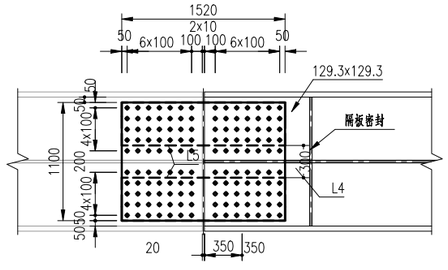

节段16~节段17拼接数量表

名称	编号	材质	规格	数量	单件重	共重（kg）	备注
上弦杆拼接	P1	Q420D	□1820×1400×40	2	800.7	1601.4	
	P2		□1820×300×40	2	172.7	345.4	
	P3		□1820×500×40	2	285.7	571.4	
	P4		□1820×400×40	2	229.2	458.4	
	P5		□1720×1100×44	1	652.8	652.8	
	P6		□1720×400×44	2	238.3	476.6	
	P7		□1320×240×24	10	60.3	603	
	M30高强螺栓	10.9S	M30x200	652	1.94	1264.9	
下弦杆拼接	K1	Q420D	□1220×1300×28	2	349.5	699	
	K2		□1220×600×28	4	160.5	642	
	K3		□1520×1100×36	1	471.9	471.9	
	K4		□1520×400×36	2	172.4	344.8	
	K5		□1320×240×24	6	60.3	361.8	
	K6		□600×1300×4	1	24.5	24.5	填板
	M30高强螺栓	10.9S	M30x200	484	1.94	939	
腹杆拼接	L1	Q420D	□1520×1500×32	2	572.7	1145.4	
	L2		□1520×400×32	4	153.2	612.8	
	L3		□1520×500×32	2	190.9	381.8	
	L4		□1520×1100×28	1	367.1	367.1	
	L5		□1520×500×28	2	167	334	
	L6		□1520×1100×40	1	524.4	524.4	
	L7		□1520×400×40	2	191.5	383	
	L8		□1320×240×24	10	60.3	603	
	M30高强螺栓	10.9S	M30x200	752	1.94	1458.9	

中交第二公路勘察设计研究院有限公司	狮子洋通道工程勘察设计 施 工 图 设 计	K6+418.3 新沙高架桥 边桁节段17设计图	设计	余汪千	复核	袁勤	一审	张华	二审	李忠	图号	SZYS/04/02/02/01/ 47

节段17材料数量表

名称	编号	材质	规格	数量	单件重	共重(kg)	备注
上弦顶板	N11a	Q420D	t=40mm,A=11.85m2	1	3720.9	3720.9	
	N11b	Q420D	t=40mm,A=10.4m2	1	3265.6	3265.6	
上弦底板	N12a	Q420D	□8050×1200×40	1	3033.2	3033.2	
	N12b	Q420D	□6950×1200×40	1	2618.8	2618.8	
上弦节点板	N13	Q420D	t=44mm,A=22.94m2	2	7923.5	15847	
上弦腹板	N14	Q420D	□7150×1628×48	2	4386	8772	
上弦横隔板	N15	Q420D	□1560×1200×16	3	234.9	704.7	
	N15a	Q420D	□1560×1200×16	2	234.9	469.8	
	N15‘	Q420D	□1657x200x16	3	41.4	124.2	
	N15b	Q420D	□1782×40×4	4	2.2	8.8	
	N15c	Q420D	□600×400×16	4	30.1	120.4	
上弦加劲肋	N16a	Q420D	□8050×320×32	6	648.1	3888.6	
	N16b	Q420D	□6950×320×32	6	557.7	3346.2	
下弦顶板	N21a	Q420D	□8050×1850×32	1	3740.4	3740.4	
	N21b	Q420D	□6950×1850×32	1	3230.4	3230.4	
下弦底板	N22a	Q420D	t=40mm,A=15.8m2	1	4961.2	4961.2	
	N22b	Q420D	t=32mm,A=10.4m2	1	2612.5	2612.5	
下弦节点板	N23	Q420D	t=44mm,A=22.56m2	2	7792.2	15584.4	Z35钢
下弦腹板	N24	Q420D	□7150×1482×44	2	3661.2	7322.4	
下弦横隔板	N25	Q420D	□1450×1200×16	3	218.5	655.5	
	N25a	Q420D	□1450×1200×16	2	218.5	437	
	N25’	Q420D	□1657×200×16	3	41.4	124.2	
下弦加劲肋	N26a	Q420D	□8050×320×32	4	648.1	2592.4	
	N26b	Q420D	□6950×320×32	4	557.7	2230.8	
	N26c	Q420D	□15000×170×14	1	280.2	280.2	
斜腹杆	N31	Q420D	□11042×1200×40	1	4160.5	4160.5	
	N31a	Q420D	□11342×1200×40	1	4273.5	4273.5	
	N32	Q420D	□7242×1760×40	2	4003.5	8007	
	N33	Q420D	□7242×320×32	4	582.8	2331.2	
	N33a	Q420D	□9642×320×32	1	776.2	776.2	
	N33b	Q420D	□9942×320×32	1	798.8	798.8	
	N34	Q420D	□1200×1600×16	3	241.2	723.6	
	N41	Q355D	□5426×1200×36	1	1839.7	1839.7	
	N41a	Q355D	□5726×1200×36	1	1941.5	1941.5	
	N42	Q355D	□3626×1360×36	2	1393.2	2786.4	
	N43	Q355D	□3626×320×32	2	291.4	582.8	
	N43a	Q355D	□4726×320×32	1	379.3	379.3	
	N43b	Q355D	□5026×320×32	1	404.4	404.4	
	N44	Q355D	□1200×1200×16	2	180.9	361.8	
	N51	Q420D	□5629×1200×40	1	2119.5	2119.5	
节点板加劲	N51a	Q420D	□5629×1200×40	1	2119.5	2119.5	
	N52	Q420D	□3629×1760×40	2	2006.5	4013	
	N53	Q420D	□3629×320×32	4	291.4	1165.6	
	N53a	Q420D	□4229×320×32	1	339.1	339.1	
	N53b	Q420D	□4229×320×32	1	339.1	339.1	
	N54	Q420D	□1200×1600×16	2	241.2	482.4	
	N55	Q420D	□2100×320×32	8	168.3	1346.4	
	N56	Q420D	□2400×320×32	8	193.4	1547.2	
横梁接头	N61	Q355D	□1560×606×14	3	104.4	313.2	
	N61a	Q355D	□1560×602×14	2	103.3	206.6	
	N62	Q355D	t=24mm,A=0.47m2	3	89.3	267.9	
	N62a	Q355D	t=24mm,A=0.48m2	2	90.4	180.8	
	N63	Q355D	□1450×606×14	2	96.7	193.4	
	N63a	Q355D	□1450×606×14	2	96.7	193.4	
支座加劲	N81	Q420D	□1450×1200×32	5	437.1	2185.5	
	N82	Q420D	□1450×602×60	3	409.8	1229.4	
	N83	Q420D	□2800×2650×80	1	4659.8	4659.8	
	N84	Q420D	□1000×568×32	4	143.2	572.8	
	N85	Q420D	□1350×570×32	7	193.4	1353.8	
	N86	Q420D	□2960×650×32	1	482.3	482.3	
小计						144369	
焊缝重1.5%						2165.5	
合计						146534.5	

节段17材料数量汇总表

规格(mm)	材质	单个合计	全桥共2个
t=60	Q420D	1229.4	2458.8
t=80		4659.8	9319.6
t=48		8772.0	17544.0
t=44		38753.8	77507.6
t=40		42292.7	84585.4
t=32		34879.3	69758.6
t=16		3841.8	7683.6
t=14		280.2	560.4
t=4		8.8	17.6
合计		134717.8	269435.6
t=36	Q355D	6567.6	13135.2
t=32		1366.5	2733.0
t=24		448.7	897.4
t=16		361.8	723.6
t=14		906.6	1813.2
合计		9651.2	19302.4
焊缝重(1.5%)		2165.5	4331.0
内表面涂装(m²)		403.3	806.6
外表面涂装(m²)		586.0	1172.0

节段16~节段17拼接数量汇总表

规格(mm)	材质	单个合计	全桥共2个
t=44	Q420D	1129.4	2258.8
t=40	Q420D	3884	7768
t=36	Q420D	816.7	1633.4
t=32	Q420D	2140	4280
t=28	Q420D	2042.1	4084.2
t=24	Q420D	1567.8	3135.6
t=4	Q420D	24.5	49
合计	Q420D	11604.5	23209
M30x200	10.9S高强螺栓	3662.8	7325.6
外表面涂装(m²)		45.4	90.88

中交第二公路勘察设计研究院有限公司	狮子洋通道工程勘察设计 施 工 图 设 计	K6+418.3 新沙高架桥 边桁节段17设计图	设计	余汪千	复核	袁勤	一审	张华	二审	李忠	图号	SZYS/04/02/02/01/47

2235011711747

大样A（节段17~节段18）

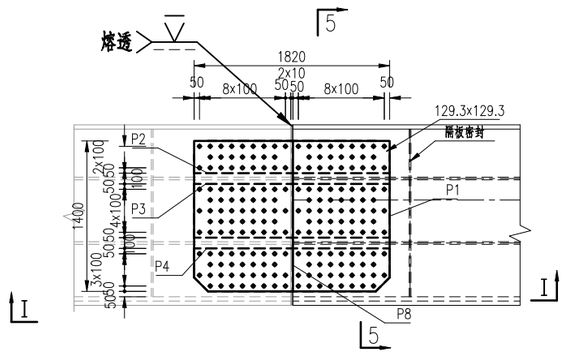

5-5

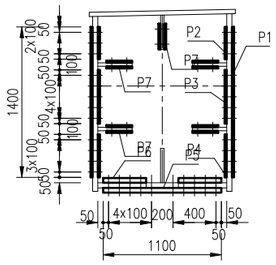

大样C（节段17~节段18）

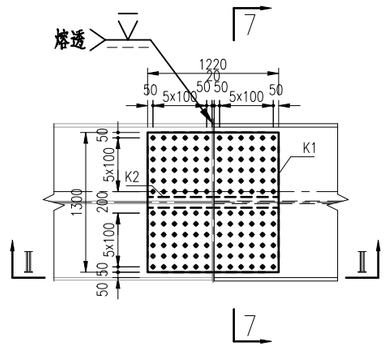

7-7

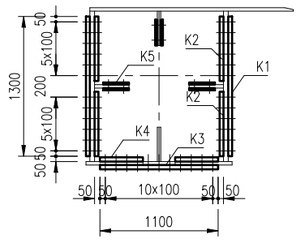

注：

1、本图尺寸均以mm计。

2、未注明的板件裁切边距M30螺栓不小50mm，M24螺栓不小40mm。

3、图中未注明的过焊孔圆弧切角半径为35mm。

4、图中未注明焊缝详见《钢梁焊缝及细节设计图》。

符号：

⊕ —— M30螺栓，开孔直径33mm

⊗ —— M24螺栓，开孔直径26mm

Ⅰ－Ⅰ

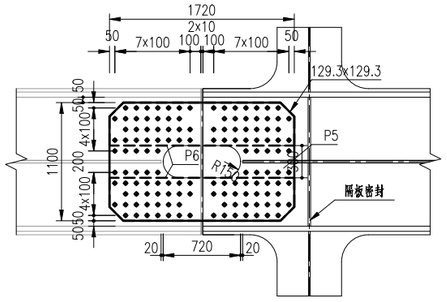

上弦杆顶板、腹板加劲肋拼接

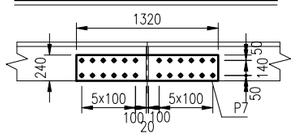

Ⅳ－Ⅳ

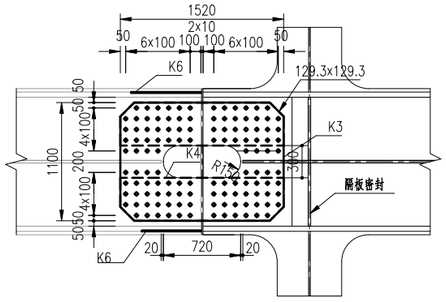

下弦杆顶板、腹板加劲肋拼接

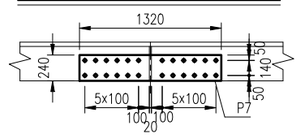

大样B（节段17~节段18）

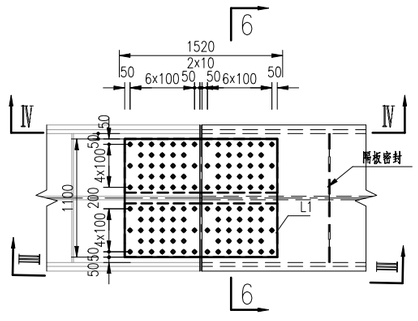

6-6

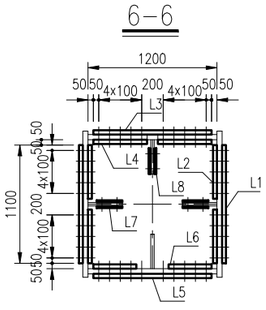

腹杆腹板加劲肋拼接

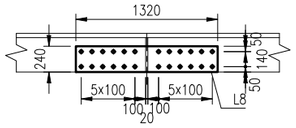

腹杆顶加劲肋拼接

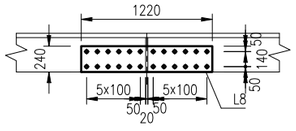

Ⅲ－Ⅲ

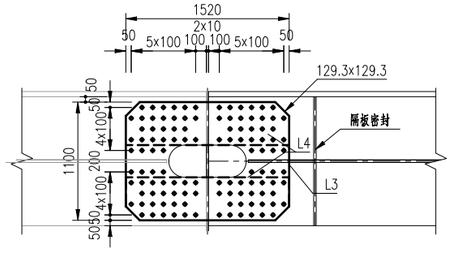

Ⅳ－Ⅳ

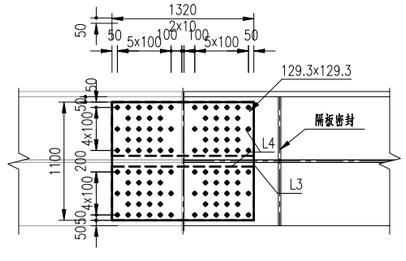

节段17~节段18拼接数量表

名称	编号	材质	规格	数量	单件重	共重（kg）	备注
上弦杆拼接	P1	Q420D	□1820×1400×40	2	800.7	1601.4	
	P2		□1820×300×40	2	172.7	345.4	
	P3		□1820×500×40	2	285.7	571.4	
	P4		□1820×400×40	2	229.2	458.4	
	P5		□1720×1100×44	1	652.8	652.8	
	P6		□1720×400×44	2	238.3	476.6	
	P7		□1320×240×24	10	60.3	603	
	M30高强螺栓	10.9S	M30x200	652	1.94	1264.9	
下弦杆拼接	K1	Q420D	□1220×1300×28	2	349.5	699	
	K2		□1220×600×28	4	160.5	642	
	K3		□1520×1100×36	1	471.9	471.9	
	K4		□1520×400×36	2	172.4	344.8	
	K5		□1320×240×24	6	60.3	361.8	
	K6		□600×1300×4	1	24.5	24.5	填板
	M30高强螺栓	10.9S	M30x200	484	1.94	939	
腹杆拼接	L1	Q355D	□1520×1100×24	2	314.6	629.2	
	L2		□1520×500×24	4	143.2	572.8	
	L3		□1320×1100×28	1	318.7	318.7	
	L4		□1320×500×28	2	145.1	290.2	
	L5		□1520×1100×44	1	576.8	576.8	
	L6		□1520×240×44	2	124.3	248.6	
	L7		□1220×240×24	4	54.6	218.4	
	L8		□1320×240×24	2	60.3	120.6	
	M30高强螺栓	10.9S	M30x200	540	1.94	1047.6	

中交第二公路勘察设计研究院有限公司	狮子洋通道工程勘察设计 施 工 图 设 计	K6+418.3 新沙高架桥 边桁节段18设计图	设计	余汪千	复核	袁勤	一审	沈华	二审	李忠	图号	SZYS/04/02/02/01/ 48

节段18材料数量表

名称	编号	材质	规格	数量	单件重	共重（kg）	备注
上弦顶板	N11a	Q420D	t=40mm,A=11.85m2	1	3721.1	3721.1	
	N11b	Q420D	t=40mm,A=10.39m2	1	3263.6	3263.6	
上弦底板	N12a	Q420D	□7900×1200×40	1	2976.7	2976.7	
	N12b	Q420D	□6950×1200×40	1	2618.8	2618.8	
上弦节点板	N13	Q420D	t=48mm,A=21.29m2	2	8023.9	16047.8	
上弦腹板	N14	Q420D	□7150×1628×48	2	4386	8772	
上弦横隔板	N15	Q420D	□1560×1200×16	3	234.9	704.7	
	N15a	Q420D	□1560×1200×16	2	234.9	469.8	
	N15‘	Q420D	□1657x200x16	3	41.4	124.2	
	N15b	Q420D	□1782×40×4	4	2.2	8.8	
	N15c	Q420D	□600×400×16	4	30.1	120.4	
上弦加劲肋	N16a	Q420D	□7900×320×32	6	635.5	3813	
	N16b	Q420D	□6950×320×32	6	557.7	3346.2	
下弦顶板	N21a	Q420D	□8050×1850×32	1	3740.4	3740.4	
	N21b	Q355D	□7100×1850×24	1	2475.6	2475.6	
下弦底板	N22a	Q420D	t=32mm,A=12.53m2	1	3147.7	3147.7	
	N22b	Q355D	t=24mm,A=9.71m2	1	1830.1	1830.1	
下弦节点板	N23	Q420D	t=48mm,A=20.71m2	2	7804.5	15609	Z35钢
下弦腹板	N24	Q355D	□7300×1474×32	2	2702.9	5405.8	
下弦横隔板	N25	Q355D	□1450×1200×16	3	218.5	655.5	
	N25a	Q355D	□1450×1200×16	2	218.5	437	
	N25'	Q355D	□1657×200×16	3	41.4	124.2	
下弦加劲肋	N26a	Q420D	□8050×320×32	4	648.1	2592.4	
	N26b	Q355D	□7100×320×32	4	570.2	2280.8	
	N26c	Q355D	□15150×170×14	1	283.5	283.5	
斜腹杆	N31	Q355D	□11023×1200×36	1	3738.8	3738.8	
	N31a	Q355D	□11423×1200×36	1	3874.4	3874.4	
	N32	Q355D	□7223×1360×36	2	2775.1	5550.2	
	N33	Q355D	□7223×320×32	2	580.3	1160.6	
	N33a	Q355D	□9623×320×32	1	773.7	773.7	
	N33b	Q355D	□10023×320×32	1	806.4	806.4	
	N34	Q355D	□1200×1200×16	3	180.9	542.7	
	N41	Q355D	□5629×1200×36	1	1907.6	1907.6	
	N41a	Q355D	□5629×1200×36	1	1907.6	1907.6	
	N42	Q355D	□3629×1360×36	2	1396	2792	
	N43	Q355D	□3629×320×32	4	291.4	1165.6	
	N43a	Q355D	□4929×320×32	1	396.9	396.9	
	N43b	Q355D	□4929×320×32	1	396.9	396.9	
	N44	Q355D	□1200×1200×16	3	180.9	542.7	
	N51	Q355D	□5826×1200×36	1	1975.4	1975.4	
	N51a	Q355D	□5626×1200×36	1	1907.6	1907.6	
	N52	Q355D	□3626×1360×36	2	1393.2	2786.4	
	N53	Q355D	□3626×320×32	4	291.4	1165.6	
	N53a	Q355D	□5126×320×32	1	412	412	
	N53b	Q355D	□4926×320×32	1	396.9	396.9	
	N54	Q355D	□1200×1200×16	3	180.9	542.7	
节点板加劲	N55	Q355D	□2300×320×32	4	185.9	743.6	
	N56	Q355D	□2400×320×32	6	193.4	1160.4	
横梁接头	N61	Q355D	□1560×602×14	3	103.3	309.9	
	N61a	Q355D	□1560×602×14	2	103.3	206.6	
	N62	Q355D	t=24mm,A=0.46m2	3	86.7	260.1	
	N62a	Q355D	t=24mm,A=0.47m2	2	88.8	177.6	
	N63	Q355D	□1450×602×14	3	95.6	286.8	
	N63a	Q355D	□1450×618×14	2	98.9	197.8	
小计						122654.6	
焊缝重1.5%						1839.8	
合计						124494.4	

节段18材料数量汇总表

规格（mm）	材质	单个合计	全桥共2个
t=48	Q420D	40428.8	80857.6
t=40		12580.2	25160.4
t=32		16639.7	33279.4
t=16		1419.1	2838.2
t=4		8.8	17.6
合计		71076.6	142153.2
t=36	Q355D	26440	52880
t=32		16265.2	32530.4
t=24		4743.4	9486.8
t=16		2844.8	5689.6
t=14		1284.6	2569.2
合计		51578	103156
焊缝重（1.5%）		1839.8	3679.6
内表面涂装（m²）		345.4	690.8
外表面涂装（m²）		540.6	1081.2

节段17~节段18拼接数量汇总表

规格（mm）	材质	单个合计	全桥共2个
t=44	Q420D	1129.4	2258.8
t=40		2976.6	5953.2
t=36		816.7	1633.4
t=28		1341	2682
t=24		964.8	1929.6
t=4		24.5	49
合计		7253.0	14506
t=44	Q355D	825.4	1650.8
t=28		608.9	1217.8
t=24		1541	3082
合计		2975.3	5950.6
M30x200	10.9S高强螺栓	3251.5	6503
外表面涂装（m²）		41.0	81.96

中交第二公路勘察设计研究院有限公司	狮子洋通道工程勘察设计 施 工 图 设 计	K6+418.3 新沙高架桥 边桁节段18设计图	设计	余汪千	复核	袁勤	一审	沈雁	二审	李忠	图号	SZYS/04/02/02/01/ 48

72550117376197

大样A（节段18~节段19）

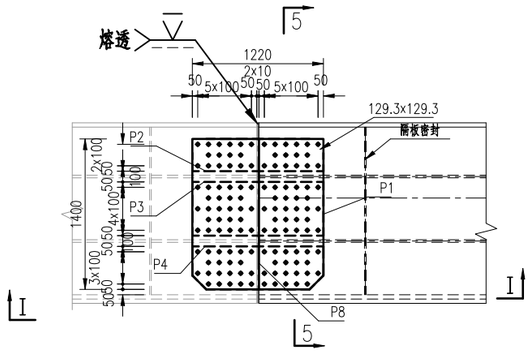

5-5

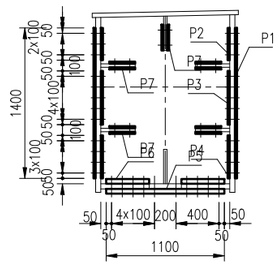

大样C（节段18~节段19）

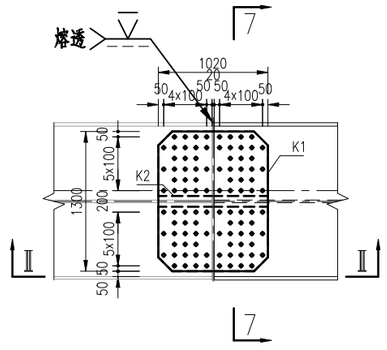

7-7

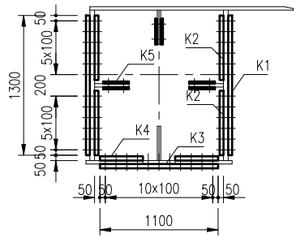

注：

1、本图尺寸均以mm计。

2、未注明的板件裁切边距M30螺栓不小50mm，M24螺栓不小40mm。

3、图中未注明的过焊孔圆弧切角半径为35mm。

4、图中未注明焊缝详见《钢梁焊缝及细节设计图》。

符号：

⊕ —— M30螺栓，开孔直径33mm

⊗ —— M24螺栓，开孔直径26mm

I－I

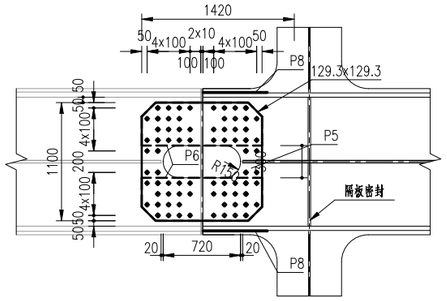

上弦杆顶板、腹板加劲肋拼接

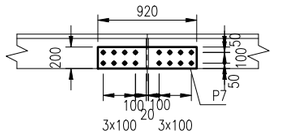

Ⅳ－Ⅳ

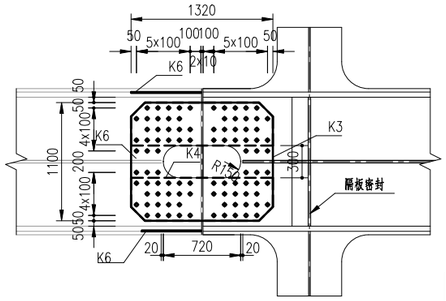

下弦杆顶板、腹板加劲肋拼接

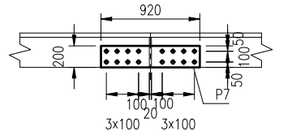

节段18~节段19拼接数量表

名称	编号	材质	规格	数量	单件重	共重（kg）	备注
上弦杆拼接	P1	Q355D	□1220×1400×28	2	375.9	751.8	
	P2		□1220×300×28	2	81.3	162.6	
	P3		□1220×500×28	2	134.1	268.2	
	P4		□1220×400×28	2	107.7	215.4	
	P5		□1420×1100×32	1	391.9	391.9	
	P6		□1420×400×32	2	143.2	286.4	
	P7		□920×200×20	10	28.3	283	
	P8		□600×1800×16	2	135.6	271.2	填板
	P9		□700×1100×16	1	96.7	96.7	填板
	M30高强螺栓	10.9S	M30×200	428	1.94	830.3	
下弦杆拼接	K1	Q355D	□1020×1300×24	2	250.6	501.2	
	K2		□1020×600×24	4	114.9	459.6	
	K3		□1320×1100×36	1	409.8	409.8	
	K4		□1320×400×36	2	149.8	299.6	
	K5		□920×200×20	6	28.3	169.8	
	K6		□500×1700×8	2	53.4	106.8	填板
	K7		□650×1100×4	1	22.6	22.6	填板
	M30高强螺栓	10.9S	M30×200	344	1.94	667.4	
腹杆拼接	L1	Q355D	□1520×1100×24	2	314.6	629.2	
	L2		□1520×500×24	4	143.2	572.8	
	L3		□1320×1100×28	1	318.7	318.7	
	L4		□1320×500×28	2	145.1	290.2	
	L5		□1520×1100×44	1	576.8	576.8	
	L6		□1520×240×44	2	124.3	248.6	
	L7		□1220×240×24	4	54.6	218.4	
	L8		□1320×240×24	2	60.3	120.6	
	M30高强螺栓	10.9S	M30×200	540	1.94	1047.6	

大样B（节段18~节段19）

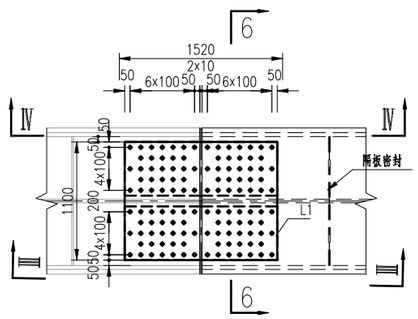

6-6

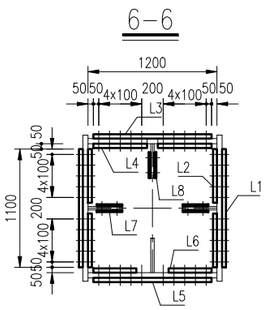

腹杆腹板加劲肋拼接

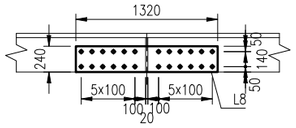

腹杆顶加劲肋拼接

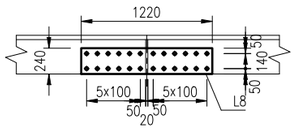

Ⅲ－Ⅲ

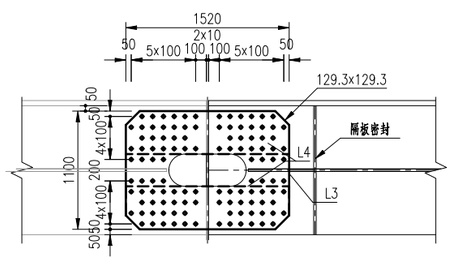

Ⅳ－Ⅳ

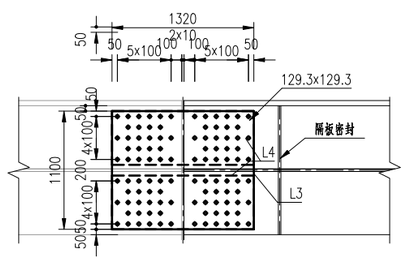

中交第二公路勘察设计研究院有限公司	狮子洋通道工程勘察设计 施 工 图 设 计	K6+418.3 新沙高架桥 边桁节段19设计图	设计	余汪千	复核	袁勤	一审	沈华	二审	李忠	图号	SZYS/04/02/02/01/ 49

节段19材料数量表

名称	编号	材质	规格	数量	单件重	共重（kg）	备注
上弦顶板	N11a	Q355D	t=20mm,A=11.85m2	1	1860.5	1860.5	
	N11b	Q355D	t=24mm,A=10.39m2	1	1958.2	1958.2	
上弦底板	N12a	Q355D	□7900×1200×20	1	1488.4	1488.4	
	N12b	Q355D	□7100×1200×24	1	1605.2	1605.2	
上弦节点板	N13	Q355D	t=40mm,A=20.38m2	2	6399.5	12799	
上弦腹板	N14	Q355D	□7300×1644×32	2	3014.4	6028.8	
上弦横隔板	N15	Q355D	□1580×1200×16	3	238.6	715.8	
	N15a	Q355D	□1576×1200×16	2	237.4	474.8	
	N15 '	Q355D	□1657x200x16	3	41.4	124.2	
	N15b	Q355D	□1782×40×4	4	2.2	8.8	
	N15c	Q355D	□600×400×16	4	30.1	120.4	
上弦加劲肋	N16a	Q355D	□7900×320×32	6	635.5	3813	
	N16b	Q355D	□7100×240×20	6	266.9	1601.4	
下弦顶板	N21a	Q355D	□7900×1850×20	1	2295.3	2295.3	
	N21b	Q355D	□7100×1850×20	1	2063	2063	
下弦底板	N22a	Q355D	t=20mm,A=12.53m2	1	1967.3	1967.3	
	N22b	Q355D	t=20mm,A=9.71m2	1	1525.1	1525.1	
下弦节点板	N23	Q355D	t=40mm,A=20.71m2	2	6503.8	13007.6	Z35钢
下弦腹板	N24	Q355D	□7300×1470×24	2	2021.5	4043	
下弦横隔板	N25	Q355D	□1450×1200×16	3	218.5	655.5	
	N25a	Q355D	□1450×1200×16	2	218.5	437	
	N25'	Q355D	□1657×200×16	3	41.4	124.2	
下弦加劲肋	N26a	Q355D	□7900×320×32	4	635.5	2542	
	N26b	Q355D	□7100×240×20	4	266.9	1067.6	
	N26c	Q355D	□15000×170×14	1	280.2	280.2	
斜腹杆	N31	Q355D	□11418×1200×36	1	3871.6	3871.6	
	N31a	Q355D	□11618×1200×36	1	3939.4	3939.4	
	N32	Q355D	□7218×1360×36	2	2775.1	5550.2	
	N33	Q355D	□7218×320×32	2	580.3	1160.6	
	N33a	Q355D	□10018×320×32	1	806.4	806.4	
	N33b	Q355D	□10218×320×32	1	821.4	821.4	
	N34	Q355D	□1200×1200×16	3	180.9	542.7	
	N41	Q355D	□3640×900×36	2	926.9	1853.8	
	N42	Q355D	□5940×1200×32	1	1791.1	1791.1	
	N43	Q355D	□5240×240×24	2	237.4	474.8	
	N51	Q355D	□5829×1200×36	1	1975.4	1975.4	
	N51a	Q355D	□5429×1200×36	1	1839.7	1839.7	
	N52	Q355D	□3629×1360×36	2	1396	2792	
节点板加劲	N53	Q355D	□3629×320×32	2	291.4	582.8	
	N53a	Q355D	□5129×320×32	1	412	412	
	N53b	Q355D	□4729×320×32	1	379.3	379.3	
	N54	Q355D	□1200×1200×16	3	180.9	542.7	
	N55	Q355D	□2300×320×32	2	185.9	371.8	
	N56	Q355D	□2600×320×32	4	208.5	834	
横梁接头	N61	Q355D	□1580×610×14	3	105.5	316.5	
	N61a	Q355D	□1576×618×14	2	106.6	213.2	
	N62	Q355D	t=24mm,A=0.47m2	3	87.8	263.4	
	N62a	Q355D	t=24mm,A=0.48m2	2	90.4	180.8	
	N63	Q355D	□1450×610×14	3	96.7	290.1	
	N63a	Q355D	□1450×626×14	2	100	200	
小计						94612	
焊缝重1.5%						1419.2	
合计						96031.2	

节段19材料数量汇总表

规格（mm）	材质	单个合计	全桥共2个
t=40	Q355D	25806.6	51613.2
t=36	Q355D	21822.1	43644.2
t=32	Q355D	19543.2	39086.4
t=24	Q355D	8525.4	17050.8
t=20	Q355D	13868.6	27737.2
t=16	Q355D	3737.3	7474.6
t=14	Q355D	1300	2600
t=4	Q355D	8.8	17.6
焊缝重（1.5%）		1419.2	2838.36
	Q355D	96031.2	192062.36
内表面涂装（m²）		320.7	641.4
外表面涂装（m²）		504.6	1009.2

节段18~节段19拼接数量汇总表

规格（mm）	材质	单个合计	全桥共2个
t=44	Q355D	825.4	1650.8
t=36	Q355D	709.4	1418.8
t=32	Q355D	678.3	1356.6
t=28	Q355D	2006.9	4013.8
t=24	Q355D	2501.8	5003.6
t=20	Q355D	452.8	905.6
t=16	Q355D	367.9	735.8
t=8	Q355D	106.8	213.6
t=4	Q355D	22.6	45.2
合计	Q355D	7671.9	15343.8
M30×200	10.9S高强螺栓	2545.3	5090.6
外表面涂装（m²）		38.2	76.48

中交第二公路勘察设计研究院有限公司	狮子洋通道工程勘察设计 施 工 图 设 计	K6+418.3 新沙高架桥 边桁节段19设计图	设计	余汪千	复核	袁勤	一审	张华	二审	李忠	图号	SZYS/04/02/02/01/ 49

大样A（节段19~节段20）

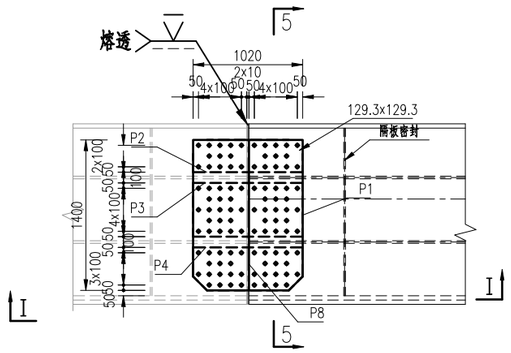

5-5

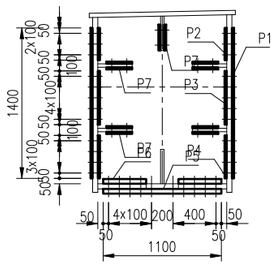

Ⅰ－Ⅰ

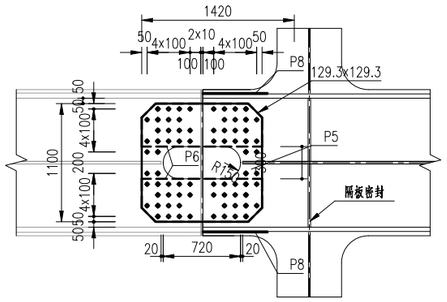

上弦杆顶板、腹板加劲肋拼接

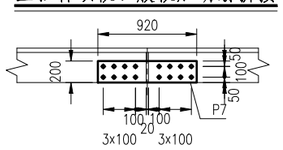

大样B（节段19~节段20）

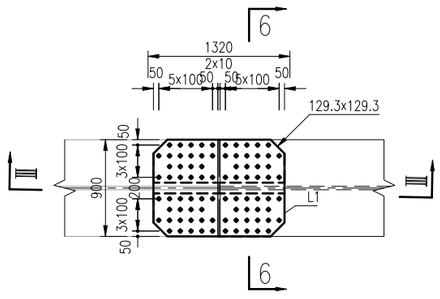

6-6

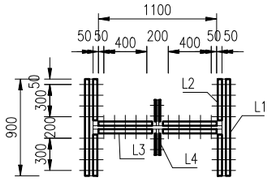

腹杆腹板加劲肋拼接

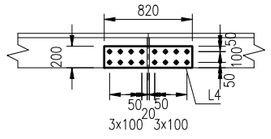

Ⅲ－Ⅲ

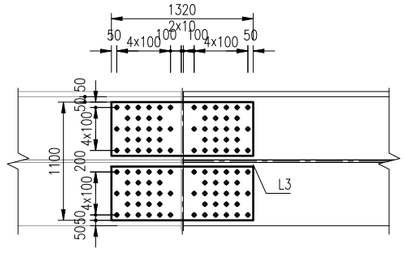

大样C（节段19~节段20）

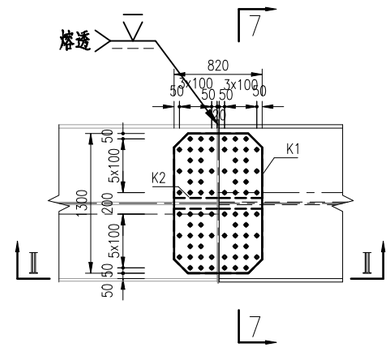

7-7

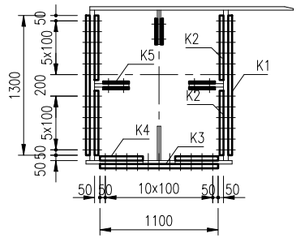

Ⅳ－Ⅳ

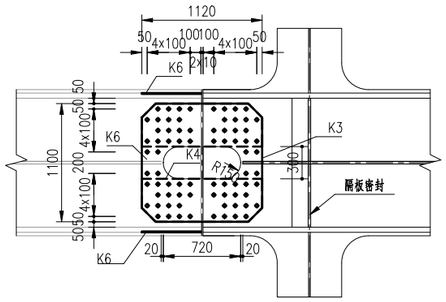

下弦杆顶板、腹板加劲肋拼接

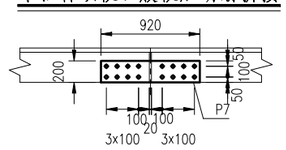

注：

1、本图尺寸均以mm计。

2、未注明的板件裁切边距M30螺栓不小50mm，M24螺栓不小40mm。

3、图中未注明的过焊孔圆弧切角半径为35mm。

4、图中未注明焊缝详见《钢梁焊缝及细节设计图》。

符号：

⊕ —— M30螺栓，开孔直径33mm

⊗ —— M24螺栓，开孔直径26mm

节段19~节段20拼接数量表

名称	编号	材质	规格	数量	单件重	共重（kg）	备注
上弦杆拼接	P1	Q355D	□1020×1400×16	2	179.6	359.2	
	P2		□1020×300×16	2	38.9	77.8	
	P3		□1020×500×16	2	64.1	128.2	
	P4		□1020×400×16	2	51.5	103	
	P5		□1420×1100×28	1	342.9	342.9	
	P6		□1420×400×28	2	125.3	250.6	
	P7		□920×200×20	10	28.3	283	
	P8		□500×1800×20	2	141.3	282.6	
	M30高强螺栓	10.9S	M30×200	380	1.94	737.2	
下弦杆拼接	K1	Q355D	□820×1300×20	2	168	336	
	K2		□820×600×20	4	76.9	307.6	
	K3		□1120×1100×32	1	309	309	
	K4		□1120×400×32	2	113	226	
	K5		□920×200×20	6	28.3	169.8	
	K6		□400×1700×16	2	85.4	170.8	
	M30高强螺栓	10.9S	M30×200	276	1.94	535.4	
腹杆拼接	L1	Q355D	□1320×900×28	2	261.6	523.2	
	L2		□1320×400×28	4	116.5	466	
	L3		□1320×500×28	4	145.1	580.4	
	L4		□820×200×20	4	25.1	100.4	
	M30高强螺栓	10.9S	M30×200	507	1.94	983.6	

中交第二公路勘察设计研究院有限公司	狮子洋通道工程勘察设计 施 工 图 设 计	K6+418.3 新沙高架桥 边桁节段20设计图	设计	余汪千	复核	袁勤	一审	沈华	二审	李忠	图号	SZYS/04/02/02/01/ 50

节段20材料数量表

名称	编号	材质	规格	数量	单件重	共重（kg）	备注
上弦顶板	N11a	Q355D	t=20mm,A=11.85m2	1	1860.5	1860.5	
	N11b	Q355D	t=20mm,A=10.39m2	1	1631.8	1631.8	
上弦底板	N12a	Q355D	□7900×1200×20	1	1488.4	1488.4	
	N12b	Q355D	□7300×1200×20	1	1375.3	1375.3	
上弦节点板	N13	Q355D	t=40mm,A=19.25m2	2	6045	12090	
上弦腹板	N14	Q355D	□7300×1648×20	2	1888.7	3777.4	
上弦横隔板	N15	Q355D	□1580×1200×16	3	238.6	715.8	
	N15a	Q355D	□1580×1200×16	2	238.6	477.2	
	N15 ‘	Q355D	□1657x200x16	3	41.4	124.2	
	N15b	Q355D	□1782×40×4	4	2.2	8.8	
	N15c	Q355D	□600×400×16	4	30.1	120.4	
上弦加劲肋	N16a	Q355D	□7900×240×20	4	298.3	1193.2	
	N16a’	Q355D	□7300×240×20	2	274.8	549.6	
	N16b	Q355D	□7300×240×20	6	274.8	1648.8	
下弦顶板	N21a	Q355D	□7900×1850×20	1	2295.3	2295.3	
	N21b	Q355D	□7100×1850×20	1	2063	2063	
下弦底板	N22a	Q355D	t=20mm,A=12.53m2	1	1967.3	1967.3	
	N22b	Q355D	t=20mm,A=9.71m2	1	1525.1	1525.1	
下弦节点板	N23	Q355D	t=40mm,A=18.38m2	2	5771	11542	Z35钢
下弦腹板	N24	Q355D	□7300×1470×24	2	2021.5	4043	
下弦横隔板	N25	Q355D	□1450×1200×16	3	218.5	655.5	
	N25a	Q355D	□1450×1200×16	2	218.5	437	
	N25’	Q355D	□1657×200×16	3	41.4	124.2	
下弦加劲肋	N26a	Q355D	□7900×240×20	4	298.3	1193.2	
	N26b	Q355D	□7100×240×20	4	266.9	1067.6	
	N26c	Q355D	□15000×170×14	1	280.2	280.2	
斜腹杆	N31	Q355D	□7227×900×36	2	1836.9	3673.8	
	N32	Q355D	□12027×1200×32	1	3624.8	3624.8	
	N33	Q355D	□10627×240×24	2	480.4	960.8	
	N41	Q355D	□3657×900×36	2	929.8	1859.6	
	N42	Q355D	□5957×1200×32	1	1796.1	1796.1	
	N43	Q355D	□5257×240×24	2	237.4	474.8	
	N51	Q355D	□3640×900×36	2	926.9	1853.8	
	N52	Q355D	□6240×1200×32	1	1881.5	1881.5	
	N53	Q355D	□5540×240×24	2	250.6	501.2	
节点板加劲	N54	Q355D	□878×1200×20	1	164.9	164.9	
	N55	Q355D	□1030×1200×20	1	194.7	194.7	
横梁接头	N61	Q355D	□1580×610×14	3	105.5	316.5	
	N61a	Q355D	□1580×630×14	2	109.9	219.8	
	N62	Q355D	t=24mm,A=0.47m2	3	87.8	263.4	
	N62a	Q355D	t=24mm,A=0.48m2	2	90.4	180.8	
	N63	Q355D	□1450×610×14	3	96.7	290.1	
	N63a	Q355D	□1450×626×14	2	100	200	
小计						72711.4	
焊缝重1.5%						1090.7	
合计						73802.1	

节段20材料数量汇总表

规格（mm）	材质	单个合计	全桥共2个
t=40	Q355D	23632	47264
t=36	Q355D	7387.2	14774.4
t=32	Q355D	7302.4	14604.8
t=24	Q355D	6424	12848
t=20	Q355D	23996.1	47992.2
t=16	Q355D	2654.3	5308.6
t=14	Q355D	1306.6	2613.2
t=4	Q355D	8.8	17.6
焊缝重（1.5%）		1090.7	2181.342
合计	Q355D	73802.1	147604.142
内表面涂装（m²）		273.0	546
外表面涂装（m²）		428.4	856.8

节段19~节段20拼接数量汇总表

规格（mm）	材质	单个合计	全桥共2个
t=32	Q355D	535	1070
t=28	Q355D	2163.1	4326.2
t=20	Q355D	1479.4	2958.8
t=16	Q355D	839	1678
合计	Q355D	5016.5	10033
M30x200	10.9S高强螺栓	2256.2	4512.4
外表面涂装（m²）		28.1	56.14

中交第二公路勘察设计研究院有限公司	狮子洋通道工程勘察设计 施 工 图 设 计	K6+418.3 新沙高架桥 边桁节段20设计图	设计	余汪千	复核	袁勤	一审	沈华	二审	李忠	图号	SZYS/04/02/02/01/ 50

大样A（节段20~节段21）

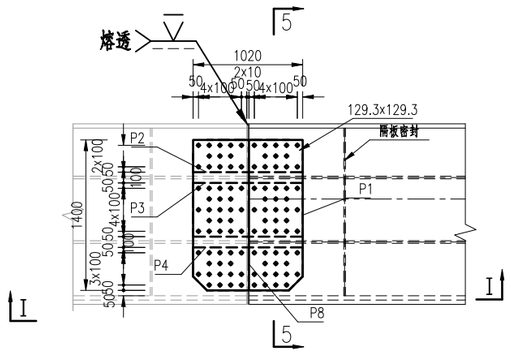

5-5

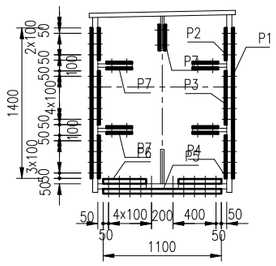

Ⅰ－Ⅰ

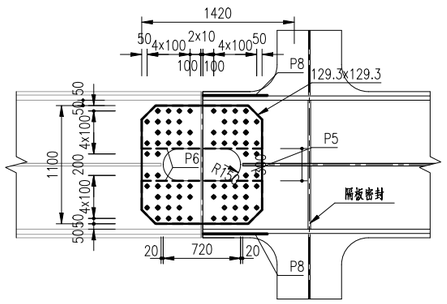

上弦杆顶板、腹板加劲肋拼接

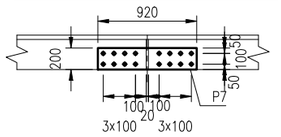

大样C（节段20~节段21）

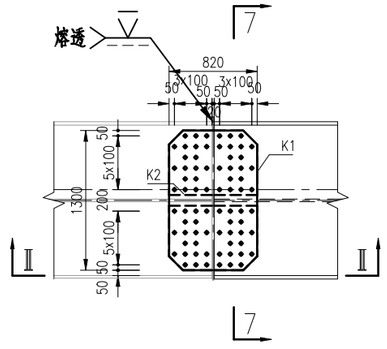

7-7

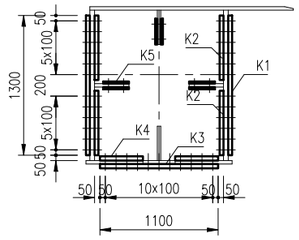

Ⅳ－Ⅳ

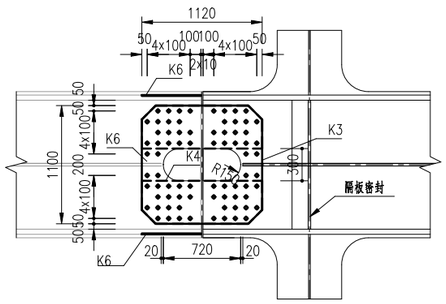

下弦杆顶板、腹板加劲肋拼接

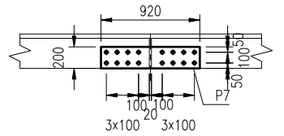

注：

1、本图尺寸均以mm计。

2、未注明的板件裁切边距M30螺栓不小50mm，M24螺栓不小40mm。

3、图中未注明的过焊孔圆弧切角半径为35mm。

4、图中未注明焊缝详见《钢梁焊缝及细节设计图》。

符号：

⊕ —— M30螺栓，开孔直径33mm

⊗ —— M24螺栓，开孔直径26mm

大样B（节段20~节段21）

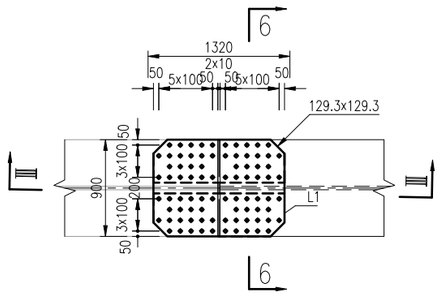

6-6

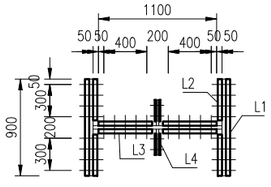

腹杆腹板加劲肋拼接

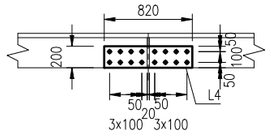

Ⅲ－Ⅲ

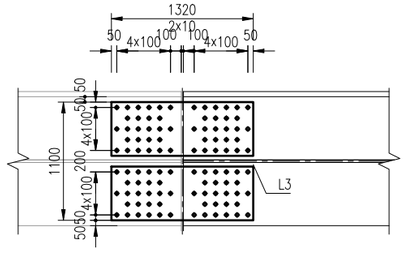

节段20~节段21拼接数量表

名称	编号	材质	规格	数量	单件重	共重（kg）	备注
上弦杆拼接	P1	Q355D	□1020×1400×16	2	179.6	359.2	
	P2		□1020×300×16	2	38.9	77.8	
	P3		□1020×500×16	2	64.1	128.2	
	P4		□1020×400×16	2	51.5	103	
	P5		□1420×1100×28	1	342.9	342.9	
	P6		□1420×400×28	2	125.3	250.6	
	P7		□920×200×20	10	28.3	283	
	P8		□500×1800×20	2	141.3	282.6	
	M30高强螺栓	10.9S	M30x200	380	1.94	737.2	
下弦杆拼接	K1	Q355D	□820×1300×20	2	168	336	
	K2		□820×600×20	4	76.9	307.6	
	K3		□1120×1100×32	1	309	309	
	K4		□1120×400×32	2	113	226	
	K5		□920×200×20	6	28.3	169.8	
	K6		□400×1700×16	2	85.4	170.8	
	M30高强螺栓	10.9S	M30x200	276	1.94	535.4	
腹杆拼接	L1	Q355D	□1320×900×28	2	261.6	523.2	
	L2		□1320×400×28	4	116.5	466	
	L3		□1320×500×28	4	145.1	580.4	
	L4		□820×200×20	4	25.1	100.4	
	M30高强螺栓	10.9S	M30x200	507	1.94	983.6	

中交第二公路勘察设计研究院有限公司	狮子洋通道工程勘察设计 施 工 图 设 计	K6+418.3 新沙高架桥 边桁节段21设计图	设计	余汪千	复核	李勤	一审	张华	二审	李忠	图号	SZYS/04/02/02/01/ 51

42550118030101

节段21材料数量表

名称	编号	材质	规格	数量	单件重	共重（kg）	备注
上弦顶板	N11a	Q355D	t=20mm,A=11.85m2	1	1860.5	1860.5	
	N11b	Q355D	t=20mm,A=12.8m2	1	2010	2010	
上弦底板	N12a	Q355D	□7900×1200×20	1	1488.4	1488.4	
	N12b	Q355D	□8800×1200×20	1	1657.9	1657.9	
上弦节点板	N13	Q355D	t=40mm,A=19.21m2	2	6031.8	12063.6	
上弦腹板	N14	Q355D	□8800×1648×20	2	2276.5	4553	
上弦横隔板	N15	Q355D	□1580×1200×16	3	238.6	715.8	
	N15a	Q355D	□1580×1200×16	2	238.6	477.2	
	N15 ‘	Q355D	□1657x200x16	3	41.4	124.2	
	N15b	Q355D	□1782×40×4	4	2.2	8.8	
	N15c	Q355D	□600×400×16	4	30.1	120.4	
上弦加劲肋	N16a	Q355D	□7900×240×20	6	298.3	1789.8	
	N16b	Q355D	□8800×240×20	6	331.3	1987.8	
下弦顶板	N21a	Q355D	□7900×1850×20	1	2295.3	2295.3	
	N21b	Q355D	□10100×1850×20	1	2934.3	2934.3	
下弦底板	N22a	Q355D	t=20mm,A=12.53m2	1	1967.3	1967.3	
	N22b	Q355D	t=20mm,A=14.16m2	1	2223.5	2223.5	
下弦节点板	N23	Q355D	t=40mm,A=18.38m2	2	5769.8	11539.6	Z35钢
下弦腹板	N24	Q355D	□10300×1470×24	2	2852.4	5704.8	
下弦横隔板	N25	Q355D	□1450×1200×16	3	218.5	655.5	
	N25a	Q355D	□1450×1200×16	2	218.5	437	
	N25'	Q355D	□1657×200×16	3	41.4	124.2	
下弦加劲肋	N26a	Q355D	□7900×240×20	4	298.3	1193.2	
	N26b	Q355D	□10100×240×20	4	379.9	1519.6	
	N26c	Q355D	□18000×170×14	1	336.3	336.3	
斜腹杆	N31	Q355D	□8075×900×36	2	2054.5	4109	
	N32	Q355D	□12975×1200×32	1	3911.2	3911.2	
	N33	Q355D	□11575×240×24	2	523.8	1047.6	
	N41	Q355D	□4054×900×36	2	1031.5	2063	
	N42	Q355D	□6404×1200×32	1	1929.2	1929.2	
	N43	Q355D	□5704×240×24	2	258.1	516.2	
	N51	Q355D	□3657×900×36	2	929.8	1859.6	
	N52	Q355D	□6257×1200×32	1	1886.5	1886.5	
	N53	Q355D	□5557×240×24	2	250.6	501.2	
节点板加劲	N54	Q355D	□904×1200×20	1	169.6	169.6	
	N55	Q355D	□1114×1200×20	1	210.4	210.4	
横梁接头	N61	Q355D	□1580×610×14	3	105.5	316.5	
	N61a	Q355D	□1580×630×14	3	109.9	329.7	
	N62	Q355D	t=24mm,A=0.47m2	3	87.8	263.4	
	N62a	Q355D	t=24mm,A=0.48m2	3	90.4	271.2	
	N63	Q355D	□1450×610×14	3	96.7	290.1	
	N63a	Q355D	□1450×626×14	3	100	300	
小计						79762.4	
焊缝重1.5%						1196.4	
合计						80958.8	

节段21材料数量汇总表

规格（mm）	材质	单个合计	全桥共2个
t=40	Q355D	23603.2	47206.4
t=36	Q355D	8031.6	16063.2
t=32	Q355D	7726.9	15453.8
t=24	Q355D	8304.4	16608.8
t=20	Q355D	27860.6	55721.2
t=16	Q355D	2654.3	5308.6
t=14	Q355D	1572.6	3145.2
t=4	Q355D	8.8	17.6
焊缝重（1.5%）		1196.4	2392.9
	Q355D	80958.8	161917.7
内表面涂装（m²）		308.0	616
外表面涂装（m²）		475.3	950.6

节段20~节段21拼接数量汇总表

规格（mm）	材质	单个合计	全桥共2个
t=32	Q355D	535	1070
t=28	Q355D	2163.1	4326.2
t=20	Q355D	1479.4	2958.8
t=16	Q355D	839	1678
合计	Q355D	5016.5	10033
M30x200	10.9S高强螺栓	2256.2	4512.4
外表面涂装（m²）		28.1	56.14

中交第二公路勘察设计研究院有限公司	狮子洋通道工程勘察设计 施 工 图 设 计	K6+418.3 新沙高架桥 边桁节段21设计图	设计	余汪千	复核	袁勤	一审	张华	二审	李忠	图号	SZYS/04/02/02/01/ 51

72550818 0007277

大样A（节段21~节段22）

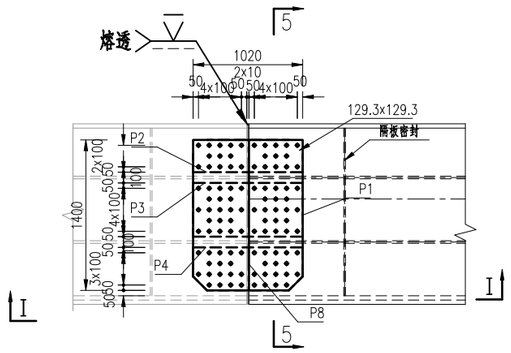

5-5

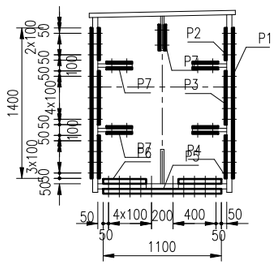

Ⅰ－Ⅰ

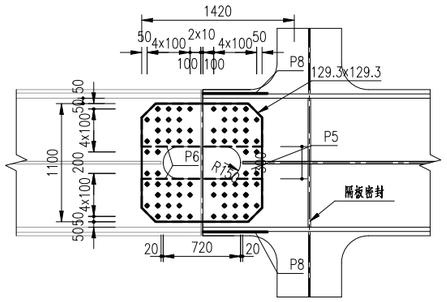

上弦杆顶板、腹板加劲肋拼接

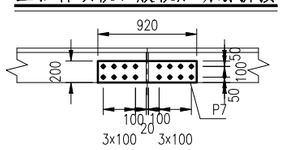

大样C（节段21~节段22）

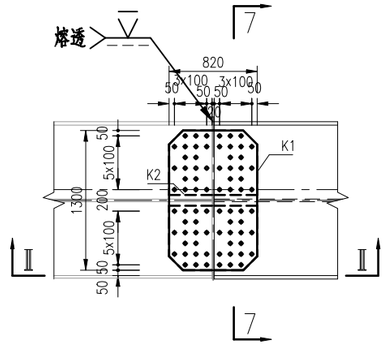

7-7

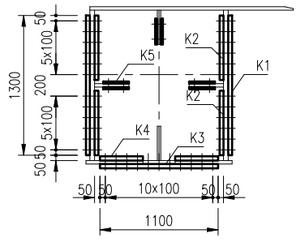

Ⅳ－Ⅳ

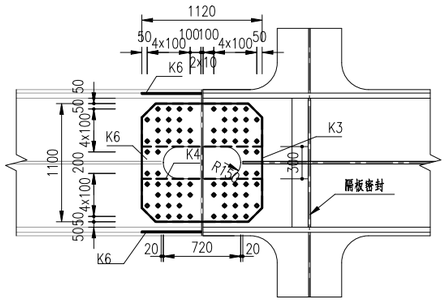

下弦杆顶板、腹板加劲肋拼接

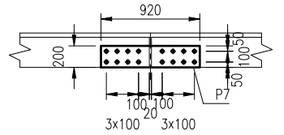

注：

1、本图尺寸均以mm计。

2、未注明的板件裁切边距M30螺栓不小50mm，M24螺栓不小40mm。

3、图中未注明的过焊孔圆弧切角半径为35mm。

4、图中未注明焊缝详见《钢梁焊缝及细节设计图》。

符号：

⊕ —— M30螺栓，开孔直径33mm

⊗ —— M24螺栓，开孔直径26mm

大样B（节段21~节段22）

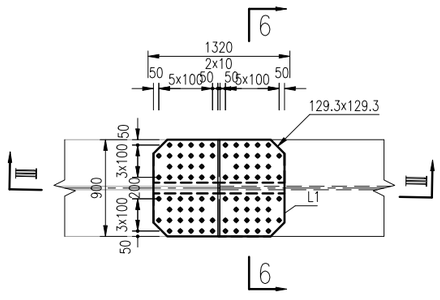

6-6

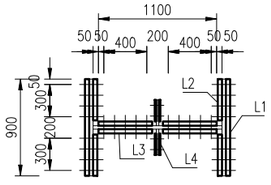

腹杆腹板加劲肋拼接

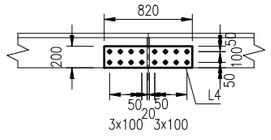

Ⅲ－Ⅲ

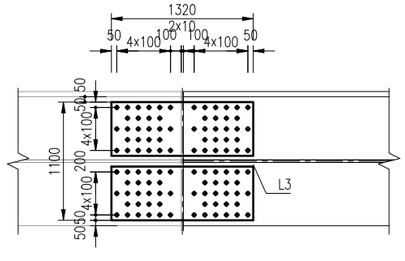

节段21~节段22拼接数量表

名称	编号	材质	规格	数量	单件重	共重（kg）	备注
上弦杆拼接	P1	Q355D	□1020×1400×16	2	179.6	359.2	
	P2		□1020×300×16	2	38.9	77.8	
	P3		□1020×500×16	2	64.1	128.2	
	P4		□1020×400×16	2	51.5	103	
	P5		□1420×1100×28	1	342.9	342.9	
	P6		□1420×400×28	2	125.3	250.6	
	P7		□920×200×20	10	28.3	283	
	P8		□500×1800×20	2	141.3	282.6	
	M30高强螺栓	10.9S	M30x200	380	1.94	737.2	
下弦杆拼接	K1	Q355D	□820×1300×20	2	168	336	
	K2		□820×600×20	4	76.9	307.6	
	K3		□1120×1100×32	1	309	309	
	K4		□1120×400×32	2	113	226	
	K5		□920×200×20	6	28.3	169.8	
	K6		□400×1700×16	2	85.4	170.8	
	M30高强螺栓	10.9S	M30x200	276	1.94	535.4	
腹杆拼接	L1	Q355D	□1320×900×28	2	261.6	523.2	
	L2		□1320×400×28	4	116.5	466	
	L3		□1320×500×28	4	145.1	580.4	
	L4		□820×200×20	4	25.1	100.4	
	M30高强螺栓	10.9S	M30x200	507	1.94	983.6	

中交第二公路勘察设计研究院有限公司	狮子洋通道工程勘察设计 施 工 图 设 计	K6+418.3 新沙高架桥 边桁节段22设计图	设计	余汪千	复核	袁勤	一审	沈华	二审	王忠	图号	SZYS/04/02/02/01/ 52

725501181589378

节段22材料数量表

名称	编号	材质	规格	数量	单件重	共重（kg）	备注
上弦顶板	N11	Q355D	t=20mm,A=35.41m2	1	5559.4	5559.4	
上弦底板	N12	Q355D	□23700x1200x20	1	4465.1	4465.1	
上弦腹板	N13	Q355D	t=20mm,A=16.97m2	2	2664.3	5328.6	
上弦节点板	N14	Q355D	t=28mm,A=10.71m2	2	2354.1	4708.2	
	N14a	Q355D	t=40mm,A=20.8m2	2	6531.2	13062.4	
上弦横隔板	N15a	Q355D	□1580x1200x16	6	238.6	1431.6	
	N15b	Q355D	□1580x1200x16	3	238.6	715.8	
	N15 ‘	Q355D	□1657x200x16	7	41.4	289.8	
	N15b	Q355D	□1782×40×4	4	2.2	8.8	
	N15c	Q355D	□600×400×16	4	30.1	120.4	
上弦加劲肋	N16a	Q355D	□5651x240x20	4	213.5	854	
	N16b	Q355D	□7700x240x20	4	290.5	1162	
	N16c	Q355D	□70300x240x20	4	2648.6	10594.4	
	N16d	Q355D	□23650x240x20	1	891.8	891.8	
	N16e	Q355D	□23650x240x20	1	891.8	891.8	
下弦顶板	N21	Q355D	□4809x1850x20	1	1397.3	1397.3	
	N21a	Q355D	□17804x1850x20	1	5171.6	5171.6	
下弦底板	N22	Q355D	t=36mm,A=9.73m2	1	2749.7	2749.7	
	N22a	Q355D	t=20mm,A=26.07m2	1	4093.1	4093.1	
下弦腹板	N23	Q355D	□10103x1470x24	2	2797.7	5595.4	
下弦节点板	N24	Q355D	t=40mm,A=16.6m2	2	5211.1	10422.2	Z35钢
	N24a	Q355D	t=40mm,A=21.3m2	2	6688.2	13376.4	Z35钢
下弦横隔板	N25	Q355D	□1450x1200x16	1	218.5	218.5	
	N25’	Q355D	□1657x200x16	5	41.4	207	
	N25a	Q355D	□1450x1200x16	6	218.5	1311	
下弦加劲肋	N26a	Q355D	□2792x320x32	2	223.6	447.2	
	N26b	Q355D	□10103x240x20	2	379.9	759.8	
	N26c	Q355D	□7700x240x20	2	290.5	581	
	N26d	Q355D	□17803x240x20	2	670.4	1340.8	
	N26d’	Q355D	□2983x320x32	2	238.6	477.2	
	N26e	Q355D	□20592x170x14	1	384.7	384.7	
斜腹杆	N31	Q355D	□11768×1200×36	1	3990.3	3990.3	
	N31a	Q355D	□12368×1200×36	1	4193.8	4193.8	
	N32	Q355D	□7568×1360×36	2	2908	5816	
	N33	Q355D	□7568×320×32	2	607.9	1215.8	
	N33a	Q355D	□10368×320×32	1	834	834	
	N33b	Q355D	□10968×320×32	1	881.7	881.7	
	N34	Q355D	□1200×1200×16	3	180.9	542.7	
	N41	Q355D	□11917×1200×36	1	4041.2	4041.2	
	N41a	Q355D	□12317×1200×36	1	4176.8	4176.8	
	N42	Q355D	□7717×1360×36	2	2967.3	5934.6	
	N43	Q355D	□7717×320×32	2	620.5	1241	
	N43a	Q355D	□11217×320×32	1	901.8	901.8	
	N43b	Q355D	□11617×320×32	1	934.5	934.5	
	N44	Q355D	□1200×1200×16	3	180.9	542.7	
竖腹杆顶底板	N51	Q355D	□10637x1200x20	1	2003.3	2003.3	
	N51a	Q355D	□9087x1200x20	1	1711.3	1711.3	
竖腹杆腹板	N52	Q355D	□6737x1500x20	2	1587.3	3174.6	
竖腹杆横隔板	N54	Q355D	□1400x1200x16	3	211	633	
竖腹杆加劲肋	N53	Q355D	□6737x190x16	2	160.8	321.6	
	N53a	Q355D	□9237x190x16	1	221.1	221.1	
	N53b	Q355D	□7687x190x16	1	183.4	183.4	
下弦节点板加劲	N61	Q355D	□3150x320x32	2	253.7	507.4	
	N62	Q355D	□2800x320x32	2	226.1	452.2	
	N63	Q355D	□750x320x28	2	52.8	105.6	
	N64	Q355D	□2300x320x32	2	185.9	371.8	
	N65	Q355D	□2300x320x32	2	185.9	371.8	
	N66	Q355D	□2600x320x32	3	208.5	625.5	
斜腹杆	N67	Q355D	□3904×900×36	2	991.9	1983.8	
	N68	Q355D	□6504×1200×32	1	1959.4	1959.4	
	N69	Q355D	□5804×240×24	2	261.9	523.8	
横梁接头	N71	Q355D	□1580x610x16	3	120.6	361.8	
	N71a	Q355D	□1580x622x16	3	123.1	369.3	
	N71b	Q355D	□1580x630x16	3	125.6	376.8	
	N72	Q355D	t=24mm,A=0.47m2	3	88.4	265.2	
	N72’	Q355D	t=24mm,A=0.48m2	4	90.4	361.6	
	N72a	Q355D	t=24mm,A=0.97m2	1	182	182	
	N73	Q355D	□1450x626x16	3	114.3	342.9	
	N73a	Q355D	□1450x610x16	6	110.5	663	
支承加劲肋	N81	Q355D	□1450x1200x32	4	437.1	1748.4	
	N82	Q355D	□502x240x20	1	18.8	18.8	
	N83	Q355D	□1800x1800x80	1	2034.7	2034.7	
	N84	Q355D	□1000x568x32	3	143.2	429.6	
	N85	Q355D	□1350x570x32	6	193.4	1160.4	
	N86	Q355D	□2200x650x32	1	359.2	359.2	
小计						157687.2	
焊缝重1.5%						2365.3	
合计						160052.5	

节段22材料数量汇总表

规格（mm）	材质	单个合计	全桥共2个
t=80	Q355D	2034.7	4069.4
t=40		36861	73722.0
t=36		32886.2	65772.4
t=32		14918.9	29837.8
t=28		4813.8	9627.6
t=24		6928	13856.0
t=20		49998.7	99997.4
t=16		8852.4	17704.8
t=14		384.7	769.4
t=4		8.8	17.6
焊缝重（1.5%）		2365.3	4730.6
		160052.5	320105.0
内表面涂装（m²）		1046.9	2093.8
外表面涂装（m²）		448.7	897.4

节段21~节段22拼接数量汇总表

规格（mm）	材质	单个合计	全桥共2个
t=32	Q355D	535	1070
t=28	Q355D	2163.1	4326.2
t=20	Q355D	1479.4	2958.8
t=16	Q355D	839	1678
合计	Q355D	5016.5	10033
M30x200	10.9S高强螺栓	2256.2	4512.4
外表面涂装（m²）		28.1	56.14

中交第二公路勘察设计研究院有限公司	狮子洋通道工程勘察设计 施 工 图 设 计	K6+418.3 新沙高架桥 边桁节段22设计图	设计	余汪千	复核	袁勤	一审	沈雁	二审	王忠	图号	SZYS/04/02/02/01/ 52

材料数量表

名称	编号	材质	规格(mm)	数量	单件重(kg)	共重(kg)	备注(㎡)
横梁顶板	T1	Q355D	□17503x600x20	228	1648.5	375858.0	
横梁腹板	T2		□17500x1955x14	228	3408.0	777024.0	A=31.01
横梁底板	T3		□17500x700x24	228	2307.9	526201.2	
横梁加劲板	T4		□1510x150x12	4560	19.8	90288.0	A=0.21
	T4a		□1632x293x12	456	31.1	14181.6	A=0.33
小纵梁顶板	T5		□2380x600x12	202	134.7	27209.4	
	T5a		□2180x600x12	20	123.4	2468.0	
	T5b		□1880x600x12	4	106.4	425.6	
	T5c		□1472x600x12	4	82.9	331.6	
小纵梁腹板	T6		□2380x500x12	202	112.1	22644.2	
	T6a		□2180x500x12	20	102.7	2054.0	
	T6b		□1880x500x12	4	88.5	354.0	
	T6c		□1472x500x12	4	69.7	278.8	
小纵梁底板	T7		□2380x300x12	202	66.9	13513.8	
	T7a		□2180x300x12	20	61.2	1224.0	
	T7b		□1880x300x12	4	52.8	211.2	
	T7c		□1472x300x12	4	41.4	165.6	
端横梁顶板	T21		□17503x1758x20	4	4149.5	16598.0	A=26.43
端横梁腹板	T22		□17500x1955x20	4	4868.6	19474.4	A=31.01
	T22'		□17500x1955x20	4	4797.9	19191.6	A=30.56
端横梁底板	T23		□17500x1500x24	4	4945.5	19782.0	
端横梁加劲板	T24		□1510x220x16	48	38.9	1867.2	A=0.31
	T25		□1396x1782x12	20	210.1	4202.0	A=2.23
端横梁隔板加劲	T26		□2018x160x12	20	30.1	602.0	
小纵梁腹板接头	T27		□784x292x12	4	18.8	75.2	A=0.2
线缆孔加劲	T30		□1374x300x14	236	45.1	10643.6	
小纵梁拼接板	T50		□400x330x12	920	12.2	11224.0	
横梁拼接板	T60		□1840x340x10	456	49.5	22572.0	
	T61		□1440x340x10	456	38.5	17556.0	
	T62		□1840x340x14	16	69.2	1107.2	
	T63		□1440x340x14	16	53.9	862.4	
小计						2000190.6	
焊缝重1.5%						30002.9	
合计						2030193.5	
外表面涂装(㎡)						30772.9	
M24高强螺栓(套)				32144	0.8	26229.5	

材料数量汇总表

规格(mm)	材质	合计(kg)
t=24	Q355D	545983.2
t=20		431122.0
t=16		1867.2
t=14		789637.2
t=12		191453.0
t=10		40128.0
焊缝重(1.5%)		30002.9
合计(kg)		2030193.5
外表面涂装(㎡)		30772.9
M24高强螺栓		26229.5

中交第二公路勘察设计研究院有限公司	狮子洋通道工程勘察设计 施 工 图 设 计	K6+418.3 新沙高架桥 上层桥面系设计图	设计	刘川	复核	袁勤	一审	沈维	二审	李忠	图号	SZYS/04/02/02/01/53

7286/05 1302574

下层桥面系材料数量表

名称	编号	材质	规格(mm)	数量	单件重(kg)	共重(kg)	备注(m²)
桥面板	D1	Q355D	□17503x343160x14	2	660095.7	1320191.4	
横梁腹板	D2		□17500x1800x14	222	3122.3	693150.6	A=28.41
	D2a		□13800x1761x20	12	3444.6	41335.2	A=21.94
	D2a'		□13800x1761x20	8	3516.8	28134.4	A=22.4
	D2b		□1740x1485x28	8	562.7	4501.6	A=2.56
	D2c		□1940x1800x28	8	760.5	6084.0	A=3.46
	D2d		□1740x1485x60	8	1205.8	9646.4	A=2.56
	D2e		□1940x1800x44	8	1195.1	9560.8	A=3.46
横梁底板	D3		□17500x600x24	222	1978.2	439160.4	
	D3a		□17500x2160x24	4	7121.5	28486.0	
	D3a'		□17350x2160x24	4	7061.2	28244.8	
横梁加劲	D4		□1240x150x12	4440	17.9	79476.0	
	D4a		□1640x1780x12	40	250.6	10024.0	A=2.66
	D4b		□1640x880x12	80	111.2	8896.0	A=1.18
U肋封端隔板	D5		□284x272x4	2052	1.9	3898.8	A=0.06
板肋	DL		□342042x170x14	6	6390.7	38344.2	
U肋	DU		□342042x710x8	54	15251.0	823554.0	
端横梁板肋	D7		□16191x200x16	8	406.9	3255.2	
	D7a		□17500x200x16	4	439.6	1758.4	
箱型横梁隔板加劲	D8		□2018x160x12	120	30.1	3612.0	
端横梁腹板加劲	D9		□450x392x14	72	9.9	712.8	A=0.09
临时支撑加劲	D10		□800x166x28	64	26.4	1689.6	A=0.12
	D10'		□800x160x28	72	26.4	1900.8	A=0.12
	D10''		□800x158x28	72	26.4	1900.8	A=0.12
临时支撑垫板	D20		□600x360x50	16	86.4	1382.4	
临时支撑垫板	D30		□900x360x50	24	125.6	3014.4	
横梁拼接板	D60		□1680x340x10	444	44.7	19846.8	
	D61		□1280x340x10	444	34.5	15318.0	
U肋连接内衬板	D70		□697x60x6	2052	1.9	3898.8	
小计						3630978.6	
焊缝重1.5%						54464.7	
合计						3685443.3	
外表面涂装(m²)						60307.8	
内表面涂装(m²)						13237.0	
M24高强螺栓(套)				23088	0.8	18839.8	

下层桥面系数量汇总表

规格(mm)	材质	合计(kg)
t=60	Q355D	9646.4
t=50		4396.8
t=44		9560.8
t=28		16076.8
t=24		495891.2
t=20		69469.6
t=16		5013.6
t=14		2052399.0
t=12		102008.0
t=10		35164.8
t=8		823554.0
t=6		3898.8
t=4		3898.8
焊缝重(1.5%)		54464.7
合计(kg)		3685443.3
内表面涂装(m²)		13237.0
外表面涂装(m²)		60307.8
M24高强螺栓		18839.8

中交第二公路勘察设计研究院有限公司	狮子洋通道工程勘察设计 施 工 图 设 计	K6+418.3 新沙高架桥 下层桥面系设计图	设计	刘川	复核	老勤	一审	沈雄	二审	李忠	图号	SZYS/04/02/02/01/ 54

检修人孔气密门正面

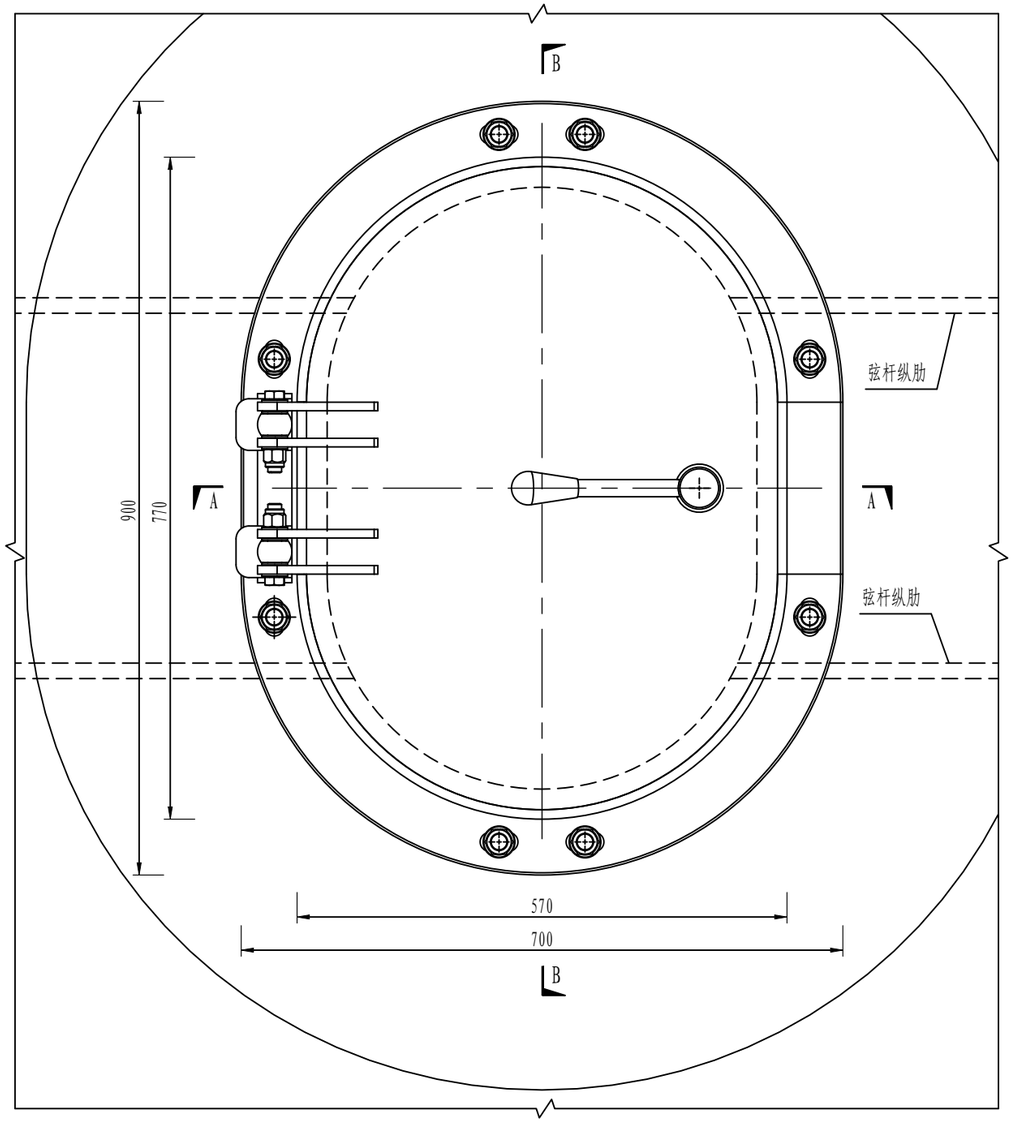

A-A

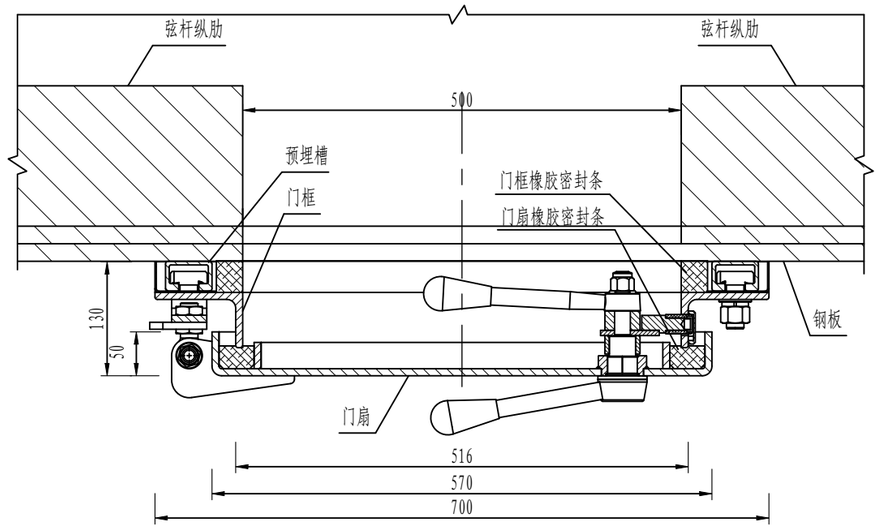

(单套)工程量总表

序号	材料名称	规格(mm)	数量	材料	单重(Kg)	总重(Kg)	总涂装（m^2）
1	人孔密封门门扇	-	1	Q235	69.24	69.24	1.43
2	人孔密封门门框	-	1	Q235	51.86	51.86	1.50
3	门扇橡胶密封条	-	1	三元乙丙	-	-	-
4	门框橡胶密封条	-	1	三元乙丙	-	-	-
5	5334预埋槽	367	2	Q345	2.44	4.89	0.20
6	5334预埋槽	167	2	Q345	1.11	2.21	0.10
重量总计（Kg）							128.19
涂装总计（m^2）							3.23

注

1、本图尺寸均以mm为单位。

2、本图适用狮子洋上下层箱型横梁检修人洞气密门。

3、设计门的数量为上层4套，下层12套。

4、门的表面处理是喷塑，环氧低粉80μm+超耐候面粉80μm。

中交第二公路勘察设计研究院有限公司	狮子洋通道工程勘察设计 施 工 图 设 计	K6+418.3 新沙高架桥 下层桥面系设计图	设计	刘川	复核	袁勤	一审	沈维	二审	李忠	图号	SZYS/04/02/02/01/54

上层桥面板总体布置图

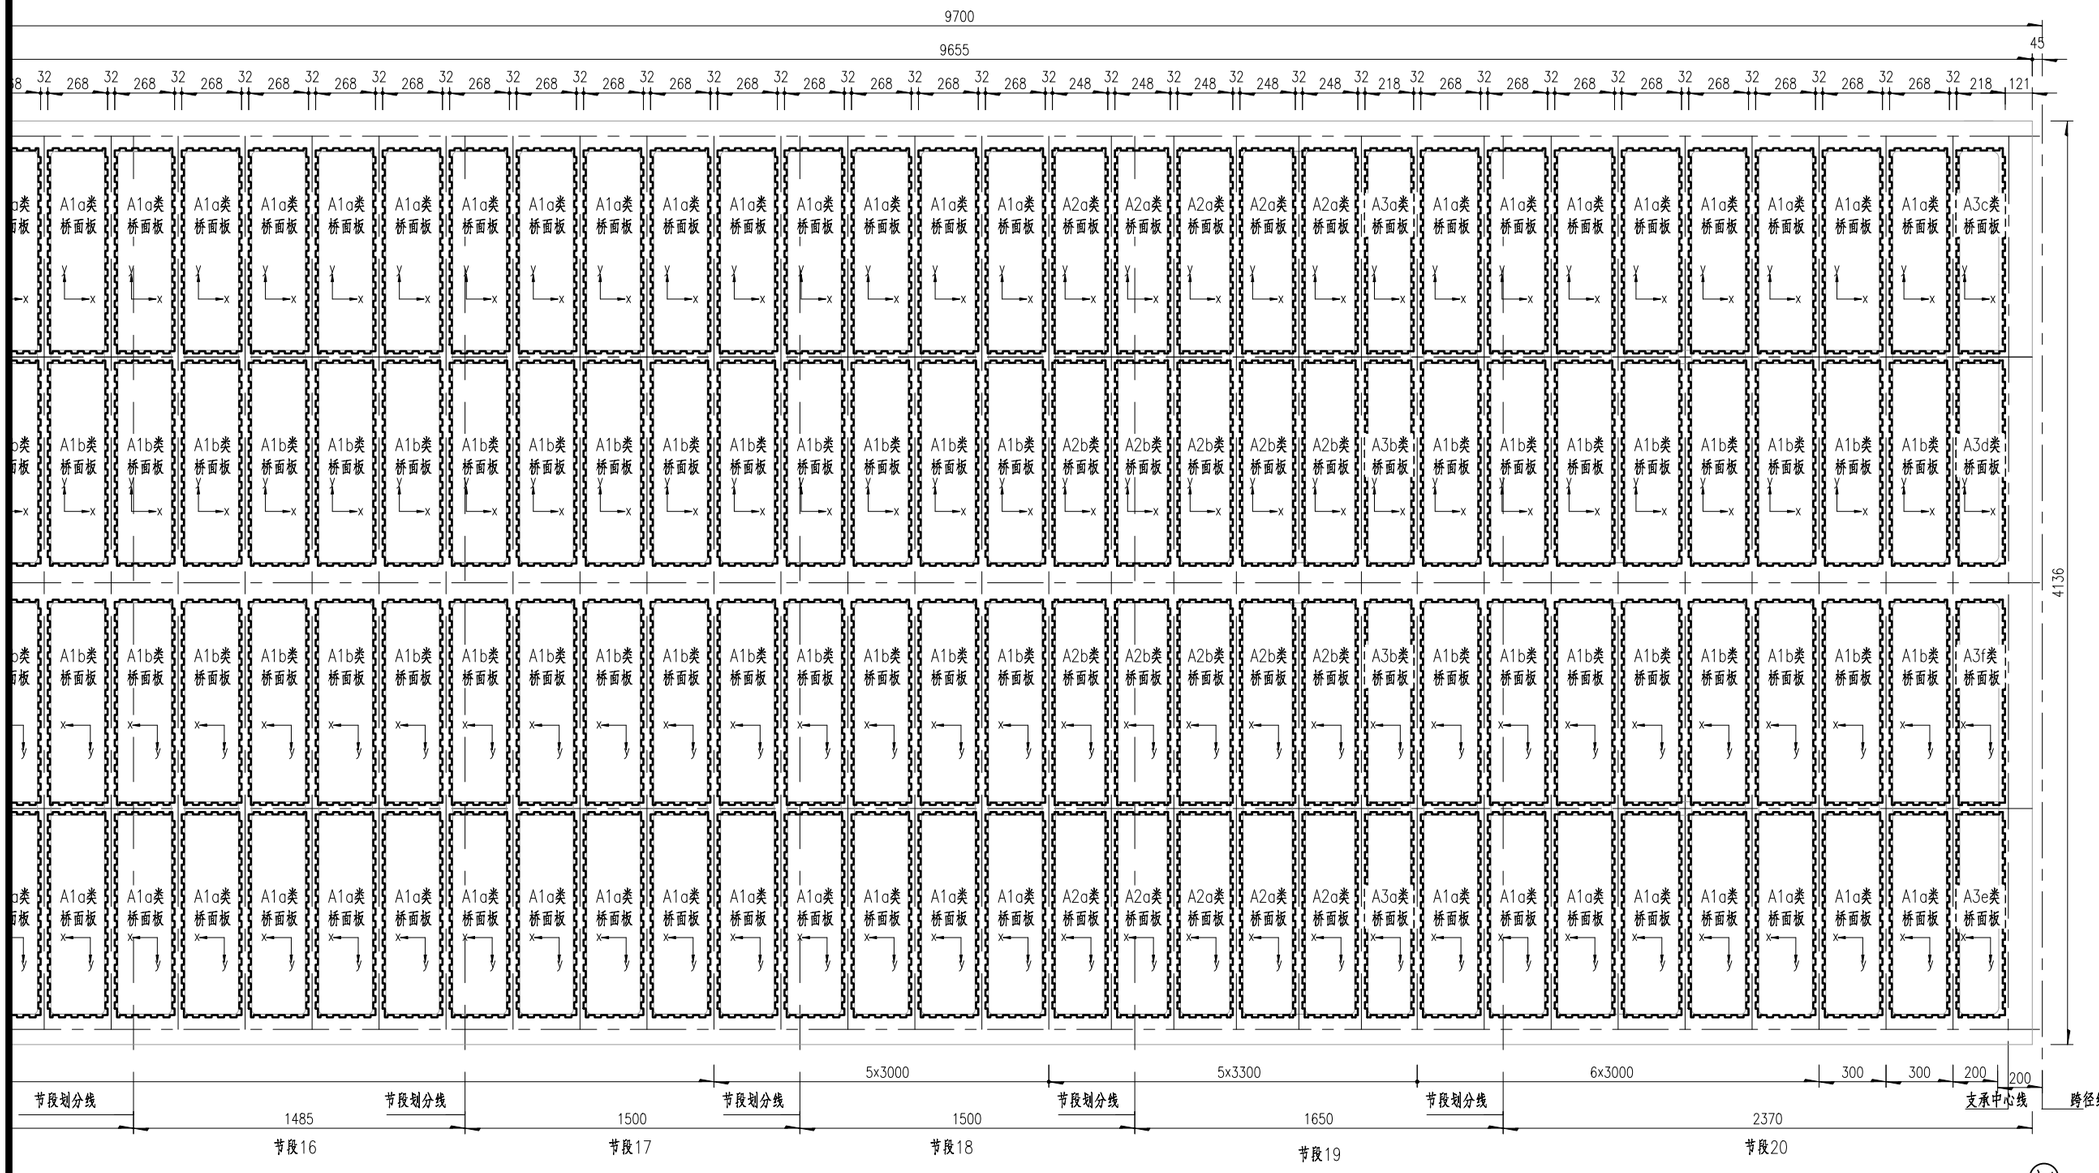

上层桥面预制板规格表

类型	规格（m）	个数	单块方量	总方量
A1类桥面板	9.19x2.68x0.18	404	4.22	1704.88
A2类桥面板	9.19x2.48x0.18	40	3.90	156.0
A3类桥面板	9.19x2.18x0.18	16	3.40	54.4
UHPC合计(m³)				1915.3

注：

1. 本图适用于上层组合梁桥面布置，图中尺寸单位均以厘米计。

中交第二公路勘察设计研究院有限公司	狮子洋通道工程勘察设计 施 工 图 设 计	K6+418.3 新沙高架桥 上层桥面系总体布置图	设计	余汪千	复核	袁勤	一审	沈华	二审	李忠	图号	SZYS/04/02/02/01/ 55

Ⅱ－Ⅱ

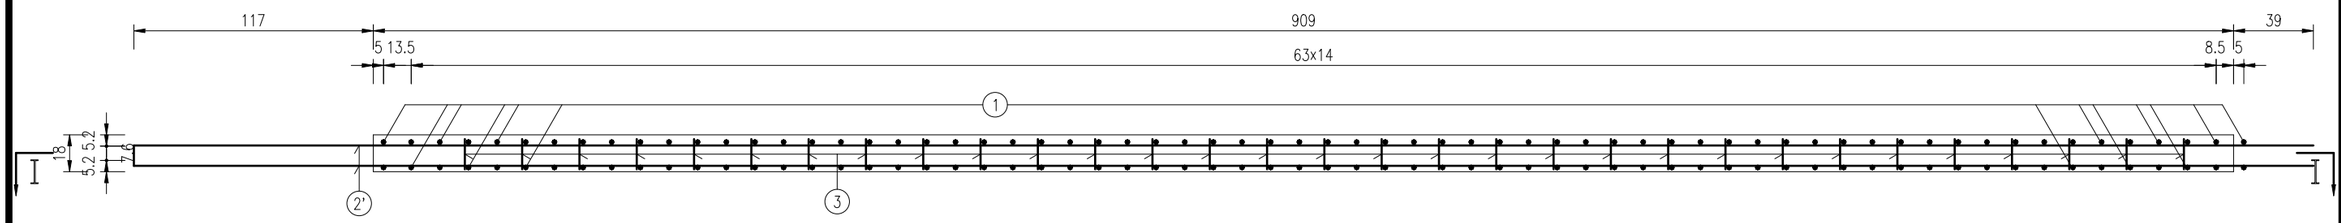

Ⅳ－Ⅳ

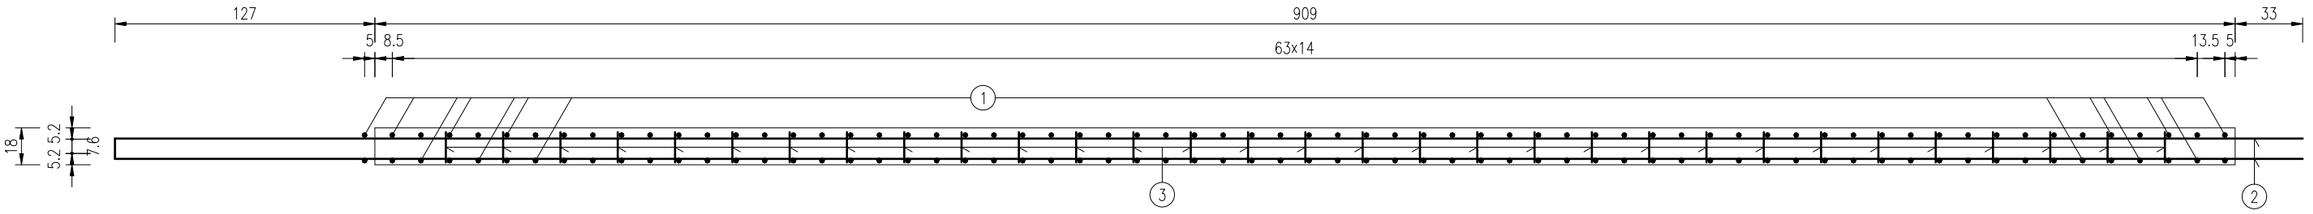

Ⅲ－Ⅲ

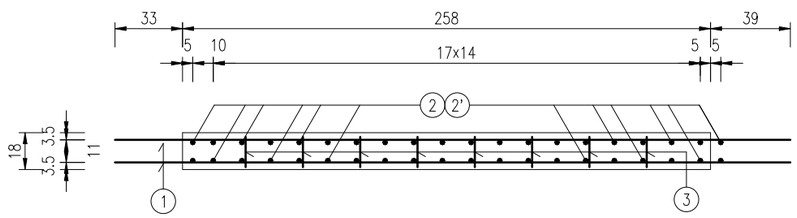

Ⅴ－Ⅴ

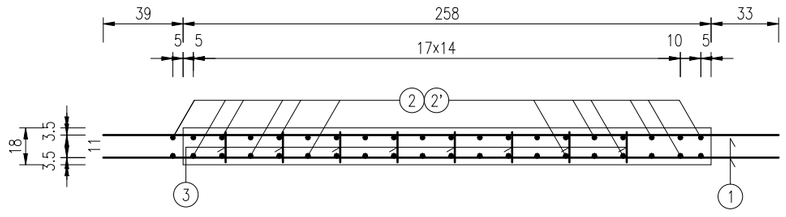

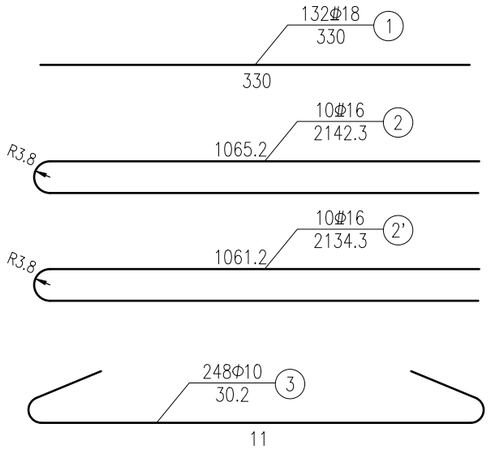

纵、横向钢筋及拉筋绑扎示意图

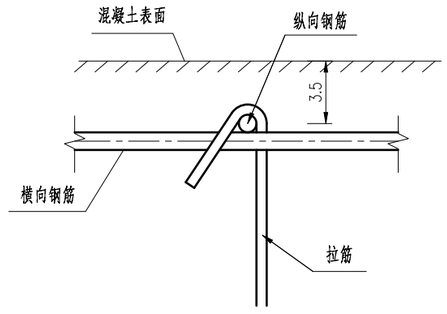

A1a桥面板钢筋数量表

编号	规格	单根长 (cm)	根数	总长 (m)	单位重 (kg/m)	总重 (kg)	单块板 合计(kg)	全桥202块 合计(kg)
1	Φ18	330.0	132	435.60	2.000	871.2	871.2	175982.4
2	Φ16	2142.3	10	214.23	1.580	338.5	675.7	136491.4
2'	Φ16	2134.3	10	213.43	1.580	337.2		
3	Φ10	30.2	248	74.90	0.617	46.2	46.2	9332.4

注：

1、本图尺寸除注明者外，其余均以厘米计。

2、图中钢筋间距尺寸标注为预制板中心处，为使纵桥向和横桥向相邻的预制板的钢筋不互相干扰，钢筋绑扎需倾斜一定角度。

3、本图适用于A1a类桥面板，钢筋保护层厚度最小不低于15mm。

中交第二公路勘察设计研究院有限公司	狮子洋通道工程勘察设计 施 工 图 设 计	K6+418.3 新沙高架桥 上层桥面预制行车道板钢筋布置图	设计		复核		一审		二审		图号	SZYS/04/02/02/01/ 58

4250104195902290

Ⅱ－Ⅱ

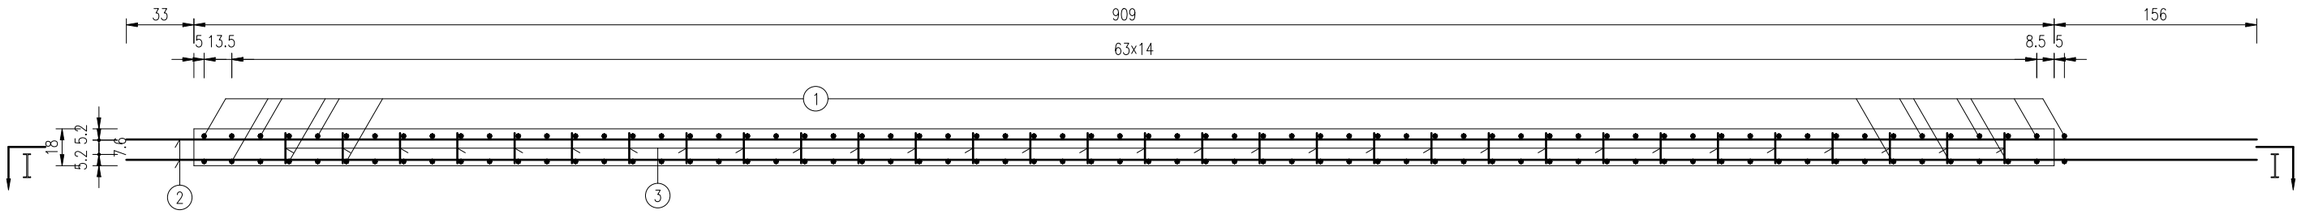

Ⅳ－Ⅳ

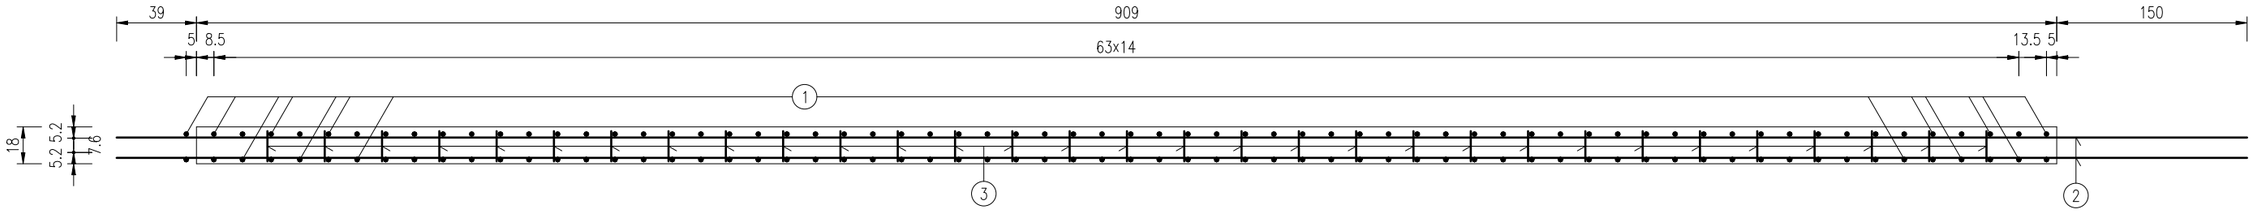

Ⅲ－Ⅲ

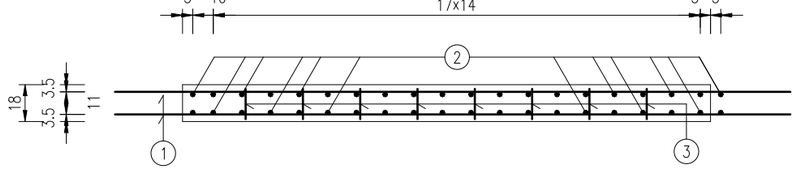

Ⅴ－Ⅴ

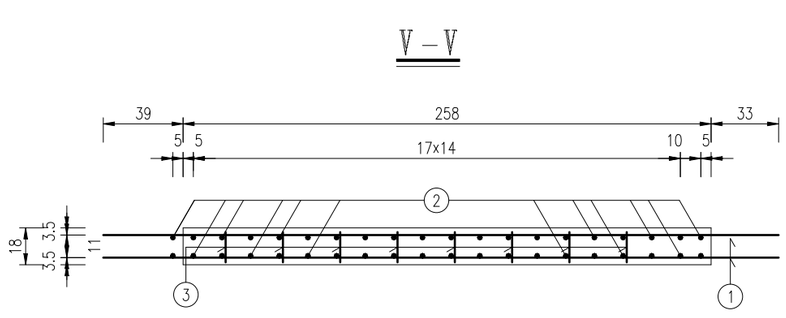

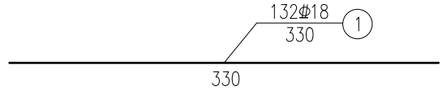

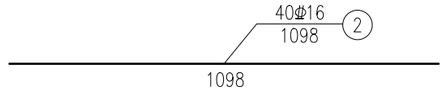

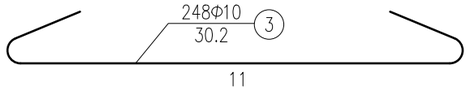

纵、横向钢筋及拉筋绑扎示意图

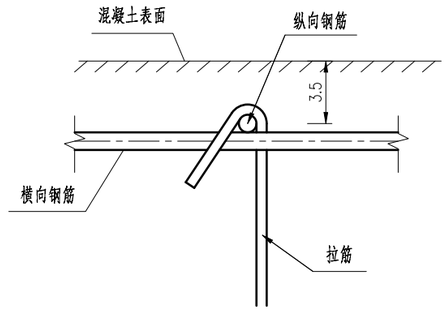

A1b桥面板钢筋数量表

编号	规格	单根长 (cm)	根数	总长 (m)	单位重 (kg/m)	总重 (kg)	单块板 合计(kg)	全桥202块 合计(kg)
1	Φ18	330.0	132	435.60	2.000	871.2	871.2	175982.4
2	Φ16	1098.0	40	439.20	1.580	693.9	693.9	140175.1
3	Φ10	30.2	248	74.90	0.617	46.2	46.2	9332.4

注：

1、本图尺寸除注明者外，其余均以厘米计。

2、图中钢筋间距尺寸标注为预制板中心处，为使纵桥向和横桥向相邻的预制板的钢筋不互相干扰，钢筋绑扎需倾斜一定角度。

3、本图适用于A1b类桥面板，钢筋保护层厚度最小不低于15mm。

中交第二公路勘察设计研究院有限公司	狮子洋通道工程勘察设计 施 工 图 设 计	K6+418.3 新沙高架桥 上层桥面预制行车道板钢筋布置图	设计		复核		一审		二审		图号	SZYS/04/02/02/01/ 58

Ⅱ－Ⅱ

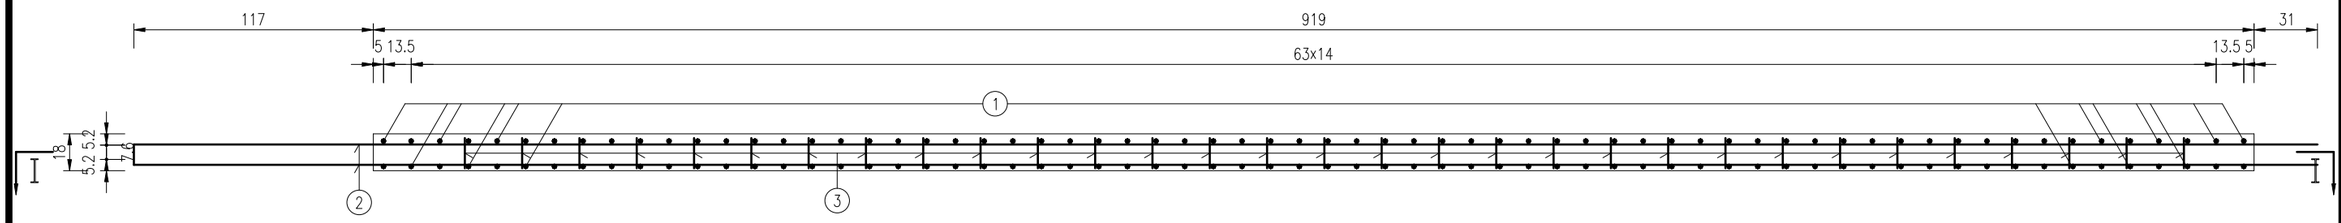

Ⅳ－Ⅳ

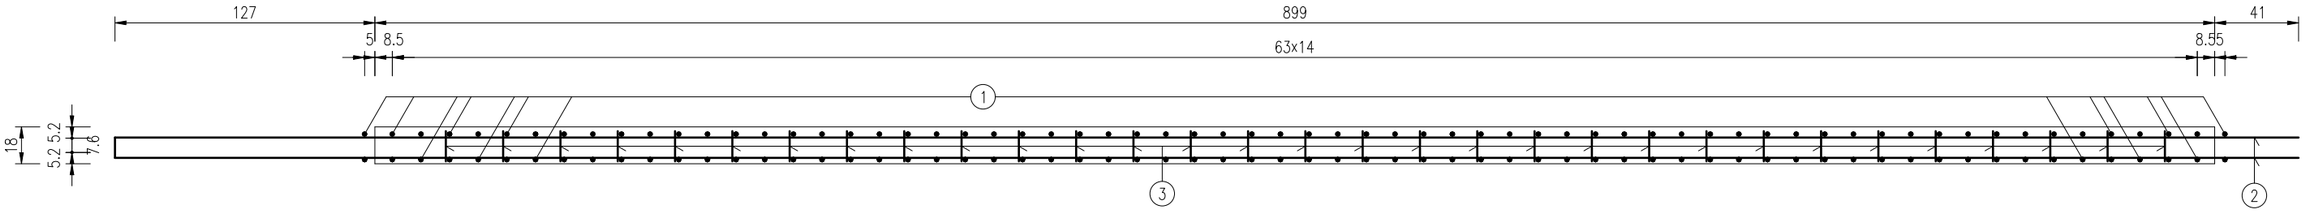

Ⅲ－Ⅲ

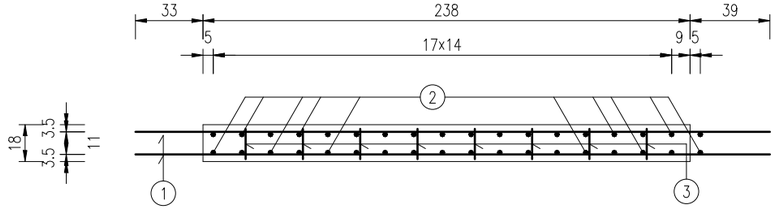

Ⅴ－Ⅴ

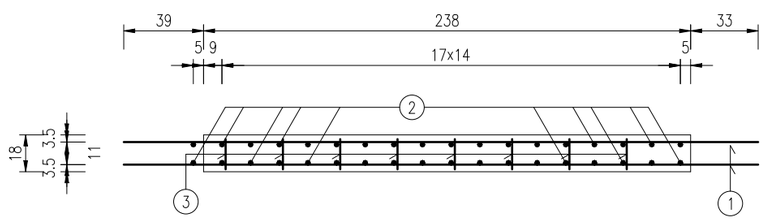

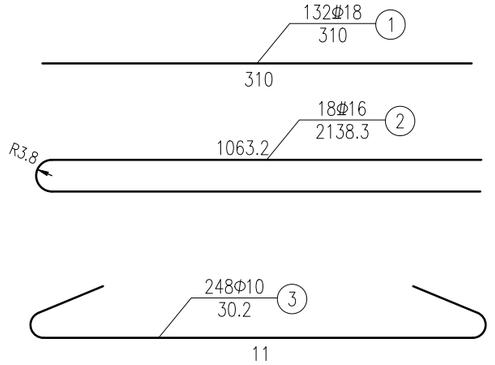

纵、横向钢筋及拉筋绑扎示意图

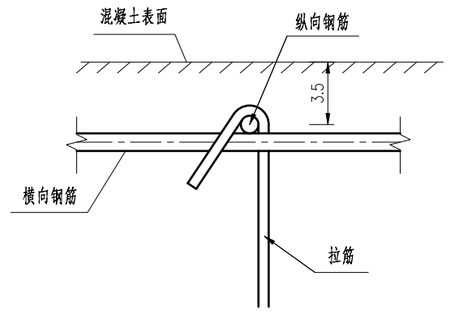

A2a桥面板钢筋数量表

编号	规格	单根长 (cm)	根数	总长 (m)	单位重 (kg/m)	总重 (kg)	单块板 合计(kg)	全桥20块 合计(kg)
1	Φ18	310.0	132	409.20	2.000	818.4	818.4	16368.0
2	Φ16	2138.3	18	384.90	1.580	608.1	608.1	12162.9
3	Φ10	30.2	248	74.90	0.617	46.2	46.2	924.0

注：

1、本图尺寸除注明者外，其余均以厘米计。

2、图中钢筋间距尺寸标注为预制板中心处，为使纵桥向和横桥向相邻的预制板的钢筋不互相干扰，钢筋绑扎需倾斜一定角度。

3、本图适用于A2a类桥面板，钢筋保护层厚度最小不低于15mm。

中交第二公路勘察设计研究院有限公司	狮子洋通道工程勘察设计 施 工 图 设 计	K6+418.3 新沙高架桥 上层桥面预制行车道板钢筋布置图	设计		复核		一审		二审		图号	SZYS/04/02/02/01/ 58

Ⅱ－Ⅱ

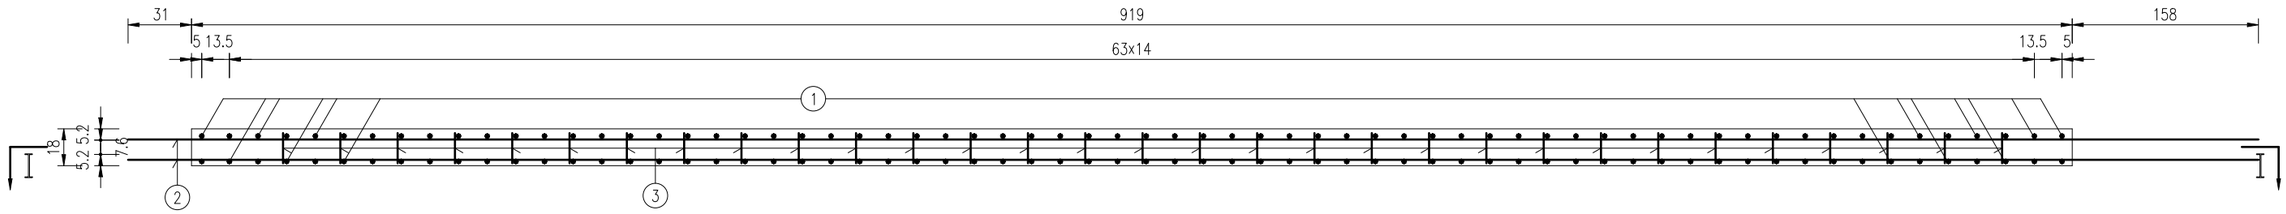

Ⅳ－Ⅳ

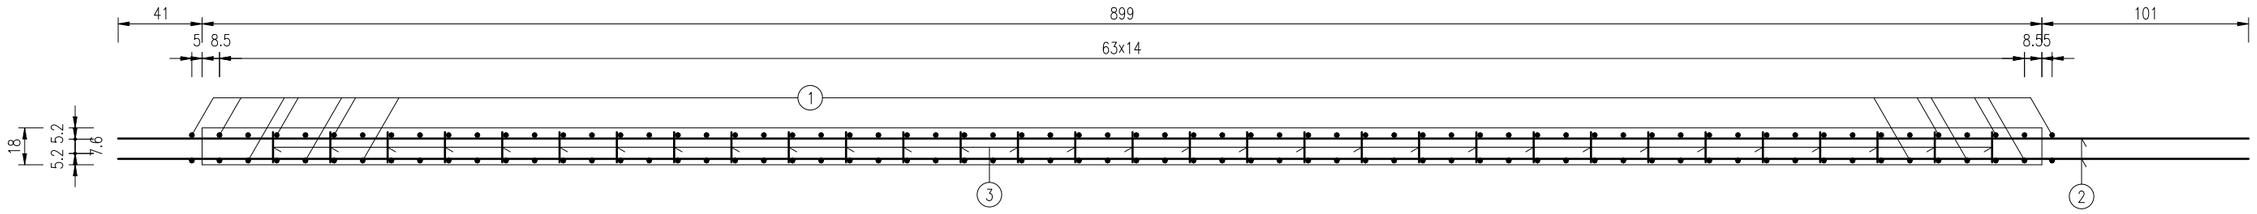

Ⅲ－Ⅲ

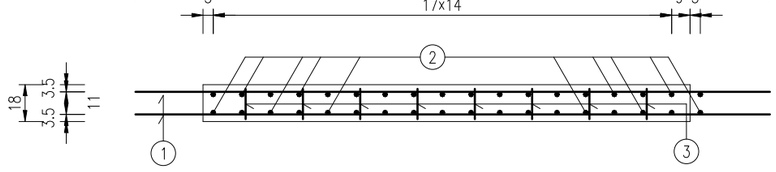

Ⅴ－Ⅴ

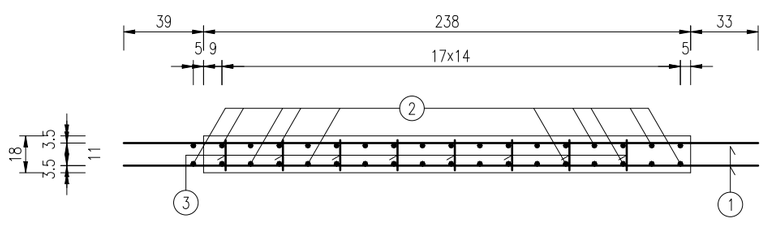

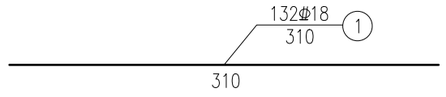

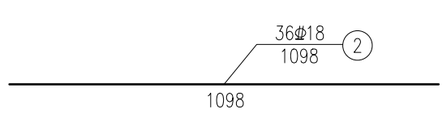

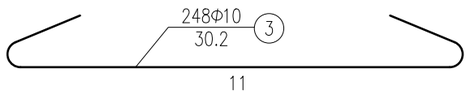

纵、横向钢筋及拉筋绑扎示意图

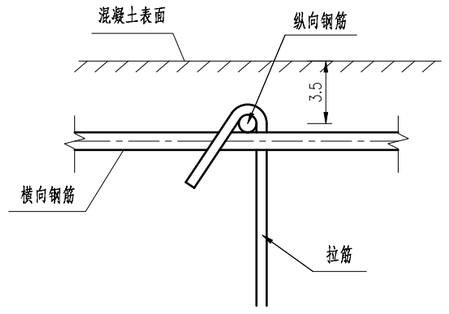

A2b桥面板钢筋数量表

编号	规格	单根长 (cm)	根数	总长 (m)	单位重 (kg/m)	总重 (kg)	单块板 合计(kg)	全桥20块 合计(kg)
1	Φ18	310.0	132	409.20	2.000	818.4	818.4	16368.0
2	Φ16	1098.0	36	395.28	1.580	624.5	624.5	12490.8
3	Φ10	30.2	248	74.90	0.617	46.2	46.2	924.0

注：

1、本图尺寸除注明者外，其余均以厘米计。

2、图中钢筋间距尺寸标注为预制板中心处，为使纵桥向和横桥向相邻的预制板的钢筋不互相干扰，钢筋绑扎需倾斜一定角度。

3、本图适用于A2b类桥面板，钢筋保护层厚度最小不低于15mm。

中交第二公路勘察设计研究院有限公司	狮子洋通道工程勘察设计 施 工 图 设 计	K6+418.3 新沙高架桥 上层桥面预制行车道板钢筋布置图	设计		复核		一审		二审		图号	SZYS/04/02/02/01/ 58

Ⅱ－Ⅱ

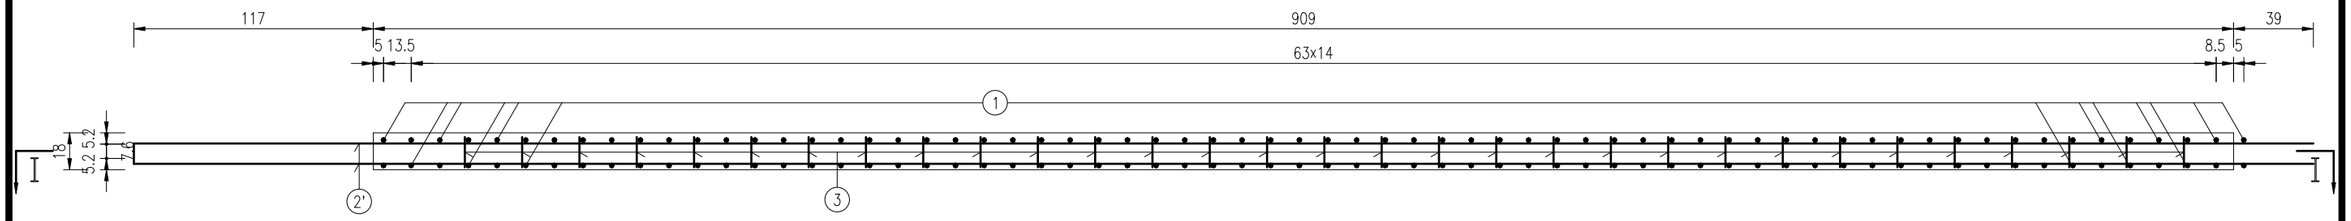

Ⅳ－Ⅳ

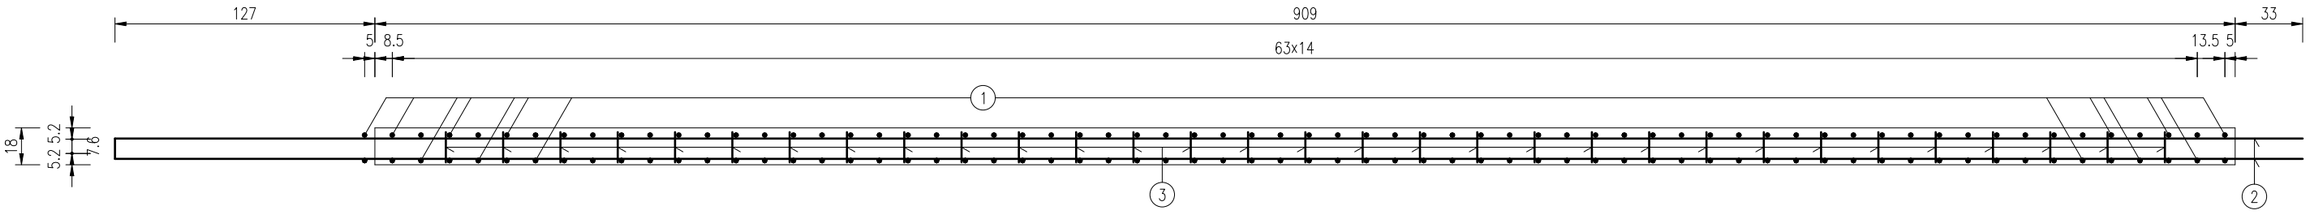

Ⅲ－Ⅲ

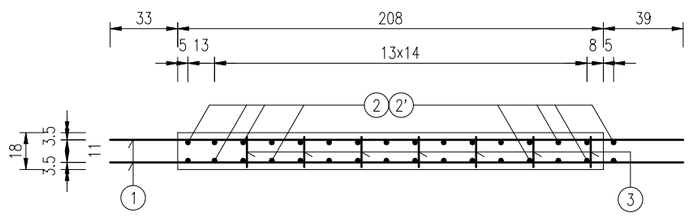

Ⅴ－Ⅴ

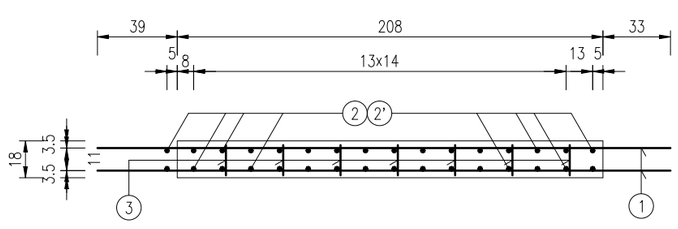

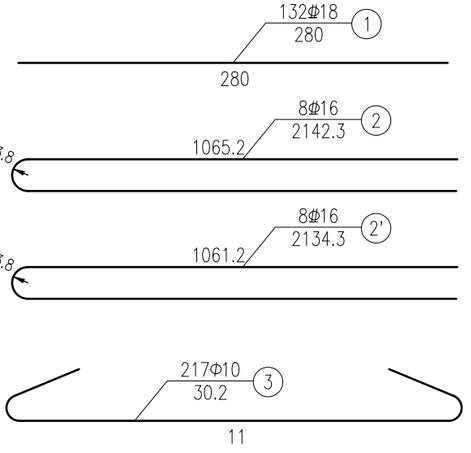

纵、横向钢筋及拉筋绑扎示意图

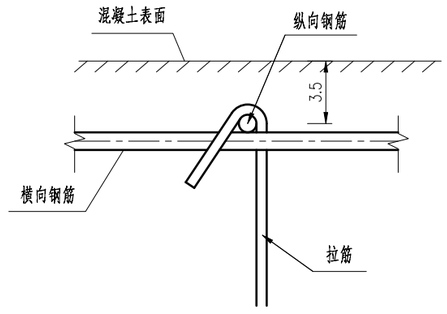

A3a桥面板钢筋数量表

编号	规格	单根长 (cm)	根数	总长 (m)	单位重 (kg/m)	总重 (kg)	单块板 合计(kg)	全桥4块 合计(kg)
1	Φ18	280.0	132	369.60	2.000	739.2	739.2	2956.8
2	Φ16	2142.3	8	171.38	1.580	270.8	540.6	2162.3
2'	Φ16	2134.3	8	170.74	1.580	269.8		
3	Φ10	30.2	217	65.53	0.617	40.4	40.4	161.7

注：

1、本图尺寸除注明者外，其余均以厘米计。

2、图中钢筋间距尺寸标注为预制板中心处，为使纵桥向和横桥向相邻的预制板的钢筋不互相干扰，钢筋绑扎需倾斜一定角度。

3、本图适用于A3a类桥面板，钢筋保护层厚度最小不低于15mm。

中交第二公路勘察设计研究院有限公司	狮子洋通道工程勘察设计 施 工 图 设 计	K6+418.3 新沙高架桥 上层桥面预制行车道板钢筋布置图	设计		复核		一审		二审		图号	SZYS/04/02/02/01/ 58

Ⅱ－Ⅱ

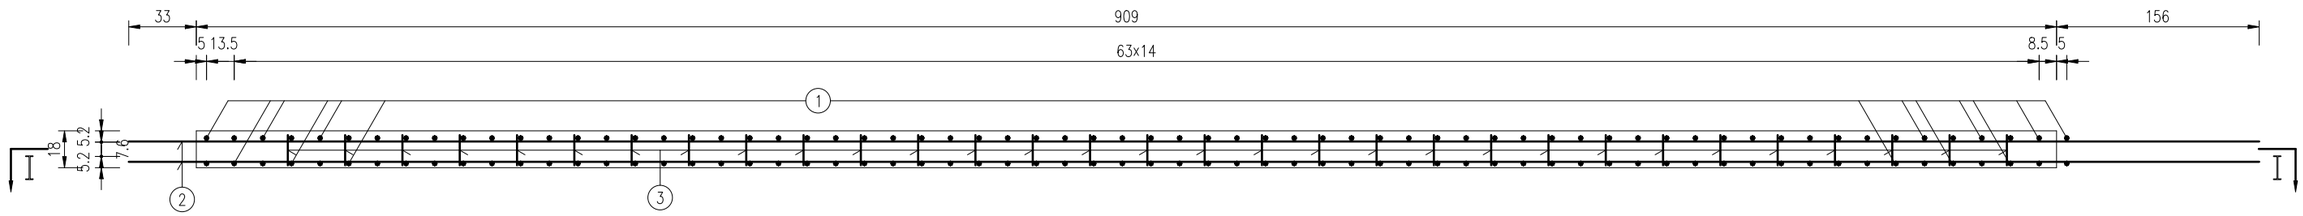

Ⅳ－Ⅳ

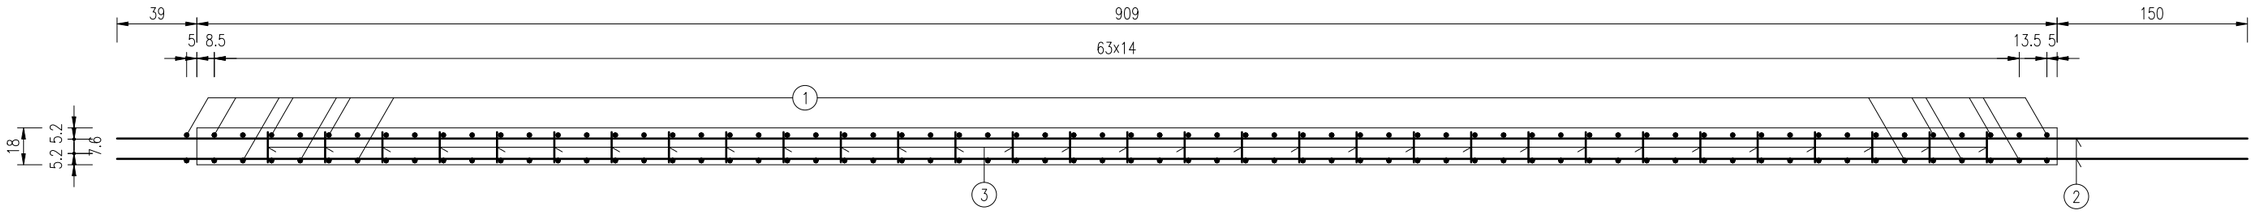

Ⅲ－Ⅲ

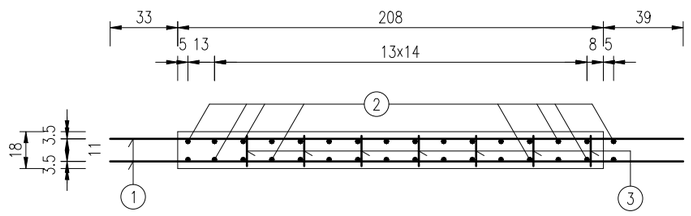

Ⅴ－Ⅴ

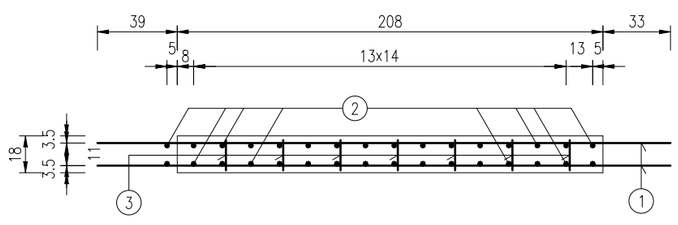

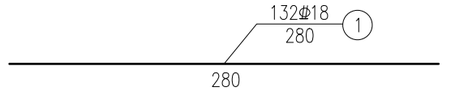

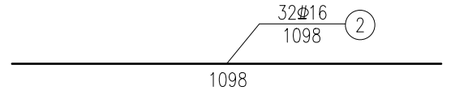

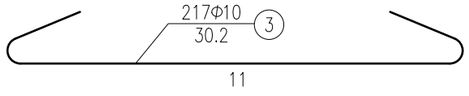

纵、横向钢筋及拉筋绑扎示意图

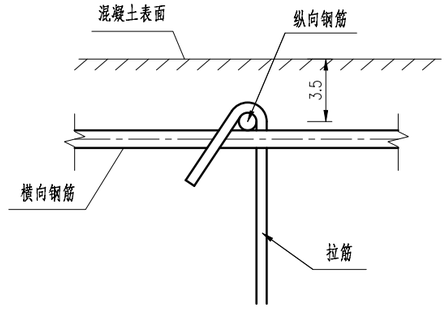

A3b桥面板钢筋数量表

编号	规格	单根长 (cm)	根数	总长 (m)	单位重 (kg/m)	总重 (kg)	单块板 合计(kg)	全桥4块 合计(kg)
1	Φ18	280.0	132	369.60	2.000	739.2	739.2	2956.8
2	Φ16	1098.0	32	351.36	1.580	555.1	555.1	2220.6
3	Φ10	30.2	217	65.53	0.617	40.4	40.4	161.7

注：

1、本图尺寸除注明者外，其余均以厘米计。

2、图中钢筋间距尺寸标注为预制板中心处，为使纵桥向和横桥向相邻的预制板的钢筋不互相干扰，钢筋绑扎需倾斜一定角度。

3、本图适用于A3b类桥面板，钢筋保护层厚度最小不低于15mm。

中交第二公路勘察设计研究院有限公司	狮子洋通道工程勘察设计 施 工 图 设 计	K6+418.3 新沙高架桥 上层桥面预制行车道板钢筋布置图	设计	彦昊	复核	袁勤	一审	沈维	二审	图号	SZYS/04/02/02/01/ 58

Ⅱ－Ⅱ

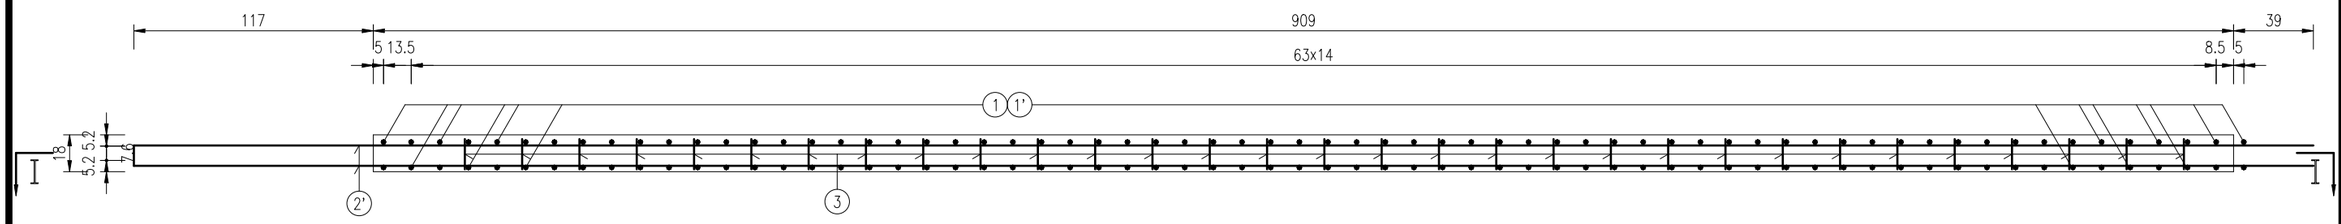

Ⅳ－Ⅳ

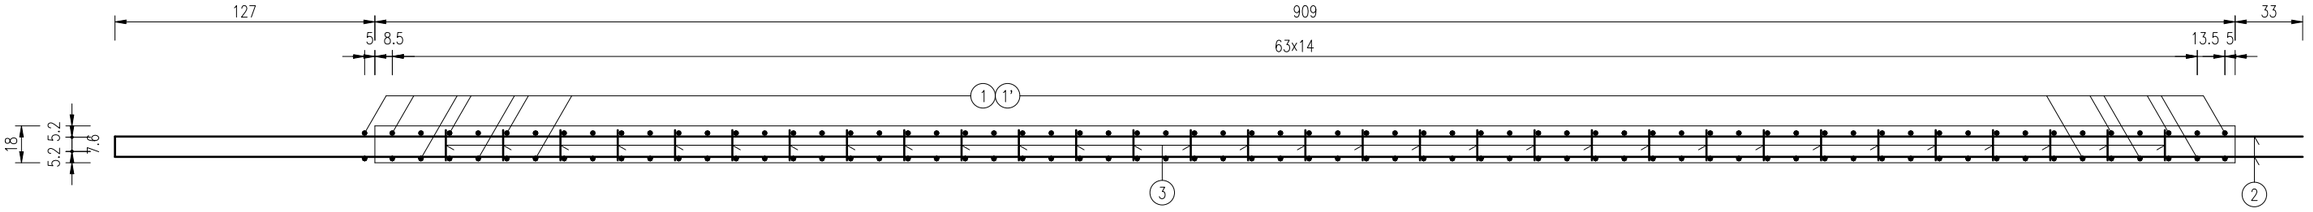

Ⅲ－Ⅲ

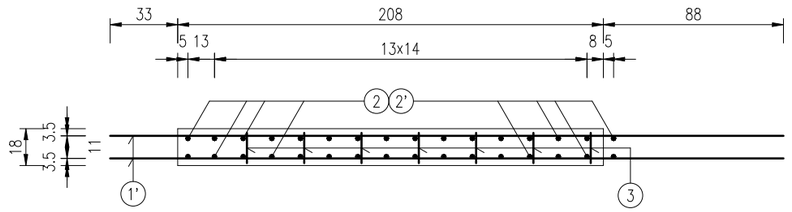

Ⅴ－Ⅴ

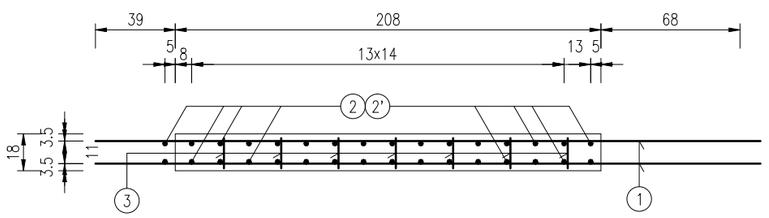

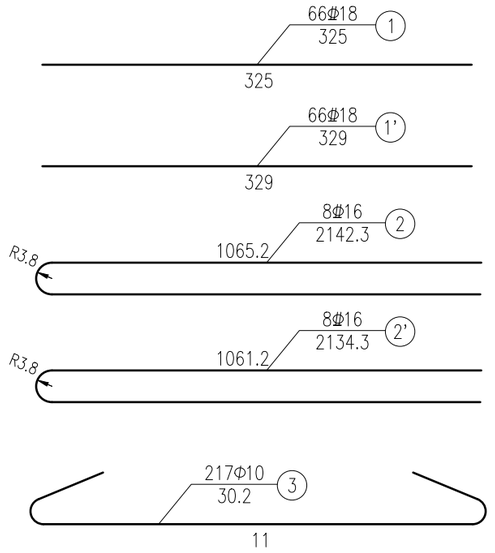

A3c桥面板钢筋数量表

编号	规格	单根长 (cm)	根数	总长 (m)	单位重 (kg/m)	总重 (kg)	单块板 合计(kg)	全桥2块 合计(kg)
1	Φ18	325.0	66	214.50	2.000	429.0	863.3	1726.6
1'	Φ18	329.0	66	217.14	2.000	434.3		
2	Φ16	2142.3	8	171.38	1.580	270.8	540.6	1081.2
2'	Φ16	2134.3	8	170.74	1.580	269.8		
3	Φ10	30.2	217	65.53	0.617	40.4	40.4	80.8

纵、横向钢筋及拉筋绑扎示意图

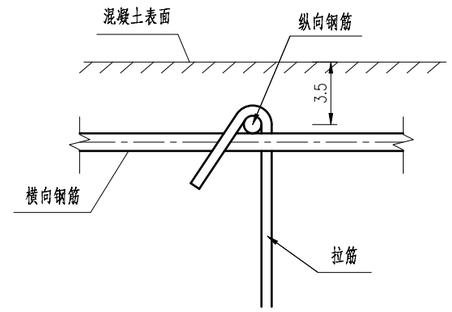

注：

1、本图尺寸除注明者外，其余均以厘米计。

2、图中钢筋间距尺寸标注为预制板中心处，为使纵桥向和横桥向相邻的预制板的钢筋不互相干扰，钢筋绑扎需倾斜一定角度。

3、本图适用于A3c类桥面板，钢筋保护层厚度最小不低于15mm。

中交第二公路勘察设计研究院有限公司	狮子洋通道工程勘察设计 施 工 图 设 计	K6+418.3 新沙高架桥 上层桥面预制行车道板钢筋布置图	设计		复核		一审		二审		图号	SZYS/04/02/02/01/ 58

Ⅱ－Ⅱ

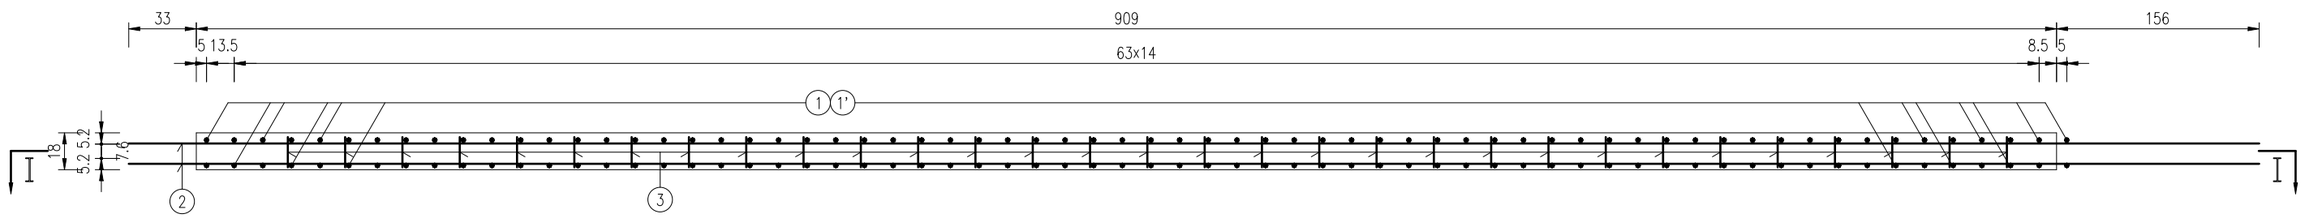

Ⅳ－Ⅳ

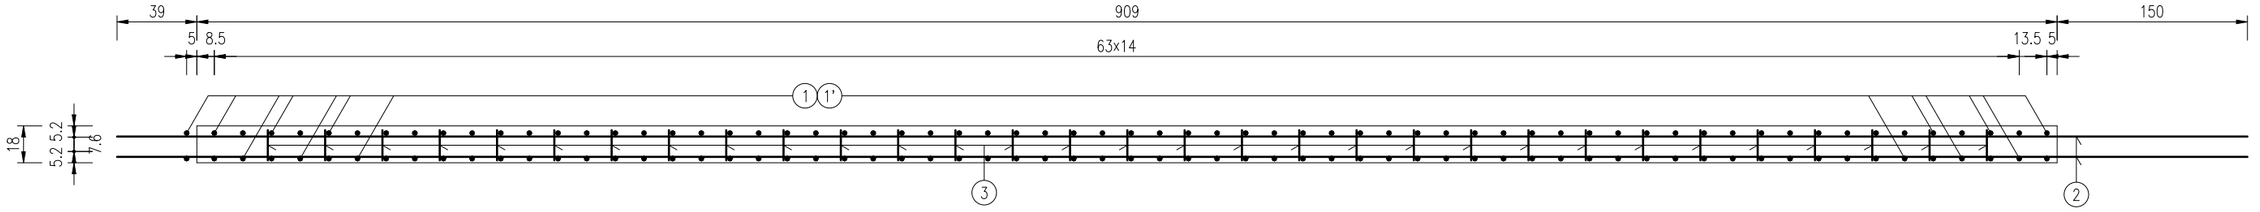

Ⅲ－Ⅲ

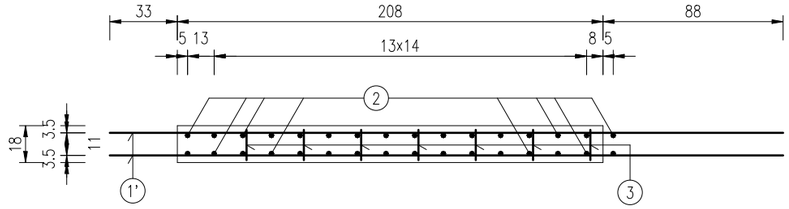

Ⅴ－Ⅴ

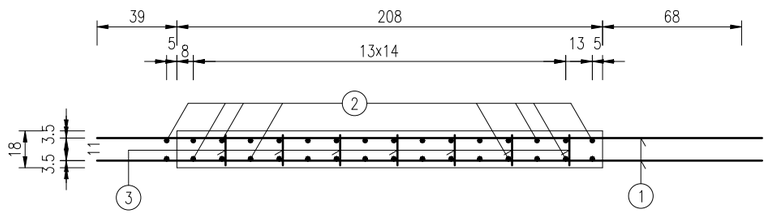

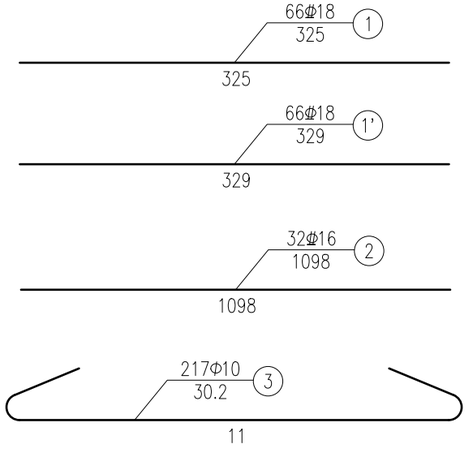

纵、横向钢筋及拉筋绑扎示意图

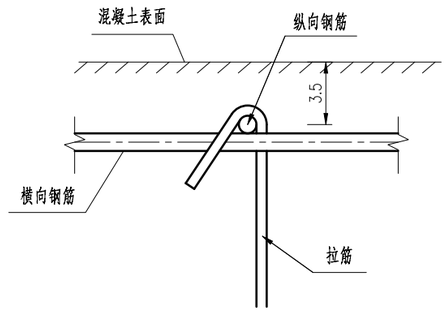

A3d桥面板钢筋数量表

编号	规格	单根长 (cm)	根数	总长 (m)	单位重 (kg/m)	总重 (kg)	单块板 合计(kg)	全桥2块 合计(kg)
1	Φ18	325.0	66	214.50	2.000	429.0	863.3	1726.6
1’	Φ18	329.0	66	217.14	2.000	434.3		
2	Φ16	1098.0	32	351.36	1.580	555.1	555.1	1110.3
3	Φ10	30.2	217	65.53	0.617	40.4	40.4	161.7

注：

1、本图尺寸除注明者外，其余均以厘米计。

2、图中钢筋间距尺寸标注为预制板中心处，为使纵桥向和横桥向相邻的预制板的钢筋不互相干扰，钢筋绑扎需倾斜一定角度。

3、本图适用于A3d类桥面板，钢筋保护层厚度最小不低于15mm。

中交第二公路勘察设计研究院有限公司	狮子洋通道工程勘察设计 施 工 图 设 计	K6+418.3 新沙高架桥 上层桥面预制行车道板钢筋布置图	设计		复核		一审		二审		图号	SZYS/04/02/02/01/ 58

Ⅱ－Ⅱ

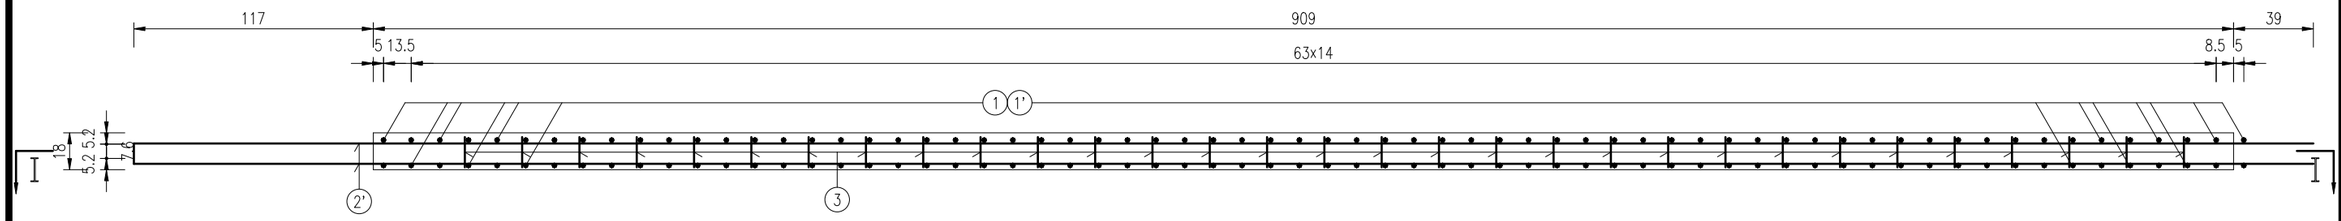

Ⅳ－Ⅳ

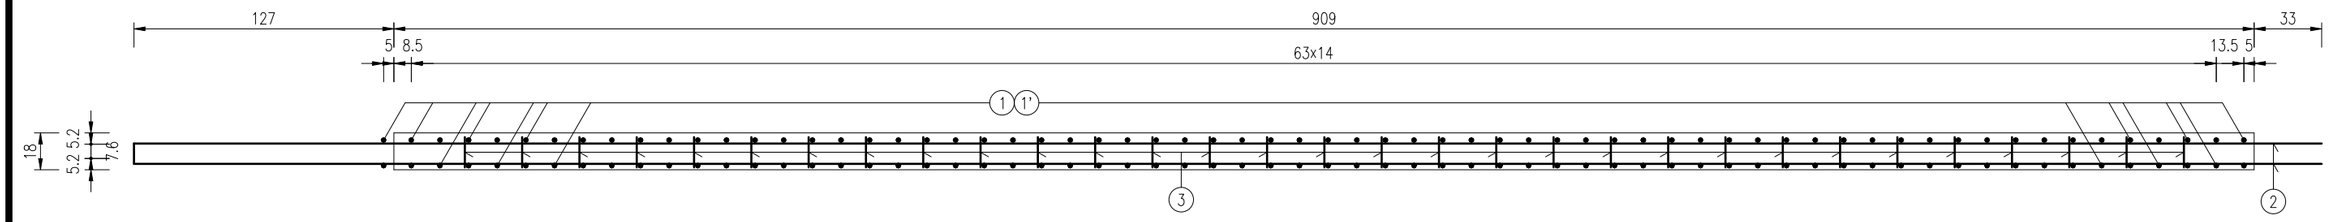

Ⅲ－Ⅲ

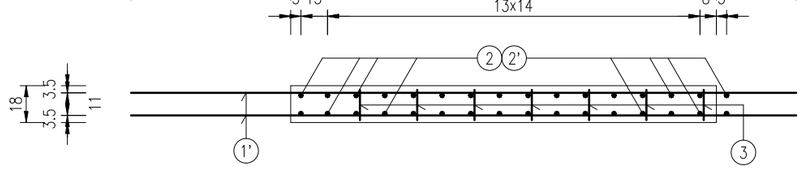

Ⅴ－Ⅴ

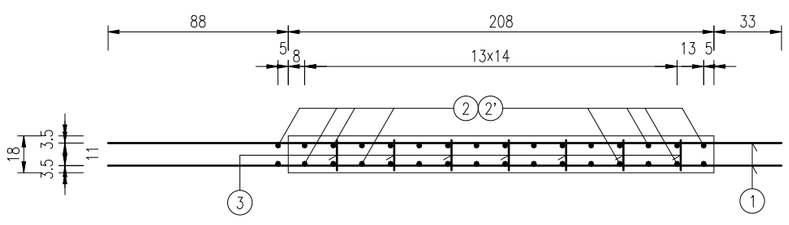

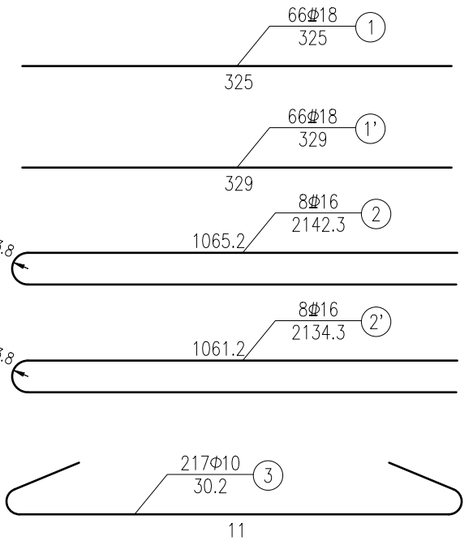

纵、横向钢筋及拉筋绑扎示意图

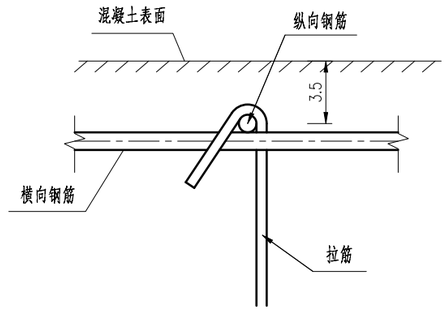

A3e桥面板钢筋数量表

编号	规格	单根长 (cm)	根数	总长 (m)	单位重 (kg/m)	总重 (kg)	单块板 合计(kg)	全桥2块 合计(kg)
1	Φ18	325.0	66	214.50	2.000	429.0	863.3	1726.6
1'	Φ18	329.0	66	217.14	2.000	434.3		
2	Φ16	2142.3	8	171.38	1.580	270.8	540.6	1081.2
2'	Φ16	2134.3	8	170.74	1.580	269.8		
3	Φ10	30.2	217	65.53	0.617	40.4	40.4	80.8

注：

1、本图尺寸除注明者外，其余均以厘米计。

2、图中钢筋间距尺寸标注为预制板中心处，为使纵桥向和横桥向相邻的预制板的钢筋不互相干扰，钢筋绑扎需倾斜一定角度。

3、本图适用于A3e类桥面板，钢筋保护层厚度最小不低于15mm。

中交第二公路勘察设计研究院有限公司	狮子洋通道工程勘察设计 施 工 图 设 计	K6+418.3 新沙高架桥 上层桥面预制行车道板钢筋布置图	设计		复核		一审		二审		图号	SZYS/04/02/02/01/ 58

Ⅱ－Ⅱ

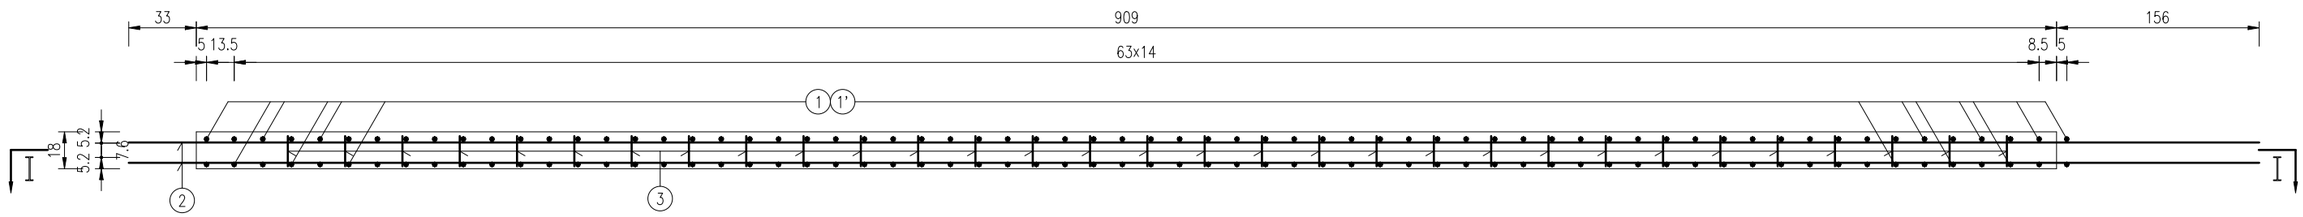

Ⅳ－Ⅳ

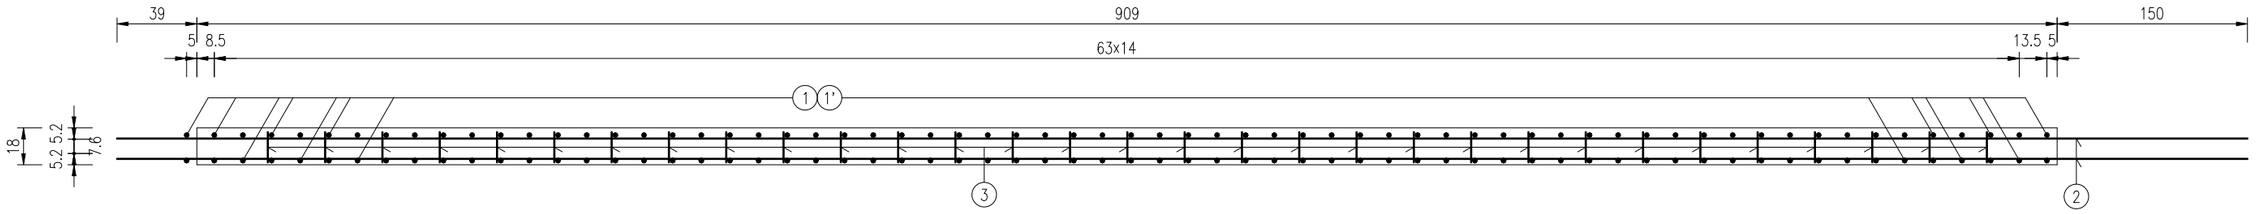

Ⅲ－Ⅲ

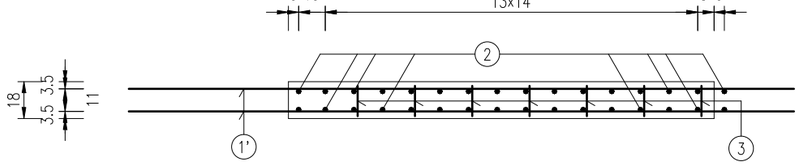

Ⅴ－Ⅴ

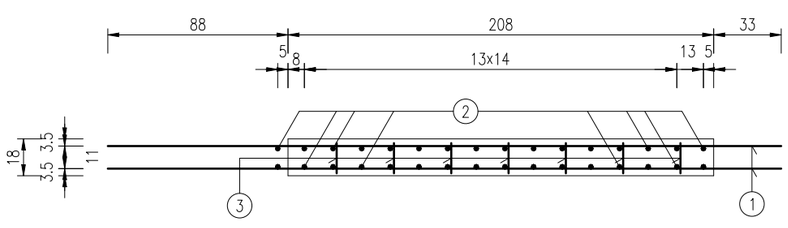

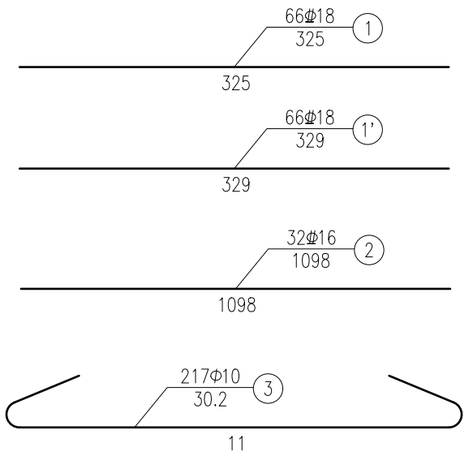

纵、横向钢筋及拉筋绑扎示意图

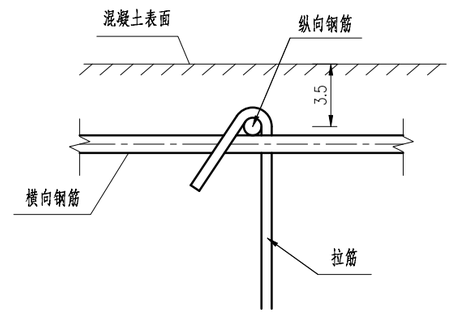

A3f桥面板钢筋数量表

编号	规格	单根长 (cm)	根数	总长 (m)	单位重 (kg/m)	总重 (kg)	单块板 合计(kg)	全桥2块 合计(kg)
1	Φ18	325.0	66	214.50	2.000	429.0	863.3	1726.6
1'	Φ18	329.0	66	217.14	2.000	434.3		
2	Φ16	1098.0	32	351.36	1.580	555.1	555.1	1110.3
3	Φ10	30.2	217	65.53	0.617	40.4	40.4	161.7

注：

1、本图尺寸除注明者外，其余均以厘米计。

2、图中钢筋间距尺寸标注为预制板中心处，为使纵桥向和横桥向相邻的预制板的钢筋不互相干扰，钢筋绑扎需倾斜一定角度。

3、本图适用于A3f类桥面板，钢筋保护层厚度最小不低于15mm。

中交第二公路勘察设计研究院有限公司	狮子洋通道工程勘察设计 施 工 图 设 计	K6+418.3 新沙高架桥 上层桥面预制行车道板钢筋布置图	设计		复核		一审		二审		图号	SZYS/04/02/02/01/ 58

上层纵向湿接缝平面图

纵向湿接缝为齿状，按直线示意

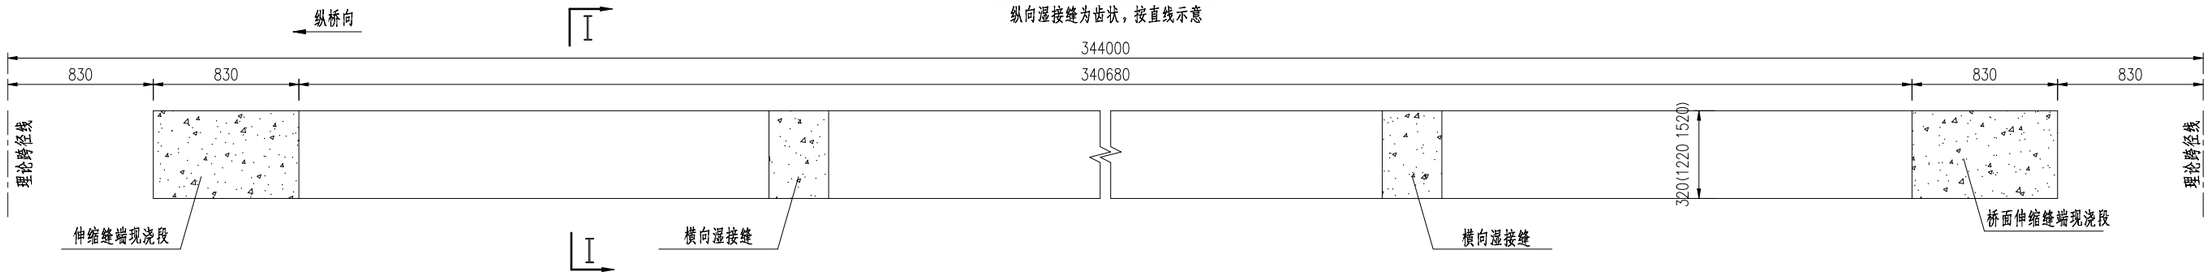

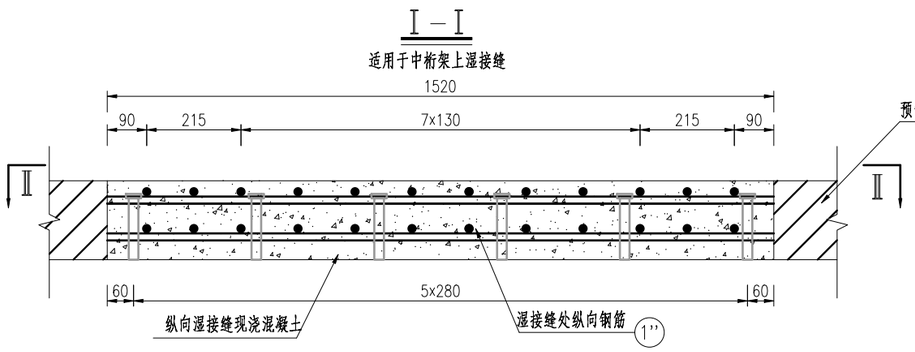

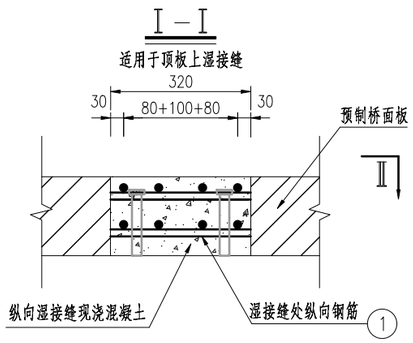

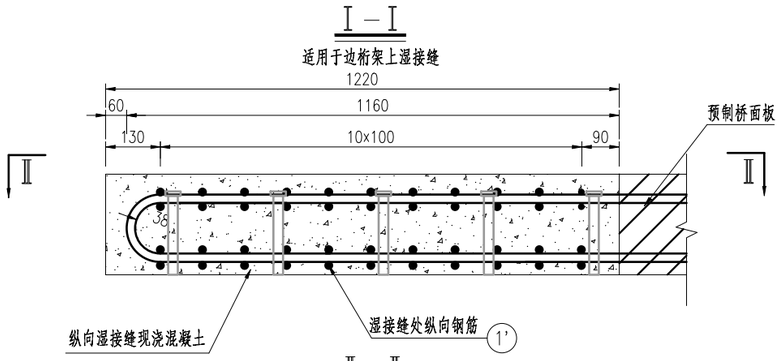

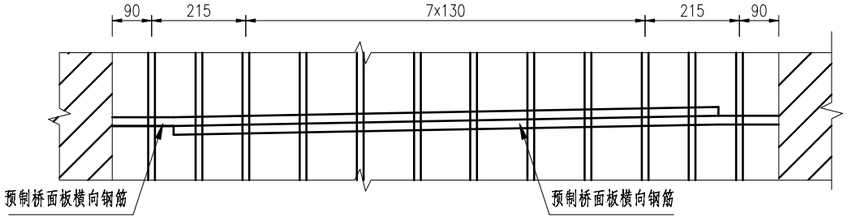

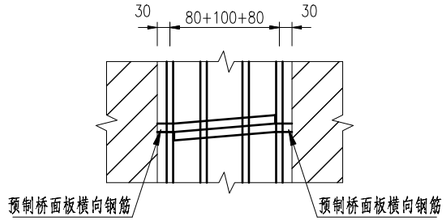

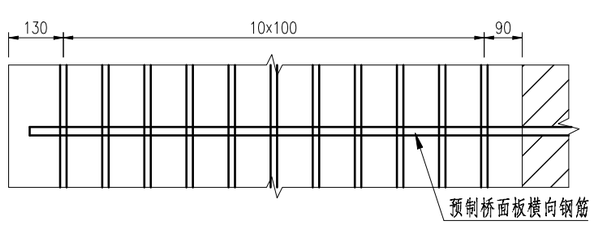

纵向湿接缝钢筋数量表

缝宽（cm）	编号	规格	单根长 (mm)	根数	总长 (m)	单位重 (kg/m)	总重 (kg)	一道缝 合计(kg)	全桥道数	全桥 合计(kg)
32	1	φ18	342340	8	2738.72	2.000	5477.4	5477.4	2	10954.9
	UHPC现浇混凝土（m³）							25.88		51.8
122	1'	φ18	342340	44	15062.96	2.000	30125.9	30125.9	2	60251.8
	UHPC现浇混凝土（m³）							78.26		156.5
152	1''	φ18	342340	24	8216.16	2.000	16432.3	16432.3	1	16432.3
	UHPC现浇混凝土（m³）							99.83		99.8

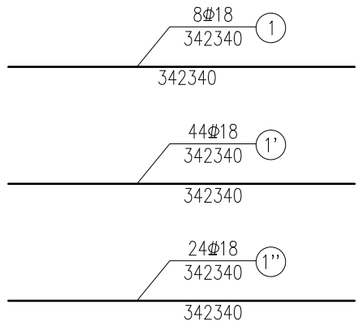

注：

1、本图适用于上层桥面纵向湿接缝，图中尺寸除注明者外，其余均以毫米计。

2、现浇缝处相邻两预制板采用扣环连接和套环焊接，并设置插筋，插筋位置和数量见图示，其搭接和焊接长度应满足规范要求。

3、环形钢筋伸长预制板部分按逆时针方向预弯一个钢筋直径，预弯具体尺寸如图所示，以便预制板之间扣环搭接，使钢筋轴线对其。

4、横向环形搭接钢筋的成型采用闪光对焊，焊接接头错开布置，在同一断面不得超过50%。

5、当现浇缝钢筋与剪力钉相碰时，可适当挪动其位置，但不得任意切断或取消。

6、本图未示出护栏、灯柱等预埋件，另见详图。

中交第二公路勘察设计研究院有限公司	狮子洋通道工程勘察设计 施 工 图 设 计	K6+418.3 新沙高架桥 桥面板现浇带钢筋布置图	设计		复核		一审		二审		图号	SZYS/04/02/02/01/ 59

1/2端横梁顶现浇带钢筋平面布置图

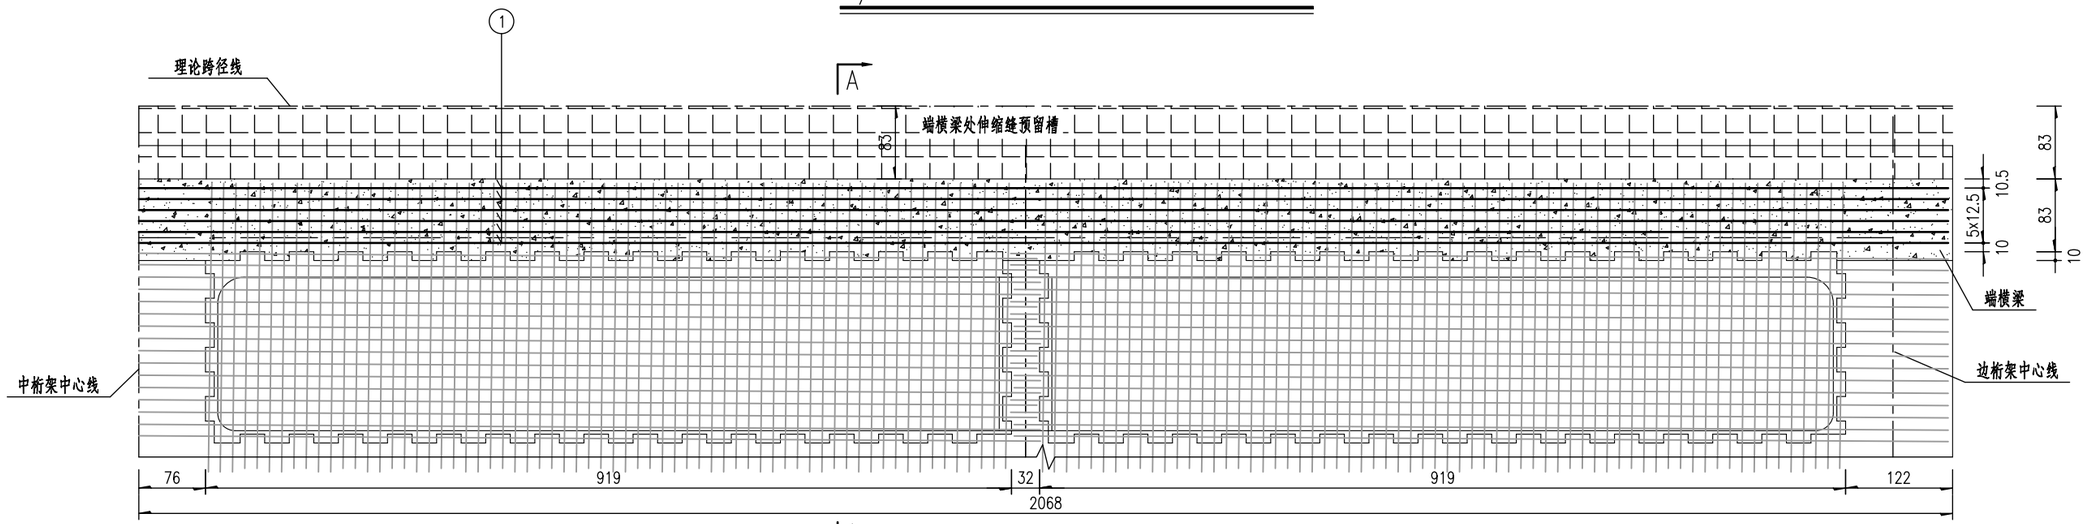

A-A

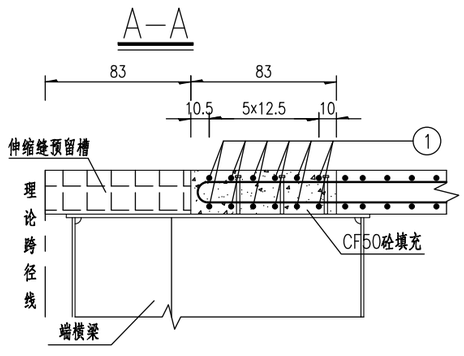

钢筋大样

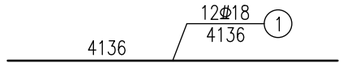

钢筋数量表 (端横梁)

钢筋编号	规格 (mm)	单根长 (cm)	根数	总长 (m)	单位重 (kg/m)	总重 (kg)	全桥2个合计 (kg)
1	Φ18	4136.0	12	496.32	2.00	992.6	1985.3
CF50钢纤维混凝土 (m^3)						6.6	13.1

注：

1、本图适用于上层桥面端横梁现浇段，图中尺寸除钢筋直径以毫米计外，其余均以厘米计。

2、桥面板现浇段采用CF50钢纤维混凝土以提高结构抗裂性能，钢纤维掺入量78.5kg/m^3。

3、端部现浇段伸缩缝范围预埋钢筋构造见《伸缩缝安装构造》。

中交第二公路勘察设计研究院有限公司	狮子洋通道工程勘察设计 施 工 图 设 计	K6+418.3 新沙高架桥 桥面现浇端横梁钢筋布置图	设计		复核		一审		二审		图号	SZYS/04/02/02/01/ 60

人行道板横断面布置图

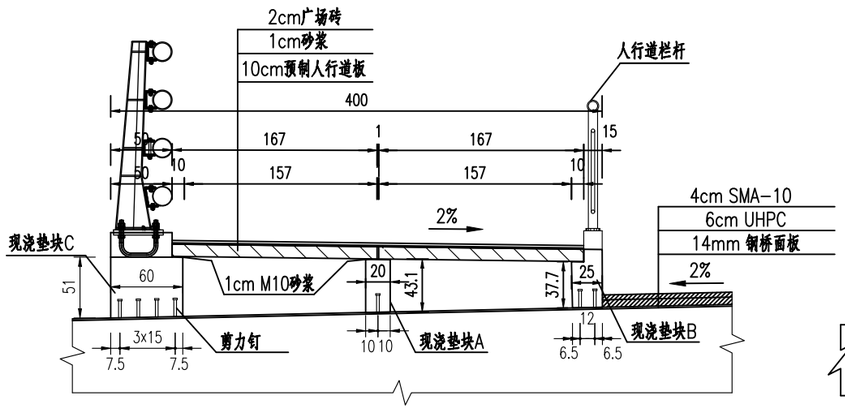

垫块A钢筋断面

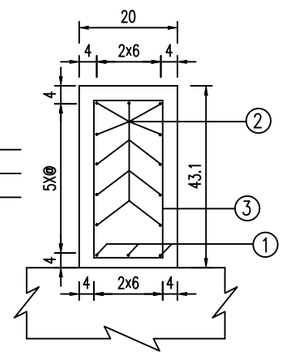

垫块B钢筋断面

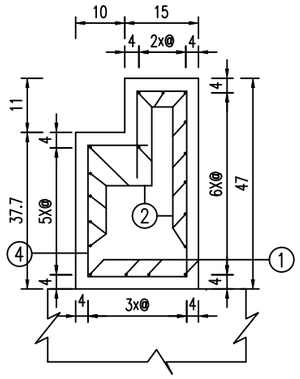

垫块C钢筋断面

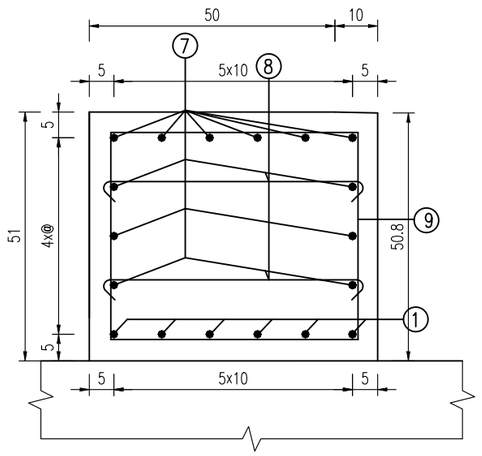

人行道板钢筋平面

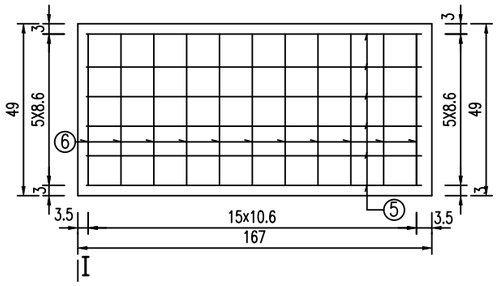

I－I

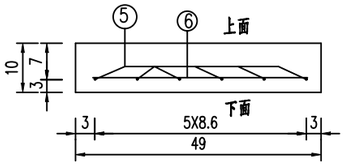

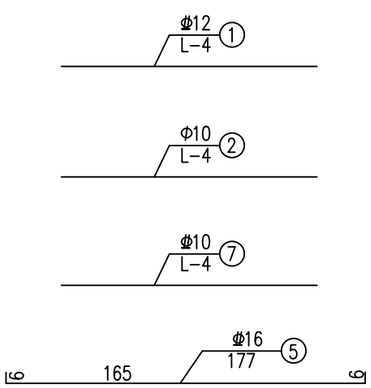

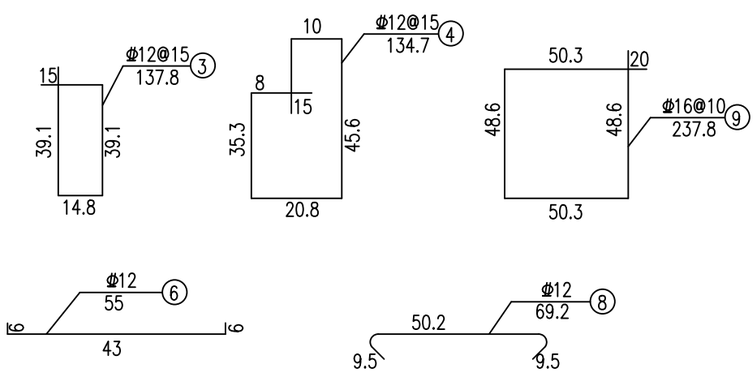

每延米人行道材料表

钢筋编号	直径(mm)	单根长(cm)	根数	总长(m)	单位重(kg)	共计(kg)	合计(kg)
1	Φ12	100.0	13	13.0	0.888	11.5	Φ10:
2	Φ10	100.0	25	25.0	0.617	15.4	15.4
3	Φ12	137.8	7	9.6	0.888	8.6	Φ10:
4	Φ12	134.7	7	9.4	0.888	8.4	7.4
5	Φ16	177.0	12	21.2	1.580	33.6	Φ12:
6	Φ12	55.0	32	17.6	0.888	15.6	56.4
7	Φ10	100.0	12	12.0	0.617	7.4	Φ16:
8	Φ12	69.2	20	13.8	0.888	12.3	71.1
9	Φ16	237.8	10	23.8	1.580	37.6	
广场砖(m²)：3.35 C30混凝土(m³)：0.84 砂浆(m³)：0.04 剪力钉(个)：49							

人行道板工程数量表

材料		单位	总计
C30混凝土		m³	577.9
广场砖		m²	2304.8
砂浆		m³	27.5
钢筋	Φ16	kg	48938.5
	Φ12	kg	38804.1
	Φ10	kg	5094.0
	Φ10	kg	10612.4
	小计	kg	103449.0
剪力钉	Φ22x150mm	个	33712

注：

1、本图尺寸除钢筋直径以毫米计外余均以厘米计。

2、浇注垫块混凝土时应注意预埋护栏钢筋。

3、图中钢筋若与路灯配电箱钢筋有冲突时可适当挪动和截断。

4、人行道板与垫块之间设1cm M10砂浆。

5、本图中L为沿桥梁纵向，每一联桥梁长度。

6、人行道板垫块每隔6m设置一道缝隙防止开裂。

7、剪力钉纵桥向间距为15cm。

8、此图适用于新沙高架桥下层人行道。

中交第二公路勘察设计研究院有限公司	狮子洋通道工程勘察设计 施 工 图 设 计	K6+418.3 新沙高架桥 人行道板设计图	设计		复核		一审		二审		图号	SZYS/04/02/02/01/61

主桥支座平面布置图

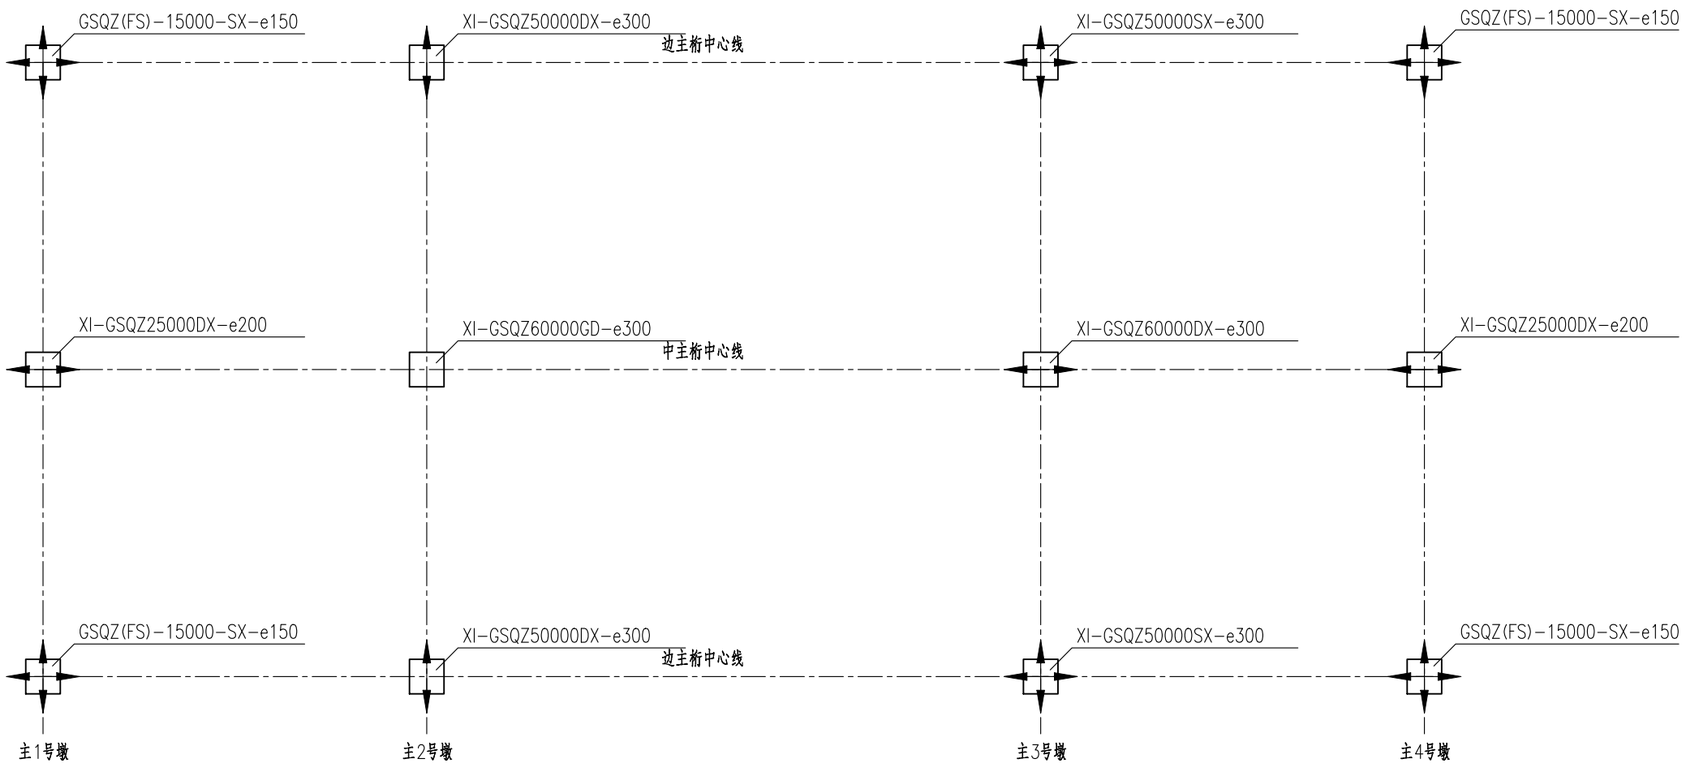

支座数量表

支座型号	数量(个)	合计(个)
XI-GSQZ60000GD-e300	1	2
XI-GSQZ60000DX-e300	1	
XI-GSQZ50000DX-e300	2	4
XI-GSQZ50000SX-e300	2	
XI-GSQZ25000DX-e200	2	2
GSQZ(FS)-15000-SX-e150	4	4

注：

1、支座采用环向钢丝绳组合阻尼支座。GD表示固定支座；DX表示单向活动支座；SX表示双向活动支座。

2、测力支座布置于主墩6个支座和过渡墩中间支座布置。

中交第二公路勘察设计研究院有限公司	狮子洋通道工程勘察设计 施 工 图 设 计	K6+418.3 新沙高架桥 主桥支座布置及安装图	设计	余汪千	复核	袁勤	一审	沈华	二审	李忠	图号	SZYS/04/02/02/01/62

支座安装尺寸表

支座型号	竖向力	支座外形尺寸														上套筒		下套筒		等效阻尼比
	KN	A	A1	A2	B	B1	B2	B0	C	C1	C2	D	D1	D2	H	φ1	L1	φ2	L2	heq
XI-GSQZ60000GD-e300	60000	2610	2290	1560	2610	2290	1560	3975	2610	2220	1310	2610	2220	1310	980	210	735	260	910	0.2
XI-GSQZ60000DX-e300	60000	2610	2290	1560	2610	2290	1560	3975	2610	2220	1310	2610	2220	1310	980	210	735	260	910	0.2
XI-GSQZ50000DX-e300	50000	2450	2150	1450	2450	2150	1450	3650	2450	2090	1250	2450	2090	1250	930	200	700	240	840	0.2
XI-GSQZ50000SX-e300	50000	2370	2070	1370	2370	2070	1370	2370	2370	2010	1170	2370	2010	1170	930	200	700	240	840	0.2
XI-GSQZ25000DX-e200	25000	1730	1510	1010	1730	1510	1010	2625	1730	1470	880	1730	1470	880	665	140	490	170	595	0.2

中交第二公路勘察设计研究院有限公司	狮子洋通道工程勘察设计 施 工 图 设 计	K6+418.3 新沙高架桥 主桥支座布置及安装图	设计	余汪千	复核	袁勤	一审	沈华	二审	李忠	图号	SZYS/04/02/02/01/62

支座垫石平面钢筋布置图

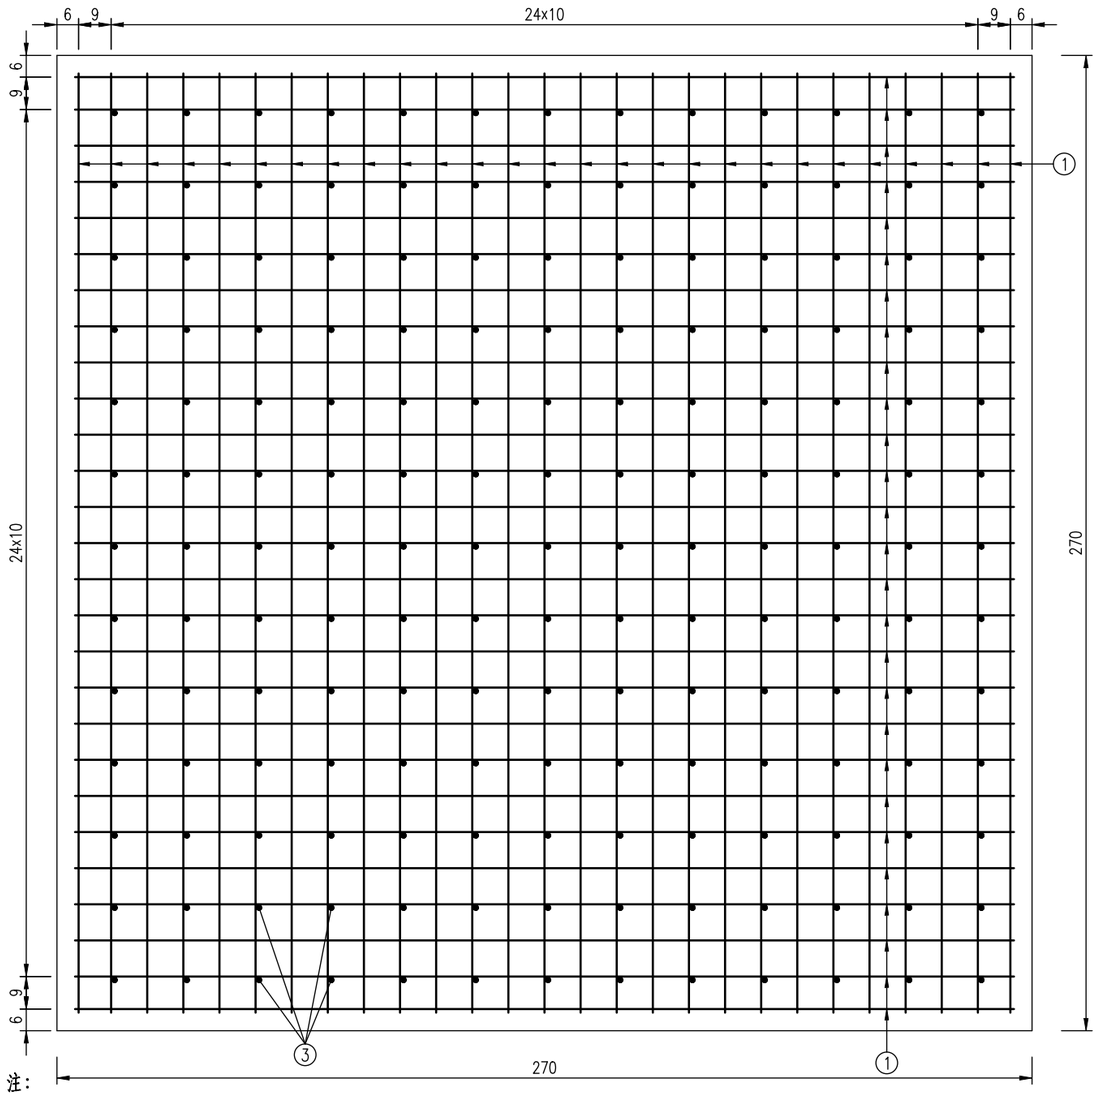

中桥支座垫石立面钢筋布置图

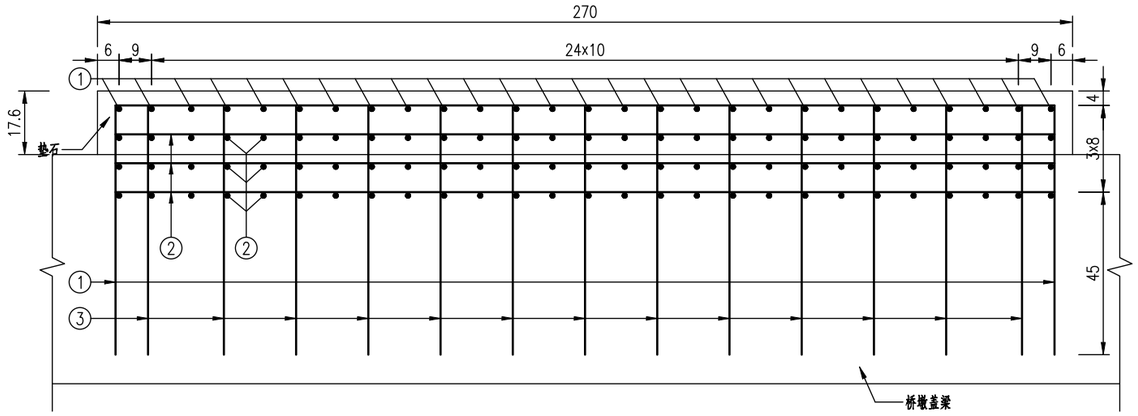

边桥支座垫石立面钢筋布置图

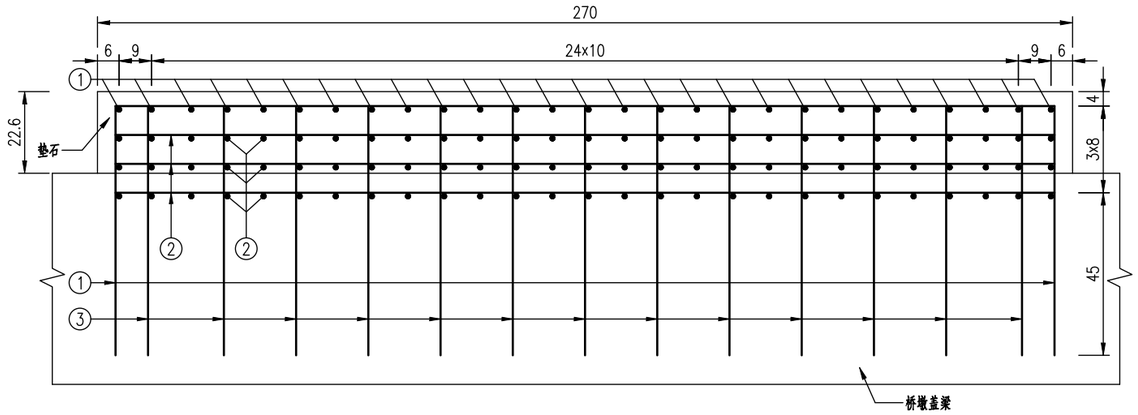

注：

1、本图尺寸除钢筋直径以毫米计外，其余均以厘米计。

2、支座垫石钢筋若与盖梁(墩柱)钢筋冲突，可适当挪动支座垫石钢筋。

3、支座垫石在盖梁上具体布置位置详见对应桥墩一般构造图。

4、本图为理论跨径线处设计标高换算的垫石中心高度，施工时的实际高度应结合路线纵、横坡进行换算。

5、本图垫石高度不含砂浆层厚度，砂浆层厚度具体参考对应的支座布置及安装图取用。

6、本图适用于新沙高架1#、2#主墩钢桁支座垫石。

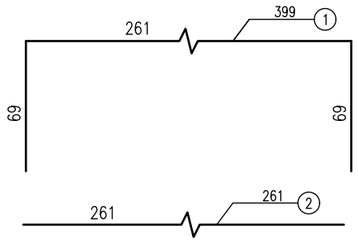

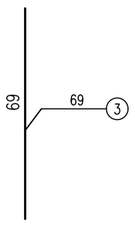

数量汇总表

编号	规格(mm)	单根长(cm)	根数	总长(m)	总重(kg)	单处合计(kg)	全桥总计(kg)
1	Φ12	399	54	215.5	191.3	670.3	4022.1
2	Φ12	261	162	422.8	375.5		
3	Φ12	69	169	116.6	103.5		
C50小石子砼(m³)							9.2

中交第二公路勘察设计研究院有限公司	狮子洋通道工程勘察设计 施 工 图 设 计	K6+418.3 新沙高架桥 全桥支座垫石构造及钢筋布置图	设计	刘川	复核	袁勤	一审	沈维	二审	李忠	图号	SZYS/04/02/02/01/63

4250220 8427189

支座垫石平面钢筋布置图

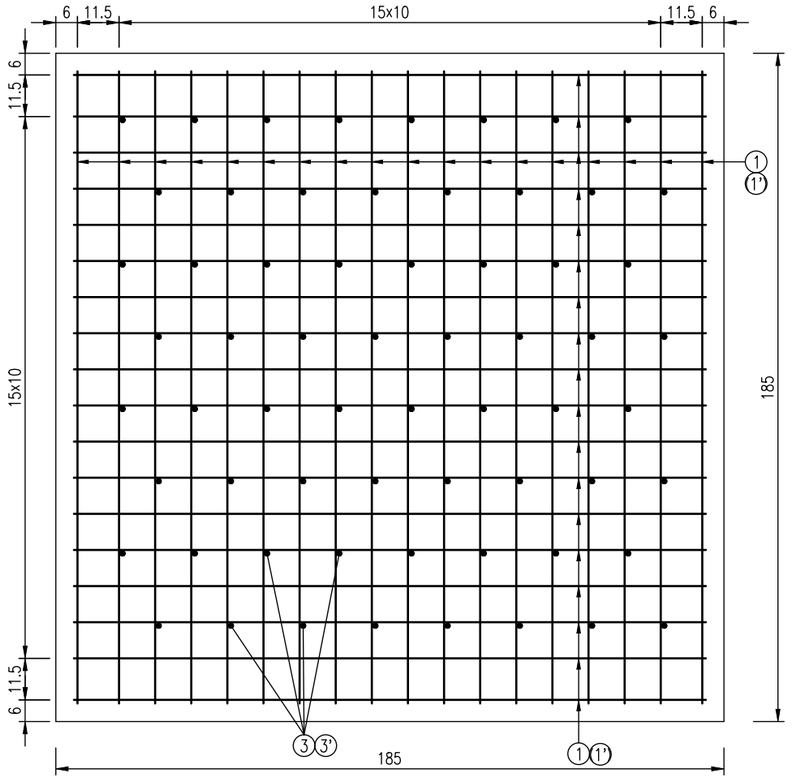

中桥支座垫石立面钢筋布置图

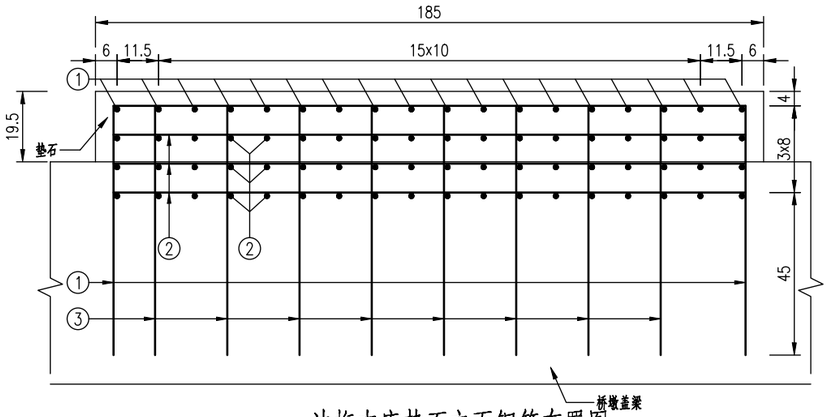

边桥支座垫石立面钢筋布置图

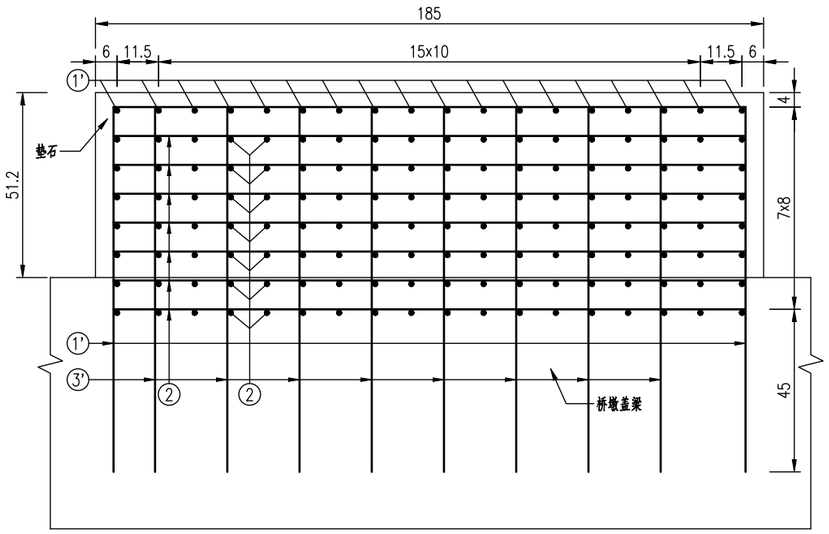

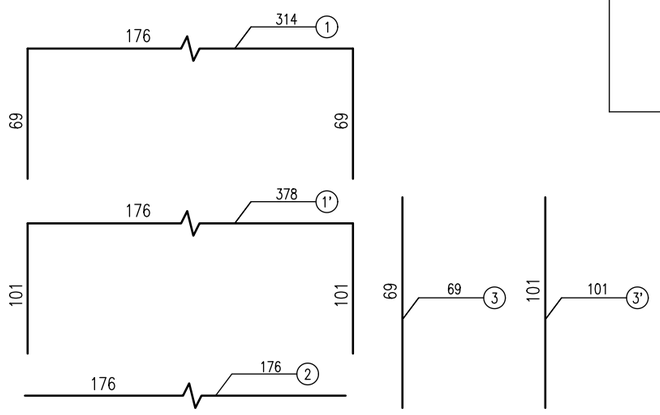

注：

1、本图尺寸除钢筋直径以毫米计外，其余均以厘米计。

2、支座垫石钢筋若与盖梁(墩柱)钢筋冲突，可适当挪动支座垫石钢筋。

3、支座垫石在盖梁上具体布置位置详见对应桥墩一般构造图。

4、本图为理论跨径线处设计标高换算的垫石中心高度，施工时的实际高度应结合路线纵、横坡进行换算。

5、本图垫石高度不含砂浆层厚度，砂浆层厚度具体参考对应的支座布置及安装图取用。

6、本图适用于新沙高架0#、3#过渡墩钢桁支座垫石。

数量汇总表

编号	规格(mm)	单根长(cm)	根数	总长(m)	总重(kg)	单处合计(kg)	全桥总计(kg)
1	Φ12	314	36	113.0	100.4	1452.6	2905.1
1'	Φ12	378	72	272.2	241.7		
2	Φ12	176	612	1077.1	956.5		
3	Φ12	69	64	44.2	39.2		
3'	Φ12	101	128	129.3	114.8		
C50小石子砼(m³)							8.3

中交第二公路勘察设计研究院有限公司	狮子洋通道工程勘察设计 施 工 图 设 计	K6+418.3 新沙高架桥 全桥支座垫石构造及钢筋布置图	设计	刘川	复核	袁勤	一审	沈雅	二审	李忠	图号	SZYS/04/02/02/01/63

引桥侧68米组合梁支座垫石钢筋平面布置图

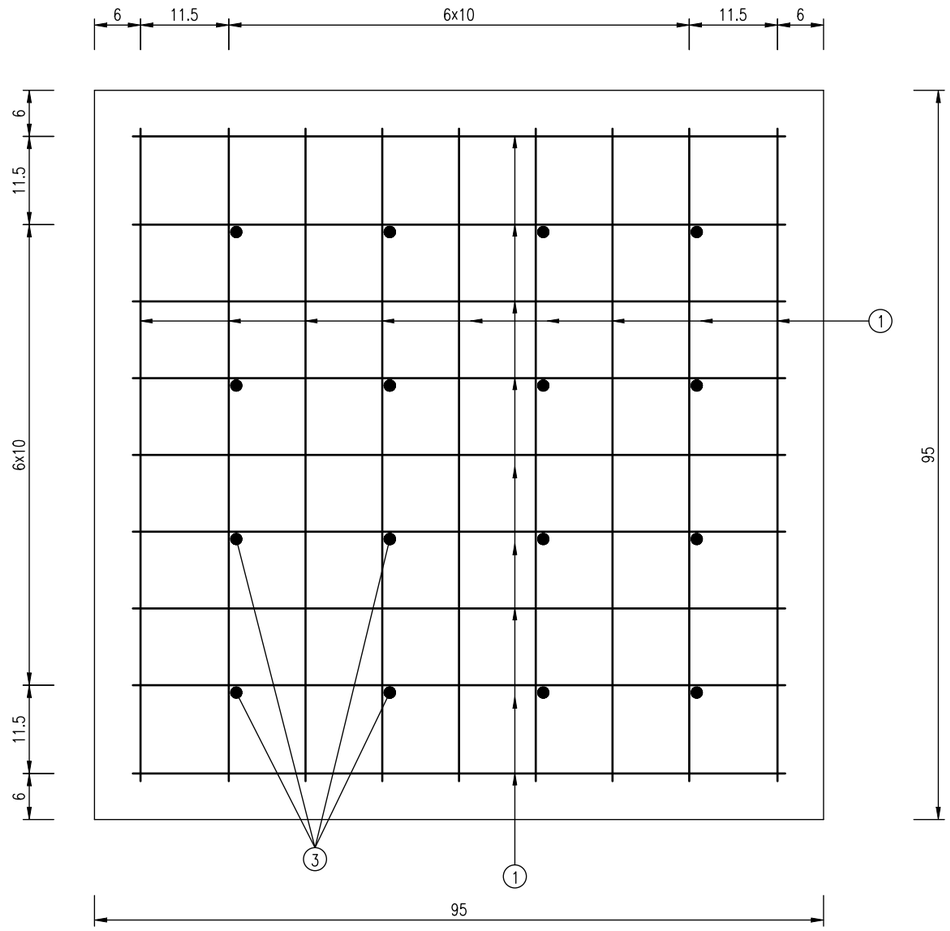

引桥侧68米组合梁支座垫石钢筋立面布置图

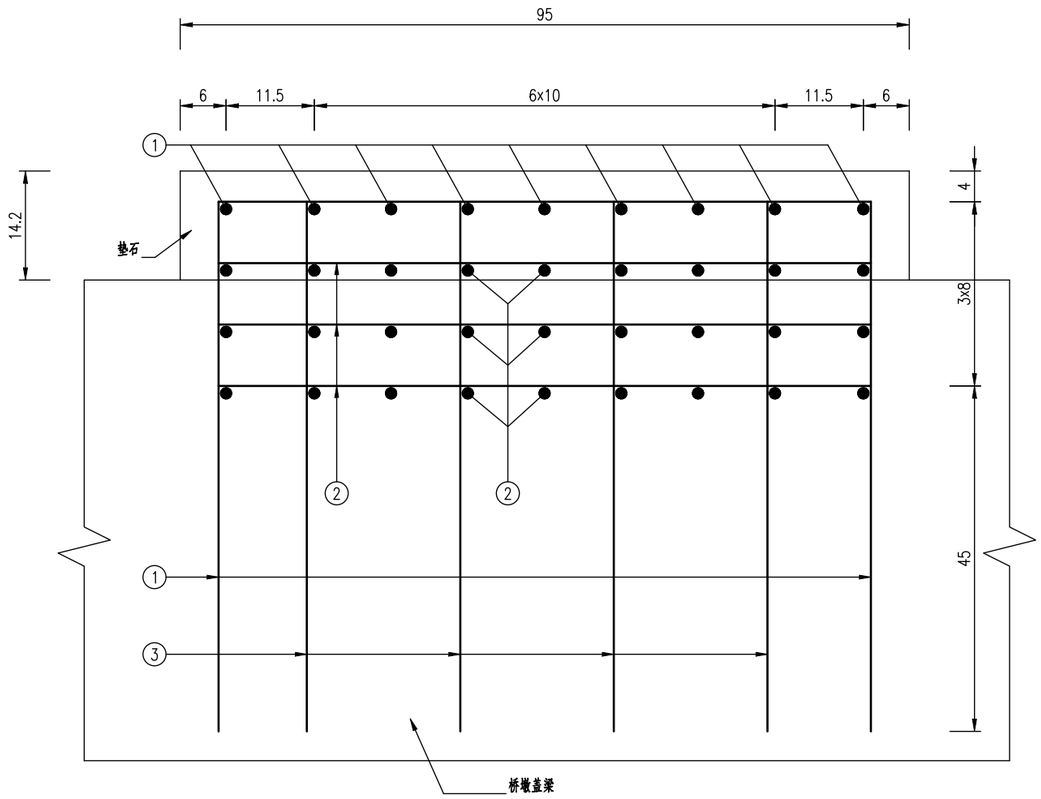

注：

1、本图尺寸除钢筋直径以毫米计外，其余均以厘米计。

2、支座垫石钢筋若与盖梁(墩柱)钢筋冲突，可适当挪动支座垫石钢筋。

3、支座垫石在盖梁上具体布置位置详见对应桥墩一般构造图。

4、本图为理论跨径线处设计标高换算的垫石中心高度，施工时的实际高度应结合路线纵、横坡进行换算。

5、施工时垫石顶面需额外设3cm厚砂浆层，本图未示意。

6、本图适用于新沙高架双层钢桁桥墩上的68米跨径的组合梁支座垫石。

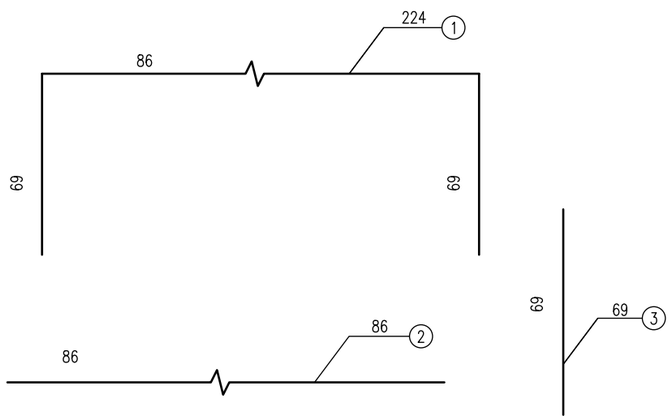

数量汇总表

编号	规格(mm)	单根长(cm)	根数	总长(m)	总重(kg)	单处合计(kg)	全桥总计(kg)
1	φ12	224	14	31.4	27.8	69.7	976.2
2	φ12	86	42	36.1	32.1		
3	φ12	69	16	11.0	9.8		
C50小石子砼(m³)							1.8

中交第二公路勘察设计研究院有限公司	狮子洋通道工程勘察设计 施 工 图 设 计	K6+418.3 新沙高架桥 全桥支座垫石构造及钢筋布置图	设计	刘川	复核	袁勤	一审	沈维	二审	李忠	图号	SZYS/04/02/02/01/63

A-A

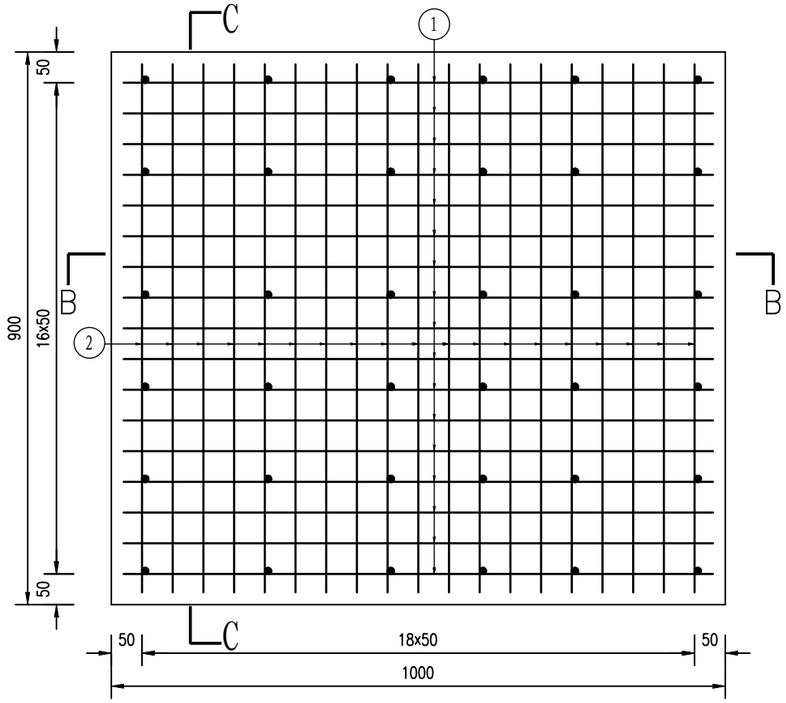

B-B

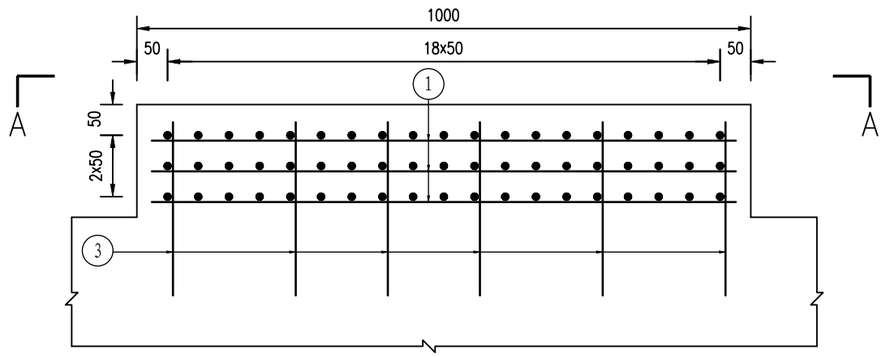

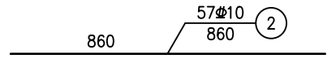

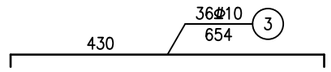

C-C

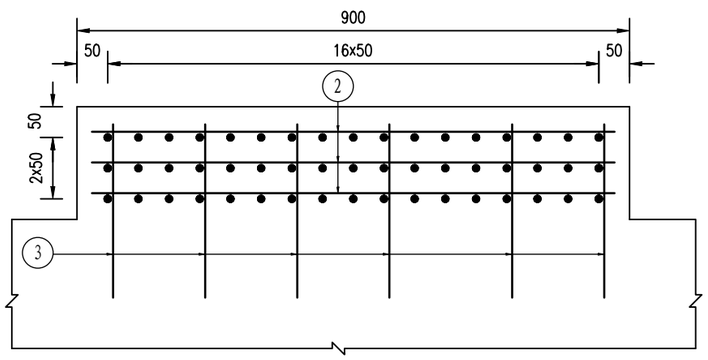

支座垫石材料数量表

钢筋编号	直 径 (mm)	每根长 (mm)	根 数	共 长 (m)	共 重 (Kg)	单个合计 (Kg)	全桥合计 (Kg)
1	Φ10	960	51	48.96	30.21	74.99	1649.78
2	Φ10	860	57	49.02	30.25		
3	Φ10	654	36	23.54	14.53		
C50小石子混凝土(m³)						0.14	3.08

注:

1.本图尺寸均以mm计。

2.本图仅为示意，施工图设计时垫石高度应根据具体情况确定。

3.支座垫石采用C50小石子混凝土，垫石在理论跨径线处的中心高度理论均为151mm，图中未示意。实际应根据纵、横坡进行计算。

4.本图适用于新沙高架双层钢桁桥墩上的40米小箱梁支座垫石。

中交第二公路勘察设计研究院有限公司	狮子洋通道工程勘察设计 施 工 图 设 计	K6+418.3 新沙高架桥 全桥支座垫石构造及钢筋布置图	设计	刘川	复核		一审		二审		图号	SZYS/04/02/02/01/63

南沙

A-A

东莞

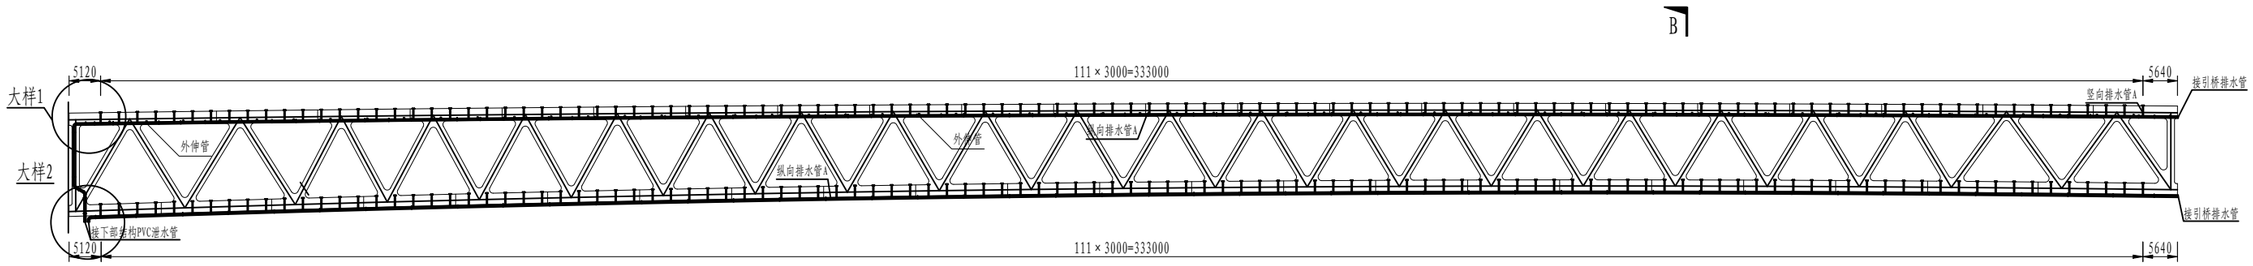

B-B

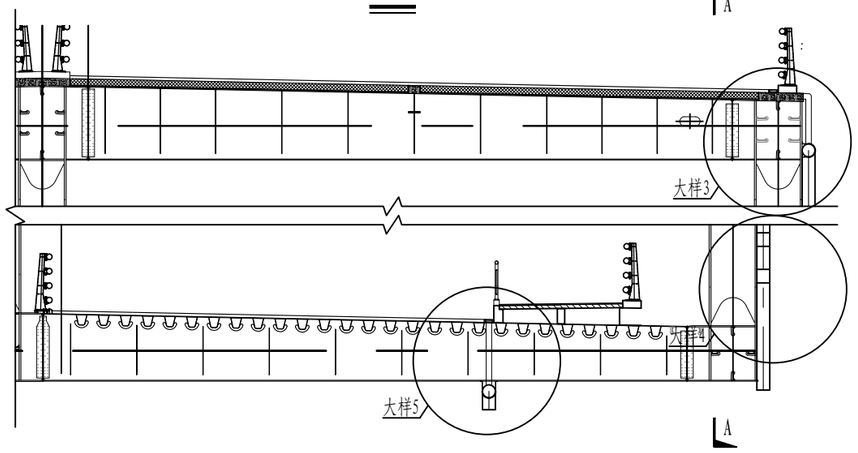

大样1

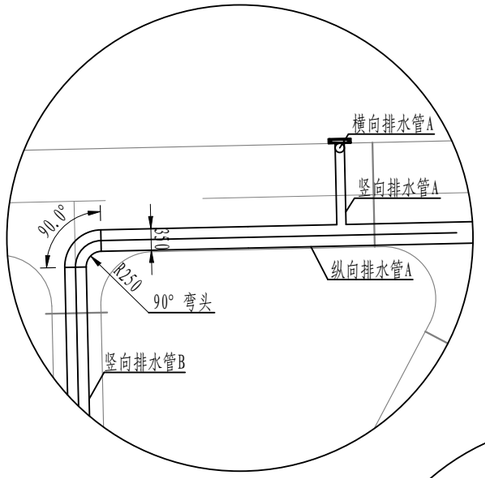

大样2

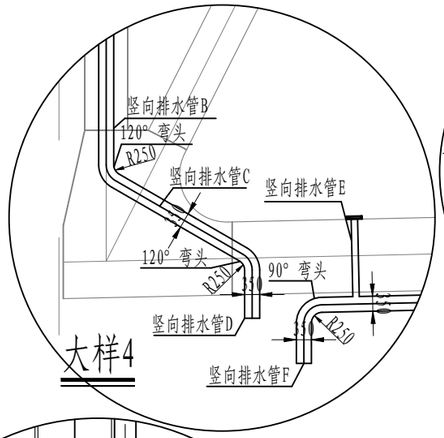

外伸管大样

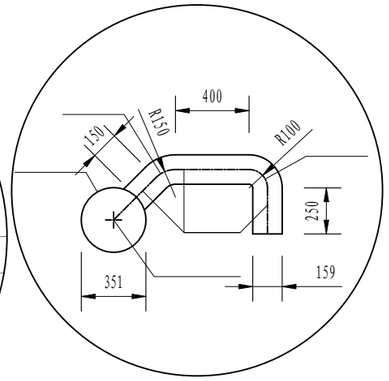

大样3

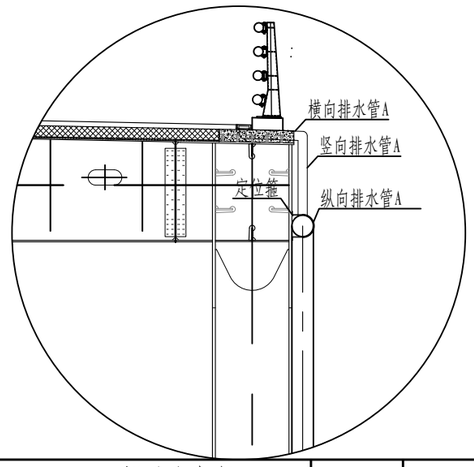

大样4

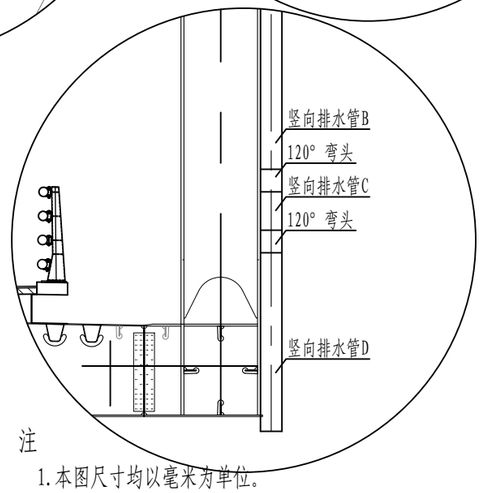

大样5

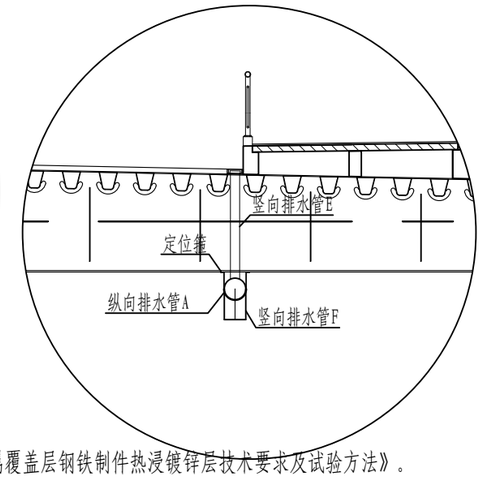

全桥排水工程数量表

项目	规格（mm）	材质	长度（m）	全桥数量	总长（m）
纵向排水管A	φ350	镀锌钢管	340.000	4	1360.000
横向排水管A	φ100		0.850	224	190.400
竖向排水管A	φ100		1.580	224	353.920
竖向排水管B	φ350		5.680	2	11.360
竖向排水管C	φ350		1.580	2	3.160
竖向排水管D	φ350		5.910	2	11.820
竖向排水管E	φ100		1.920	224	430.080
竖向排水管F	φ350		0.350	2	0.700
外伸管	φ150		0.800	112	89.600
转向管1	90°		0.667	564	376.188
转向管2	120°		0.445	4	1.780
转向管3	135°		0.500	112	56.000
三通管	90°		560(个)		
合计(m)					2885.008
泄水槽（套）					448
盖板（套）					448
定位箍(套)					708

注

1. 本图尺寸均以毫米为单位。
2. 桥架梁范围的泄水管均采用镀锌钢管，镀锌执行《金属覆盖层钢铁制件热浸镀锌层技术要求及试验方法》。
3. 定位箍采用M10膨胀螺栓固定，螺栓应采用镀锌防腐措施，上层每隔6米设置一道外伸管。
4. 本图适用于新沙高架桥。
5. 纵向排水管为单向坡度。

中交第二公路勘察设计研究院有限公司	狮子洋通道工程勘察设计 施 工 图 设 计	K6+418.3 新沙高架桥 桥面排水布置图	设计		复核		一审		二审		图号	SZYS/04/02/02/01/65

上层桥面D320型伸缩装置构造示意图

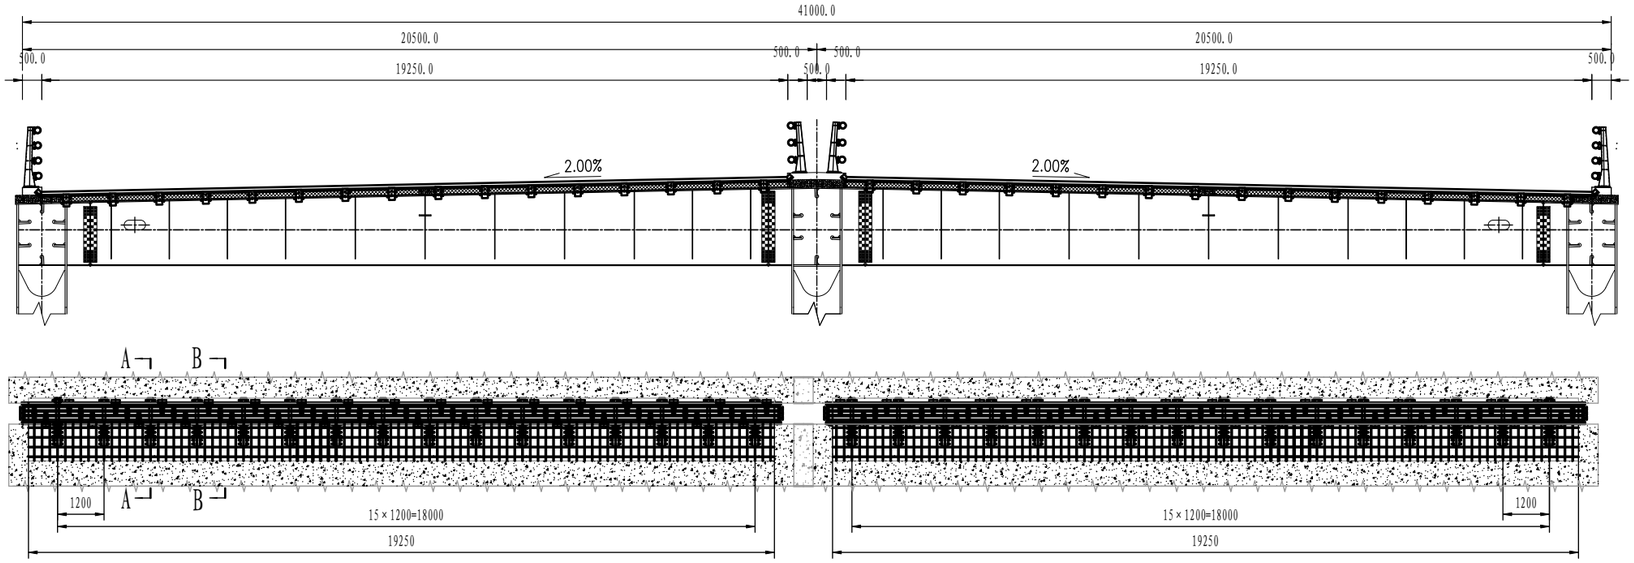

支承系统截面示意图(A-A)

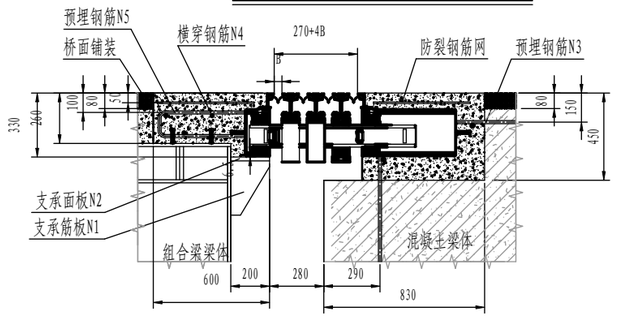

锚固组件截面示意图(B-B)

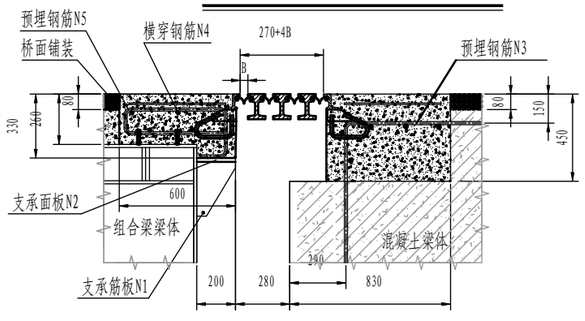

中梁型钢大样

(Q355, ⩾42.3kg/m)

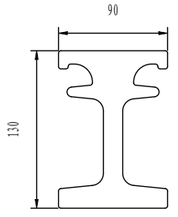

伸缩装置每延米材料用量表

N	规格型号	数量	单重(kg)	共重(kg)
N1	t16	7	3.75	26.5
N2	t20	1	31.4	31.4
N3	Φ16	6	3	18
N4	Φ16	10	1.58	15.8
N5	Φ16	6	2.37	14.22
防裂钢筋网	φ8×100×100	2	施工时配置	10.6

附注:

1. 本图尺寸均以mm为单位；伸缩装置满足《公路桥梁伸缩装置通用技术条件》（JT/T 327-2016）的相关规定。
2. 此模数式伸缩装置位移量0～320mm，出厂定位缝宽B=40mm，工地安装时根据温度调整缝宽以适应梁体位移。
3. 支承面板N2沿横桥向通长布置，支承筋板N1间距250mm；支承面（筋）板在梁体施工时由专业焊工根据标高定位焊接，焊后去应力，并做好防腐涂装。
4. 预埋钢筋N3在梁体施工时预埋，间距200mm，锚固长度不小于25d；预埋钢筋N5在伸缩装置施工时预埋，间距200mm;
5. 先安装伸缩装置后铺路面，伸缩装置与设计路面标高平齐，用3m直尺检查高差，高差⩽2mm。
6. 伸缩装置表面涂装满足《公路桥梁钢结构防腐涂装技术条件》（JT/T 722-2008）中配套编号S05相关要求。
7. 槽区浇筑C50结构型短切玄武岩纤维混凝土。

中交第二公路勘察设计研究院有限公司	狮子洋通道工程勘察设计 施 工 图 设 计	K6+418.3 新沙高架桥 伸缩缝安装构造图	设计		复核		一审		二审		图号	SZYS/04/02/02/01/66

下层桥面D320型伸缩装置构造示意图

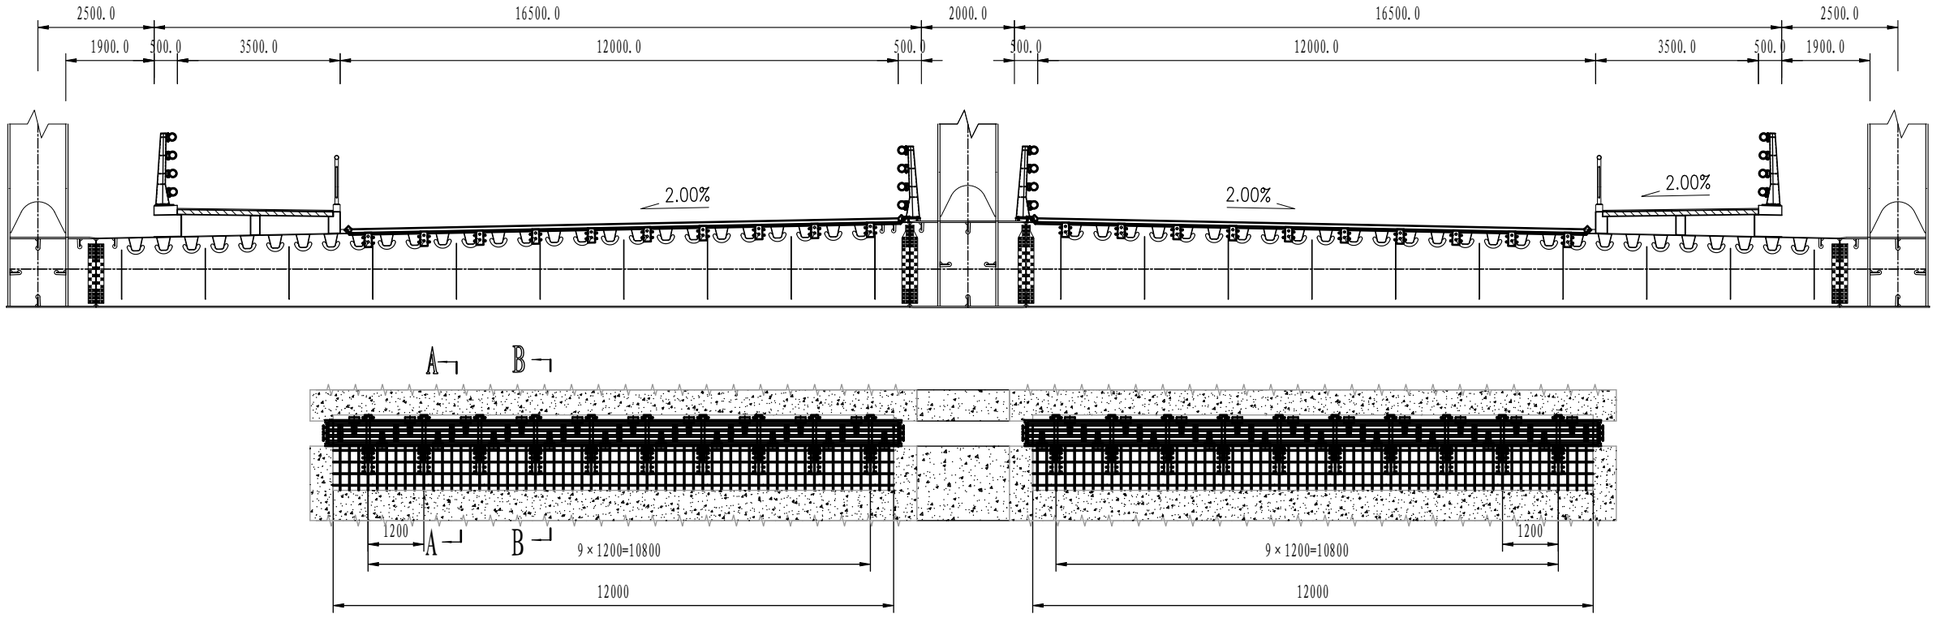

支承系统截面示意图(A-A)

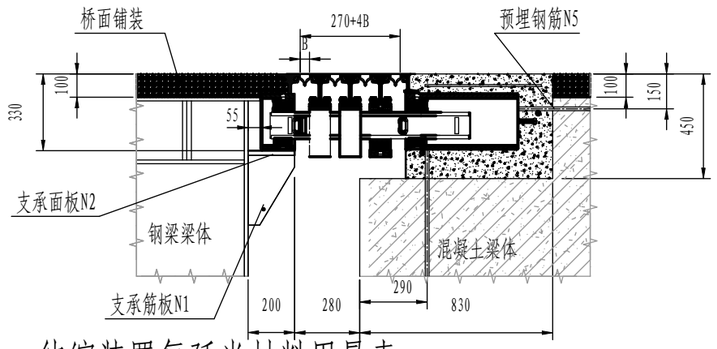

锚固组件截面示意图(B-B)

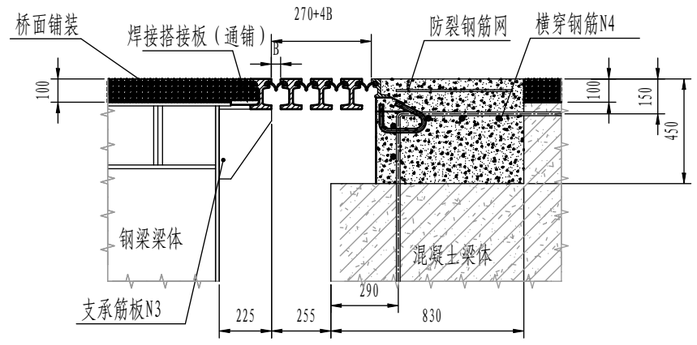

中梁型钢大样

(Q355, ≥42.3kg/m)

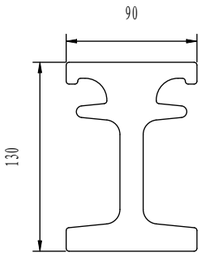

伸缩装置每延米材料用量表

N	规格型号	数量	单重(kg)	共重(kg)
N1	t16	2	3.75	7.5
N2	t20×200×250	1	7.85	7.85
N3	t16	5	4.24	21.2
N4	Φ16	6	3	18
N5	Φ16	5	1.58	7.9
防裂钢筋网	φ8×100×100	1	施工时配置	5.32

附注：

1. 本图尺寸均以mm为单位；伸缩装置满足《公路桥梁伸缩装置通用技术条件》（JT/T327-2016）的相关规定。
2. 此模数式伸缩装置位移量0～320mm，出厂定位缝宽B=40mm，工地安装时根据温度调整缝宽以适应梁体位移。
3. 支承面板N2梁体施工时由专业焊工根据标高定位焊接，间距1200mm，焊后去应力，并做好防腐涂装；
   每一块N2下焊接2块支承筋板N1，间距200mm；支承筋板N3在伸缩装置施工时安装，间距200mm。
4. 预埋钢筋N5在梁体施工时预埋，间距200mm，锚固长度不小于25d。
5. 先安装伸缩装置后铺路面，伸缩装置与设计路面标高平齐，用3m直尺检查高差，高差≤2mm。
6. 伸缩装置表面涂装满足《公路桥梁钢结构防腐涂装技术条件》（JT/T 722-2008）中配套编号S05相关要求。
7. 槽区浇筑C50结构型短切玄武岩纤维混凝土。

中交第二公路勘察设计研究院有限公司	狮子洋通道工程勘察设计 施 工 图 设 计	K6+418.3 新沙高架桥 伸缩缝安装构造图	设计	彦昊	复核	袁勤	一审	张华	二审	李忠	图号	SZYS/04/02/02/01/66

上层桥面D240型伸缩装置构造示意图

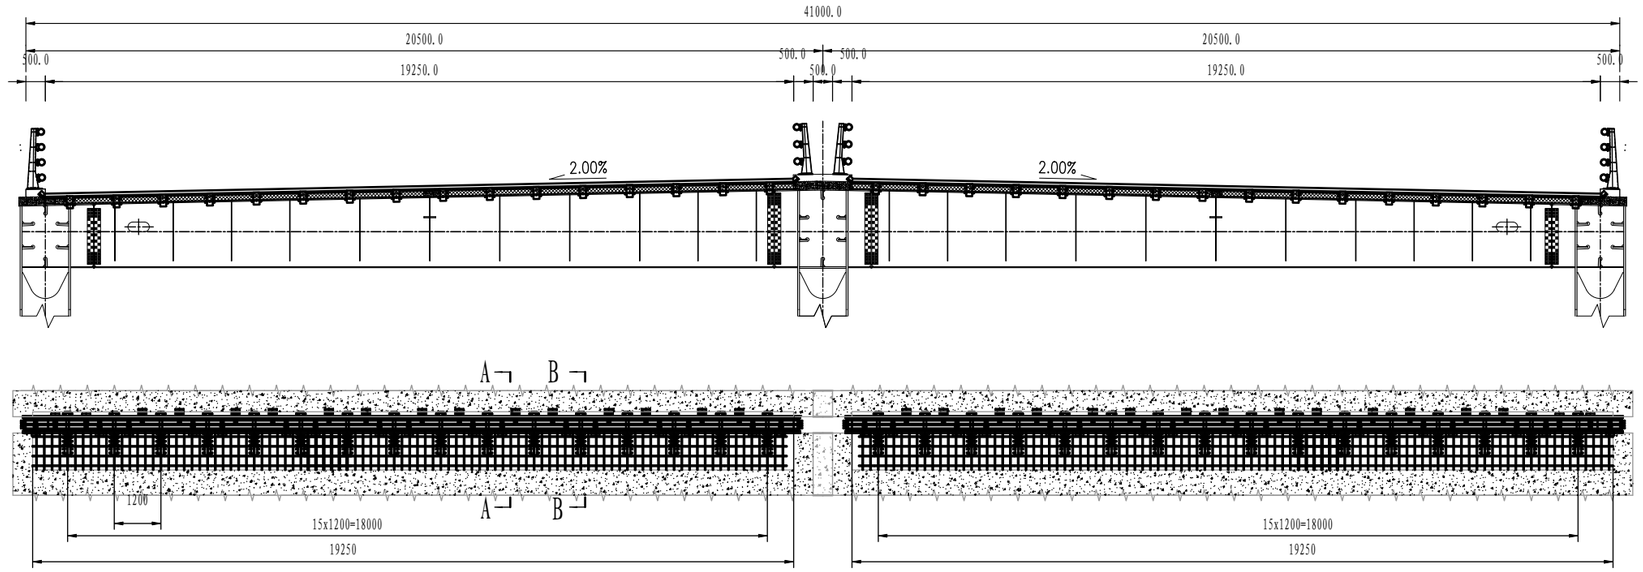

支承系统截面示意图(A-A)

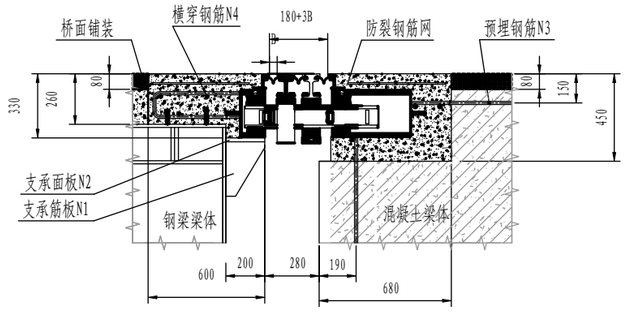

锚固组件截面示意图(B-B)

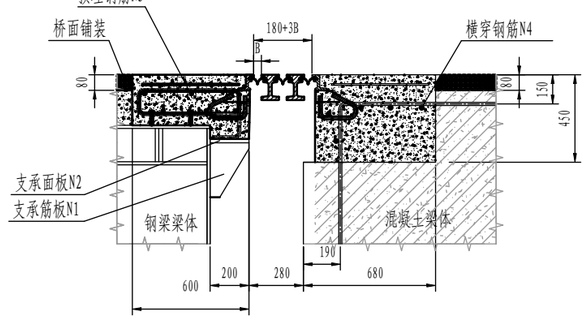

中梁型钢大样

(Q355, ≥42.3kg/m)

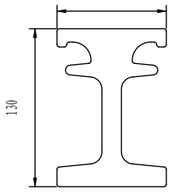

伸缩装置每延米材料用量表

N	规格型号	数量	单重(kg)	共重(kg)
N1	t16	7	3.75	26.5
N2	t20	1	31.4	31.4
N3	Φ16	6	3	18
N4	Φ16	10	1.58	15.8
N5	Φ16	6	2.37	14.22
防裂钢筋网	φ8×100×100	2	施工时配置	10.6

附注:

1. 本图尺寸均以mm为单位；伸缩装置满足《公路桥梁伸缩装置通用技术条件》（JT/T 327-2016）的相关规定。
2. 此模数式伸缩装置位移量0～240mm，出厂定位缝宽B=40mm，工地安装时根据温度调整缝宽以适应梁体位移。
3. 支承面板N2沿横桥向通长布置，支承筋板N1间距250mm；支承面（筋）板在梁体施工时由专业焊工根据标高定位焊接，焊后去应力，并做好防腐涂装。
4. 预埋钢筋N3在梁体施工时预埋，间距200mm，锚固长度不小于25d；预埋钢筋N5在伸缩装置施工时预埋，间距200mm;
5. 先安装伸缩装置后铺路面，伸缩装置与设计路面标高平齐，用3m直尺检查高差，高差≤2mm。
6. 伸缩装置表面涂装满足《公路桥梁钢结构防腐涂装技术条件》（JT/T 722-2008）中配套编号S05相关要求。
7. 槽区浇筑C50结构型短切玄武岩纤维混凝土。

中交第二公路勘察设计研究院有限公司	狮子洋通道工程勘察设计 施 工 图 设 计	K6+418.3 新沙高架桥 伸缩缝安装构造图	设计	蔡昊	复核	袁勤	一审	张华	二审	李超	图号	SZYS/04/02/02/01/66

下层桥面D240型伸缩装置构造示意图

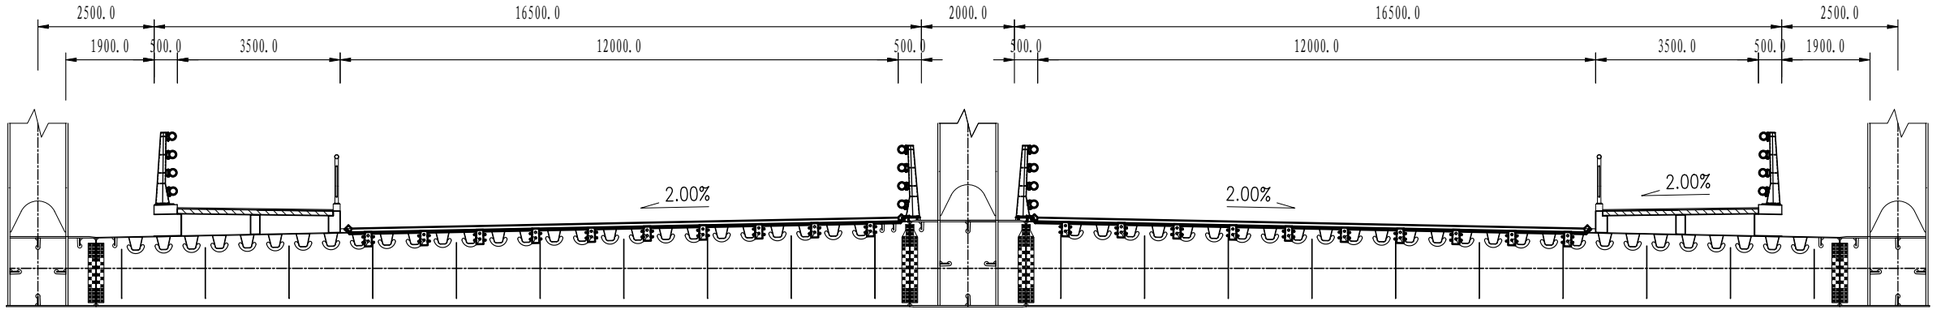

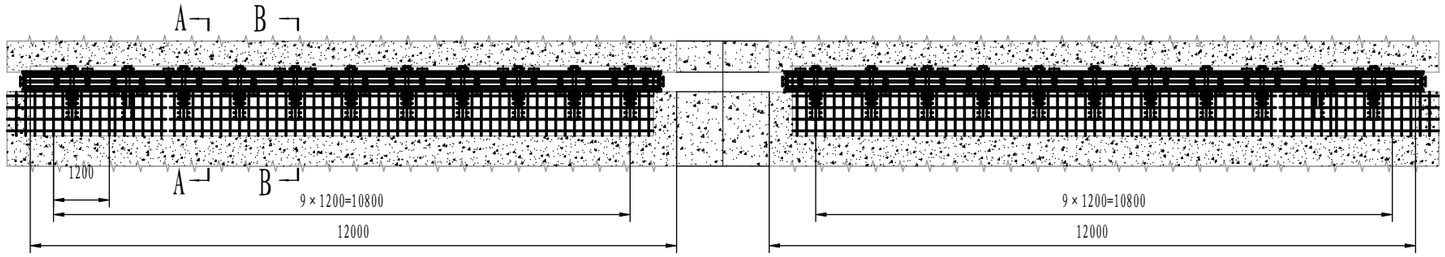

支承系统截面示意图(A-A)

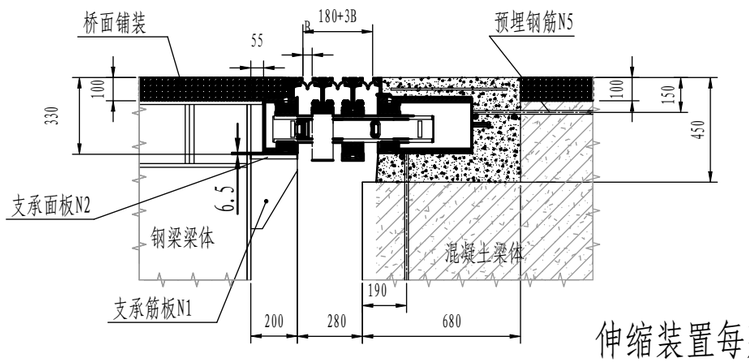

锚固组件截面示意图(B-B)

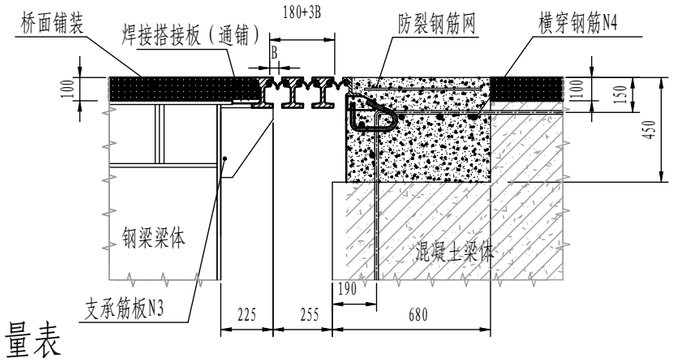

中梁型钢大样

(Q355, ⩾42.3kg/m)

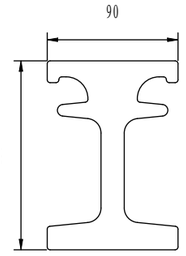

伸缩装置每延米材料用量表

N	规格型号	数量	单重(kg)	共重(kg)
N1	t16	2	3.75	7.5
N2	t20×200×250	1	7.85	7.85
N3	t16	5	4.24	21.2
N4	Φ16	6	3	18
N5	Φ16	5	1.58	7.9
防裂钢筋网	φ8×100×100	1	施工时配置	5.32

附注：

1. 本图尺寸均以mm为单位；伸缩装置满足《公路桥梁伸缩装置通用技术条件》（JT/T327-2016）的相关规定。
2. 此模数式伸缩装置位移量0～240mm，出厂定位缝宽B=40mm，工地安装时根据温度调整缝宽以适应梁体位移。
3. 支承面板N2梁体施工时由专业焊工根据标高定位焊接，间距1200mm，焊后去应力，并做好防腐涂装；每一块N2下焊接2块支承筋板N1，间距200mm；支承筋板N3在伸缩装置施工时安装，间距200mm。
4. 预埋钢筋N5在梁体施工时预埋，间距200mm，锚固长度不小于25d。
5. 先安装伸缩装置后铺路面，伸缩装置与设计路面标高平齐，用3m直尺检查高差，高差⩽2mm。
6. 伸缩装置表面涂装满足《公路桥梁钢结构防腐涂装技术条件》（JT/T 722-2008）中配套编号S05相关要求。
7. 槽区浇筑C50结构型短切玄武岩纤维混凝土。

中交第二公路勘察设计研究院有限公司	狮子洋通道工程勘察设计 施 工 图 设 计	K6+418.3 新沙高架桥 伸缩缝安装构造图	设计	彦昊	复核	袁勤	一审	沈维	二审	图号	SZYS/04/02/02/01/66

上层外侧防撞护栏材料数量表

名称		材质	规格（mm）	单件重（kg）	数量	总重（kg）	备注
立柱	柱体	Q355C	厚度8mm	64.95	458	29747.1	含腹板、柱帽
	立柱法兰		□405x500x22	34.54	458	15819.3	
	预埋钢板		□405x500x20	31.79	458	14559.8	
	加劲肋1		厚度8mm	0.06	458	27.5	设立于立柱底端
	加劲肋2		厚度8mm	0.06	916	55.0	设立于立柱底端
	托架1（立柱端）		厚度6mm	1.99	458	911.4	
	托架2（立柱端）		厚度6mm	1.85	458	847.3	
	托架3（立柱端）		厚度6mm	1.73	458	792.3	
	托架4（立柱端）		厚度6mm	1.78	458	815.2	
标准横梁（7.5m）	横梁1		Φ159x4x7490	121.67	90	10950.0	含托架1（横梁端）
	横梁2		Φ159x6x7490	175.79	90	15821.2	含托架2（横梁端）
	横梁3		Φ159x8x7490	229.66	90	20669.3	含托架3（横梁端）
	横梁4		Φ159x8x7490	229.02	90	20611.4	含托架4（横梁端）
端部横梁（2.75m）	横梁1		Φ159x4x2750	44.91	4	179.6	含托架1（横梁端）
	横梁2		Φ159x6x2750	64.75	4	259.0	含托架2（横梁端）
	横梁3		Φ159x8x2750	84.54	4	338.1	含托架3（横梁端）
	横梁4		Φ159x8x2750	84.28	4	337.1	含托架4（横梁端）
内套管1			Φ146x6x500	10.36	92	953.1	
内套管2			Φ140x9x500	14.53	92	1336.8	
内套管3			Φ133x15x500	21.82	184	4014.9	
外包托架			厚度4.5mm	3.84	368	1413.1	
连接螺栓A（U型带肋螺杆）		10.9级	M30x780		1832	（套）	六角头
连接螺栓B		8.8级	M16x50		2748	（套）	六角头
连接螺栓C		8.8级	M16x170		458	（套）	六角头
连接螺栓D		8.8级	M16x55		1472	（套）	蘑菇头
预埋钢筋（圈型）		HRB400	Φ16	2.04	1832	3737.3	
预埋钢筋（线型）		HRB400	Φ16	543.52	24	13044.5	
基座混凝土		C50			68.8	m³	
密封构件	立柱法兰橡胶垫	氯丁橡胶	405x500x5		458	（个）	
	托架1橡胶垫	氯丁橡胶			458	（个）	
	托架2橡胶垫	氯丁橡胶			458	（个）	
	托架3橡胶垫	氯丁橡胶			458	（个）	
	托架4橡胶垫	氯丁橡胶			458	（个）	
	内套管密封圈1	氯丁橡胶			184	（个）	
	内套管密封圈2	氯丁橡胶			184	（个）	
	内套管密封圈3	氯丁橡胶			368	（个）	
	横梁拔调孔密封塞1	氯丁橡胶			184	（个）	
	横梁拔调孔密封塞2	氯丁橡胶			184	（个）	
	横梁拔调孔密封塞3	氯丁橡胶			368	（个）	

上层内侧防撞护栏材料数量表

名称		材质	规格（mm）	单件重（kg）	数量	总重（kg）	备注
立柱	柱体	Q355C	厚度8mm	51.96	458	23797.7	
	立柱法兰		□380x440x22	28.88	458	13225.0	
	预埋钢板		□380x440x20	26.25	458	12022.7	
	加劲肋1		厚度8mm	0.06	458	27.5	设立于立柱底端
	加劲肋2		厚度8mm	0.06	916	55.0	设立于立柱底端
	托架1（立柱端）		厚度6mm	1.35	458	618.3	
	托架2（立柱端）		厚度6mm	1.35	458	618.3	
	托架3（立柱端）		厚度6mm	1.26	458	577.1	
标准横梁（7.5m）	横梁1		Φ159x4x7490	121.45	90	10930.6	含托架1（横梁端）
	横梁2		Φ159x8x7490	230.11	90	20710.1	含托架2（横梁端）
	横梁3		Φ159x8x7490	229.39	90	20644.9	含托架3（横梁端）
端部横梁（2.75m）	横梁1		Φ159x4x2750	44.82	4	179.3	含托架1（横梁端）
	横梁2		Φ159x8x2750	84.72	4	338.9	含托架2（横梁端）
	横梁3		Φ159x8x2750	84.43	4	337.7	含托架3（横梁端）
内套管1			Φ146x6x500	10.36	92	953.1	
内套管2			Φ133x15x500	21.82	184	4014.9	
外包托架			厚度4.5mm	3.84	276	1059.8	
连接螺栓A（U型带肋螺杆）		10.9级	M30x780		1832	（套）	六角头
连接螺栓C		8.8级	M16x170		1374	（套）	六角头
连接螺栓D		8.8级	M16x55		1104	（套）	蘑菇头
预埋钢筋（圈型）		HRB400	Φ16	2.04	1832	3737.3	
预埋钢筋（线型）		HRB400	Φ16	543.52	24	13044.5	
基座混凝土		C50			68.8	m³	
密封构件	立柱法兰橡胶垫	氯丁橡胶	405x500x5		458	（个）	
	托架1橡胶垫	氯丁橡胶			458	（个）	
	托架2橡胶垫	氯丁橡胶			458	（个）	
	托架3橡胶垫	氯丁橡胶			458	（个）	
	内套管密封圈1	氯丁橡胶			184	（个）	
	内套管密封圈2	氯丁橡胶			368	（个）	
	横梁拔调孔密封塞1	氯丁橡胶			184	（个）	
	横梁拔调孔密封塞2	氯丁橡胶			368	（个）	

下层内侧防撞护栏材料数量表

名称		材质	规格（mm）	单件重（kg）	数量	总重（kg）	备注
立柱	柱体	Q355C	厚度8mm	64.95	458	29747.1	含腹板、柱帽
	立柱法兰		□405x500x22	34.54	458	15819.3	
	底板座		□405x500x87	122.93	458	56301.9	
	加劲肋1		厚度8mm	0.06	458	27.5	设立于立柱底端
	加劲肋2		厚度8mm	0.06	916	55.0	设立于立柱底端
	托架1（立柱端）		厚度6mm	1.99	458	911.4	
	托架2（立柱端）		厚度6mm	1.85	458	847.3	
	托架3（立柱端）		厚度6mm	1.73	458	792.3	
	托架4（立柱端）		厚度6mm	1.78	458	815.2	
标准横梁（7.5m）	横梁1		Φ159x4x7490	121.67	90	10950.0	含托架1（横梁端）
	横梁2		Φ159x6x7490	175.79	90	15821.2	含托架2（横梁端）
	横梁3		Φ159x8x7490	229.66	90	20669.3	含托架3（横梁端）
	横梁4		Φ159x8x7490	229.02	90	20611.4	含托架4（横梁端）
端部横梁（2.75m）	横梁1		Φ159x4x2750	44.91	4	179.6	含托架1（横梁端）
	横梁2		Φ159x6x2750	64.75	4	259.0	含托架2（横梁端）
	横梁3		Φ159x8x2750	84.54	4	338.1	含托架3（横梁端）
	横梁4		Φ159x8x2750	84.28	4	337.1	含托架4（横梁端）
内套管1			Φ146x6x500	10.36	92	953.1	
内套管2			Φ140x9x500	14.53	92	1336.8	
内套管3			Φ133x15x500	21.82	184	4014.9	
外包托架			厚度4.5mm	3.84	368	1413.1	
路缘石			□720x8x1200	54.26	4	217.0	
			□720x8x900	40.69	448	18229.1	
挡水板			□600x8x150	5.65	458	2587.7	
路缘石加劲			□464x8x142	4.14	452	1871.3	
端封板			□480x8x150	4.52	904	4086.1	
连接螺栓A		10.9级	M30x75		3664	（套）	六角头
连接螺栓B		8.8级	M16x50		2748	（套）	六角头
连接螺栓C		8.8级	M16x170		458	（套）	六角头
连接螺栓D		8.8级	M16x55		1472	（套）	蘑菇头
密封构件	立柱法兰橡胶垫	氯丁橡胶	405x500x5		458	（个）	
	托架1橡胶垫	氯丁橡胶			458	（个）	
	托架2橡胶垫	氯丁橡胶			458	（个）	
	托架3橡胶垫	氯丁橡胶			458	（个）	
	托架4橡胶垫	氯丁橡胶			458	（个）	
	内套管密封圈1	氯丁橡胶			184	（个）	
	内套管密封圈2	氯丁橡胶			184	（个）	
	内套管密封圈3	氯丁橡胶			368	（个）	
	横梁拔调孔密封塞1	氯丁橡胶			184	（个）	
	横梁拔调孔密封塞2	氯丁橡胶			184	（个）	
	横梁拔调孔密封塞3	氯丁橡胶			368	（个）	

下层外侧防撞护栏材料数量表

名称		材质	规格（mm）	单件重（kg）	数量	总重（kg）	备注
立柱	柱体	Q550	厚度8mm	78.30	458	35861.4	含腹板、柱帽
	立柱法兰		□405x500x22	34.54	458	15819.3	
	预埋钢板		□405x500x20	31.79	458	14559.8	
	加劲肋1		厚度8mm	0.06	916	55.0	设立于立柱底端
	加劲肋2		厚度8mm	0.06	2748	164.9	设立于立柱底端
	托架1（立柱端）		厚度8mm	2.09	458	957.2	
	托架2（立柱端）		厚度8mm	1.88	458	861.0	
	托架3（立柱端）		厚度8mm	1.72	458	787.8	
	托架4（立柱端）		厚度8mm	1.79	458	819.8	
标准横梁（7.5m）	横梁1		Φ159x4x7490	124.63	90	11216.5	含托架1（横梁端）
	横梁2		Φ159x4x7490	123.48	90	11113.6	含托架2（横梁端）
	横梁3		Φ159x8x7490	231.15	90	20803.9	含托架3（横梁端）
	横梁4		Φ159x8x7490	231.49	90	20834.2	含托架4（横梁端）
端部横梁（2.75m）	横梁1		Φ159x4x2750	46.09	4	184.4	含托架1（横梁端）
	横梁2		Φ159x4x2750	45.63	4	182.5	含托架2（横梁端）
	横梁3		Φ159x8x2750	85.13	4	340.5	含托架3（横梁端）
	横梁4		Φ159x8x2750	85.27	4	341.1	含托架4（横梁端）
内套管1			Φ146x6x674	13.96	184	2569.1	
内套管2			Φ133x15x674	29.42	184	5413.4	
连接螺栓A（U型带肋螺杆）		10.9级	M30x780		1832	（套）	六角头
连接螺栓B		8.8级	M16x50		1832	（套）	六角头
连接螺栓C		8.8级	M16x170		916	（套）	六角头
连接螺栓D		10.9级	M18x190		2208	（套）	蘑菇头
预埋钢筋（圈型）		HRB400	Φ16	2.04	1832	3737.3	
预埋钢筋（线型）		HRB400	Φ16	543.52	24	13044.5	
基座混凝土		C50			68.8	m^3	
密封构件	立柱法兰橡胶垫	天然橡胶	405x500x5		458	（个）	
	托架1橡胶垫	三元乙丙橡胶			458	（个）	
	托架2橡胶垫	三元乙丙橡胶			458	（个）	
	托架3橡胶垫	三元乙丙橡胶			458	（个）	
	托架4橡胶垫	三元乙丙橡胶			458	（个）	
	内套管密封圈1	三元乙丙橡胶			368	（个）	
	内套管密封圈2	三元乙丙橡胶			368	（个）	
	横梁拔调孔密封塞1	三元乙丙橡胶			368	（个）	
	横梁拔调孔密封塞2	三元乙丙橡胶			368	（个）	

中交第二公路勘察设计研究院有限公司	狮子洋通道工程勘察设计 施 工 图 设 计	K6+418.3 新沙高架桥 防撞护栏设计图	设计	彦昊	复核	春勤	一审	张华	二审	李忠	图号	SZYS/04/02/02/01/67

立面

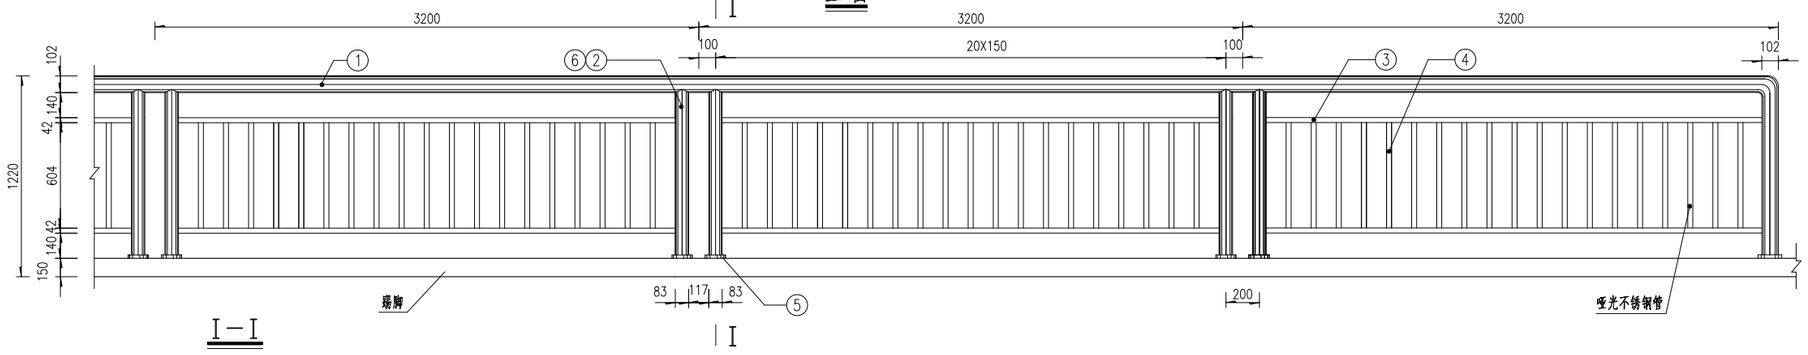

I－I

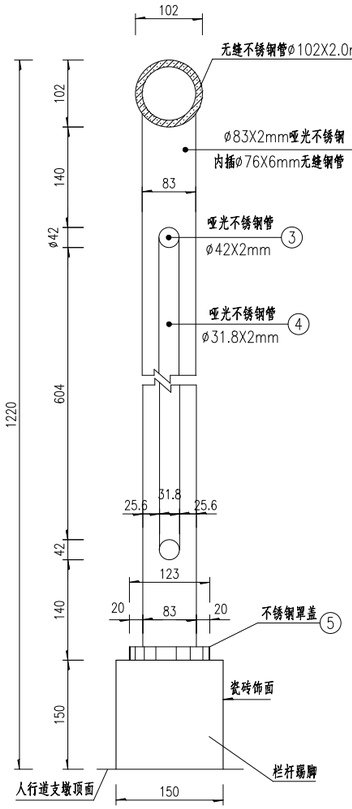

预埋钢板大样

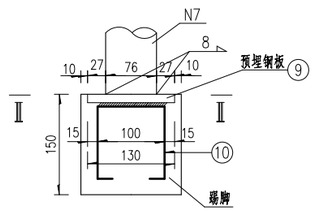

Ⅱ－Ⅱ

（仅示出预埋件）

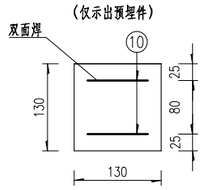

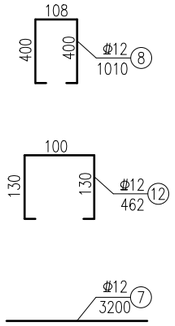

踢脚钢筋大样

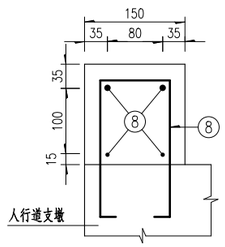

材料数量表

一个标准节间（L=3200）						单侧每3.2米合计	平均每延米合计
编号	规格	长度	单件重	件数	总重		
	(mm)	(mm)	(kg)		(kg)	(kg)	(kg)
1	Φ102X2	3200	15.8	1	15.8	哑光不锈钢管 54.4	哑光不锈钢管 17.0
2	Φ83X2	998	4.0	2	8.0	Q235A钢管 20.8	Q235A钢管 6.5
3	Φ42X2	2930	5.8	2	11.6	Q235B钢板 2.6	Q235B钢板 0.813
4	Φ31.8X2	656	1.0	19	19.0	Ø12钢筋 32.6	Ø12钢筋 10.2
5	Φ123X2			2		C30踢脚混凝土 0.072m³	C30踢脚混凝土 0.023m³
6	Φ76X6	998	10.4	2	20.8	3cm厚瓷砖饰面 0.96m²	3cm厚瓷砖饰面 0.3m²
7	Ø12	3200	2.8	4	11.2		
8	Ø12	1010	0.9	22	19.8		
9	130X130X10	130	1.3	2	2.6		
10	Ø12	462	0.4	4	1.6		

人行道板栏杆材料数量表

材料	单位	总计
哑光不锈钢管	kg	11696.0
Q235A钢管	kg	4472.0
Q235B钢板	kg	559.3
Ø12钢筋	kg	7017.6
C30踢脚混凝土	m³	15.8
3cm厚瓷砖饰面	m²	206.4

注：

1、本图尺寸以毫米计。

2、栏杆采用哑光不锈钢，哑光不锈钢装饰构件在其背面与栏杆点焊，栏杆立柱N6、N2必须与踢脚钢板焊接牢固。

3、梁端等不足标准段处适当调整N4不锈钢管的根数，但管间净距不得大于110mm，立柱间距不得大于3000mm。

4、Q235B碳素结构钢，其技术指标均应符合《碳素结构钢》（GB/T 700-2006）相关要求。

5、本图适用于人行道处栏杆。

中交第二公路勘察设计研究院有限公司	狮子洋通道工程勘察设计 施 工 图 设 计	K6+418.3 新沙高架桥 人行道栏杆构造图	设计		复核		一审		二审		图号	SZYS/04/02/02/01/68

立面

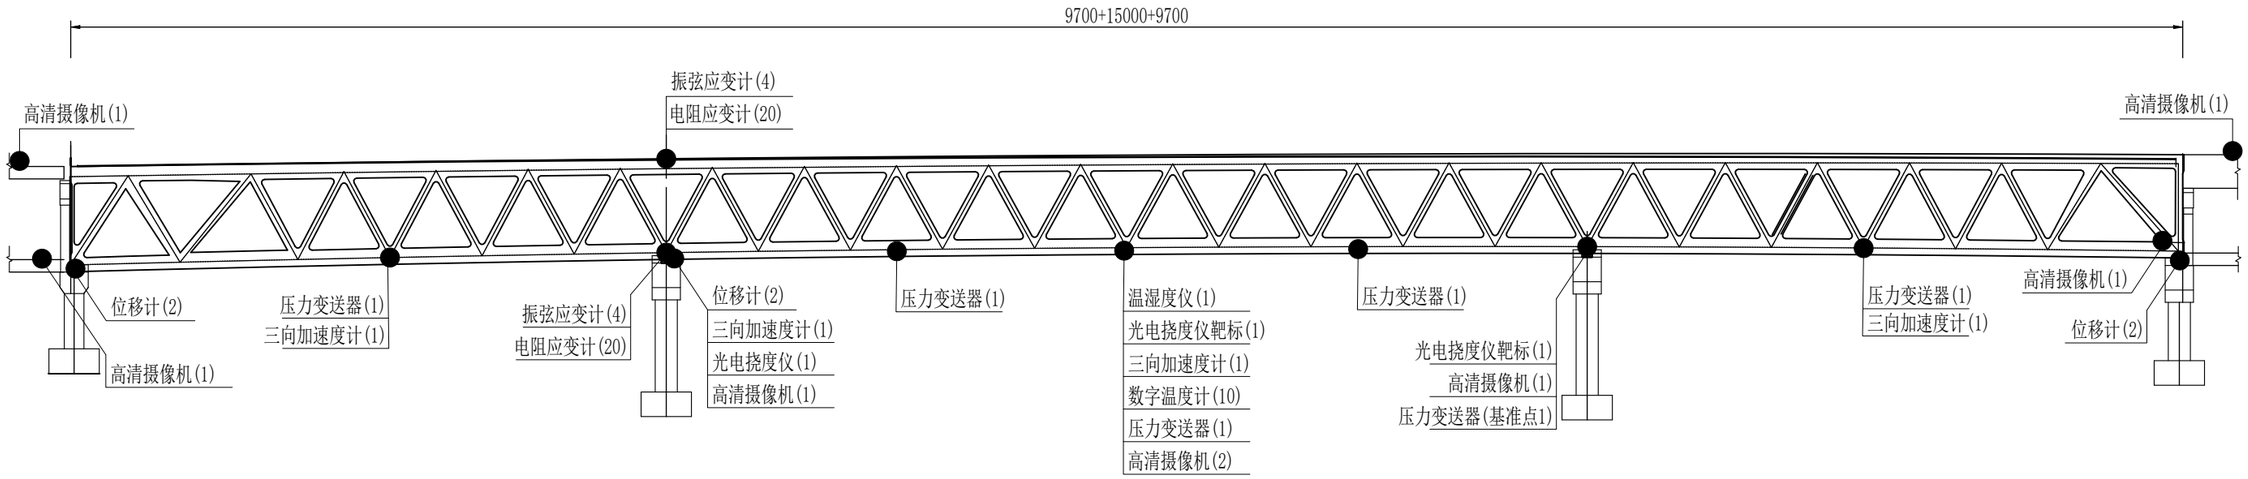

测点一览表

监测类别		监测内容	传感器类型	测点数量
环境	温湿度	环境温度、湿度	温湿度计	1
作用	结构温度	结构构件温度	数字温度计	10
	地震/船撞	桥墩底部加速度	三向加速度计	1
结构响应	位移	主梁线形	压力变送器	6
		主梁动挠度	光电挠度仪	1
		支座位移及梁端纵向位移	磁致伸缩位移计	6
	应变	正交异性钢桥面板应力	电阻应变计	32
		主梁动应变	电阻应变计	8
		主梁静应变	振弦应变计	8
	振动	主梁振动加速度	三向加速度计	3
视频	视频监控	桥面交通状况、通航状况	高清摄像机	8
合计				84

注：
1、本图尺寸以cm为单位；
2、文字后面（）内数字表示测点数量。

中交第二公路勘察设计研究院有限公司	狮子洋通道工程勘察设计 施 工 图 设 计	K6+418.3 新沙高架桥 健康监测系统测点布置图	设计	余汪千	复核	袁勤	一审	沈华	二审	李超	图号	SZYS/04/02/02/01/ 69

4295022747455S

防撞护墙路灯基座平面图

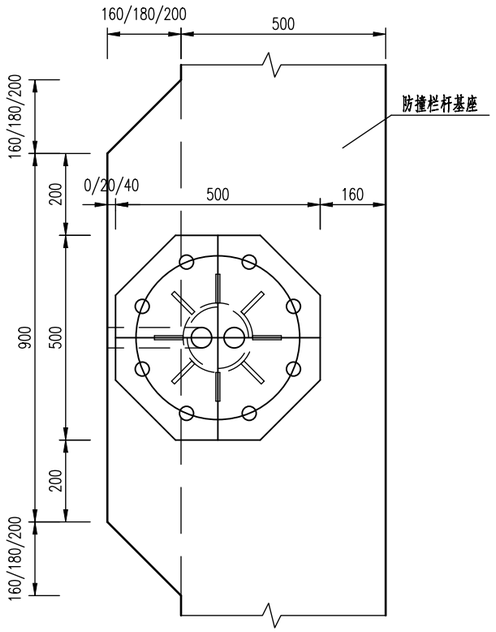

灯柱底座断面图

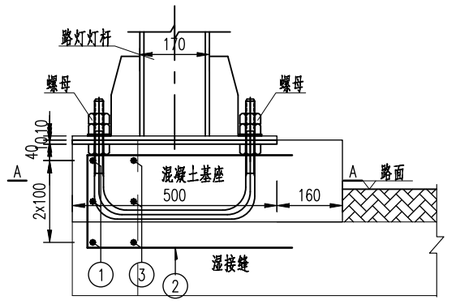

底座与桥梁连接图

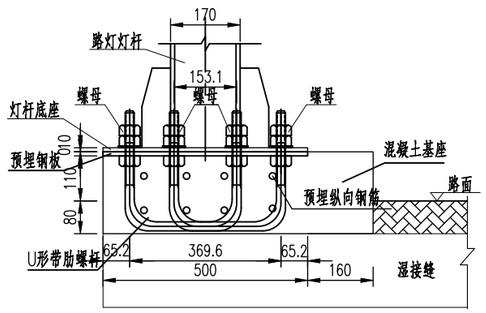

1--1

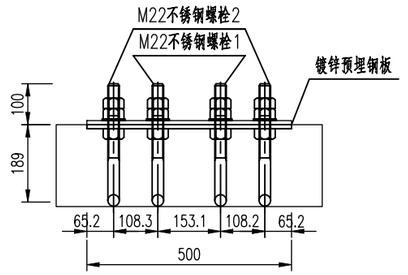

立柱螺栓预埋大样

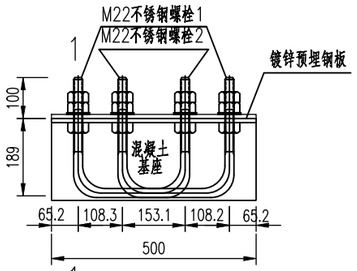

预埋钢板大样

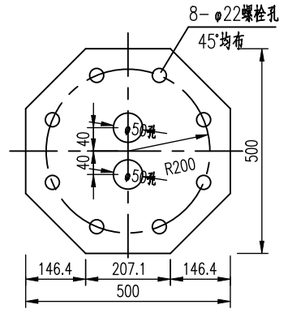

A-A

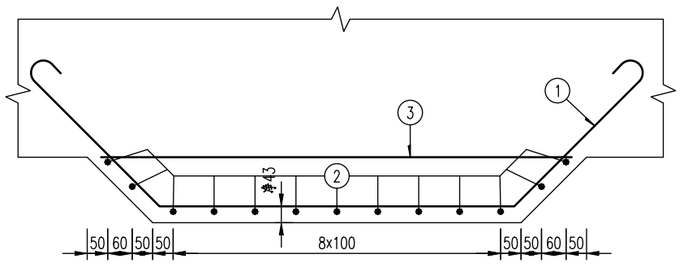

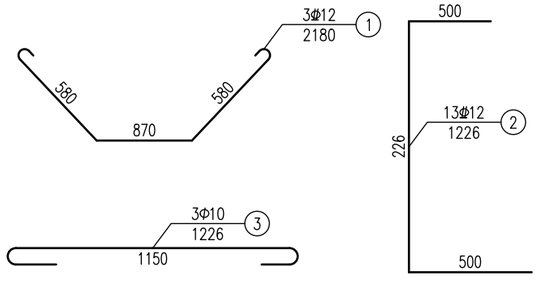

路灯基座钢筋数量表

编号	规格 (mm)	单根长 (mm)	根数	总长 (m)	总重 (kg)	一处合计 (kg)
1	φ12	2180	3	6.54	5.8	φ12:20.0 Φ10:2.3
2	φ12	1226	13	15.94	14.2	
3	Φ10	1226	3	3.68	2.3	
C30混凝土(m³)						0.2

附注：

1. 本图尺寸以毫米为计。
2. 底座板采用Q355C钢材，
3. 灯柱底部法兰同预埋钢板之间应有橡胶密封垫圈。
4. 路灯灯柱及底座详见另册。
5. 此图适用于新沙高架桥上层桥面的灯柱底座。

上层桥面路灯基座材料数量表 (新沙高架桥)

名称	材质	规格/(长度，直径)		单件重(kg)	数量	总重(kg)	备注
预埋钢板	Q355C	□500×500×10		19.63	16	314.0	
M22不锈钢螺栓1	10.9级	900	22		32(套)		
M22不锈钢螺栓2		690	22		32(套)		
M22不锈钢螺母					64(套)		

中交第二公路勘察设计研究院有限公司	狮子洋通道工程勘察设计 施 工 图 设 计	K6+418.3 新沙高架桥 路灯基座构造图	设计		复核		一审		二审		图号	SZYS/04/02/02/01/ 70

7251302272523583

检查车立面布置图

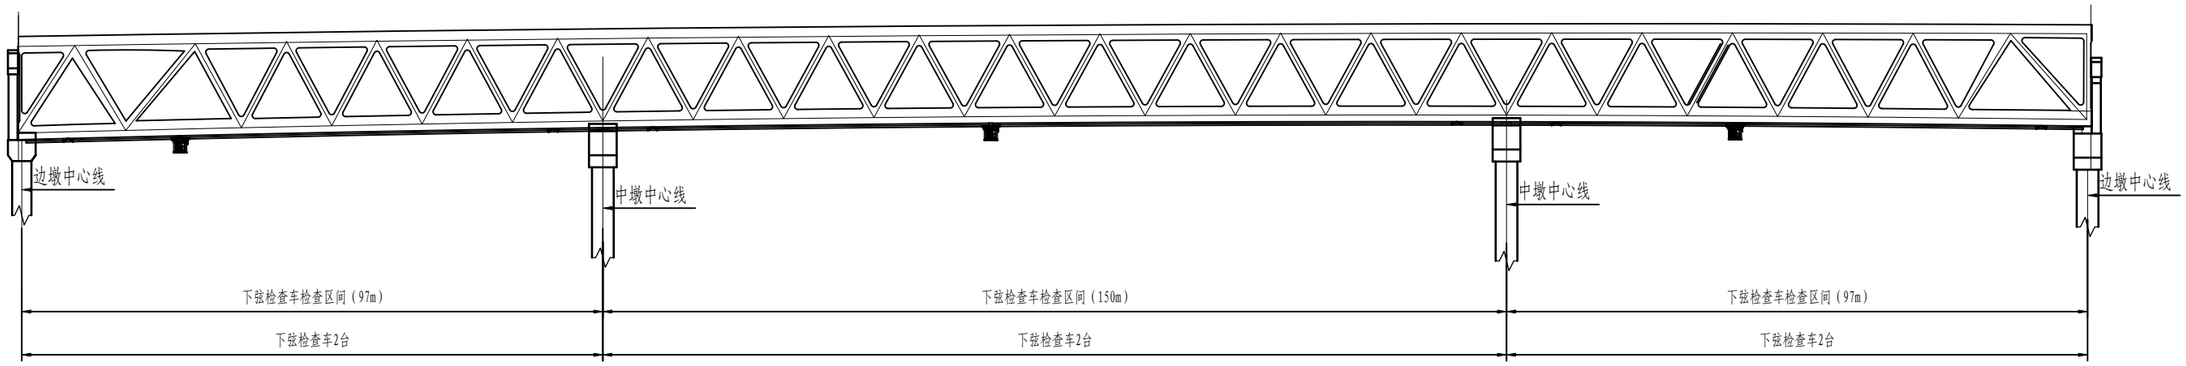

检查车布置表

项　目	数　量	覆盖范围	备　注
下弦检查车	3	下层桥梁底部	全幅布置

下弦检查车主要技术参数表

项目			规格	备注
整车重量			约7.1T	
外形尺寸			18000MM×2610MM×2960MM	
承载能力	额定荷载		1000Kg	分散放置
	集中载荷	跨中	500KG	
		端部	500KG	含升降平台
行走速度			0-10m/min	无极调速
抗风能力	工作抗风		8级风	
	泊车抗风		16级风	
工作净空			约1900MM-2500MM	
行走机构	主驱动机构		2×2.2Kw	电机驱动
	随动机构		2	
轨道	轨道型号		HM294×200	
	轨距		10800MM	
电气	动力源		锂电池	
结构材质	桁架		6061-T6、3003等	
	驱动箱及龙门架		Q235B、Q355B、45、40Cr等	

附注：

1. 本图尺寸均以m计。
2. 下弦检查车全幅布置，共3台。
3. 图中所示检查车仅为示意，检查车具体尺寸由厂家根据技术要求自行设计，经设计确认后执行。

中交第二公路勘察设计研究院有限公司	狮子洋通道工程勘察设计 施 工 图 设 计	K6+418.3 新沙高架桥 检查车设计图	设计		复核		一审		二审		图号	SZYS/04/02/02/01/ 72

下弦检查车立面（过墩状态）

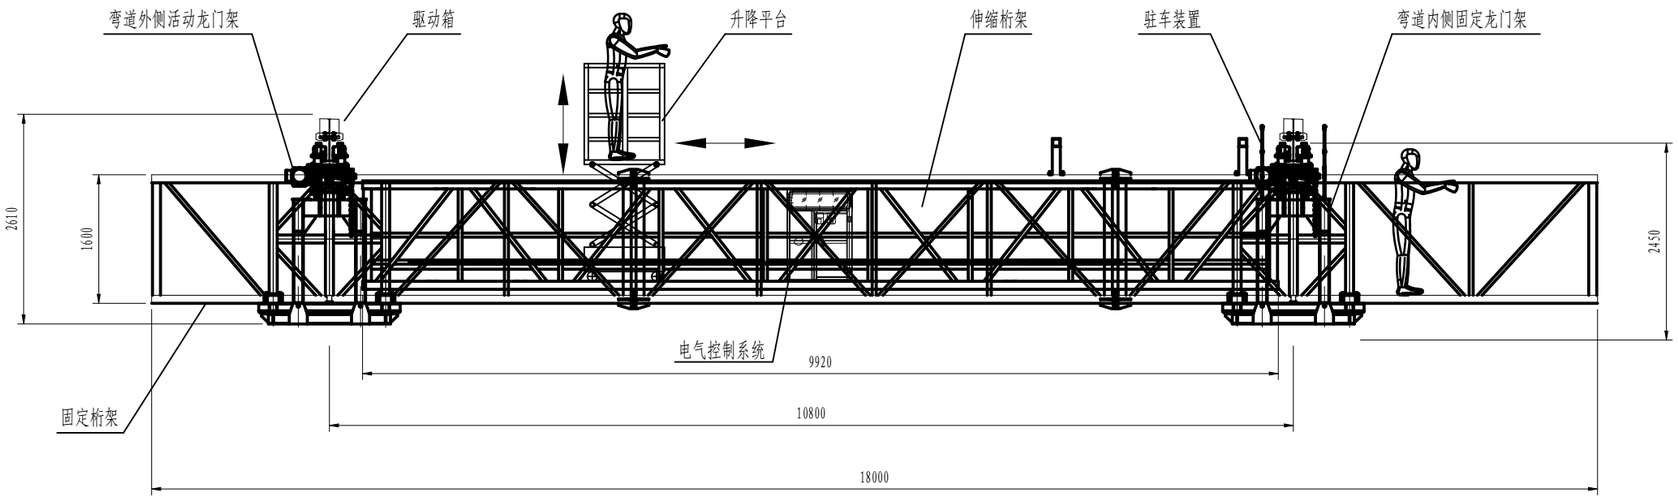

下弦检查车立面（过墩状态）

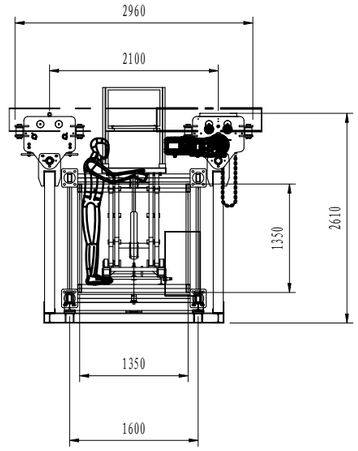

下弦检查车立面（伸出状态）

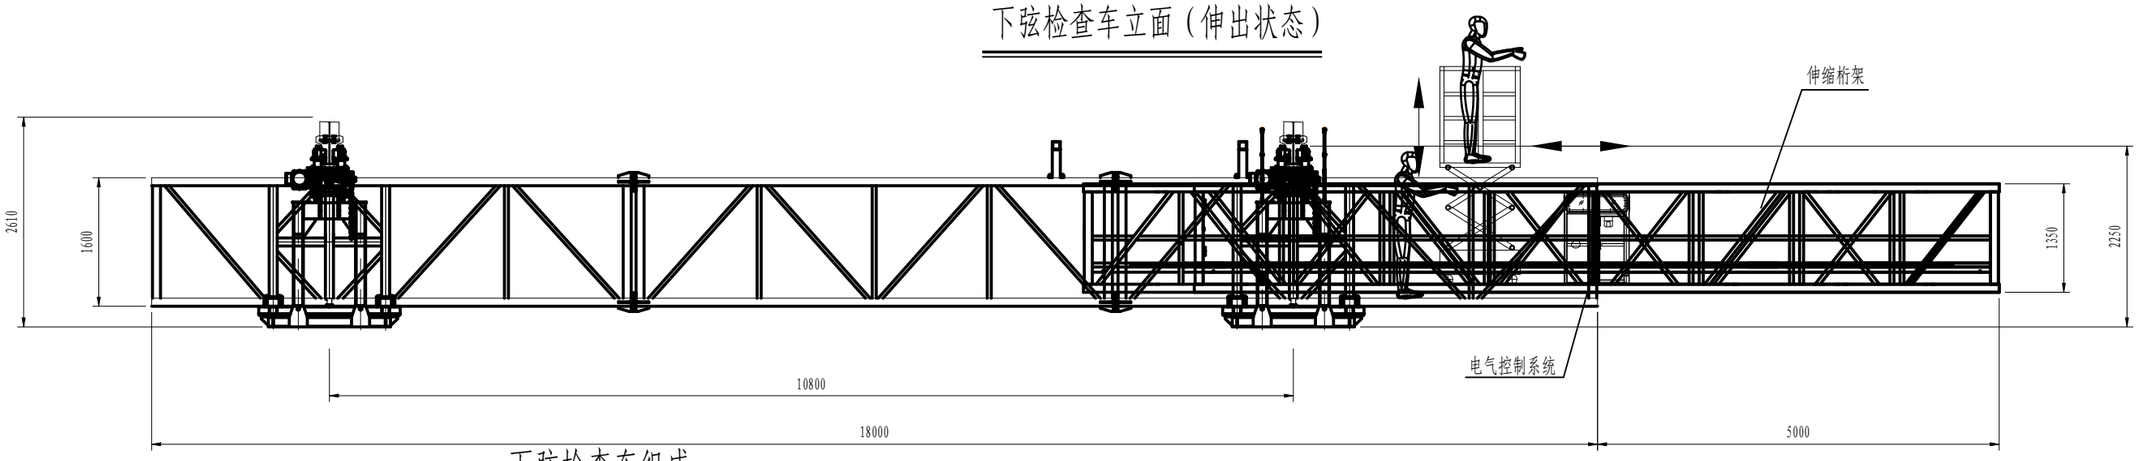

下弦检查车组成

序号	名 称	数 量	材料	单 重	总 重	备注
1	固定桁架	1	6061-T6	1500	1500	
2	伸缩桁架	1	6061-T6	750	750	
3	主驱动箱	2	组件	400	800	
4	从动箱	2	组件	300	600	
5	活动龙门架	1	组件	1100	1100	
6	固定龙门架	1	组件	1050	1050	
7	电气控制系统	1	组件	500	500	
8	升降平台系统	1	组件	600	600	含轨道
9	驻车装置	4	组件	50	200	

附注：

1、本图尺寸均以毫米（mm）单位。
2、检查车为钢桁梁下弦检查车，单幅布置。
3、为适应弯道、轨距误差及左右侧行走速度不一致，检查车需具备同步直线行走功能。
4、检查车桁架采用铝合金结构，龙门架采用钢结构。
5、为便于检查车日常充电，在检查车停靠处需要设置AC220V，功率6kW以上的插线板作为预留充电接口。
6、梁底检查车表面防腐涂装处理按具体要求进行。

中交第二公路勘察设计研究院有限公司	狮子洋通道工程勘察设计 施 工 图 设 计	K6+418.3 新沙高架桥 检查车设计图	设计		复核		一审		二审		图号	SZYS/04/02/02/01/ 72